


www.slamcoll.com

1. REFER TO GENERAL INFORMATION SHEET FOR LIST OF TYPICAL ABBREVIATIONS AND GRAPHIC ARCHITECTURAL GRAPHIC LEGENDS AND SYMBOLS.
2. REFER TO TYPICAL PARTITION TYPES AND DETAILS. ALL PARTITIONS SHALL BE TYPE 1 UNLESS OTHERWISE NOTED.
3. REFER TO CODE INFORMATION AND FIRE SAFETY PLAN DRAWINGS FOR REQUIREMENTS OF FIRE RESISTANCE RATED PARTITIONS AND NON-FIRE RESISTANCE RATED SMOKE PARTITIONS.
4. ALIGN PARTITIONS WITH COLUMN OR MULLION CENTERLINE. UNLESS OTHERWISE NOTED.
5. DIMENSIONS ARE FROM FACE OF WALL TO FACE OF WALL, (i.e. FACE OF COVER FROM FACE OF WALL FOR EXISTING CONDITION OR FROM COLUMN CENTERLINE, UNLESS OTHERWISE NOTED. DIMENSIONS NOTED AS "CLEAR" SHALL BE FROM FINISH FACE TO FINISH FACE, (i.e. face of ceramic tile to face of ceramic tile). VERIFY ALL EXISTING DIMENSIONS IN THE FIELD.
6. REFER TO PLAN ENLARGEMENTS FOR ADDITIONAL DIMENSIONS.
7. REFER TO DOOR AND FRAME DETAILS FOR ADDITIONAL INFORMATION. PROVIDE MINIMUM 4" CLEARANCE FROM FACE OF DOOR JAMB TO FACE OF ADJACENT WALL, UNLESS OTHERWISE NOTED.
8. REFER TO TYPICAL MOUNTING LOCATIONS AND HEIGHTS FOR TOILET ACCESSORIES. EQUIPMENT, WALL SPECIALLY DESIGNATED, ETC., TYPICAL TOILET ROOM ELEVATIONS AND TOILET ACCESSORY SCHEDULE.
9. PROVIDE FIRE TREATED WOOD BLOCKING OR MINIMUM 1/2"x2" THICK STEEL PLAT STRAP AND BACKING PLATE AT, BUT NOT LIMITED TO, THE FOLLOWING LOCATIONS: TOILET ACCESSORIES, CASEWORK, MILLWORK, DOOR WALL BUMPERS, AND ALL OTHER WALL MOUNTED EQUIPMENT OR DEVICES.
10. REFERENCE THE FIRE SAFETY PLANS, ALL EXISTING PARTITIONS INDICATED TO BEING AS FIRE BARRIERS. FIRE PARTITIONS, SMOKE BARRIERS OR SMOKE PARTITIONS, TO MEET ALL REQUIREMENTS FOR STATED FIRE AND/OR SMOKE RATING.
11. CONSTRUCTION OF PARTITION MUST MATCH REQUIREMENTS FOR STATED FIRE AND/OR SMOKE RATING.
12. EXTENTS OF PARTITION MUST EXTEND FULL HEIGHT, SEALED TO UNDERSIDE OF DECK ABOVE. PARTITION TO EXTEND LATERALLY FULL LENGTH WITHOUT DISCONTINUITY OR INTERRUPTIONS.
13. FIRST STOPS MUST BE PROVIDED AT ALL HOLES, PENETRATIONS AND EGRESS.
14. REFER TO THE EQUIPMENT PLANS FOR RESIDENTIAL APPLIANCE, AND TOILET ACCESSORY LOCATIONS. REFER TO THE EQUIPMENT PLANS FOR EQUIPMENT LOCATIONS AND SCHEDULE.
15. REFER TO THE FINISH PLANS FOR PART PATTERNS.
16. FLOOR PATCH AND FLOOR LEVELING: REPAIR EXISTING TOPPING SLAB AND CONCRETE FLOOR AT DEMOLITION OF WALLS AND AT ALL OTHER LOCATIONS AS REQUIRED. REFER TO DEMOLITION PLANS FOR ADDITIONAL INFORMATION.
17. PATCHING AND REPAIRING OF EXISTING PARTITIONS, CEILINGS, FLOORS, ETC. TO MATCH EXISTING ADJACENT CONSTRUCTION AND FINISHES, UNLESS OTHERWISE NOTED.
18. PROVIDE PATCHING AND OPENINGS AS REQUIRED FOR ALL INTERSECTING TRADES (EXISTING & NEW), AND THEN PATCH TO MATCH EXISTING. THIS INCLUDES EXISTING CONSTRUCTION, CONSTRUCTION PERIOD AND/OR DISTURBED BY THE DEMOLITION, INSTALLATION AND/OR RELOCATION OF MEP/AVT SERVICES, EQUIPMENT AND DEVICES.
19. PATCHING AND REPAIR ALL EXISTING SURFACES TO BE REPAIRED OR DISTURBED BY NEW CONSTRUCTION AND/OR EXISTING CONSTRUCTION SCHEDULED TO BE DEMOLISHED.
20. PATCHING AND REPAIR ALL EXISTING SURFACES THAT ARE TO RECEIVE NEW MATERIALS, FINISHES, ETC.

	NEW WALL CONSTRUCTION
	EXISTING WALL CONSTRUCTION TO REMAIN
	CASEWORK
	FIRE EXTINGUISHER CABINET
	CARD READER
	AUTOMATIC - HAND SWIPE
	BOTTLE FILLER
	Z LOCKER
	FLAT PANEL DISPLAY
	NOT IN SCOPE

**440 Mamaroneck Ave.
Harrison, NY
Suite 301**

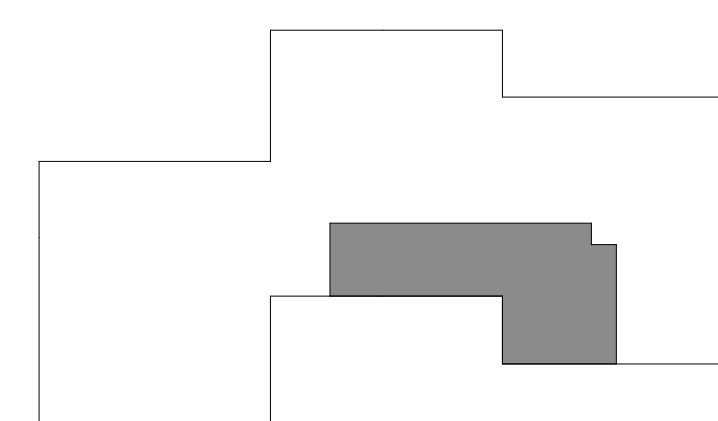

Number	Date	Issued For

Date 4/10/2026	Drawing Number
Scale As indicated	A103
Proj. Number 25195.25	

