



NOTE: FULL PROJECT SCOPE IS SHOWN AT PLANS, ELEVATIONS AND DETAILS. WORK IS TO BE COMPLETED IN MULTIPLE PHASES. SEE SCHEMATIC PHASING DIAGRAM AT SHEET G001. COORDINATE FINAL DEMARCATION BETWEEN PHASES WITH TENANT REPRESENTATIVE AND ON-SITE CONDITIONS.



No.	Description	Date
1	75% CD REVIEW	2026-06-23
2	PERMIT SET / ISSUE FOR BID	2026-07-07


GENERAL PLAN NOTES

- SEE SHEET G001 FOR GRAPHIC LEGEND INFORMATION.
- SEE SHEET G002 FOR ADDITIONAL PLAN SPECIFIC GENERAL NOTES.
- SEE SHEET G010 FOR WALL AND CEILING DEVICE ALIGNMENT DIAGRAMS. PROVIDE ADDITIONAL CONCEALED FRAMING FOR EXACT PLACEMENT.
- SEE SHEET SERIES A75X FOR SCHEMATIC 3-DIMENSIONAL SPACE DEPICTIONS.
- SEE ALSO SEPARATELY ISSUED SOS INTERIOR SIGNAGE AND GRAPHICS* FOR ADDITIONAL INFORMATION AND FOR SCOPE NOT DESCRIBED AT THIS DOCUMENTATION SET.

KEYNOTE LEGEND

C102	FIVE ADJUSTABLE PLASTIC LAMINATE SHELVES ON HEAVY-DUTY SHELF STANDARDS, 8 FEET LONG. PROVIDE CONCEALED BLOCKING. SEE DETAIL 7/A805.
C103	AT ALL ALUMINUM AND GLASS ENTRY WALLS, SEE SEPARATE SIGNAGE VENDOR DRAWINGS FOR GRAPHIC FILM DISTRACTION MARKERS FOR FULL LENGTH OF SAFETY GLASS PANELS AND DOORS.
C105	AT ALL WALLS WITH WALL COVERING, PROVIDE LEVEL 5 FINISH, INCLUDING PRIMER AND PAINT. TO BE HAND TROWELED AND SANDED LEVEL 5 FINISH TO ELIMINATE APPEARANCE AND SHADOWING OF METAL STUDS TELEGRAPHING TO PARTITION FACE. SPRAY APPLIED OR ROLLER-APPLIED LEVEL 5 COMPOUND WILL NOT BE ACCEPTED. COORDINATE WITH FINISH PLAN.
C106	FIRE EXTINGUISHER CABINETS TO BE FLUSH FACE DOOR. TYP. TO RECEIVE CUSTOM VINYL IDENTIFICATION GRAPHIC. SEE DETAIL AT SHEET 2/A812.
C107	PROVIDE CONCEALED BLOCKING FOR SUPPORT OF WALL MOUNTED MONITOR(S). PROVIDE ADDITIONAL FRAMING FOR EXACT PLACEMENT OF RECEPTACLES. RECEPTACLES AND CABLES TO BE CONCEALED FROM VIEW.
C108	CENTERLINE OF NEW PARTITION TO ALIGN WITH CENTERLINE OF EXISTING COLUMN OR EXTERIOR MULLION AS SHOWN. SEE TYPICAL PARTITION-TO-MULLION DETAIL A612.
C109	PROVIDE ADDITIONAL PARTITION CONSTRUCTION TO CLOSE GAP BETWEEN BACK FACE OF EXISTING COLUMN OR BUILD-OUT AND EXISTING PERIMETER GLAZING SYSTEM. TO YIELD ACoustICAL PRIVACY BETWEEN ADJACENT SPACES. SEE TYPICAL PARTITION-TO-MULLION DETAIL A612.
C111	FIXED MILLWORK RECEPTION DESK. PROVIDE FLUSH MOUNTED POWER AND DATA RECEPTACLES. PROVIDE TRIMLESS MILLWORK ACCESS PANELS BELOW WORKSURFACE TO ACCOMMODATE CONNECTIONS. REFER TO ELECTRICAL DRAWINGS AND SHEET A801 FOR DETAILS.
C113	PROVIDE HEAVY-GAUGE METAL STUD FRAMING ABOVE CEILING FOR SUPPORT OF PIVOT DOOR HARDWARE. LATERALLY BRACE. SEE DETAIL 7/A900.
C114	PROVIDE FLEXIBLE TUBE WATER CONNECTION WITH SEPARATE SHUT OFF FOR FREESTANDING COFFEE MAKER. COORDINATE FINAL LOCATION OF PENETRATION IN MILLWORK ON SITE WITH ARCHITECT.
C117	REFER TO SEPARATE SIGNAGE VENDOR DRAWINGS FOR NEW CUSTOM ADA-COMPLIANT IDENTIFICATION SIGNAGE AT TOILET ROOMS. SIGNAGE TO INCORPORATE BRILLE AND RAISED CHARACTERS PLUS UNIVERSAL PICTOGRAMS. ALL IN CONTRAST COLOR TO BACKGROUND.
C118	ELEVATOR CALL BUTTONS, HALL LANTERNS, AND SIMILAR ITEMS TO BE RELOCATED TO MOUNT FLUSH WITH NEW ORNAMENTAL PARTITION FACE FINISH. FULLY CLEAN EXISTING DEVICES TO BE REUSED. PROVIDE ADDITIONAL CONCEALED WIRING AND MOUNTING BACK BONES OR EXTENSION RINGS. SEE SEPARATE SIGNAGE VENDOR DRAWINGS FOR EVACUATION SIGNAGE WITH ETCHED MAP AND 5-COLOR PAINT INFILL.
C119	COORDINATE WITH ENGINEERING REQUIREMENTS FOR SCOPE NOT SHOWN AT THIS AREA.
C123	LOCATION OF TENANT PROVIDED DEFIBRILLATOR. COORDINATE MOUNTING LOCATION WITH ARCHITECT IN FIELD.
C126	PROVIDE NEW WORKSURFACE TO BE SUPPORTED BY SEPARATELY PROVIDED FILE CABINETS BELOW. TO BE PLASTIC LAMINATE ON 3/4" INCH SUBSTRATE WITH 1-1/2" INCH BUILT-UP NOSE AT ALL EDGES. PROVIDE ADDITIONAL SPACERS AND BLOCKING FOR LEVEL INSTALLATION. ATTACH TO FILE ASSEMBLY WITH HIGH-STRENGTH DOUBLE FACED FOAM TAPE AS MANUFACTURED BY 3M. PROVIDE FULLY FINISHED MATCHING WATERFALL END PANEL. COORDINATE FINAL DIMENSIONS IN PLAN WITH SEPARATE FURNITURE VENDOR.
C127	FOR ENTIRE LENGTH OF WALL, ADD ONE LAYER OF 1/4" DRYWALL. PROVIDE LEVEL 5 FINISH.

Legend	Description	Quantity	Unit
✓	Count Measurement	29	Count

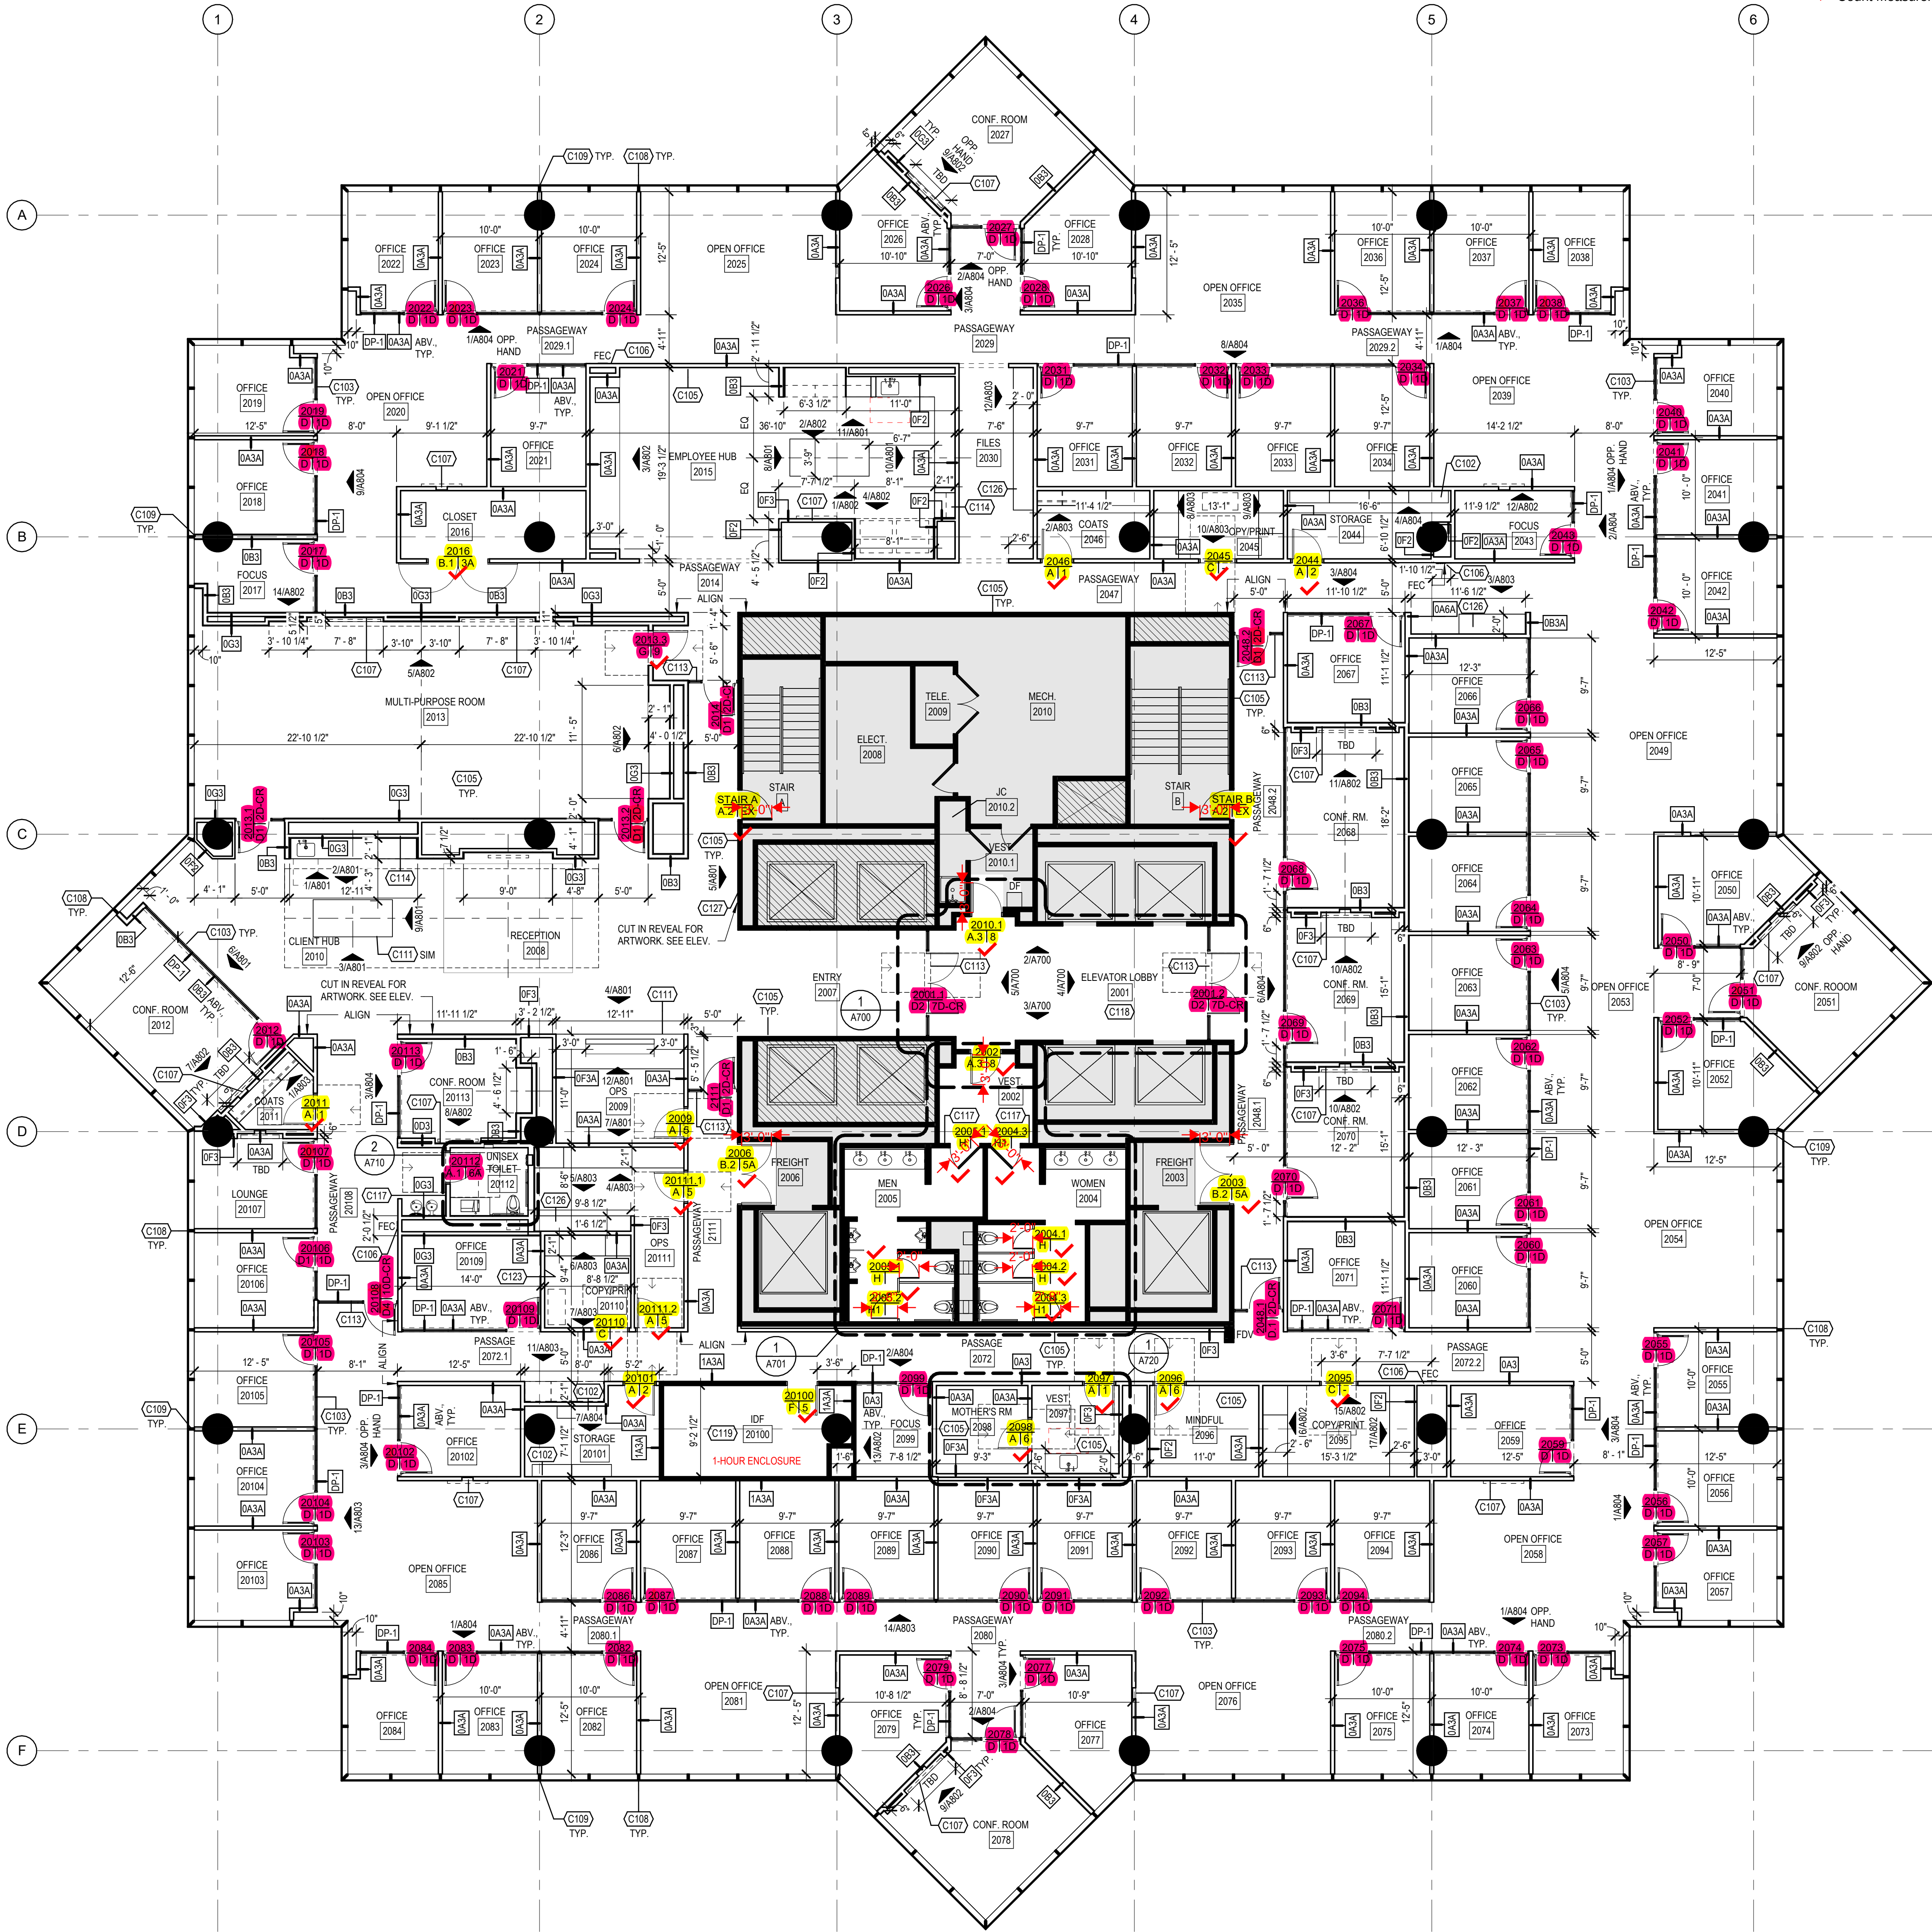

1 FLOOR PLAN - LEVEL 20
1/8" = 1'-0"