




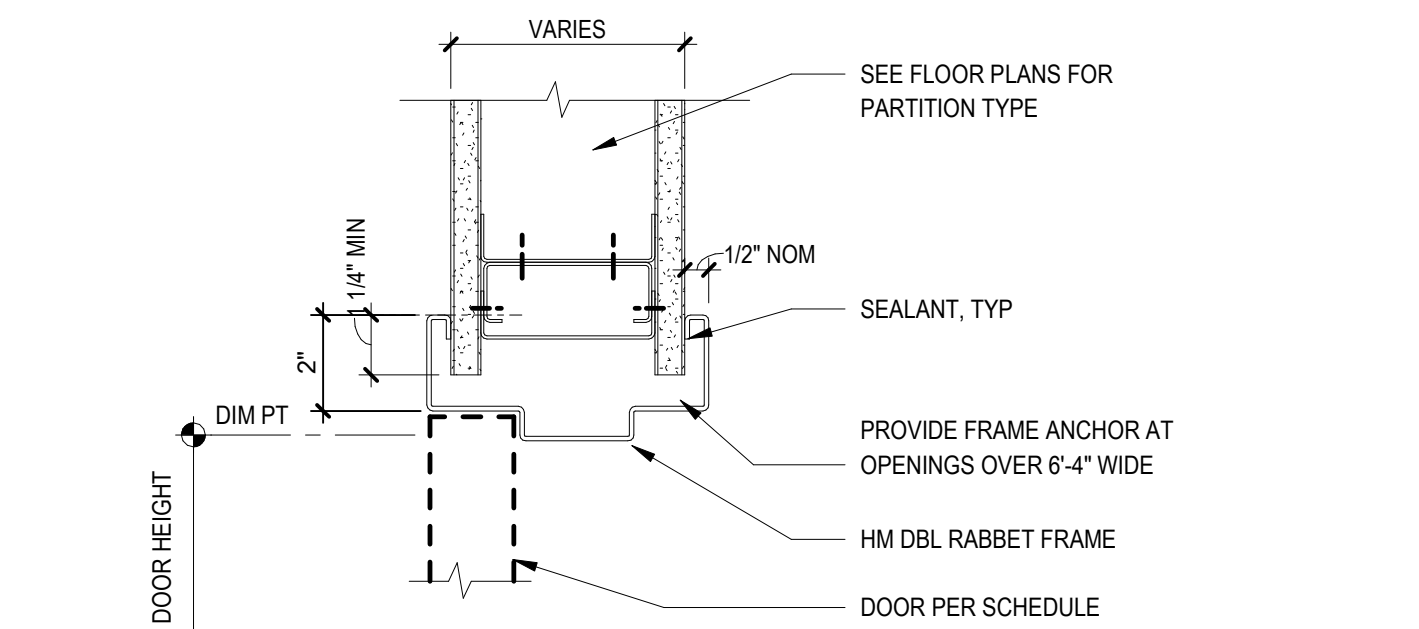


E1 FRAME TYPE: S - HM DOOR HEAD
3" = 1'-0"

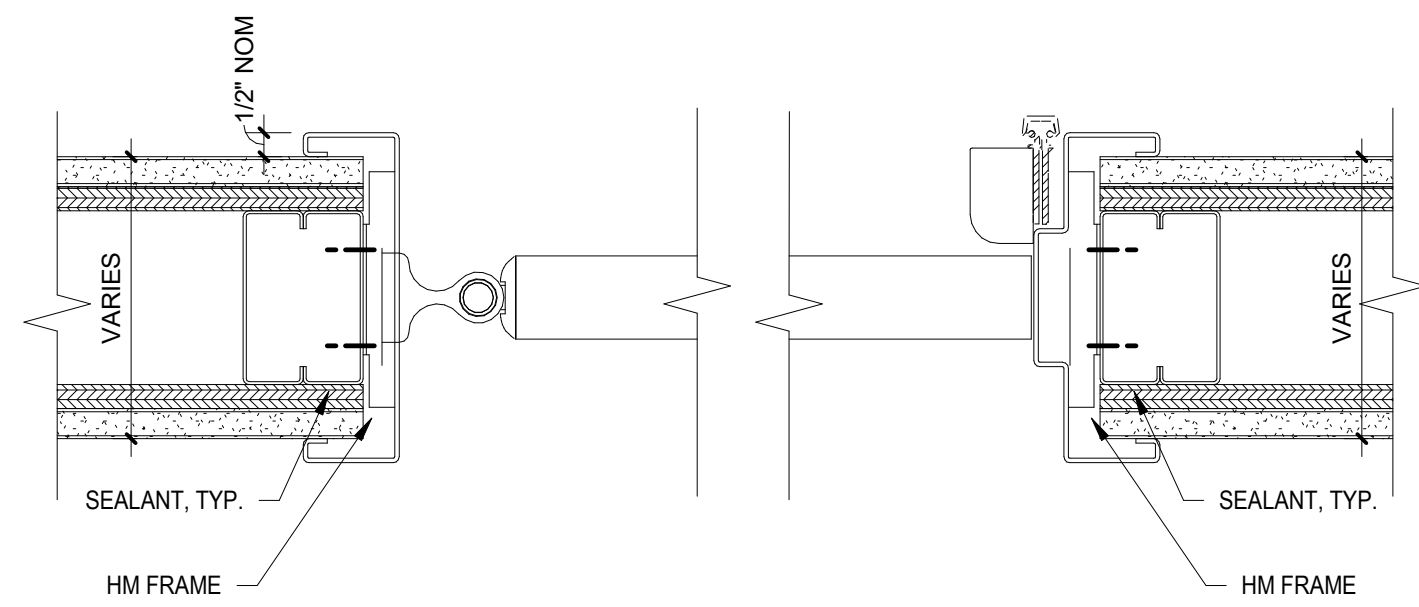


D1 FRAME TYPE: ANT-BARRICADE - HM DOOR JAMB
3" = 1'-0"

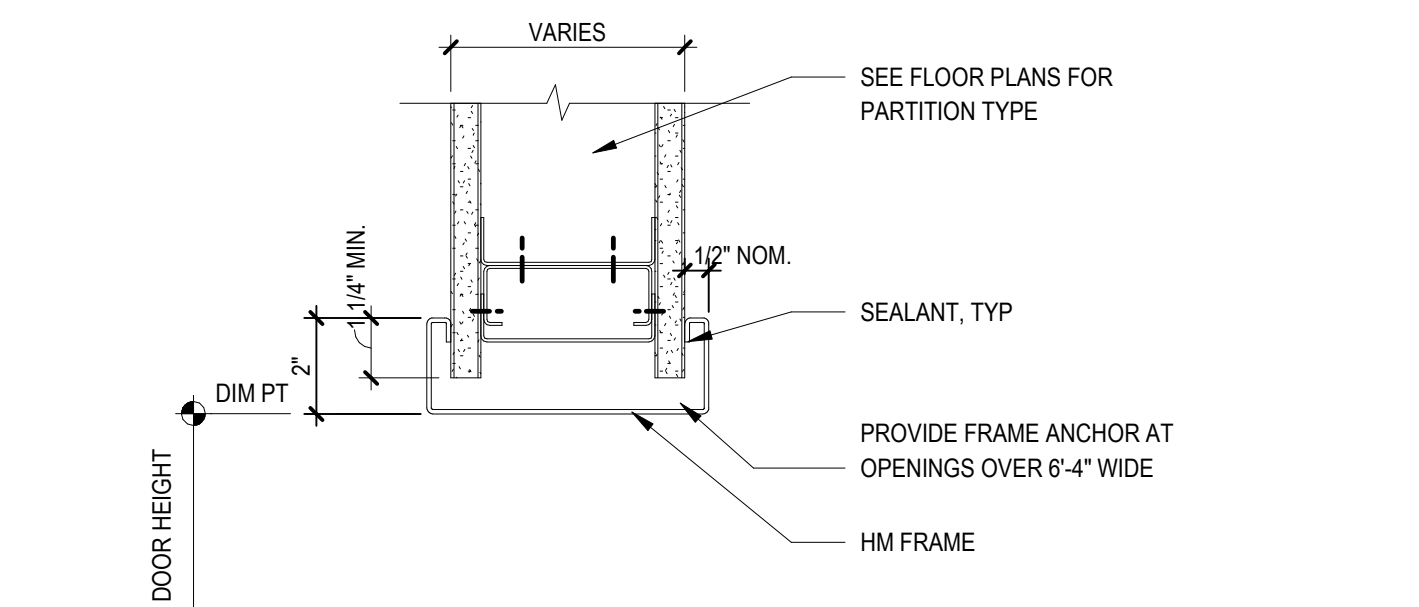

C1 FRAME TYPE: S - HM DOOR HEAD
3" = 1'-0"

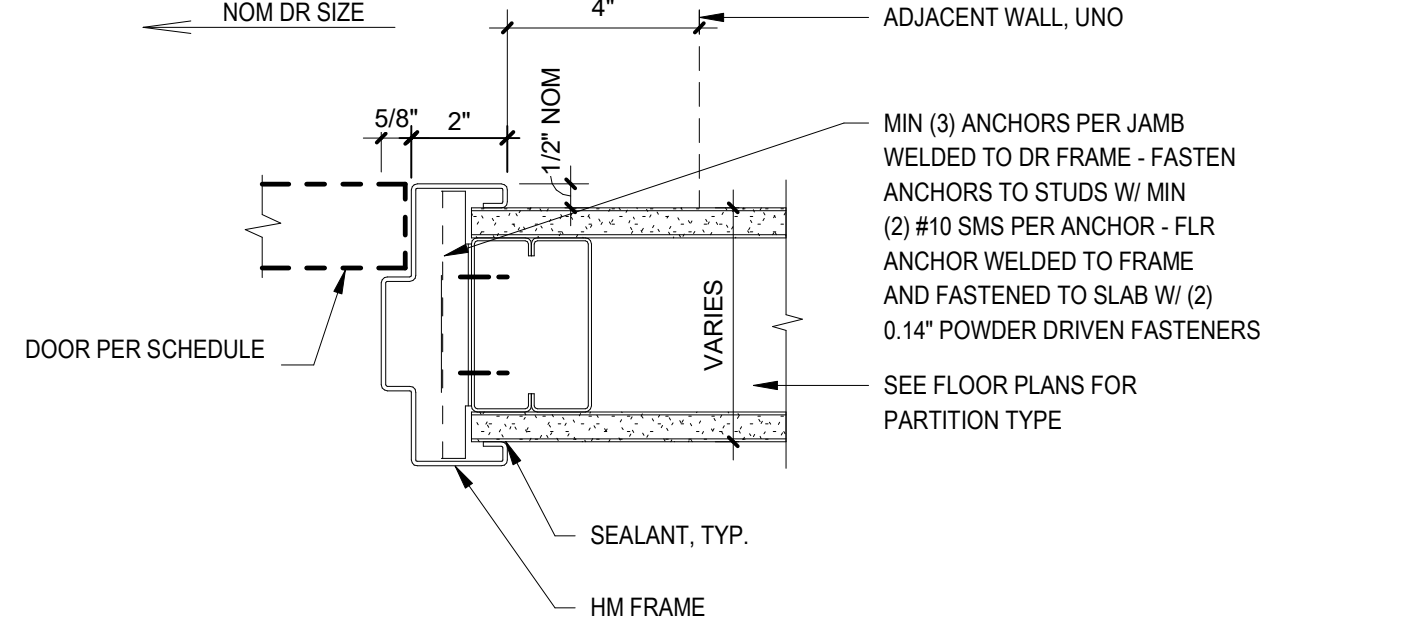


E2 FRAME TYPE: S - HM DOOR JAMB
3" = 1'-0"

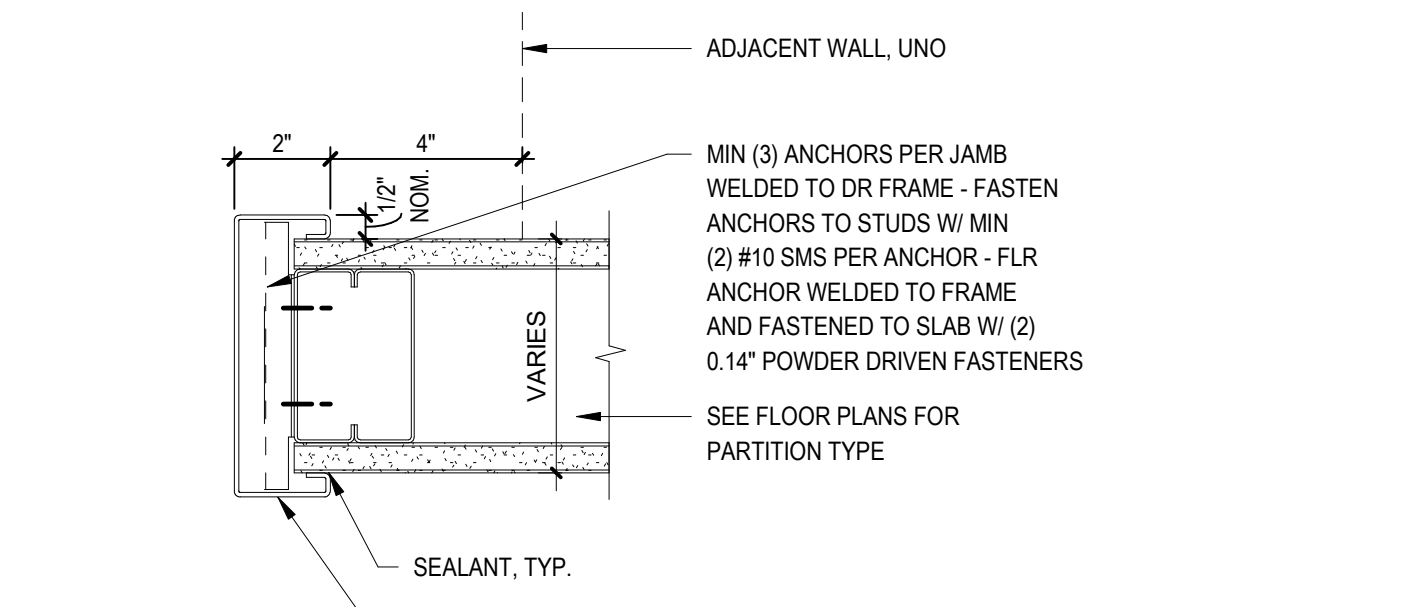


D2 FRAME TYPE: S - HM CASED OPEN JAMB
3" = 1'-0"

DOOR PANEL TYPE LEGEND

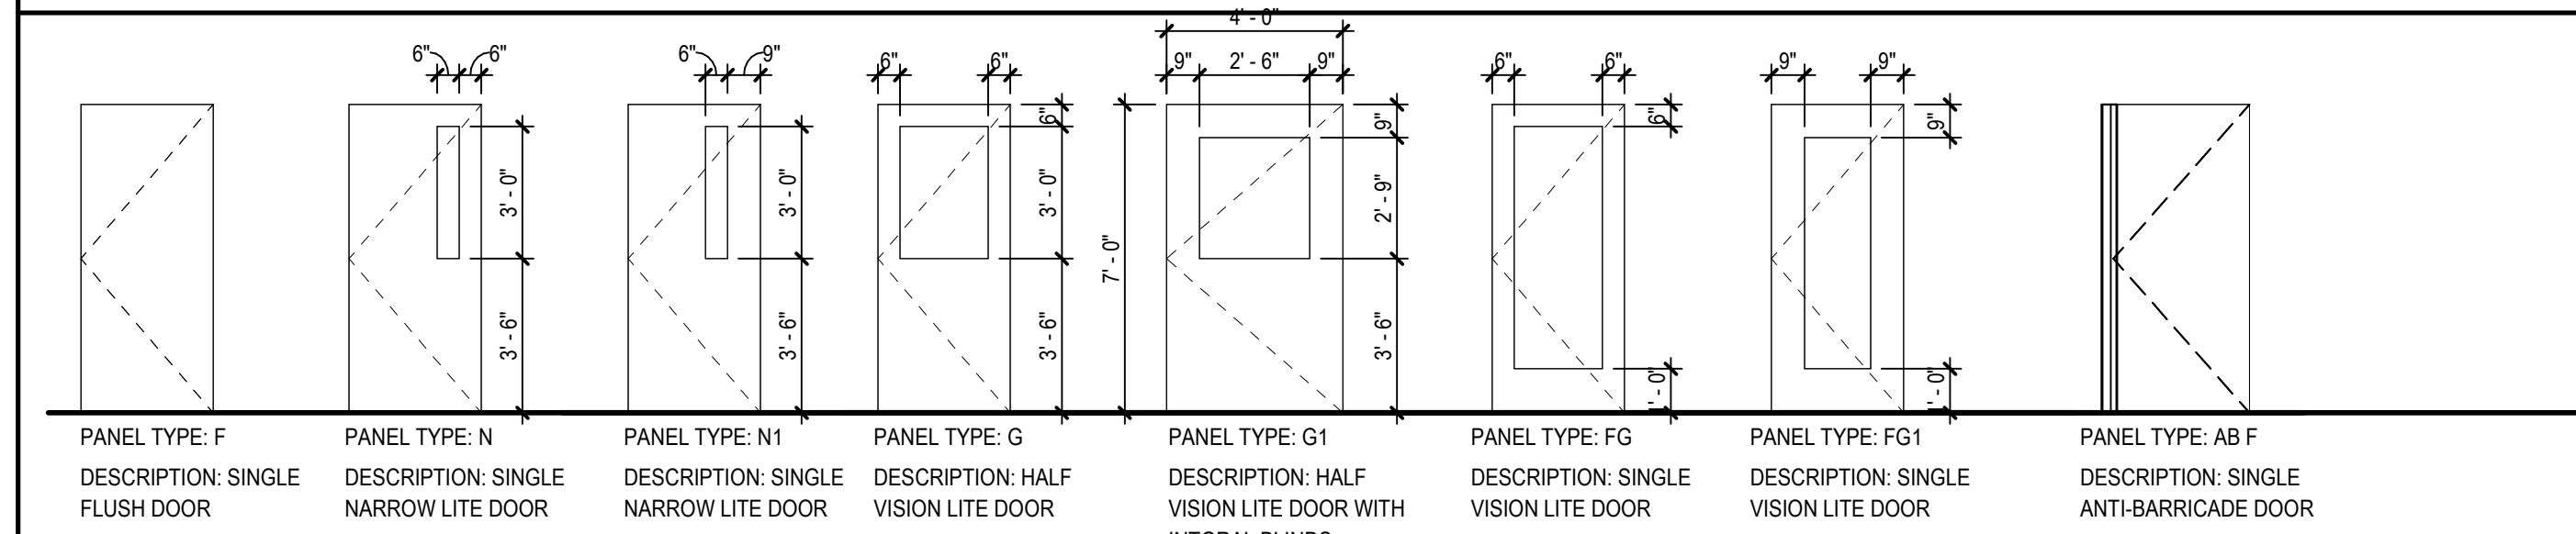

DOOR FRAME TYPE LEGEND

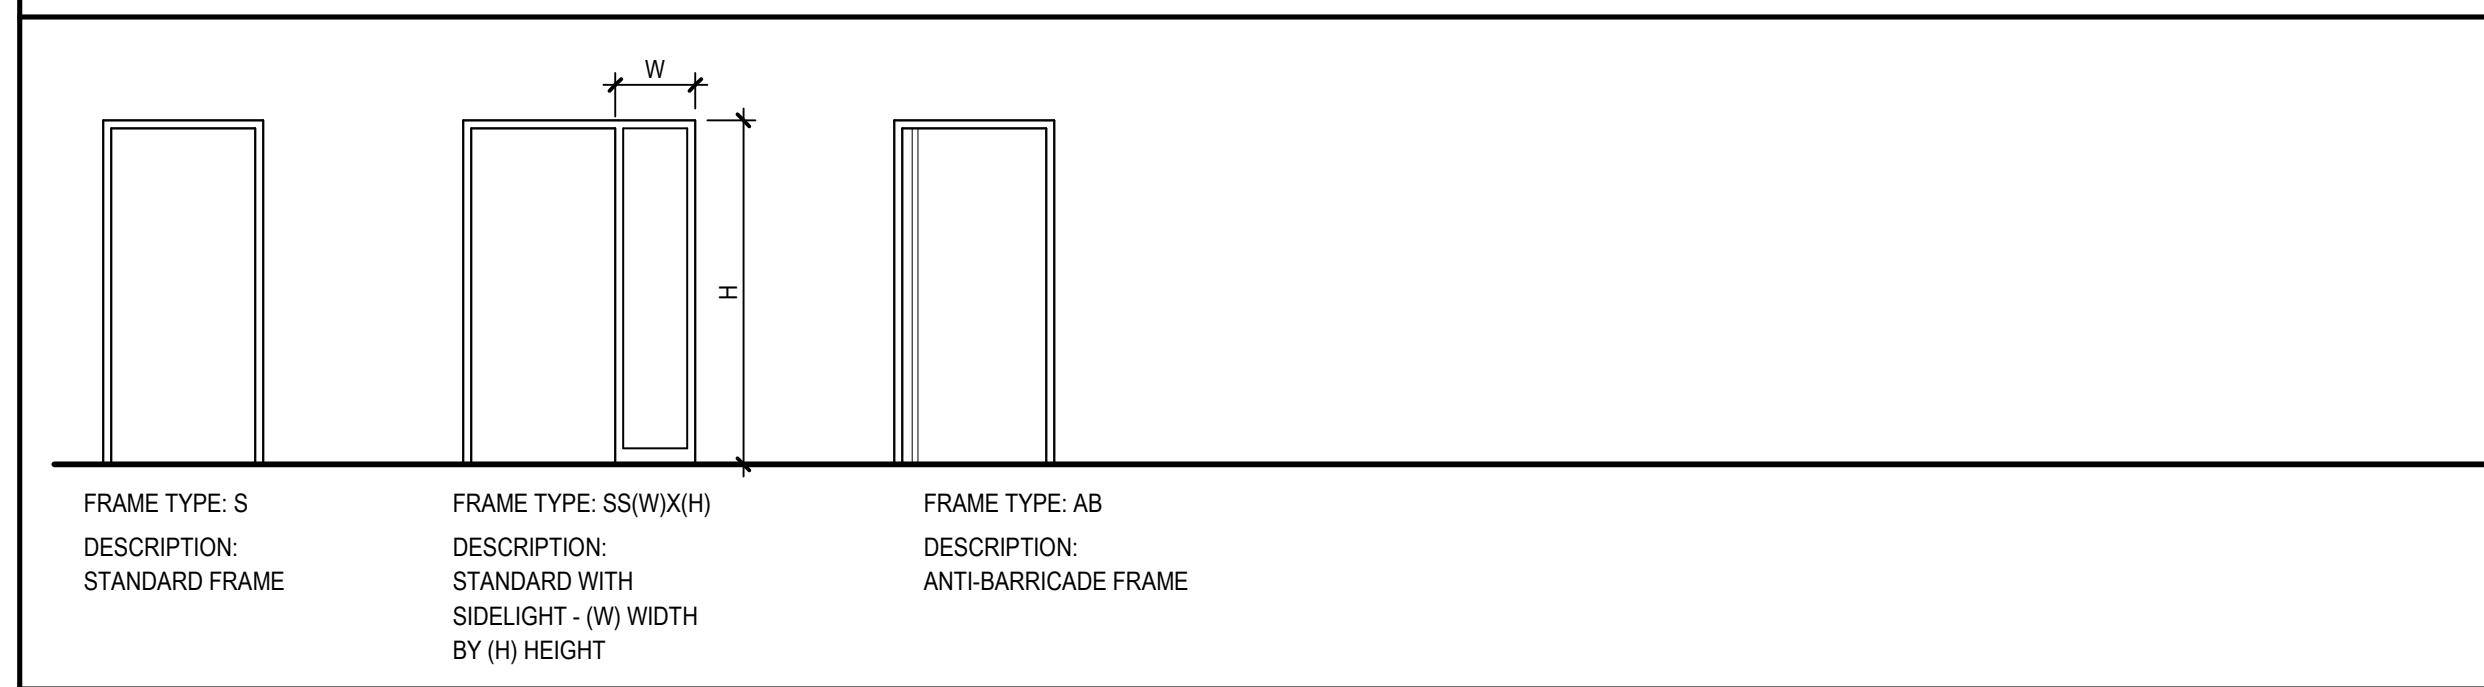

DOOR TYPE NOTES

1. NUMBER OF PANELS IS INDICATED IN THE DOOR AND FRAME SCHEDULE BY A DOOR TYPE PREFIX. (EXAMPLE: 2F = PAIR FLUSH DOOR)
2. DOOR HARDWARE IS NOT GRAPHICALLY SHOWN IN ANY VIEW. REFER TO HARDWARE GROUP IN DOOR AND FRAME SCHEDULE.

Montefiore
Einstein

nbbj

111 FIFTH AVENUE, 10TH FLOOR
NEW YORK, NY 10003
PHONE 212 924 9000
www.nbbj.com

OWNER:
MONTEFIORE MOSES MEDICAL CENTER
111 EAST 210TH STREET
NEW YORK, NY 10003

STRUCTURAL ENGINEER:
LERA
40 WALL STREET, FLOOR 23
NEW YORK, NY 10005
212-750-9000

MEP:
WSP
200 LIBERTY STREET, SUITE 302
NEW YORK, NY 10281
212-465-5000

MONTEFIORE
MEDICAL CENTER
CPEP BHCOE

ISSUE FOR BID

SEAL

Issue Date

REVISIONS

MARK DATE DESCRIPTION

PROJECT NUMBER 103435.00

PROJECT ARCHITECT DT

NYC DOB NUMBER

CON NUMBER

SHEET NAME

DOOR DETAIL &
SCHEDULES

SHEET NUMBER

A-700.00

NYC DOB STAMP

NYC DOB BSCAN

DOOR AND FRAME SCHEDULE AREA A

DOOR										FRAME					GLAZING	FIRE RATING LABEL	HARDWARE	
MARK	SIZE			MATERIAL	TYPE	FINISH	GLAZING	MATERIAL	TYPE	FINISH	DETAIL							
	W	H	T								HEAD	JAMB	SILL	GROUP NO			COMMENTS	
RS012	3'-0"	7'-0"	1 3/4"	WD	F			HM	S		E1/A700	E2/A700			3			
RS013	3'-0"	3'-0"	7'-0"	1 3/4"	WD			HM	S		E1/A700	E2/A700			4.3	CREDENTIAL READER		
RS014	3'-0"	3'-0"	7'-0"	1 3/4"	WD	N	1/2" LAMINATED	HM	S		E1/A700	E2/A700			5.1			
RS015	3'-0"	3'-0"	7'-0"	1 3/4"	WD	N	1/2" LAMINATED	HM	S		E1/A700	E2/A700			6			
RS016	3'-0"	3'-0"	7'-0"	1 3/4"	WD	F		HM	S		E1/A700	E2/A700			7			
RS017A	3'-0"	3'-0"	7'-0"	1 3/4"	WD	N	1/2" LAMINATED	HM	S		E1/A700	E2/A700			6			
RS017B	3'-0"	3'-0"	7'-0"	1 3/4"	WD	F	IRWC-1	HM	S		E1/A700	E2/A700		45 MINS	4.3	CREDENTIAL READER		
RS020A	4'-0"	4'-0"	7'-0"	1 3/4"	WD	N1	1/2" LAMINATED	HM	SS24x84		E1/A700	E2/A700		45 MINS	9.1	CREDENTIAL READER		
RS020B	4'-0"	4'-0"	7'-0"	1 3/4"	WD	FG1	IRWC-2	3/8" POLYCARBONATE	HM	SS24x84	E1/A700	E2/A700			9	CREDENTIAL READER		
RS021	4'-0"	4'-0"	7'-0"	1 3/4"	WD	G1	IRWC-2	3/8" POLYCARBONATE	HM	S	E1/A700	E2/A700			1	VISION PANEL WITH INTEGRAL BLINDS, DOOR TOP MONITOR ALARMED		
RS022	4'-0"	4'-0"	7'-0"	1 3/4"	WD	G1	IRWC-2	3/8" POLYCARBONATE	HM	S	E1/A700	E2/A700			1	VISION PANEL WITH INTEGRAL BLINDS, DOOR TOP MONITOR ALARMED		
RS023	4'-0"	4'-0"	7'-0"	1 3/4"	WD	G1	IRWC-2	3/8" POLYCARBONATE	HM	S	E1/A700	E2/A700			1	VISION PANEL WITH INTEGRAL BLINDS, DOOR TOP MONITOR ALARMED		
RS024	4'-0"	4'-0"	7'-0"	1 3/4"	WD	G1	IRWC-2	3/8" POLYCARBONATE	HM	S	E1/A700	E2/A700			1	VISION PANEL WITH INTEGRAL BLINDS, DOOR TOP MONITOR ALARMED		
RS025	4'-0"	4'-0"	7'-0"	1 3/4"	WD	G1	IRWC-2	3/8" POLYCARBONATE	HM	S	E1/A700	E2/A700			1	VISION PANEL WITH INTEGRAL BLINDS, DOOR TOP MONITOR ALARMED		
RS026	4'-0"	4'-0"	7'-0"	1 3/4"	WD	G1	IRWC-2	3/8" POLYCARBONATE	HM	S	E1/A700	E2/A700			1	VISION PANEL WITH INTEGRAL BLINDS, DOOR TOP MONITOR ALARMED		
RS027	4'-0"	4'-0"	7'-0"	1 3/4"	WD	G1	IRWC-2/ SP-1	3/8" POLYCARBONATE	HM	S	SP-1	E1/A700	E2/A700			1	VISION PANEL WITH INTEGRAL BLINDS, DOOR TOP MONITOR ALARMED	
RS028	3'-0"	3'-0"	7'-0"	1 3/4"	WD	F	IRWC-1	HM	S		E1/A700	E2/A700			4.2	CREDENTIAL READER		
RS029A	3'-0"	3'-0"	7'-0"	1 3/4"	WD	FG1	IRWC-2	3/8" POLYCARBONATE	HM	SS24x84	E1/A700	E2/A700			8			
RS029B	3'-0"	3'-0"	7'-0"	1 3/4"	WD	G1	IRWC-1	3/8" POLYCARBONATE	HM	S	E1/A700	E2/A700			4.1	VISION PANEL WITH INTEGRAL BLINDS, DOOR TOP MONITOR ALARMED		
RS030	3'-0"	3'-0"	7'-0"	1 3/4"	WD	F	IRWC-1	HM	S		E1/A700	E2/A700			6			
RS030A	3'-0"	3'-0"	7'-0"	1 3/4"	WD	FG1	IRWC-1	3/8" POLYCARBONATE	HM	S	E1/A700	E2/A700			4	CREDENTIAL READER		
RS030B	3'-0"	3'-0"	7'-0"	1 3/4"	WD	FG1	IRWC-1	3/8" POLYCARBONATE	HM	S	E1/A700	E2/A700			4	CREDENTIAL READER		
RS030C	4'-0"	4'-0"	7'-0"	1 3/4"	WD			HM	S		C1/A700	D2/A700						
RS032	3'-0"	3'-0"	7'-0"	1 3/4"	WD	F	IRWC-1	HM	S		E1/A700	E2/A700			3			
RS033	3'-0"	3'-0"	7'-0"	1 3/4"	WD	F	IRWC-1	HM	S		E1/A700	E2/A700			4	CREDENTIAL READER		
RS034	3'-0"	3'-0"	7'-0"	1 3/4"	WD	F AB	IRWC-2	HM	AB		C1/A700	D1/A700			2	ANTI - BARRICADE, DOOR TOP MONITOR ALARMED		
RS035	3'-0"	3'-0"	7'-0"	1 3/4"	WD	F AB	IRWC-2	HM	AB		C1/A700	D1/A700			2	ANTI - BARRICADE, DOOR TOP MONITOR ALARMED		
RS036	3'-0"	3'-0"	7'-0"	1 3/4"	WD	F	IRWC-1	HM	S		E1/A700	E2/A700			5			
RS037	3'-0"	3'-0"	7'-0"	1 3/4"	WD	F	IRWC-1	HM	S		E1/A700	E2/A700			7			
RS038	3'-0"	3'-0"	7'-0"	1 3/4"	WD	F	IRWC-1	HM	S		E1/A700	E2/A700			5			
RS040	3'-0"	3'-0"	7'-0"	1 3/4"	-	-	-	HM	S		C1/A700	D2/A700						

AREA B

MARK	DOOR							FRAME						GLAZING	FIRE RATING LABEL	HARDWARE	
	SIZE			MATERIAL	TYPE	FINISH	GLAZING	MATERIAL	TYPE	FINISH	DETAIL					GROUP NO	COMMENTS
	W	H	T								HEAD	JAMB	SILL				
F100	4'-0"	7'-0"	1 3/4"	WD	G1	IRWC-1	3/8" POLYCARBONATE	HM	S		E1/A700	E2/A700		20 MIN. SMOKE BARRIER	4.4	CREDENTIAL READER	
F101	4'-0"	7'-0"	1 3/4"	WD	G1	IRWC-2	3/8" POLYCARBONATE	HM	S		E1/A700	E2/A700			1	VISION PANEL WITH INTEGRAL BLINDS, DOOR TOP MONITOR ALARMED	
F102	4'-0"	7'-0"	1 3/4"	WD	G1	IRWC-2	3/8" POLYCARBONATE	HM	S		E1/A700	E2/A700			1	VISION PANEL WITH INTEGRAL BLINDS, DOOR TOP MONITOR ALARMED	
F103	4'-0"	7'-0"	1 3/4"	WD	G1	IRWC-2	3/8" POLYCARBONATE	HM	S		E1/A700	E2/A700			1	VISION PANEL WITH INTEGRAL BLINDS, DOOR TOP MONITOR ALARMED	
F104	4'-0"	7'-0"	1 3/4"	WD	G1	IRWC-2	3/8" POLYCARBONATE	HM	S		E1/A700	E2/A700			1	VISION PANEL WITH INTEGRAL BLINDS, DOOR TOP MONITOR ALARMED	
F105	4'-0"	7'-0"	1 3/4"	WD	G1	IRWC-2	3/8" POLYCARBONATE	HM	S		E1/A700	E2/A700		1	VISION PANEL WITH INTEGRAL BLINDS, DOOR TOP MONITOR ALARMED		
F107A	3'-0"	7'-0"	1 3/4"	WD	FG1	IRWC-1	3/8" POLYCARBONATE	HM	S		E1/A700	E2/A700		20 MIN. SMOKE BARRIER	10	CREDENTIAL READER	
F107B	3'-0"	7'-0"	1 3/4"	WD	FG1	IRWC-1		HM	S		E1/A700	E2/A700			5		
F108	3'-0"	7'-0"	1 3/4"	WD	F AB	IRWC-2		HM	AB		C1/A700	D1/A700			2	ANTI - BARRICADE, DOOR TOP MONITOR ALARMED	
F110	3'-0"	7'-0"	1 3/4"	WD	G	IRWC-1		HM	S		E1/A700	E2/A700		20 MIN. SMOKE BARRIER	5		
F111	3'-0"	7'-0"	1 3/4"	WD	F	IRWC-1		HM	S		E1/A700	E2/A700			7.1		
F112	4'-0"	7'-0"	1 3/4"	WD	G1	IRWC-1/ SP-1	3/8" POLYCARBONATE	HM	S		E1/A700	E2/A700			1.1	VISION PANEL WITH INTEGRAL BLINDS, DOOR TOP MONITOR ALARMED	
F112A	3'-0"	7'-0"	1 3/4"	WD	F	IRWC-1	1/4" LAMINATED	HM	S		E1/A700	E2/A700		20 MIN. SMOKE BARRIER	4.3	CREDENTIAL READER	
F112B	3'-0"	7'-0"	1 3/4"	WD	G	IRWC-1	1/4" LAMINATED	HM	S		E1/A700	E2/A700			4.3	CREDENTIAL READER	