

A

B


C

D


E

DOOR AND FRAME SCHEDULE													
DOOR						FRAME		DETAIL					
OPENING SIZE			Thickness	Type	Material	Frame Type	Material	Jamb	Head	Glazing	Hardware Set	Fire Rating (Mins)	Comments
Door No	Width A	Width B											
3.0 - THIRD FLOOR													
3003	3'-0"		7'-0"	1 3/4"	F	WD	A	HM	5C/A611	5C/A611	-	7.0	CR
3006A	3'-0"		7'-0"	1 3/4"	F	WD	A	HM	5C/A611	5C/A611	-	7.0	CR
300-01A	3'-0"	3'-0"	6'-8"	1 3/4"	EXIST	EXIST	EXIST	EXIST	EXIST	EXIST	-	5.2	EXIST, 2 AUTOMATIC, CR, NOTE B, NOTE C
300-01B	3'-0"		7'-0"	1 3/4"	FG	WD	A	HM	5C/A611	5C/A611	-	5.0	AUTOMATIC, CR
300-01C	3'-0"		7'-0"	1 3/4"	F	WD	AF1	HM	5B, 5C, 5D/A611	5C, 5D/A611	TS	5.0	AUTOMATIC, CR
300-02	3'-0"		7'-0"	1 3/4"	F	WD	A	HM	5C/A611	5C/A611	-	9.0	
300-03	3'-0"		7'-0"	1 3/4"	F	WD	DA	HM	5A/A611	5A/A611	-	9.1	DBL ACT
300-04	3'-0"		7'-0"	1 3/4"	F	WD	A	HM	5C/A611	5C/A611	-	2.0	
300-05	3'-0"		7'-0"	1 3/4"	F	WD	A	HM	5C/A611	5C/A611	-	1.0	
300-06	3'-0"		7'-0"	1 3/4"	F	WD	A	HM	5C/A611	5C/A611	-	1.0	
300-08	3'-0"		7'-0"	1 3/4"	F	WD	A	HM	5C/A611	5C/A611	-	1.0	
300-09	3'-0"		7'-0"	1 3/4"	F	WD	A	HM	5C/A611	5C/A611	-	1.0	
300-10	3'-0"		7'-0"	1 3/4"	F	WD	A	HM	5C/A611	5C/A611	-	3.0	
300-11	3'-0"		7'-0"	1 3/4"	F	WD	A	HM	5C/A611	5C/A611	-	1.0	
300-12A							AL	2D/A611	2B&3B/A611	TS			AD SYSTEM
300-12B							AL	2D/A611	2B&3B/A611	TS			AD SYSTEM
300-13	3'-0"		7'-0"	1 3/4"	F						-	6.0	
300-14	3'-0"		7'-0"	1 3/4"	F	WD	A	HM	5C/A611	5C/A611	-	6.0	CR
300-15	3'-0"		7'-0"	1 3/4"	F	WD	A	HM	5C/A611	5C/A611	-	8.0	
300-16	3'-0"		7'-0"	1 3/4"	N	WD	A	HM	5C/A611	5C/A611	-	6.1	AUTOMATIC, CR
300-17	3'-0"		7'-0"	1 3/4"	F	WD	A	HM	5C/A611	5C/A611	-	1.0	
300-18	3'-0"		7'-0"	1 3/4"	F	WD	A	HM	5C/A611	5C/A611	-	1.0	
300-19	3'-0"		7'-0"	1 3/4"	F	WD	A	HM	5C/A611	5C/A611	-	1.0	
300-20	3'-0"		7'-0"	1 3/4"	F	WD	A	HM	5C/A611	5C/A611	-	1.0	
300-21	3'-0"		7'-0"	1 3/4"	F	WD	A	HM	5C/A611	5C/A611	-	1.0	
300-22	3'-0"		7'-0"	1 3/4"	F	WD	A	HM	5C/A611	5C/A611	-	1.0	
300-23	3'-0"		7'-0"	1 3/4"	F	WD	A	HM	5C/A611	5C/A611	-	7.0	CR
300-23A	3'-0"		7'-0"	1 3/4"	F	WD	A	HM	5C/A611	5C/A611	-	7.0	CR
300-25	3'-0"		7'-0"	1 3/4"	F	WD	DA	HM	5A/A611	5A/A611	-	1.0	
300-26	3'-0"		7'-0"	1 3/4"	F	WD	A	HM	5C/A611	5C/A611	-	1.0	
300-27	3'-0"		7'-0"	1 3/4"	F	WD	A	HM	5C/A611	5C/A611	-	1.0	
300-28	3'-0"		7'-0"	1 3/4"	F	WD	A	HM	5C/A611	5C/A611	-	1.0	
300-29	3'-0"		7'-0"	1 3/4"	F	WD	A	HM	5C/A611	5C/A611	-	2.0	
300-29A							AL	2D/A611	2B&3B/A611	TS			AD SYSTEM
300-30	3'-0"		7'-0"	1 3/4"	F	WD	A	HM	5C/A611	5C/A611	-	1.0	
300-31	3'-0"		7'-0"	1 3/4"	F	WD	A	HM	5C/A611	5C/A611	-	9.0	
300-32	3'-0"		7'-0"	1 3/4"	F	WD	A	HM	5C/A611	5C/A611	-	1.0	
300-33	3'-0"		7'-0"	1 3/4"	F	WD	A	HM	5C/A611	5C/A611	-	1.0	
300-34	3'-0"		7'-0"	1 3/4"	F	WD	A	HM	5C/A611	5C/A611	-	1.0	
300-35	3'-0"		7'-0"	1 3/4"	F	WD	DA	HM	5A/A611	5A/A611	-	9.1	DBL ACT
300-37	3'-0"		7'-0"	1 3/4"	F	WD	A	HM	5C/A611	5C/A611	-	2.0	
300-38	3'-0"		7'-0"	1 3/4"	N	WD	A	HM	5C/A611	5C/A611	-	6.0	CR

DOOR TYPE DESIGNATIONS

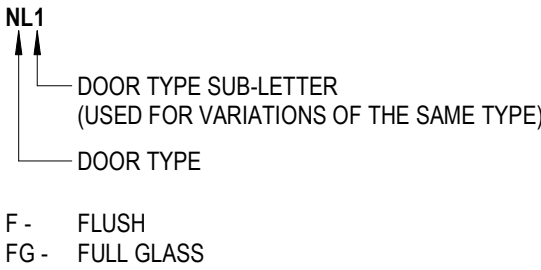

FRAME TYPE DESIGNATIONS

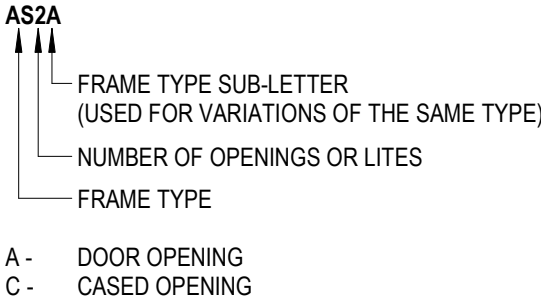

DOOR / FRAME MATERIAL

GL - GLASS
HM - HOLLOW METAL
WD - WOOD, WOOD VENEER


GLASS MATERIAL

PG - PATTERN GLASS
TS - TEMPERED SAFETY GLASS

HARDWARE SETS


SEE DOOR HARDWARE SPEC

WOOD AND HOLLOW METAL DOORS

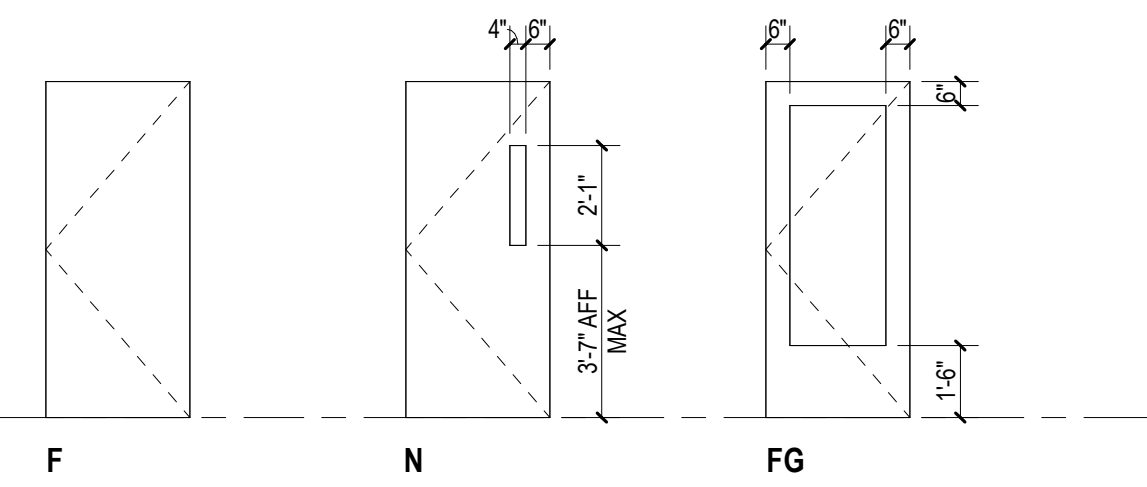


FRAMES

SEE DOOR SCHEDULE FOR DOOR OPENING SIZES AND HEAD / JAMB DETAIL DESIGNATIONS.
REFER TO TYPICAL HOLLOW METAL FRAME DETAILS FOR FRAME PROFILES, DIMENSIONS, ANCHORAGE, ETC.

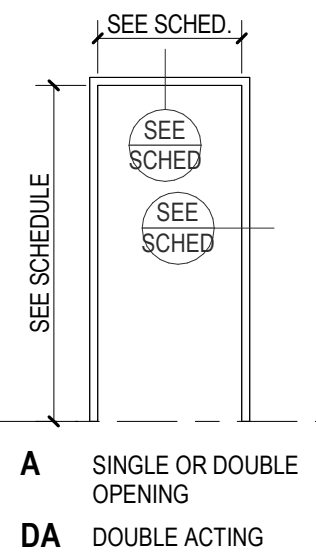

BORROWED LITES

SEE DOOR SCHEDULE FOR DOOR OPENING SIZES AND HEAD / JAMB DETAIL DESIGNATIONS.
FRAME TYPE ELEVATIONS SHOW GLASS OPENING DIMENSIONS AND INTERMEDIATE MULLION WIDTHS ONLY.
REFER TO TYPICAL HOLLOW METAL FRAME DETAILS FOR FRAME PROFILES, DIMENSIONS, ANCHORAGE, ETC.

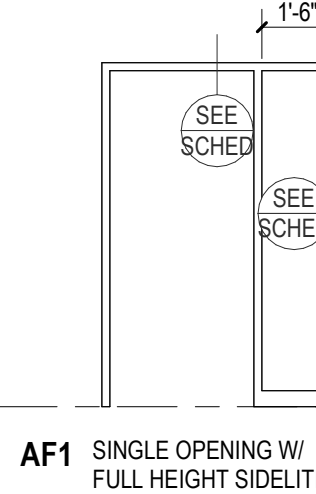

GENERAL DOOR NOTES

- ALL DOORS ARE 1 3/4" THICKNESS, UNLESS OTHERWISE NOTED.
- ALL WOOD DOORS ARE SOLID CORE UNLESS OTHERWISE NOTED.
- ALL INTERIOR GLASS IS 1/4" AND ALL INSULATED GLASS IS 1" UNLESS OTHERWISE INDICATED.
- REFER TO HARDWARE SCHEDULE ATTACHED TO DIVISION 8, SECTION "FINISH HARDWARE" FOR HARDWARE SET DESCRIPTIONS.
- REFER TO TYPICAL PARTITION DETAILS FOR FRAME THROAT REQUIREMENTS UNLESS OTHERWISE INDICATED ON DOOR SCHEDULE.
- REFER TO TYPICAL HOLLOW METAL FRAME DETAILS FOR FRAME PROFILES, DIMENSIONS, ANCHORAGE, ETC.
- ALL DOORS TO HAVE STANDARD 5/8" UNDERCUT (UNLESS OTHERWISE INDICATED OR REQUIRED TO RECEIVE SCHEDULED THRESHOLD). UNDERCUT DIMENSION IS MEASURED FROM UNDERSIDE OF DOOR LEAF TO TOP OF FLOOR FINISH OR TOP OF THRESHOLD. REFER TO TYPICAL INTERIOR DETAILS - FLOOR TRANSITIONS/THRESHOLD DETAILS.
- 20, 45, 60, 90, ETC. INDICATES FIRE RATING IN MINUTES.
- A PREFIX OF "E" MEANS EXISTING DOOR OR FRAME BEING REUSED.

REMARKS NOTATION

- AUTOMATIC DBL ACT OR
HAND SWING OPERATED AUTOMATIC DOOR DOUBLE ACTION SWING (NO STOPS AT FRAME) CARD READER
- NOTE A: REFER TO DRAWING A611 (INSERT DRAWING NUMBER HERE) FOR ALUMINUM FRAME ELEVATIONS AND DETAIL REFERENCES. ALUMINUM DOOR MANUFACTURER SHALL VERIFY DOOR DIMENSIONS BASED UPON APPROVED SYSTEM STANDARDS.
- NOTE B: MODIFY EXISTING DOOR AND/OR FRAME AS REQUIRED TO ACCOMMODATE INSTALLATION OF NEW HARDWARE.
- NOTE C: REFINISH EXISTING WOOD DOOR. REFER TO FINISH SCHEDULE FOR SURFACE PREPARATION AND FINISH SYSTEMS REMOVE EXISTING HARDWARE SCHEDULED TO REMAIN PRIOR TO REFINISHING AND REINSTALL.

80 Glastonbury Boulevard
Glastonbury, CT 06033-4410
Phone: 860 657.8077

www.slamcoll.com


Drawn
ES, JC
Checked
SRD

YaleNewHavenHealth

Northeast
Medical Group
Ambulatory
Expansion

440 Mamaroneck Ave.
Harrison, NY

Suite 301

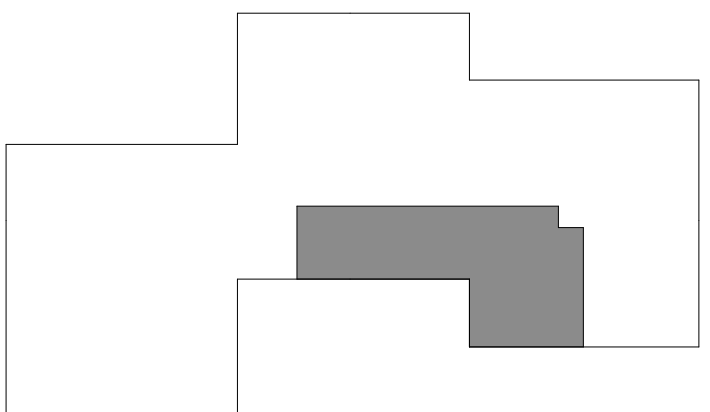

Number	Date	Issued For

DOOR AND FRAME TYPES,
DOOR SCHEDULE

Date
4/10/2026
Scale
1/4" = 1'-0"
Proj. Number
25195.25
Drawing Number
A610