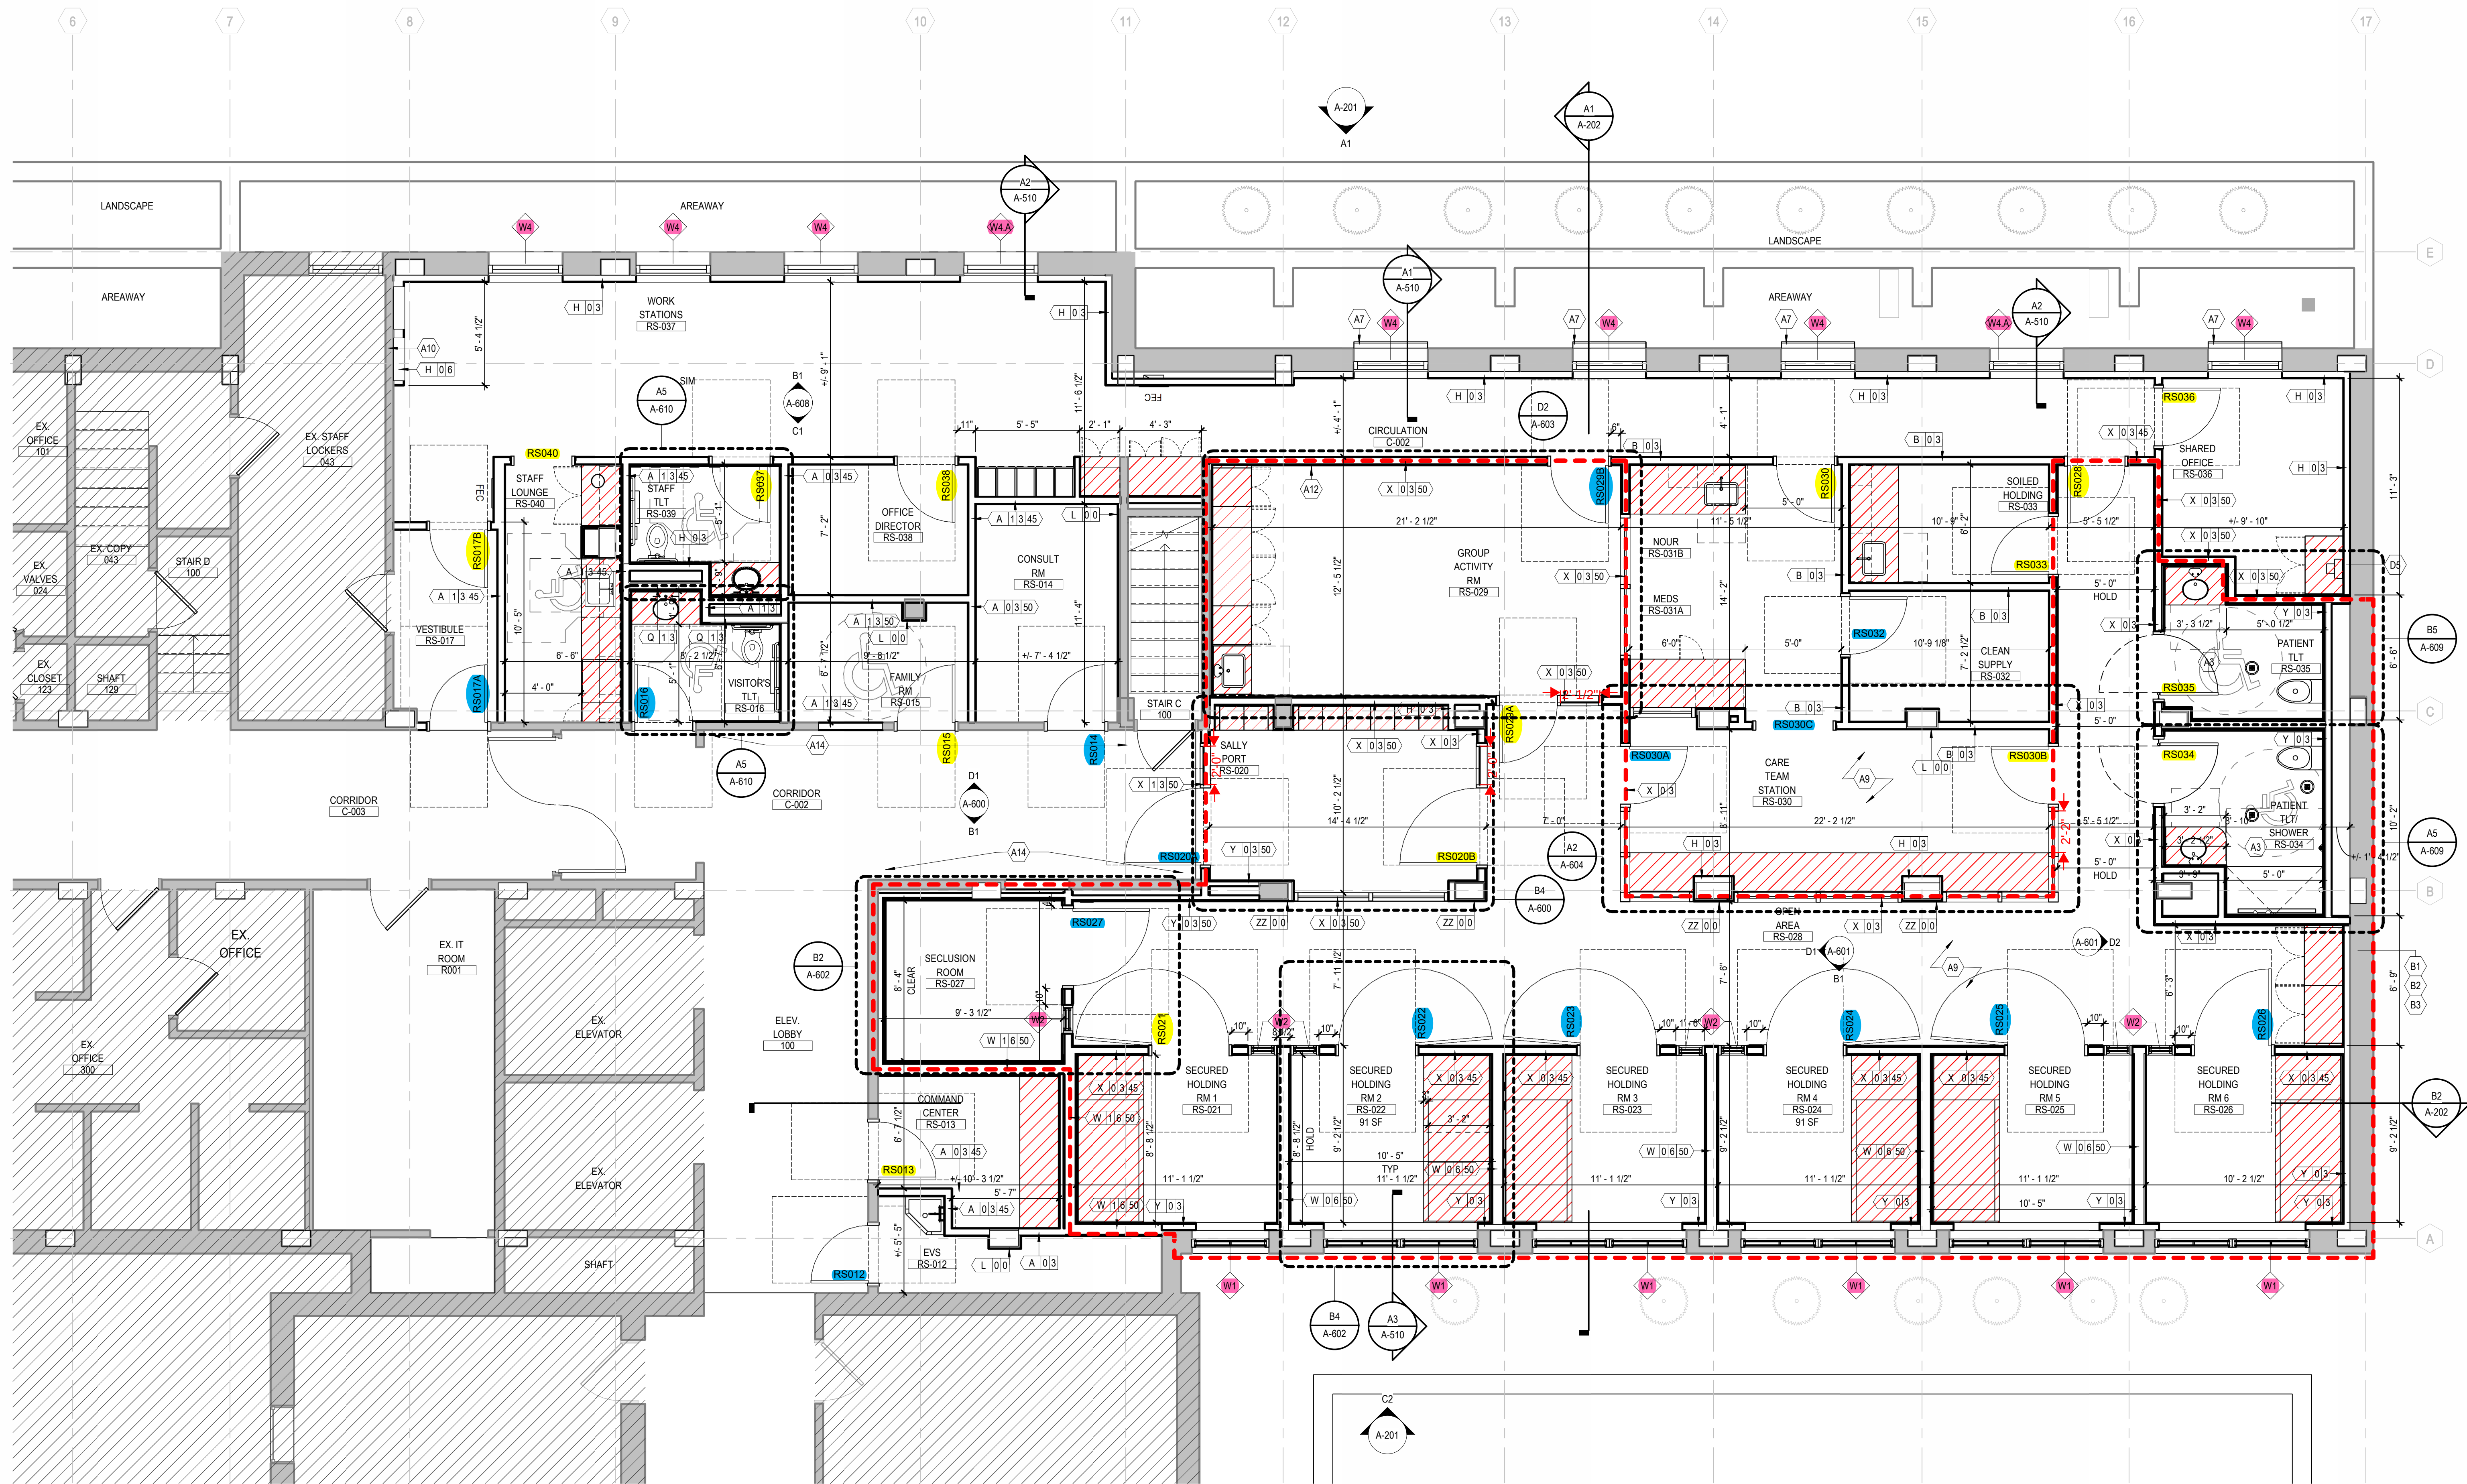




A1 FIRST FLOOR PLAN - AREA 1
1/4" = 1'-0"

ARCHITECTURAL PLAN NOTES

1. OPENINGS SHALL BE LOCATED 6" FROM ADJACENT PARTITIONS UNLESS INDICATED OTHERWISE.

**Montefiore
Einstein*****nbbj***

111 FIFTH AVENUE, 10TH FLOOR
NEW YORK, NY 10003
PHONE 212 924 9000
www.nbbj.com

OWNER:
MONTEFIORE MOSES MEDICAL CENTER
111 EAST 210TH STREET
NEW YORK, NY 10003

STRUCTURAL ENGINEER:
LERA
40 WALL STREET, FLOOR 23
NEW YORK, NY 10005
212-750-9000

MEP:
WSP
200 LIBERTY STREET, SUITE 302
NEW YORK, NY 10281
212-465-5000

 
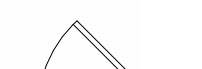
MONTEFIORE
MEDICAL CENTER
CPEP BHCOE

ISSUE FOR BID

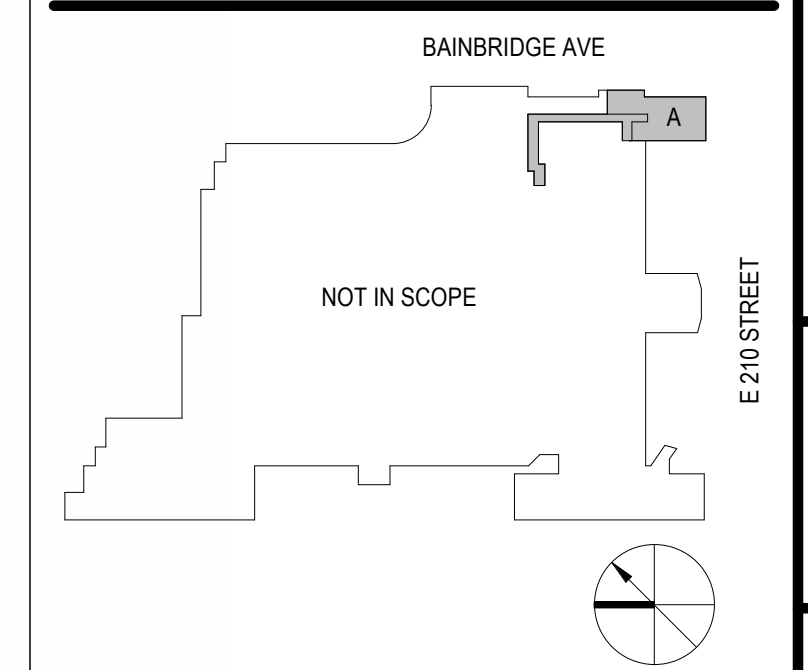
KEYNOTES ARCHITECTURAL

KEYNOTE	DESCRIPTION
A3	ANTI-LIGATURE COMPLIANT PLUMBING FIXTURES
A7	STEEL WINDOW SECURITY GUARD, SEE SPEC, COLOR WHITE
A9	NEW FLOOR SLAB. SEE STRUCT. DWGS FOR ADDITIONAL INFO.
A10	EXISTING PARTITIONS TO BE REPAIRED AND PATCHED AS REQUIRED TO ACHIEVE A MINIMUM 1-HOUR FIRE-RESISTANCE RATING TYP.
A12	CLERESTORY WINDOWS ABOVE, SEE ELEVATION.
A14	PATCH AND REPLACED 4'-0" OF GYPSUM BOARD, FLUSH WITH EXISTING GYPSUM BOARD.
B1	ALL PARTITIONS FOR THE PATIENT AREA WITHIN THE RED LINE BOUNDARY ARE TO BE CONSTRUCTED WITH IMPACT-RESISTANT GYPSUM BOARD.
B2	ALL GLAZING FOR THE PATIENT AREA WITHIN THE RED LINE BOUNDARY ARE POLYCARBONATE GLAZING.
B3	ALL DOOR HARDWARE WITHIN THE RED LINE BOUNDARY TO BE LIGATURE-RESISTANT.
D5	EXISTING GAS METER TO REMAIN.

PLAN LEGEND

	EXISTING PARTITION
	NEW PARTITION
	BOUNDARY OF BEHAVIORAL PATIENT AREA
	EXISTING DOOR TO REMAIN
	NEW DOOR
	MILLWORK
	AREA NOT IN SCOPE (FOR ARCHITECTURAL WORK ONLY)

KEYPLAN

[illegible]

PROJECT NUMBER	103435.00
PROJECT ARCHITECT	DT
NYC DOB NUMBER	
CON NUMBER	

FIRST FLOOR
PLAN - AREA 1

SHEET NUMBER

A-103.00

NYC DOB STAMP

NYC DOB BSCAN

