


B1.1

UNIT PLAN NOTES

1. ALL INTERIOR DIMENSIONS TO WOOD FRAME PARTITIONS ARE TO FACE OF FRAMING. ALL INTERIOR DIMENSIONS TO METAL FRAME PARTITIONS ARE TO FACE OF FINISH AND ARE NOTED WITH ASTERISKS "X". ALL OTHER DIMENSIONS ARE AS SHOWN.
2. ALL UNIT INTERIOR PARTITIONS TO BE WALL TYPE XX UNLESS OTHERWISE NOTED.
3. LOCATE DOOR OPENINGS 4" FROM ADJACENT WALL UNLESS OTHERWISE NOTED.
4. SEE MECHANICAL AND PLUMBING DRAWINGS FOR EQUIPMENT SPECIFICATIONS.
5. SEE ELECTRICAL AND LOW VOLTAGE DRAWINGS FOR POWER AND LOW VOLTAGE PLANS.


KEYNOTES

#	DESCRIPTION
01	MECH. CHASE REF. MEP DRAWINGS
02	ELECTRICAL LOAD CENTER. REFER TO ELEC. DRAWINGS
03	NID BOX REF. TO ELEC. FOR MORE INFO
04	WALL RETURN REF. TO ELEC. DRAWINGS

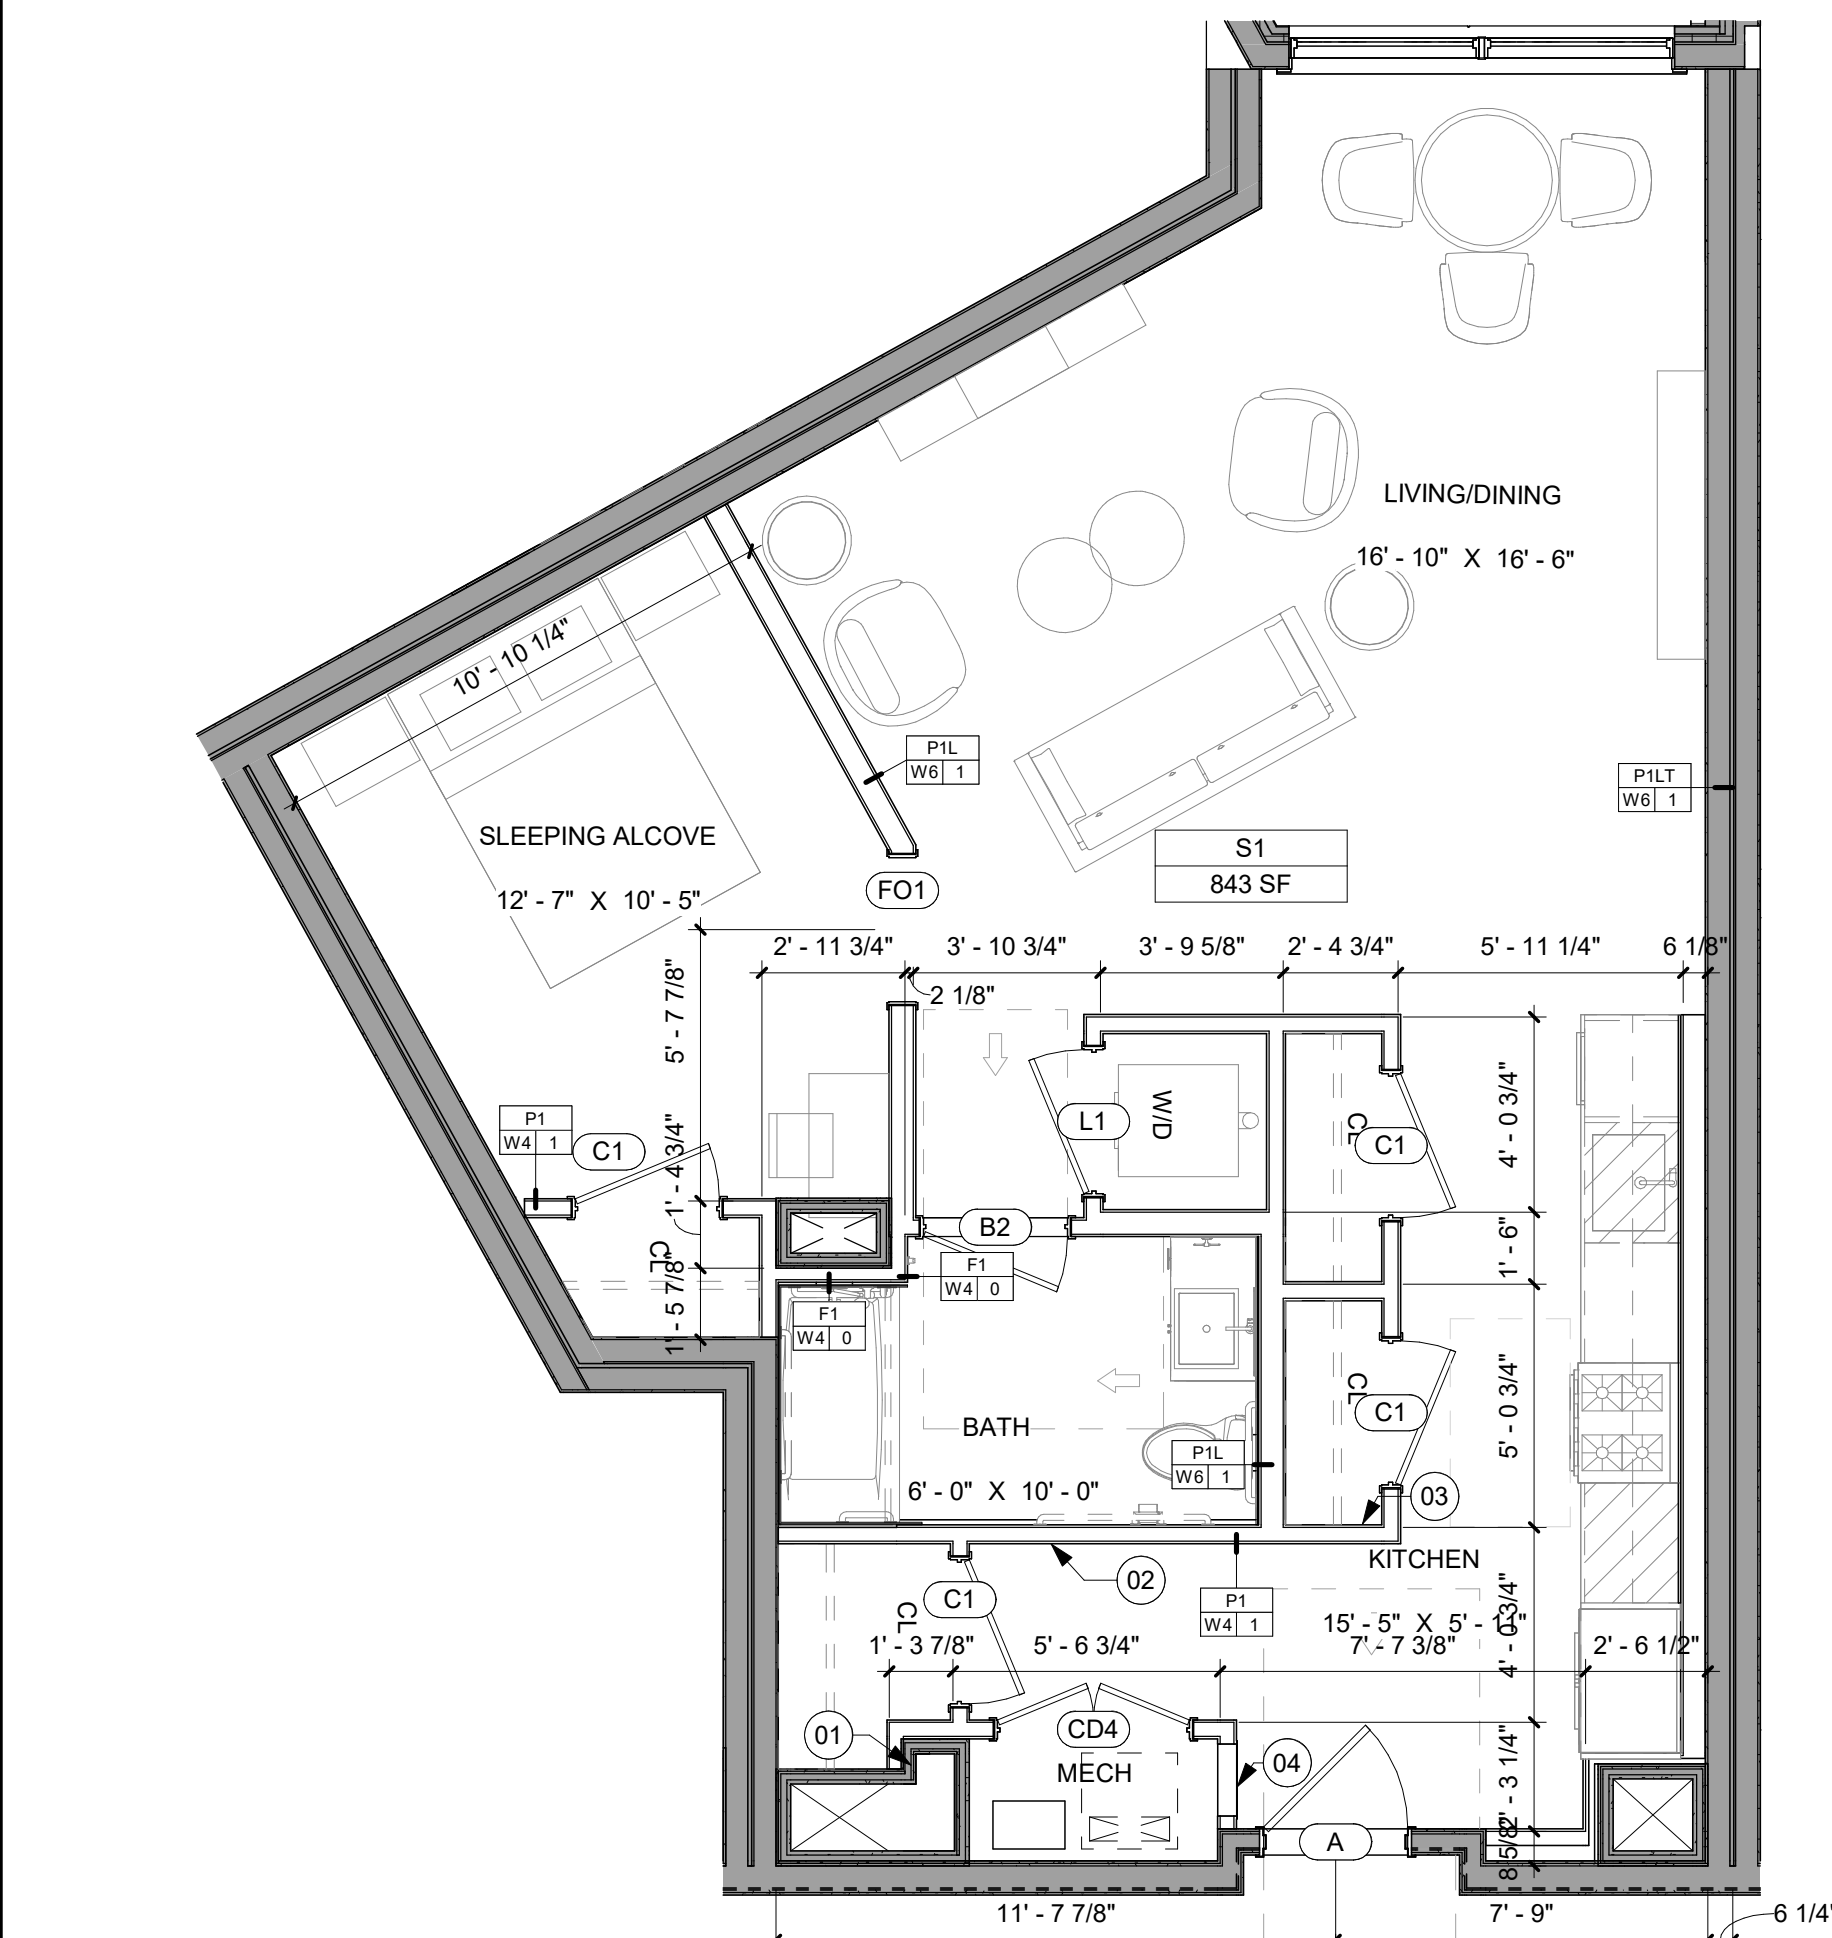


7 UNIT TYPE S1
SCALE: 1/4" = 1'-0"

UNIT TYPE	KITCHEN TYPE	BATHROOM TYPE	COUNT	AREA
S1	K6	B2	4	843 SF

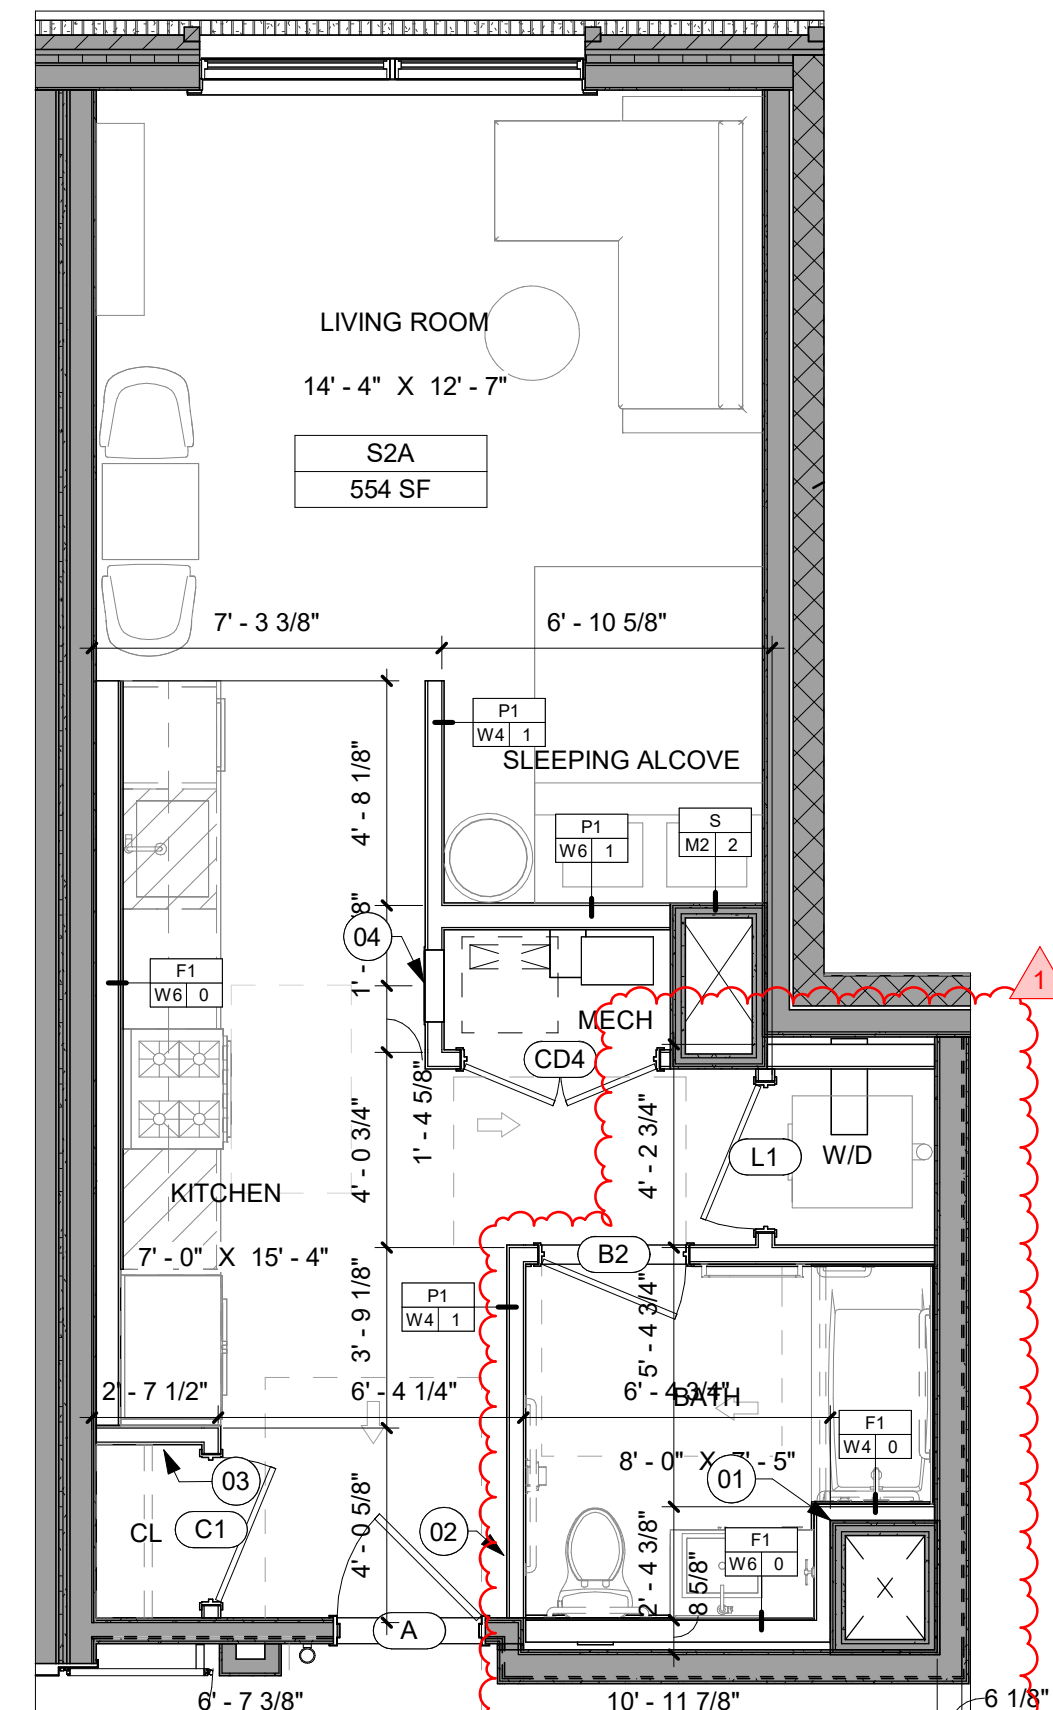


6 UNIT TYPE S2A - AFFORDABLE
SCALE: 1/4" = 1'-0"

UNIT TYPE	KITCHEN TYPE	BATHROOM TYPE	COUNT	AREA
S2A	K6	B7	4	554 SF

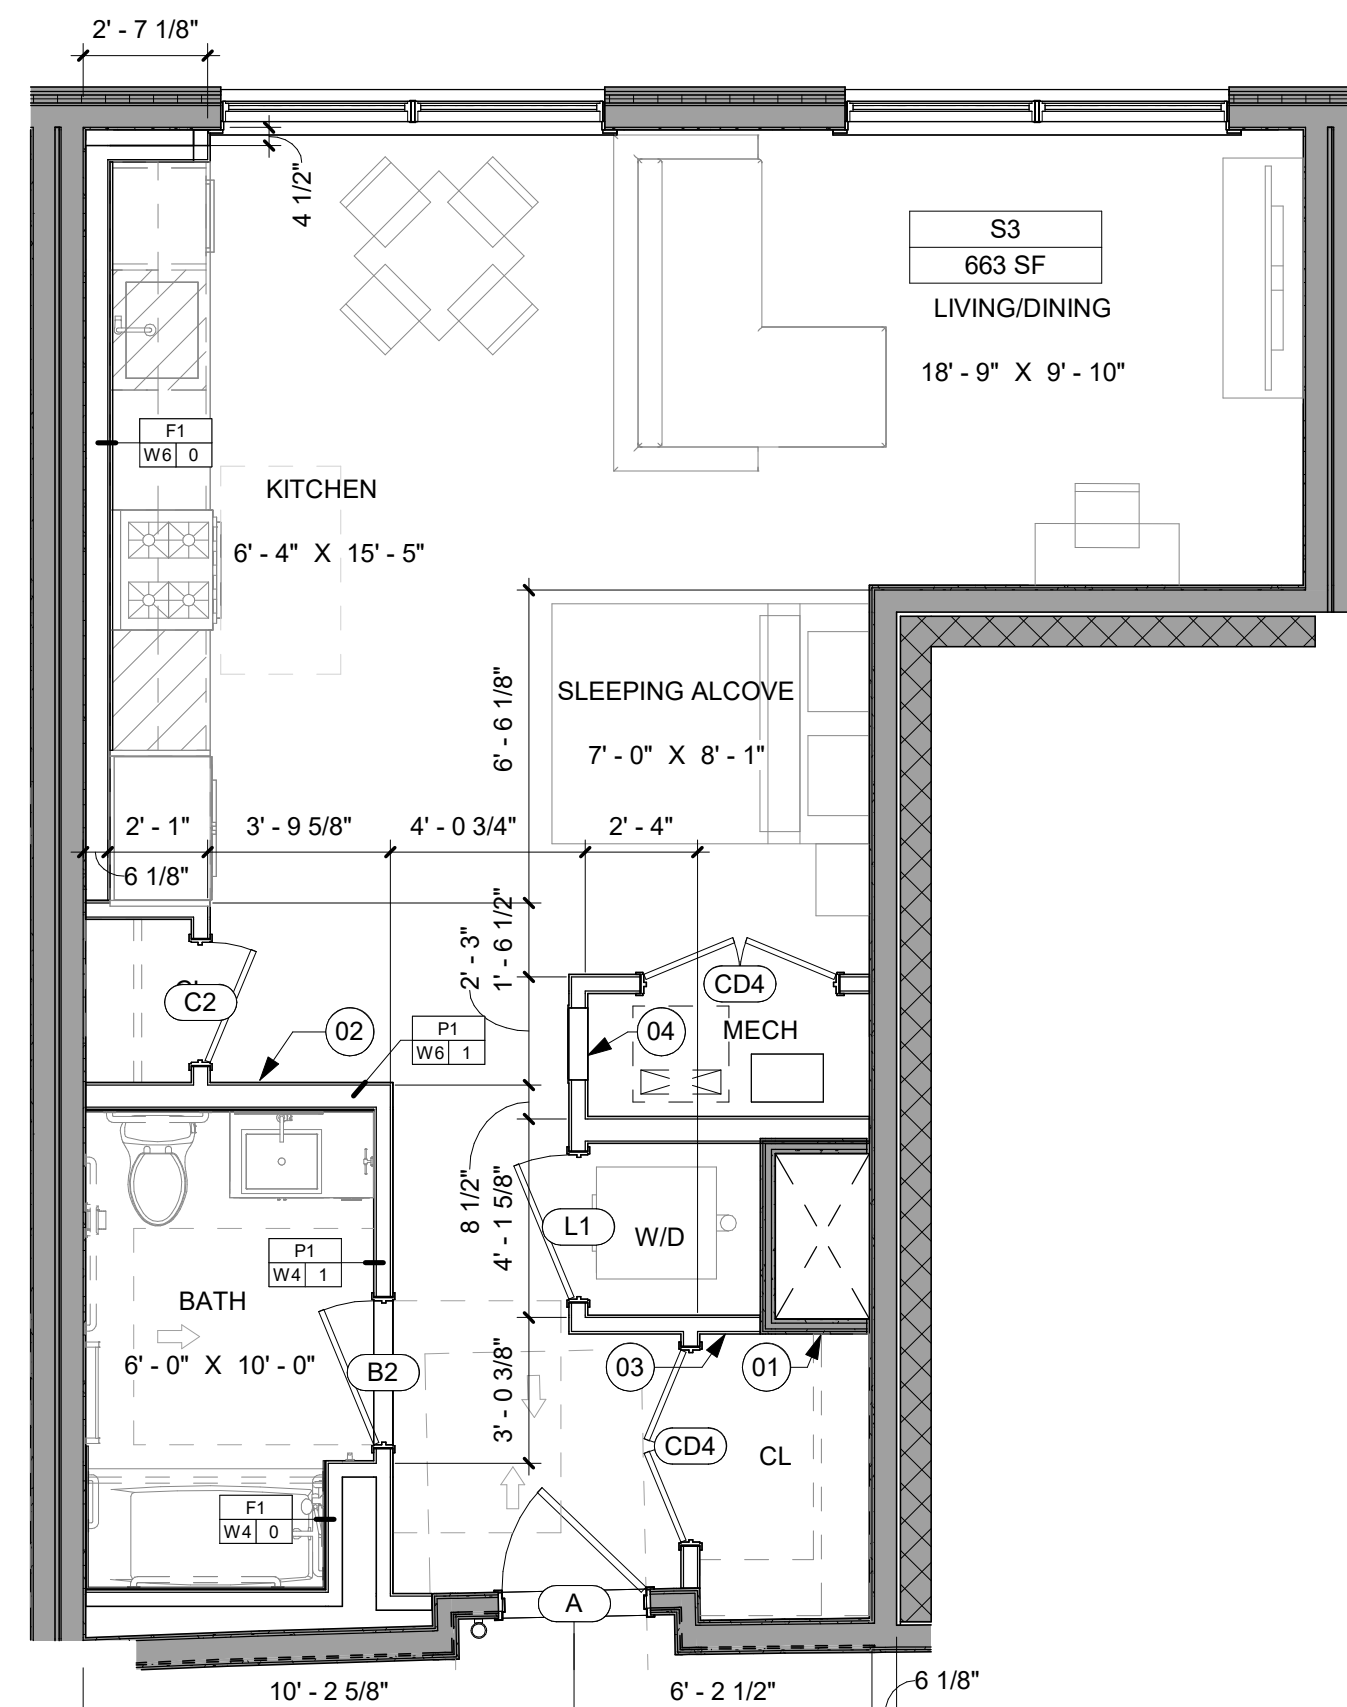


5 UNIT TYPE - S3
SCALE: 1/4" = 1'-0"

UNIT TYPE	KITCHEN TYPE	BATHROOM TYPE	COUNT	AREA
S3	K6	B2	3	663 SF

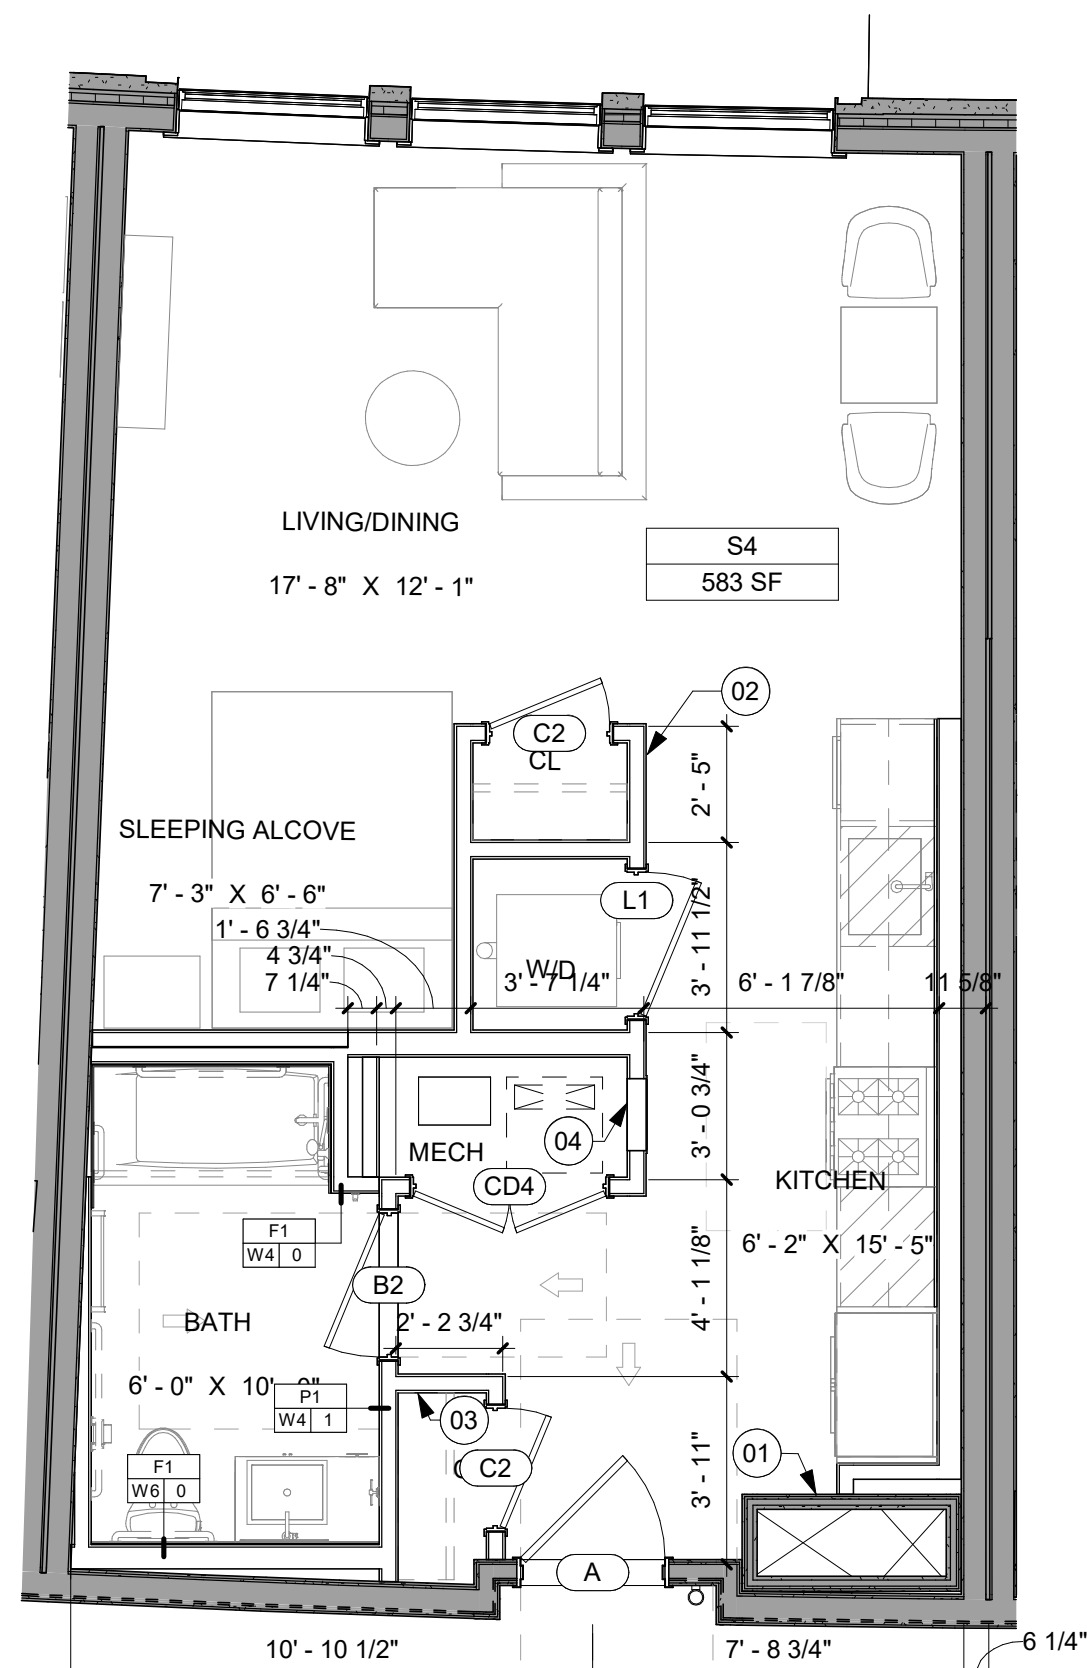


4 UNIT TYPE - S4
SCALE: 1/4" = 1'-0"

UNIT TYPE	KITCHEN TYPE	BATHROOM TYPE	COUNT	AREA
S4	K6	B2	3	583 SF - 585 SF

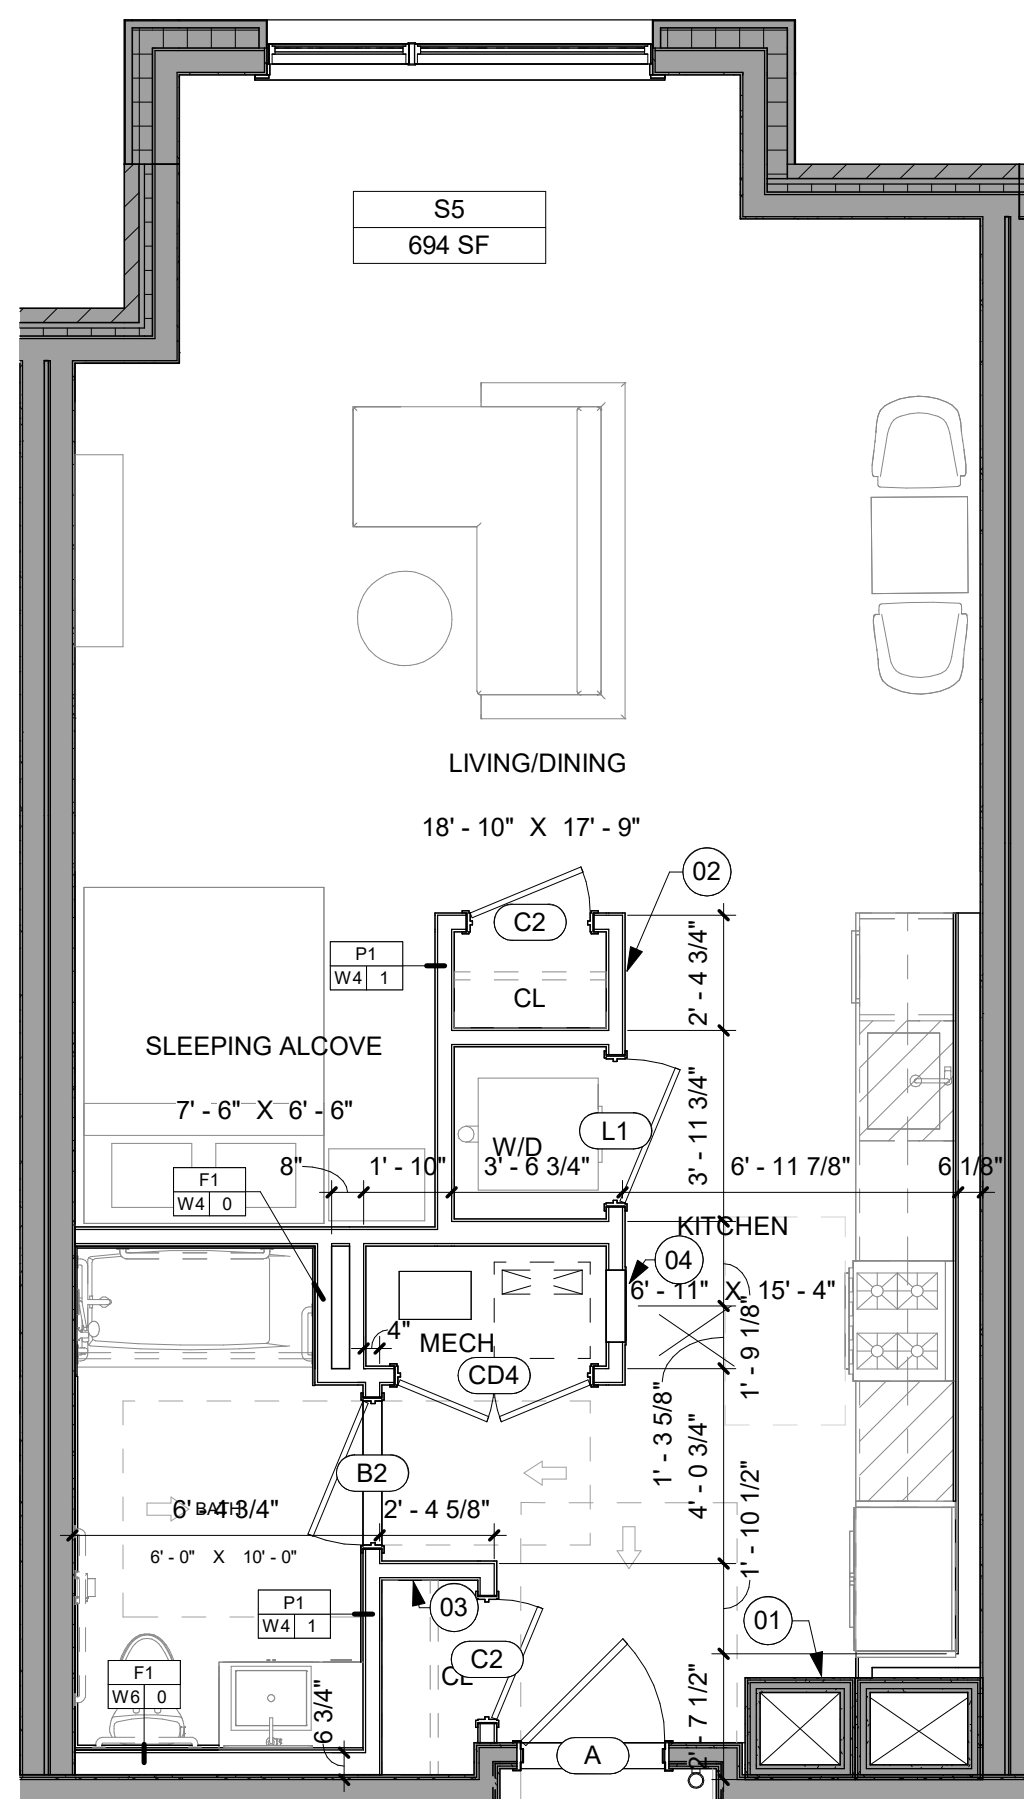


3 UNIT TYPE - S5
SCALE: 1/4" = 1'-0"

UNIT TYPE	KITCHEN TYPE	BATHROOM TYPE	COUNT	AREA
S5	K6	B9.1	3	656 SF - 694 SF

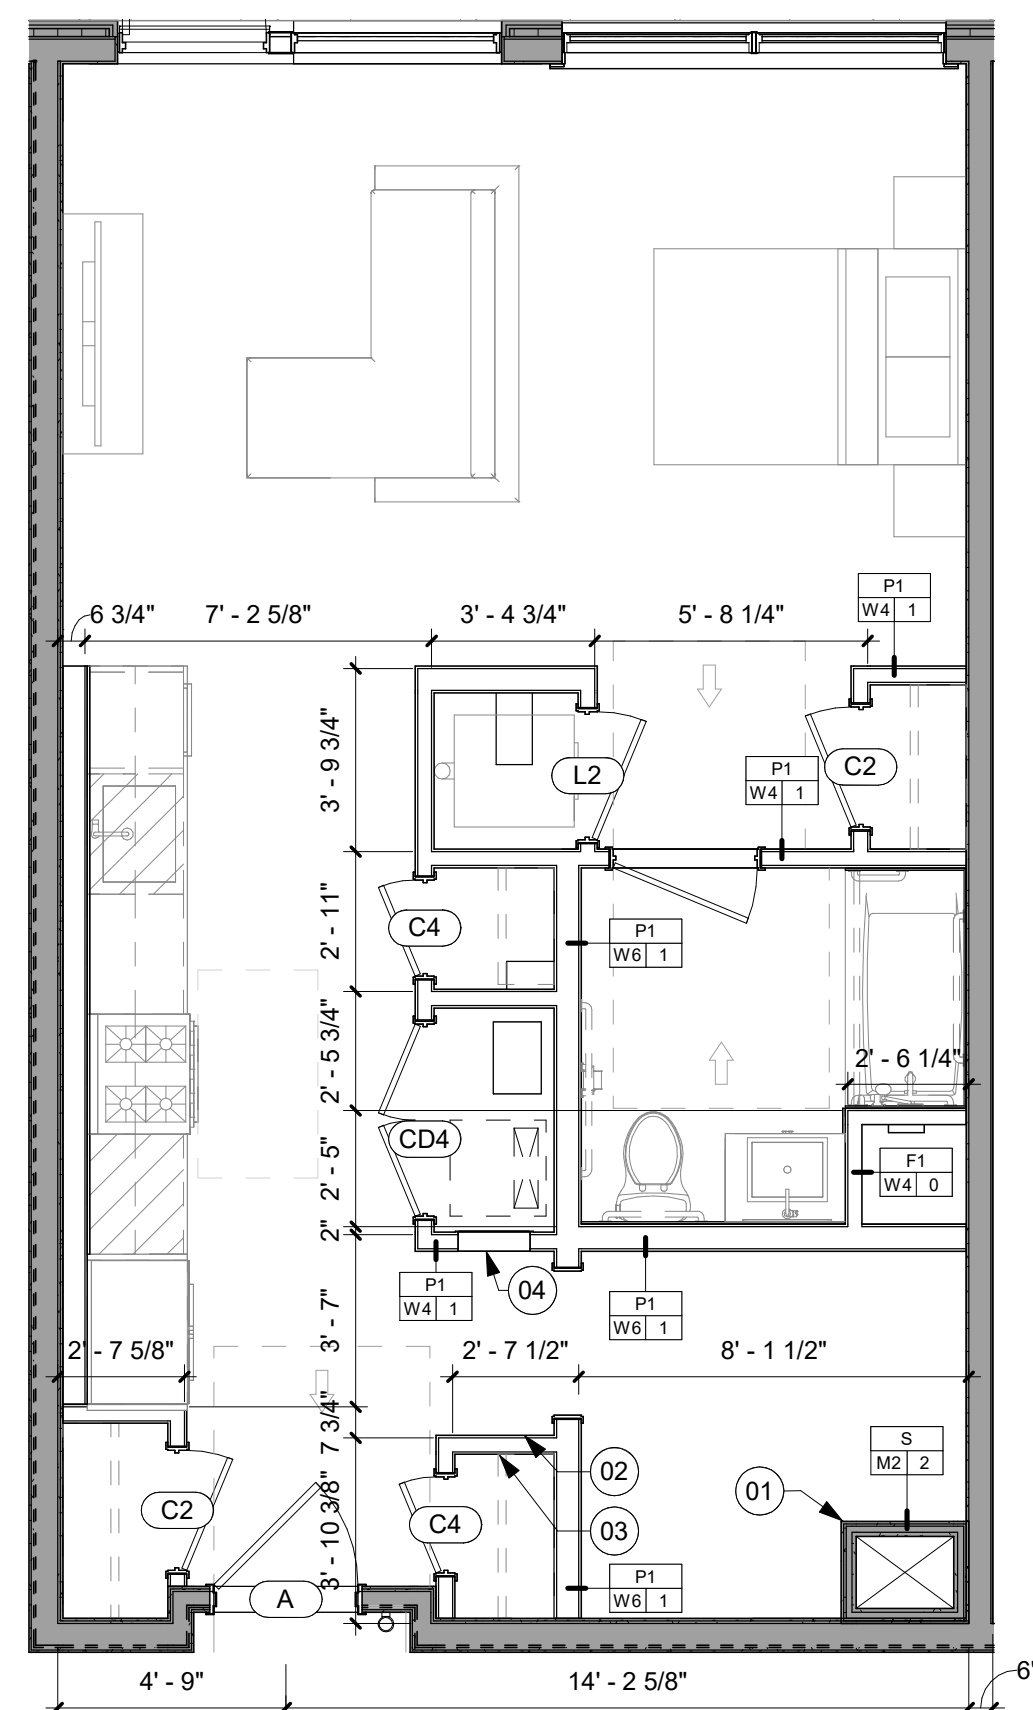

2 UNIT TYPE - S6
SCALE: 1/4" = 1'-0"

UNIT TYPE	KITCHEN TYPE	BATHROOM TYPE	COUNT	AREA
S6	K6	B8	1	660 SF

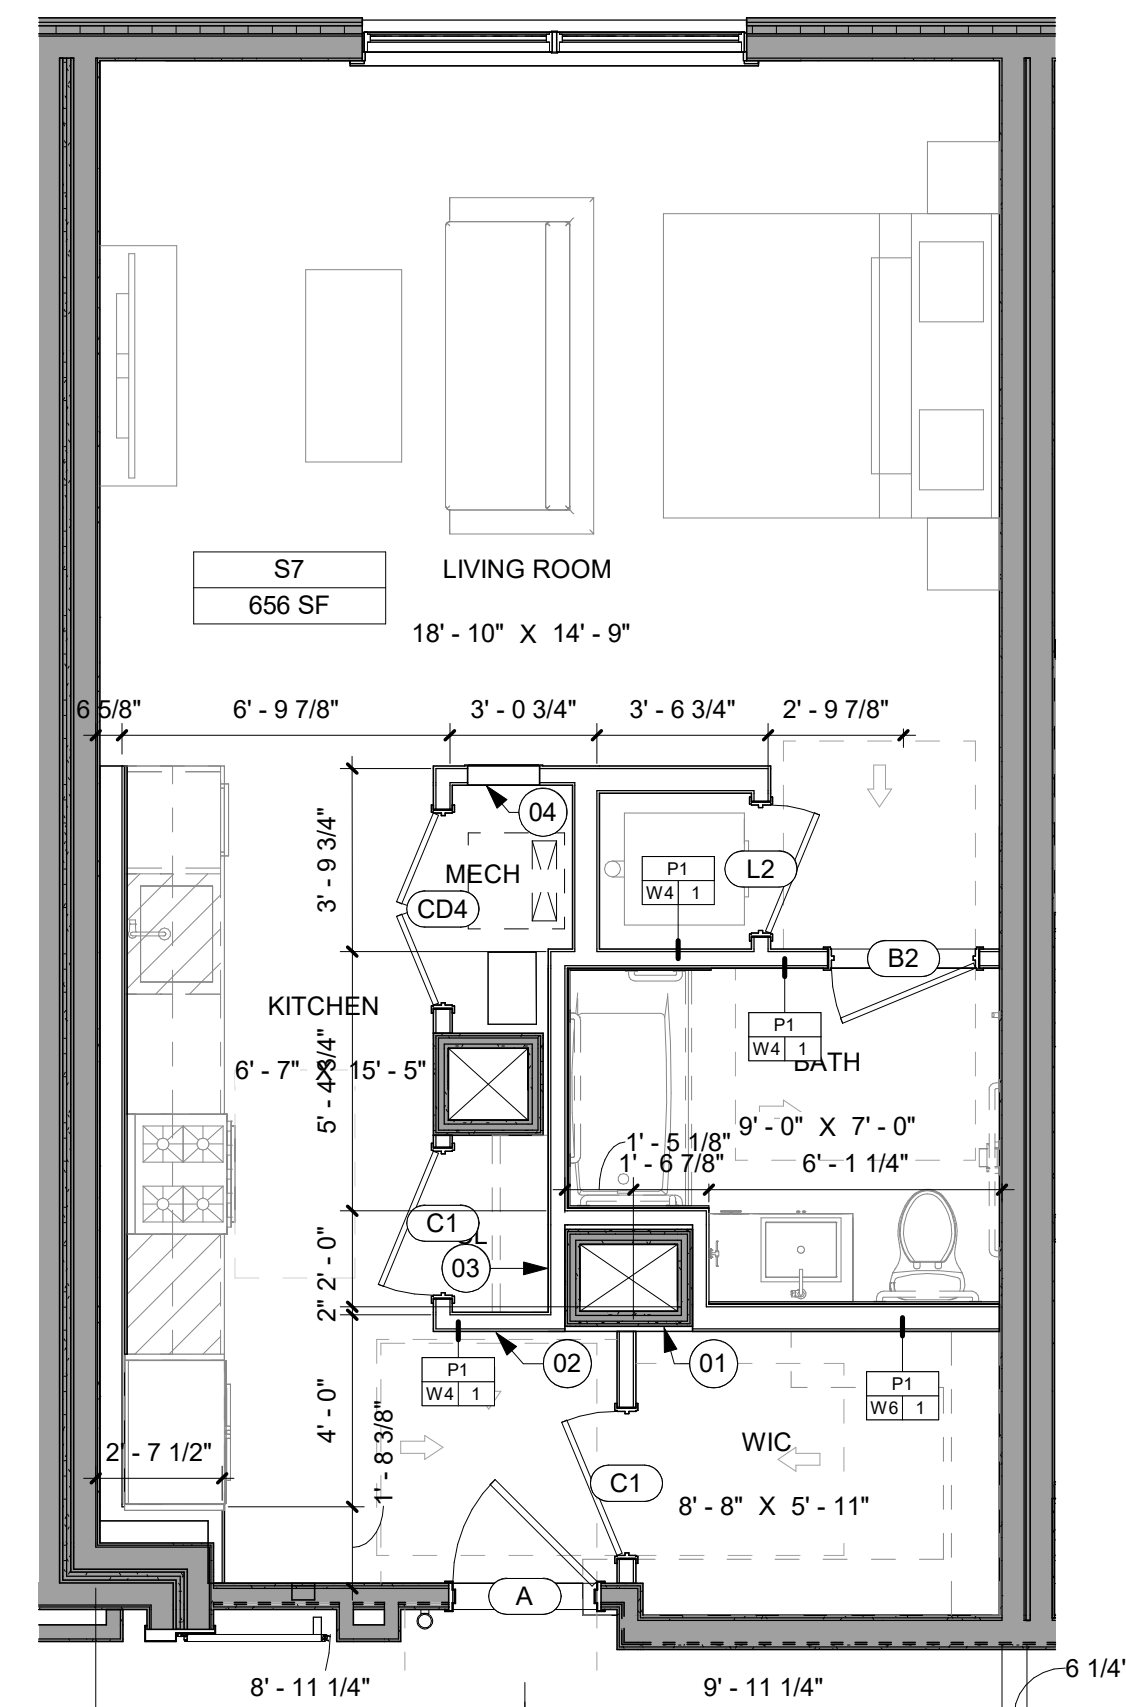

1 UNIT TYPE - S7
SCALE: 1/4" = 1'-0"

UNIT TYPE	KITCHEN TYPE	BATHROOM TYPE	COUNT	AREA
S7	K6	B1	1	656 SF



1422 Grand Street
Suite 5b
Hoboken, NJ 07030
T.201-795-1505
MHSarchitecture.com

PROJECT NAME:

**MORRISTOWN GREEN
APARTMENTS**
22 LAFAYETTE AVENUE
TOWN OF MORRISTOWN, NEW JERSEY

PREPARED FOR:

**MORRISTOWN
ASSOCIATES LLC**
4 CUNNINGHAM DRIVE
WEST ORANGE, NJ

ISSUE

#	DATE	FOR:
1	06/03/2026	BID SET
1	07/09/26	ADDENDUM #1

ENLARGED UNIT PLANS - ST

	PROJECT NUMBER:	2202
	SCALE:	As indicated
	DRAWN BY:	CM / TM / JE
	CHECKED BY:	FT / MB

A09.01

Copyright © 2026 MHS Architecture