

- UNIT PLAN NOTES
- ALL INTERIOR DIMENSIONS TO WOOD FRAME PARTITIONS ARE TO FACE OF FRAMING. ALL INTERIOR DIMENSIONS TO METAL FRAME PARTITIONS ARE TO FACE OF FINISH AND ARE NOTED WITH ASTERISKS "X-X". ALL OTHER DIMENSIONS ARE AS SHOWN.
 - ALL UNIT INTERIOR PARTITIONS TO BE WALL TYPE XX UNLESS OTHERWISE NOTED.
 - LOCATE DOOR OPENINGS 4" FROM ADJACENT WALL UNLESS OTHERWISE NOTED.
 - SEE MECHANICAL AND PLUMBING DRAWINGS FOR EQUIPMENT SPECIFICATIONS.
 - SEE ELECTRICAL AND LOW VOLTAGE DRAWINGS FOR POWER AND LOW VOLTAGE PLANS.

KEYNOTES	
#	DESCRIPTION
01	MECH. CHASE REF. MEP DRAWINGS
02	ELECTRICAL LOAD CENTER. REFER TO ELEC. DRAWINGS
03	IND BOX REF. TO ELEC. FOR MORE INFO
04	WALL RETURN REF. TO ELEC. DRAWINGS

Dean Marchetto, FAIA, PP
NJ 07045
Michael Higgins, AIA, LEED
NJ21A0130830
Bruce A. Silver, AIA
NJ21A0137710
Michael Buldo, AIA
NJ21A01708800
NY 035161
Vincent Marchetto, AIA
NJ21A02151000

MHS
ARCHITECTURE

1422 Grand Street
Suite 5b
Hoboken, NJ 07030
T.201-795-1505
MHSArchitecture.com

PROJECT NAME:
**MORRISTOWN GREEN
APARTMENTS**
22 LAFAYETTE AVENUE
TOWN OF MORRISTOWN, NEW JERSEY

PREPARED FOR:
**MORRISTOWN
ASSOCIATES LLC**
4 CUNNINGHAM DRIVE
WEST ORANGE, NJ





ISSUE	
#	DATE
1	06/03/2026
FOR:	
BID SET	ADDENDUM #1

ENLARGED UNIT PLANS -
ST

	PROJECT NUMBER:	2202
	SCALE:	As indicated
	DRAWN BY:	CM / TM / JE
	CHECKED BY:	FT / MB

A09.02

Copyright © 2026 MHS Architecture

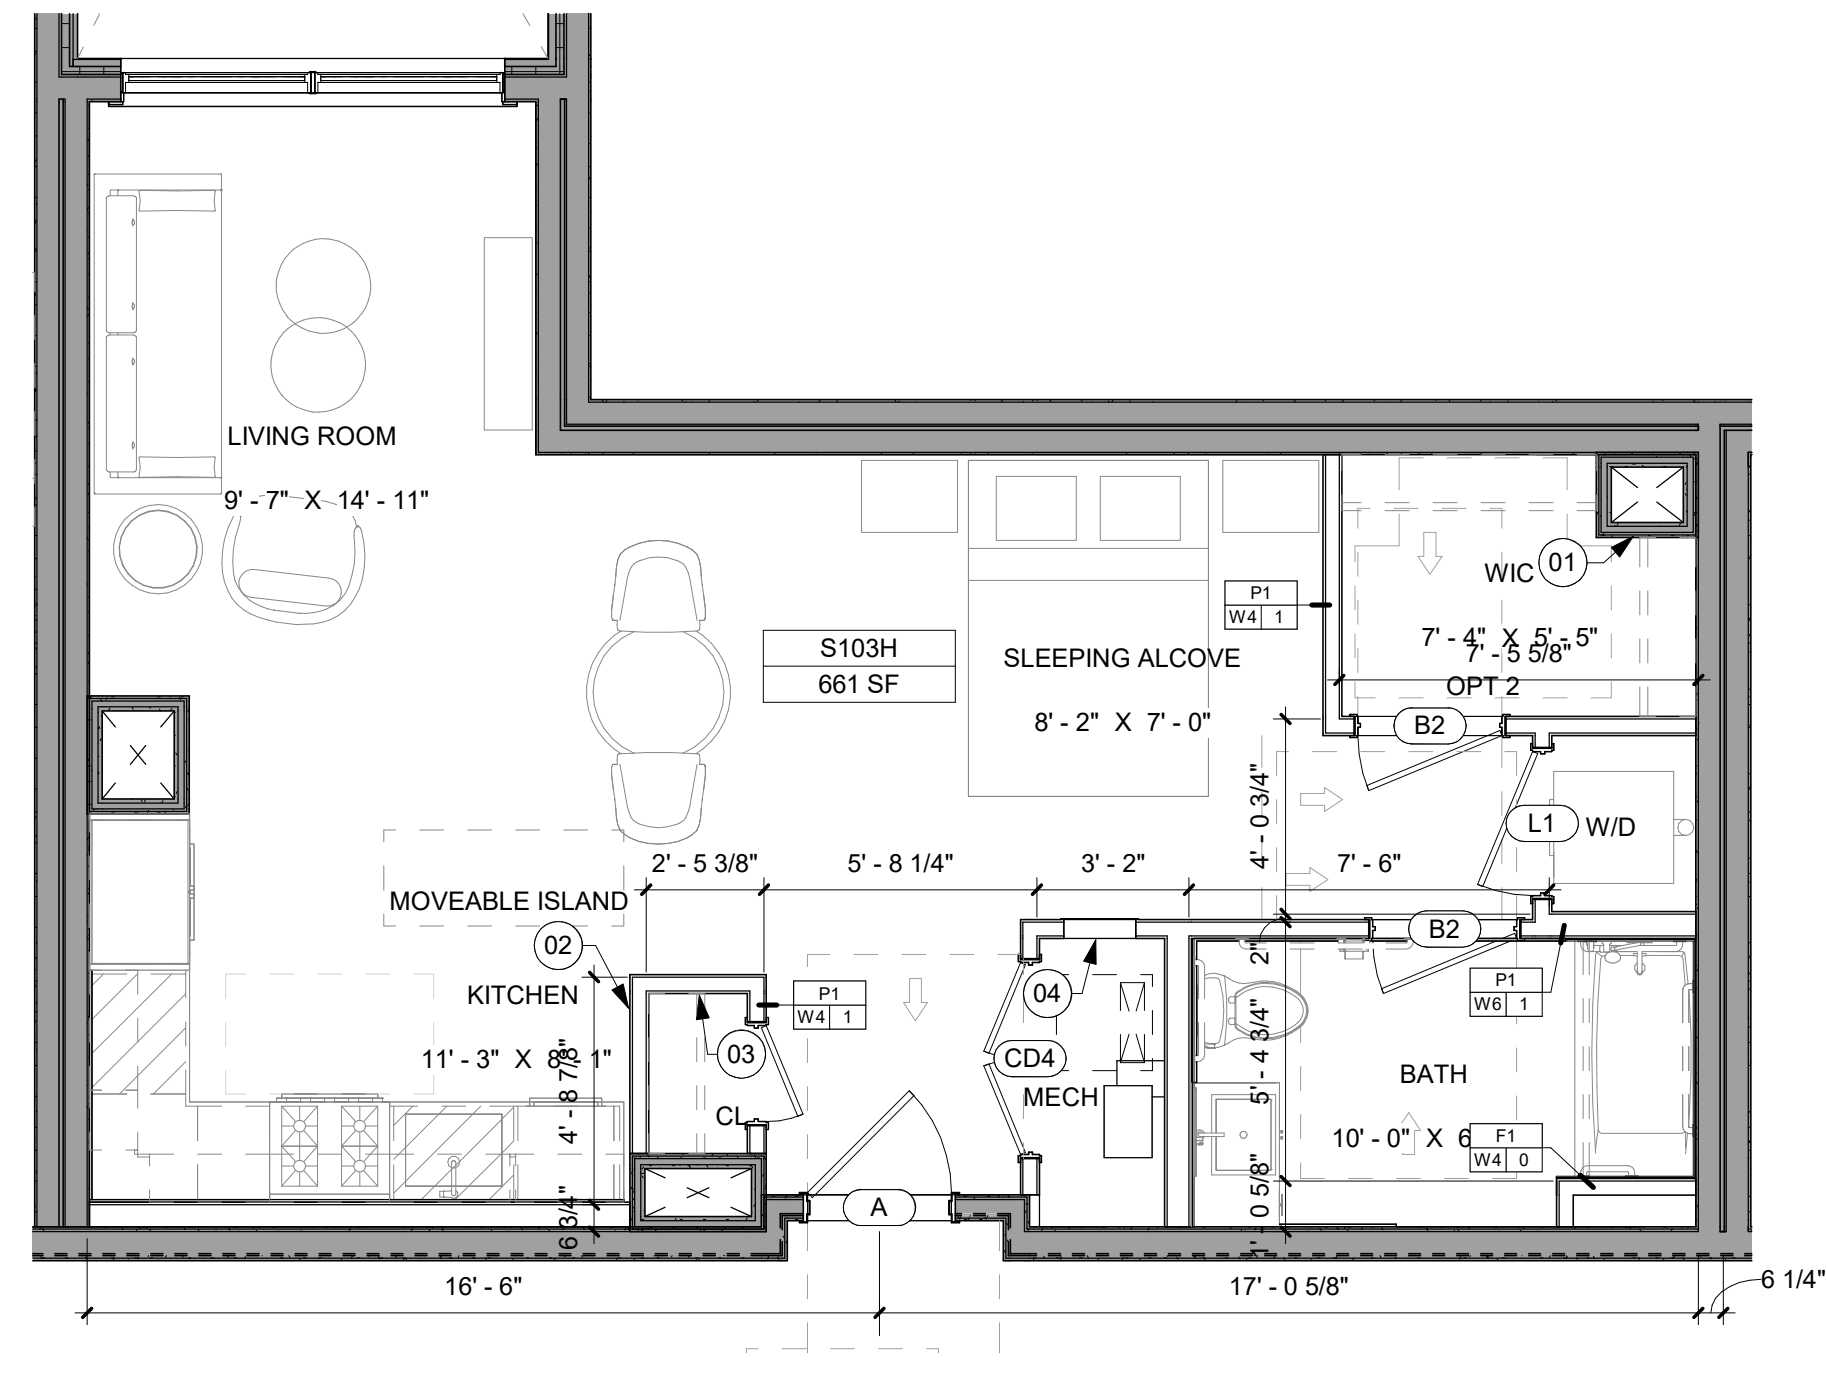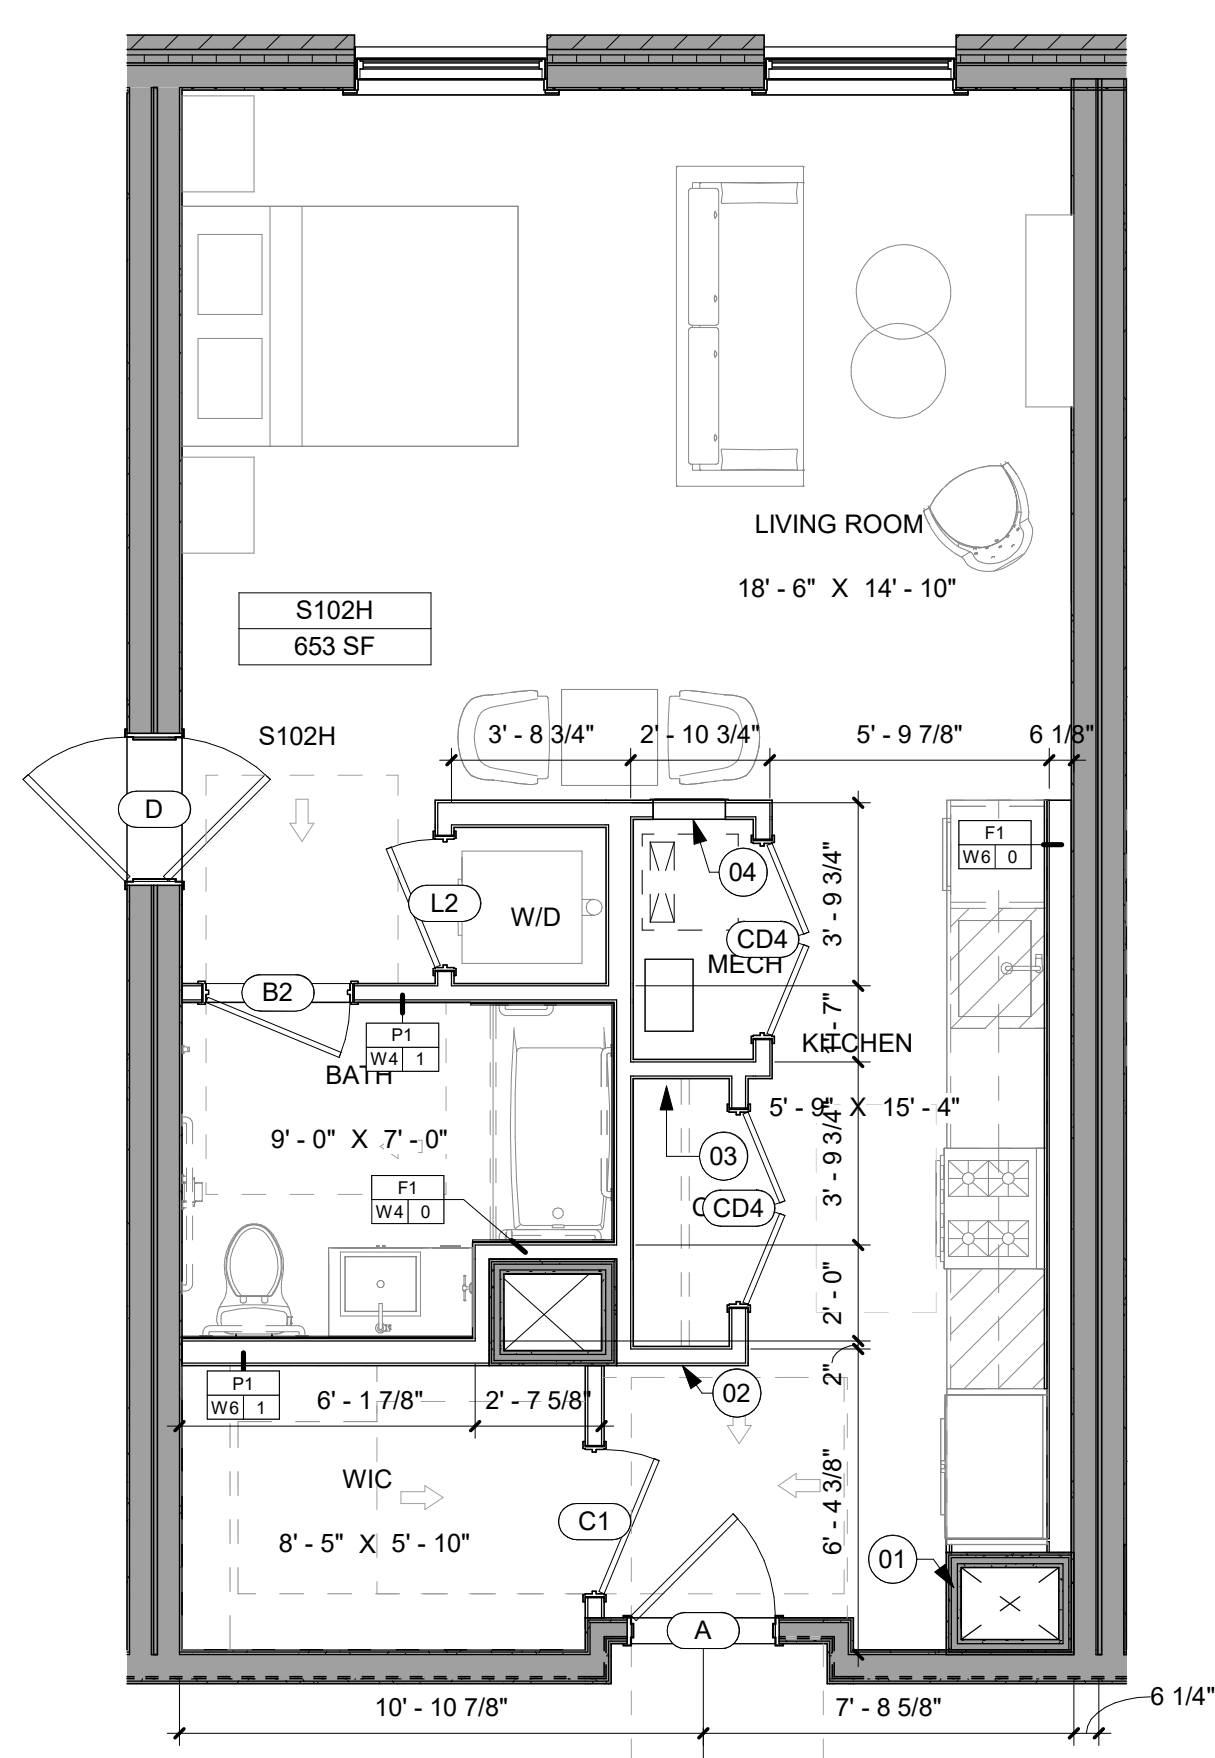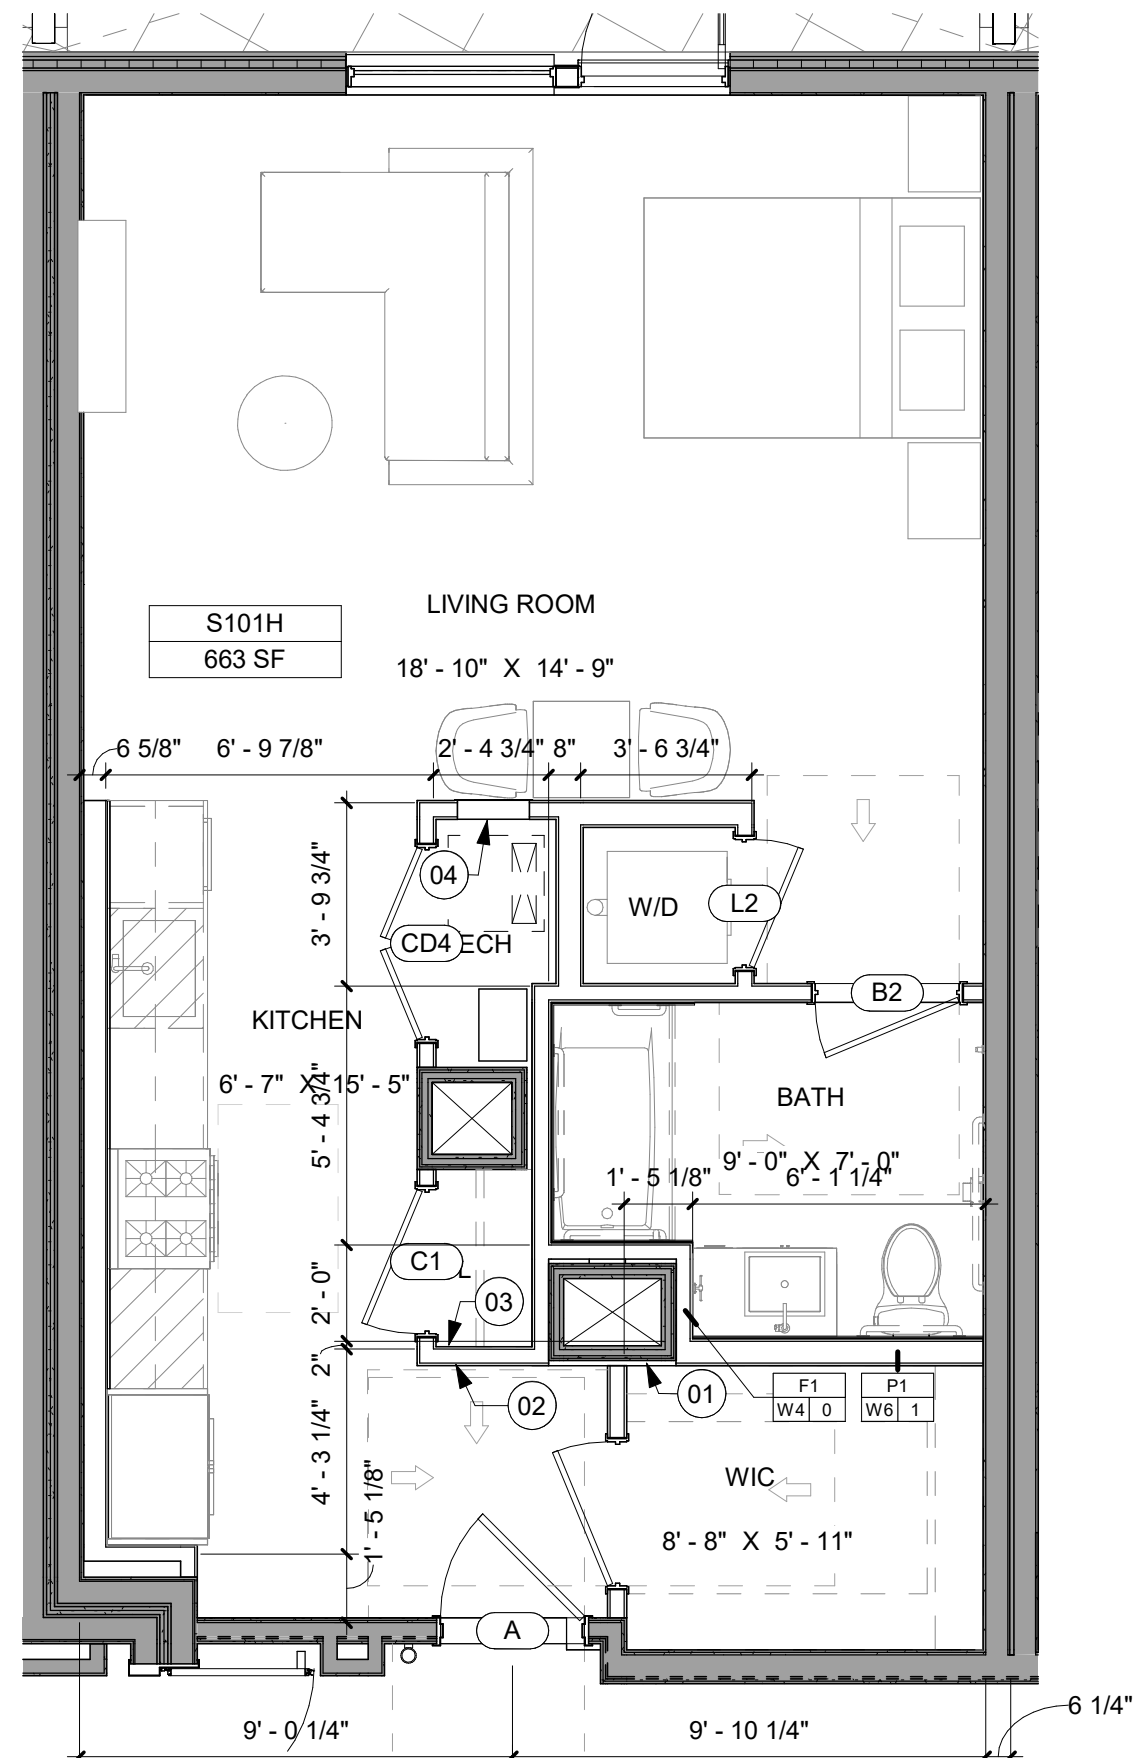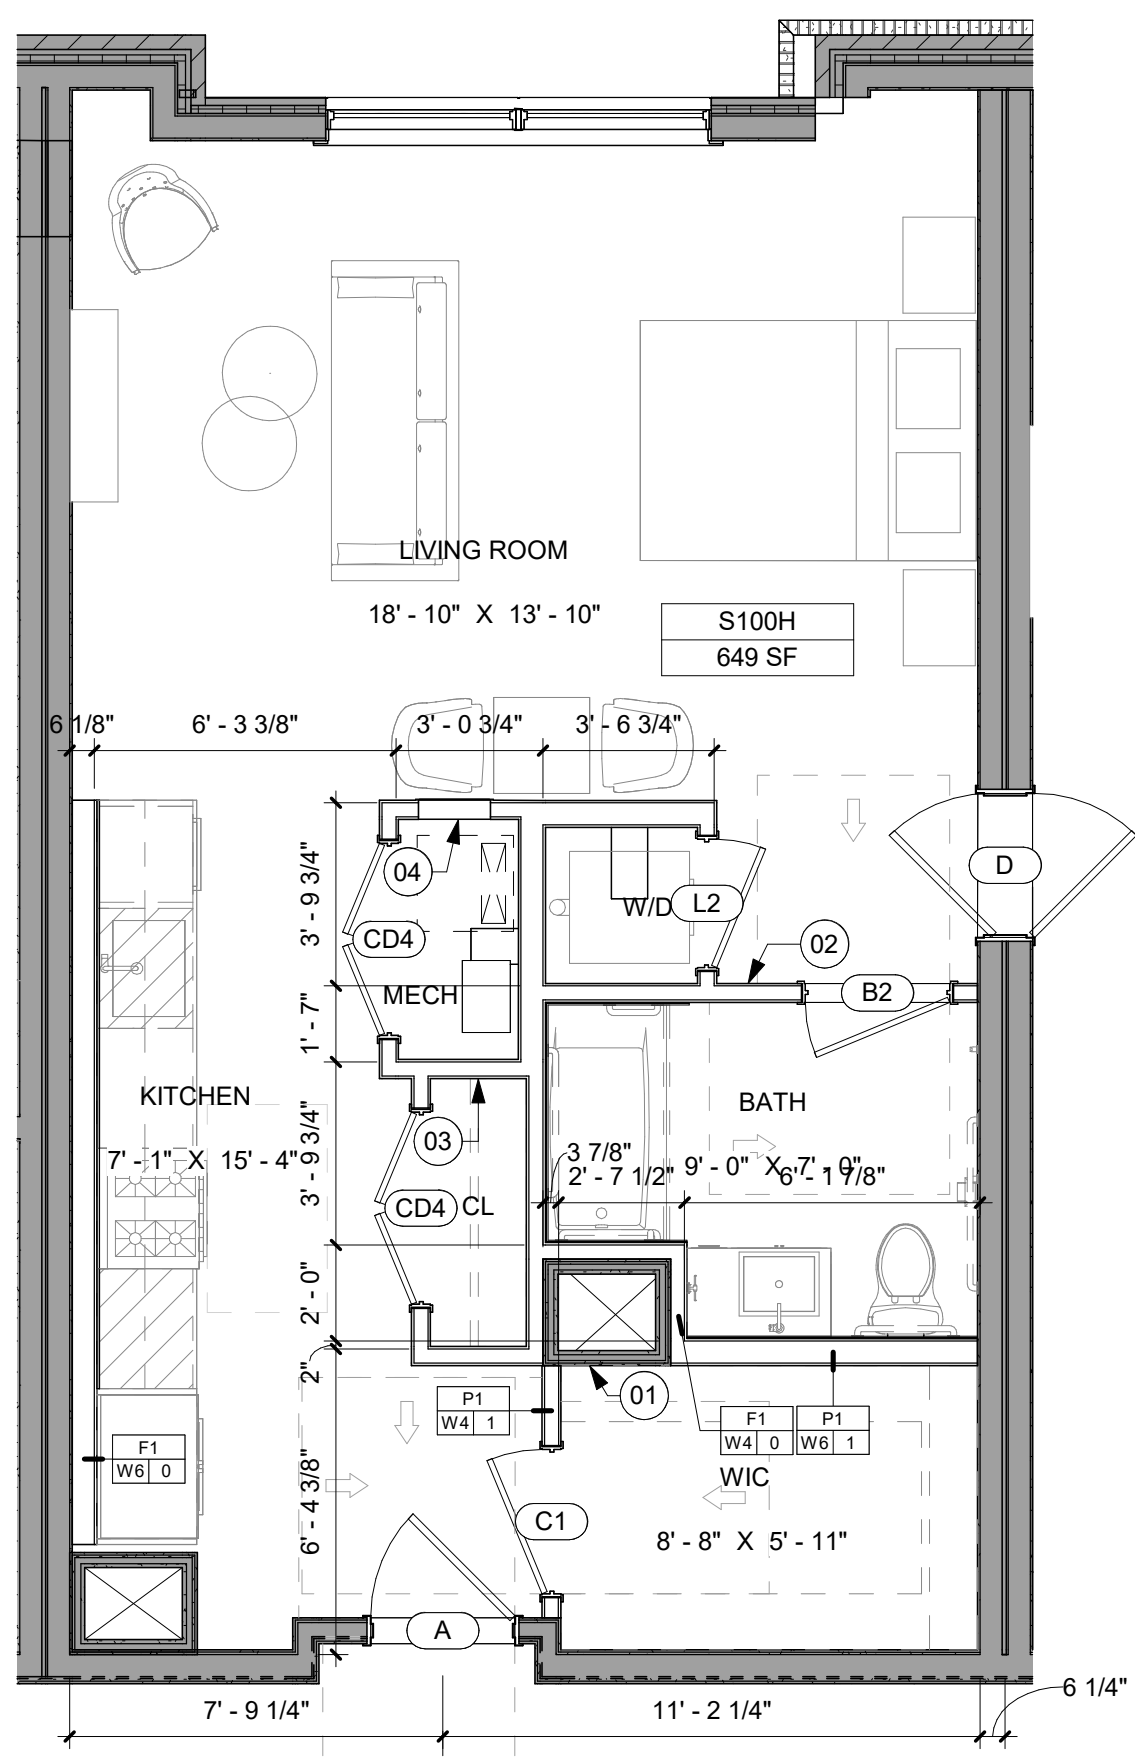

8 UNIT TYPE - S100H
SCALE: 1/4" = 1'-0"

UNIT TYPE	KITCHEN TYPE	BATHROOM TYPE	COUNT	AREA
S100H	K6	B1	8	649 SF ... 649 SF

7 UNIT TYPE - S101H
SCALE: 1/4" = 1'-0"





UNIT TYPE	KITCHEN TYPE	BATHROOM TYPE	COUNT	AREA
S101H	K6	B1	3	656 SF ... 663 SF

6 UNIT TYPE - S102H
SCALE: 1/4" = 1'-0"

UNIT TYPE	KITCHEN TYPE	BATHROOM TYPE	COUNT	AREA
S102H	B1	K6	4	<varies>

5 UNIT TYPE - S103H
SCALE: 1/4" = 1'-0"

UNIT TYPE	KITCHEN TYPE	BATHROOM TYPE	COUNT	AREA
S103H	K6	K1	4	661 SF ... 665 SF

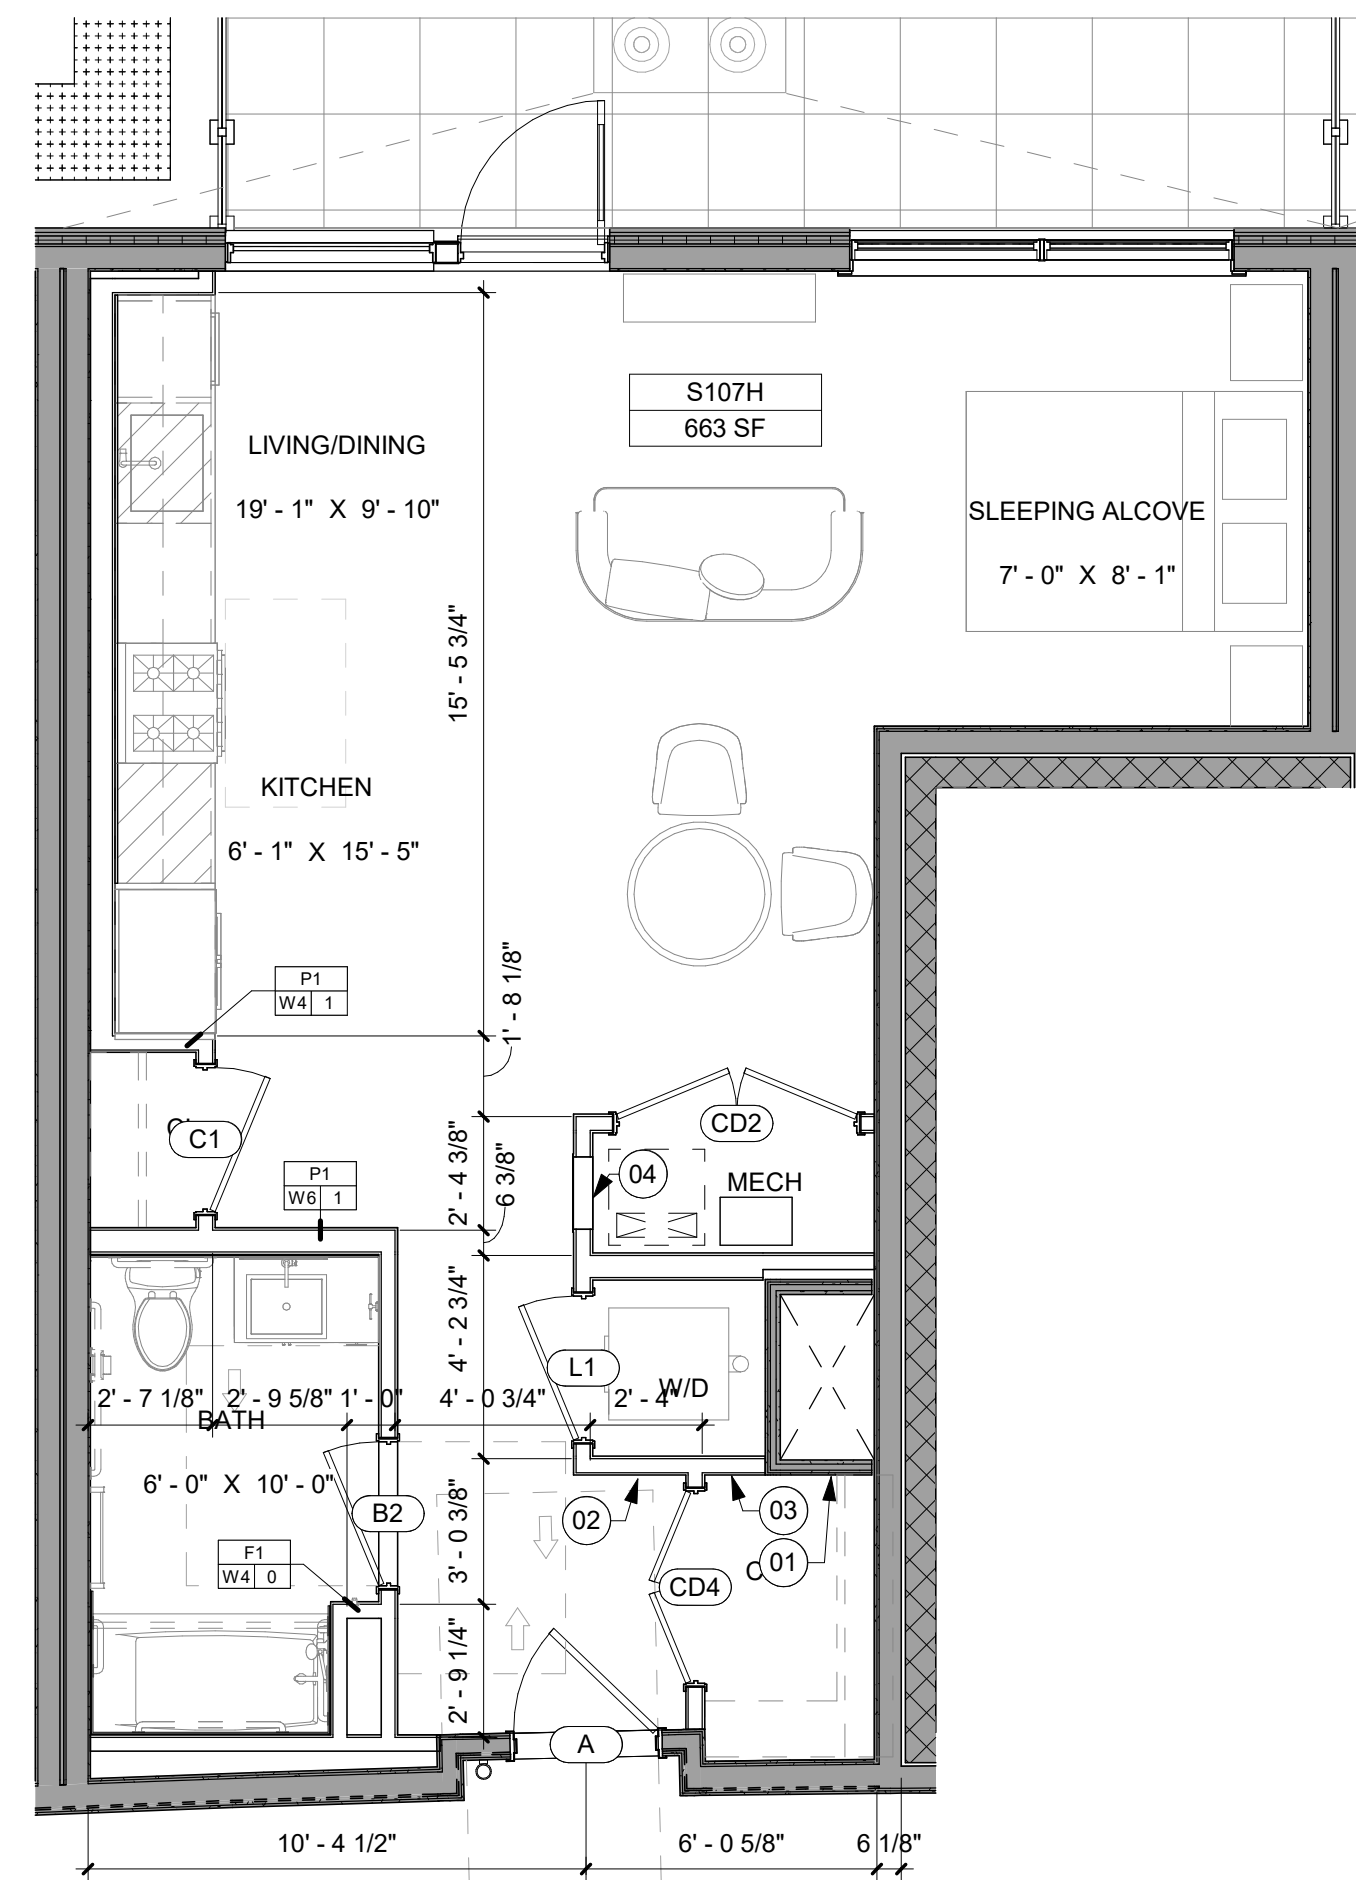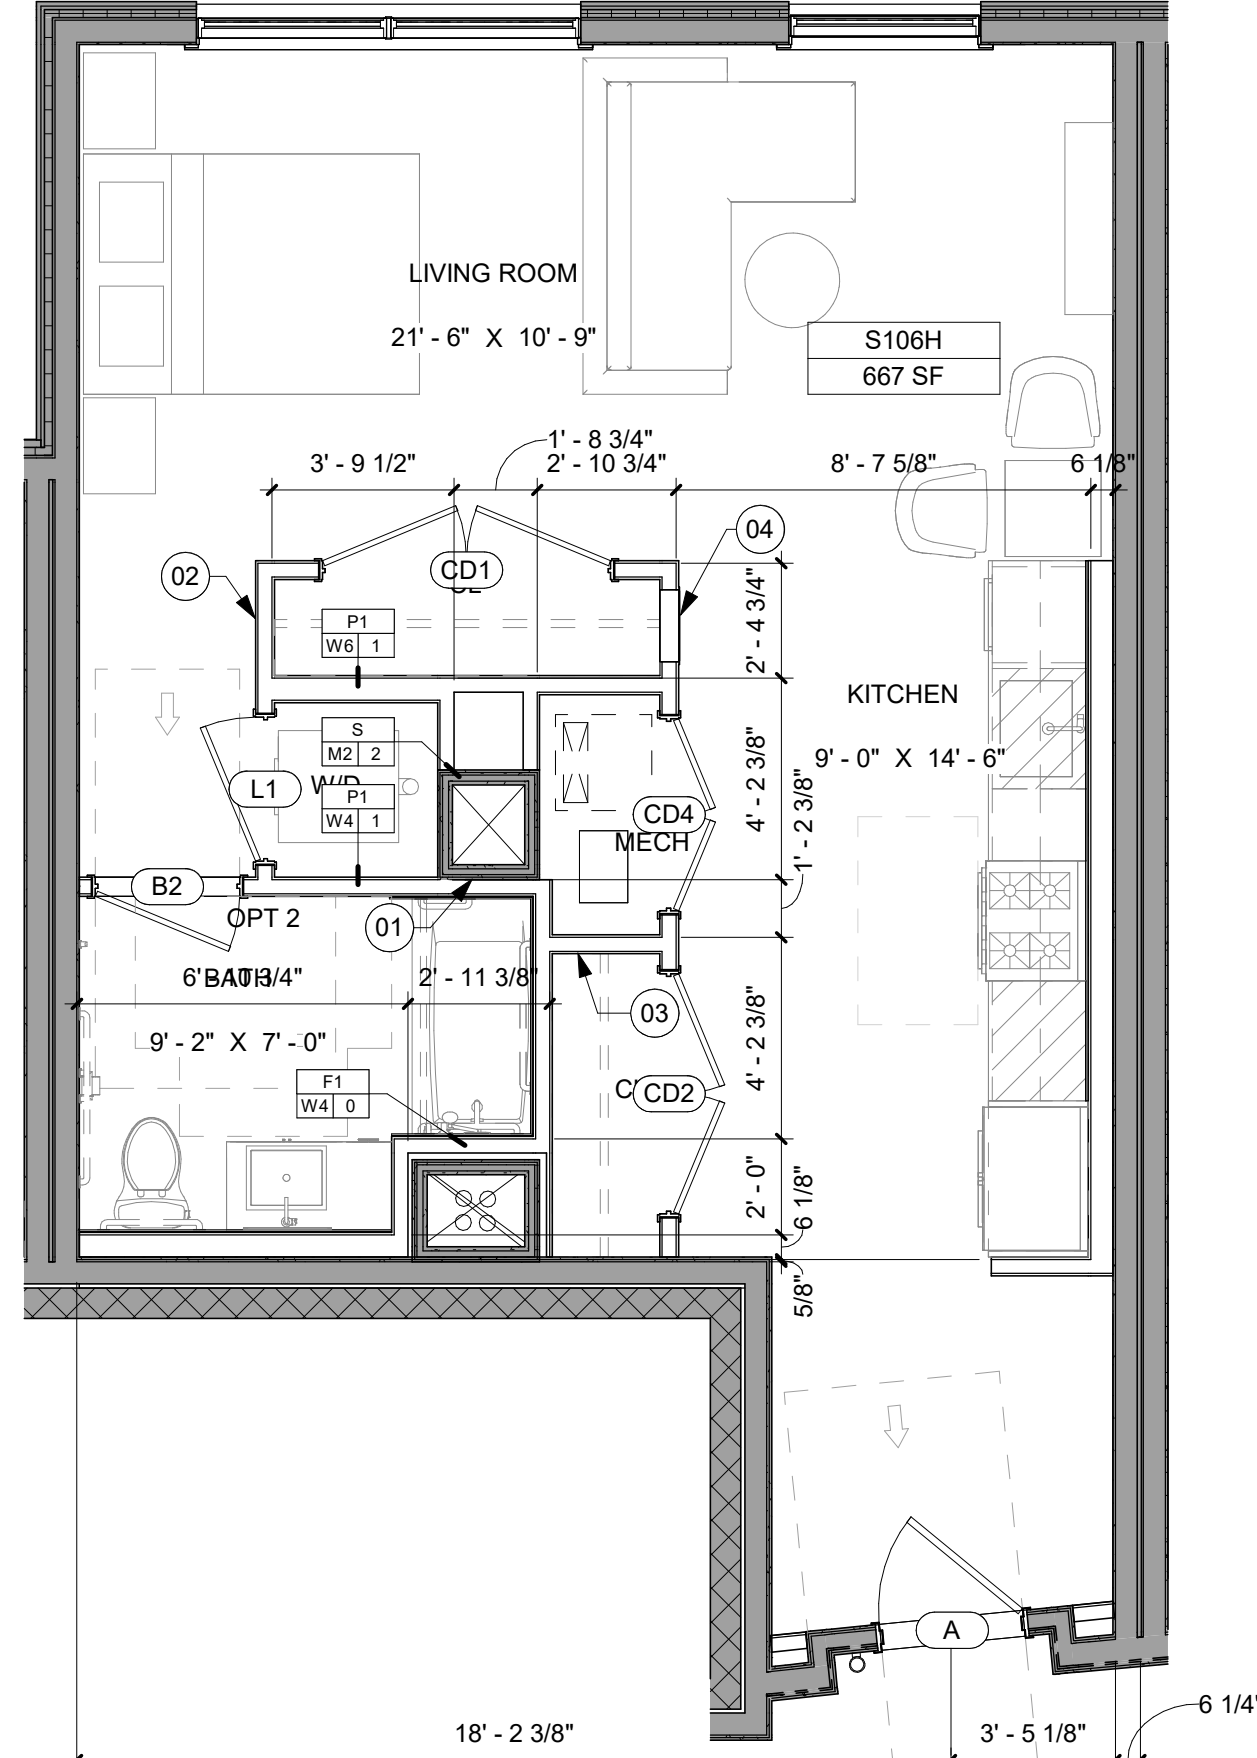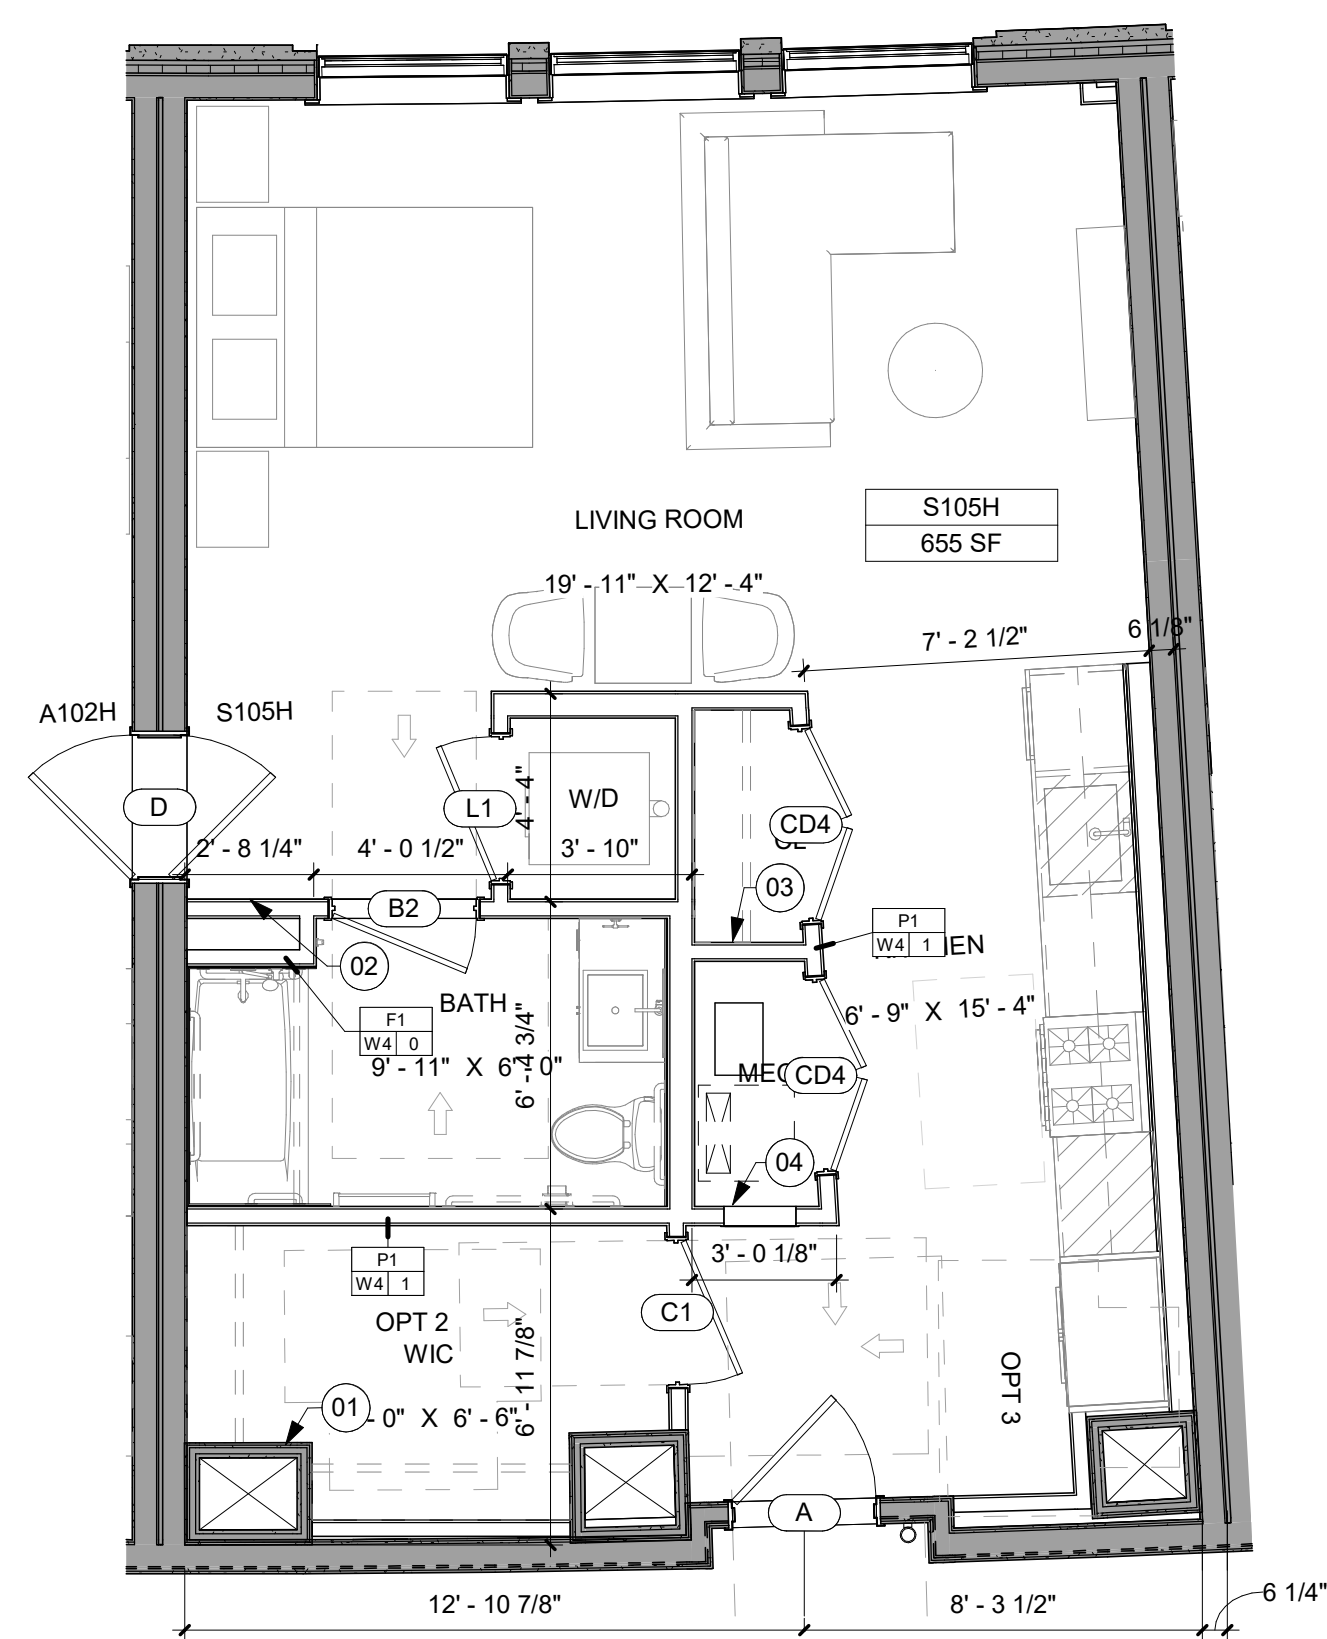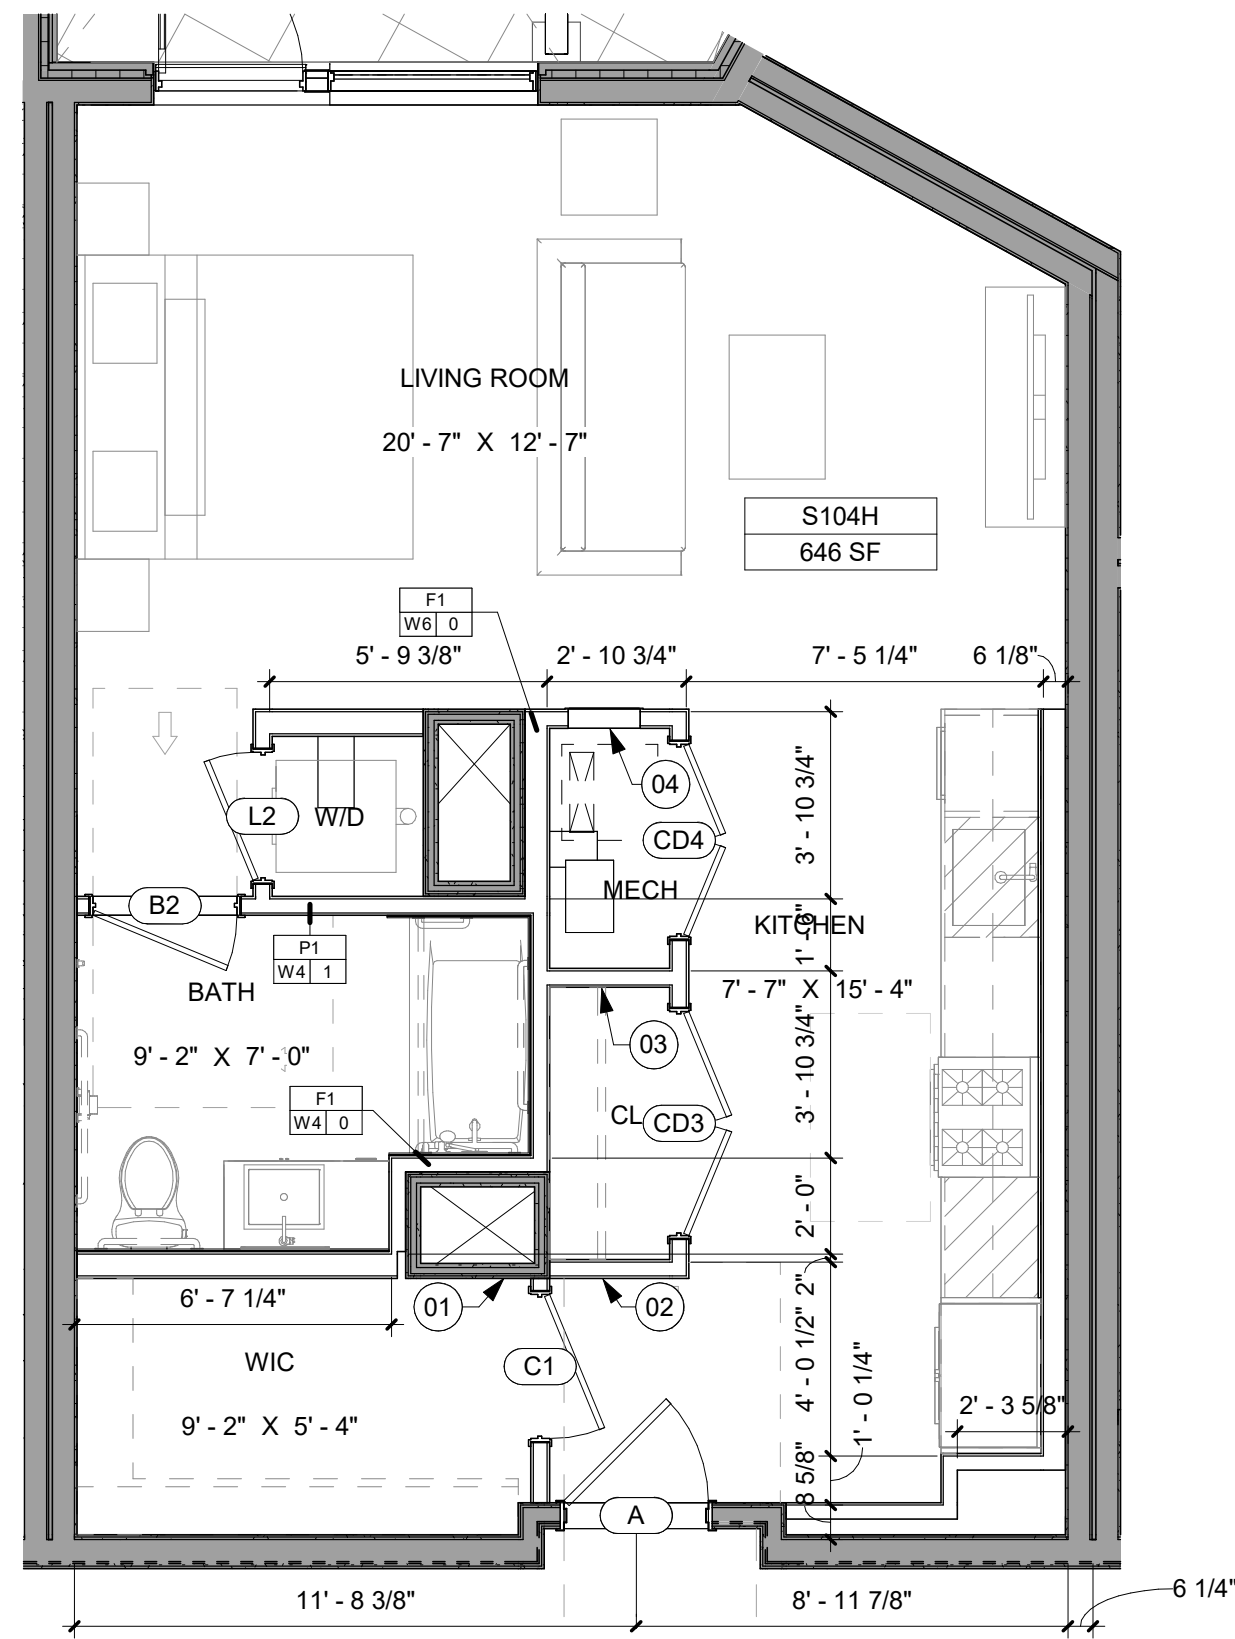

4 UNIT TYPE - S104H
SCALE: 1/4" = 1'-0"

UNIT TYPE	KITCHEN TYPE	BATHROOM TYPE	COUNT	AREA
S104H	K4	B9.1	4	646 SF ... 654 SF

3 UNIT TYPE - S105H
SCALE: 1/4" = 1'-0"

UNIT TYPE	KITCHEN TYPE	BATHROOM TYPE	COUNT	AREA
S105H	K6	B2	3	655 SF ... 656 SF

2 UNIT TYPE - S106H
SCALE: 1/4" = 1'-0"

UNIT TYPE	KITCHEN TYPE	BATHROOM TYPE	COUNT	AREA
S106H	K7	B3	3	667 SF

1 UNIT TYPE - S107H
SCALE: 1/4" = 1'-0"

UNIT TYPE	KITCHEN TYPE	BATHROOM TYPE	COUNT	AREA
S107H	K6	B1	3	663 SF