
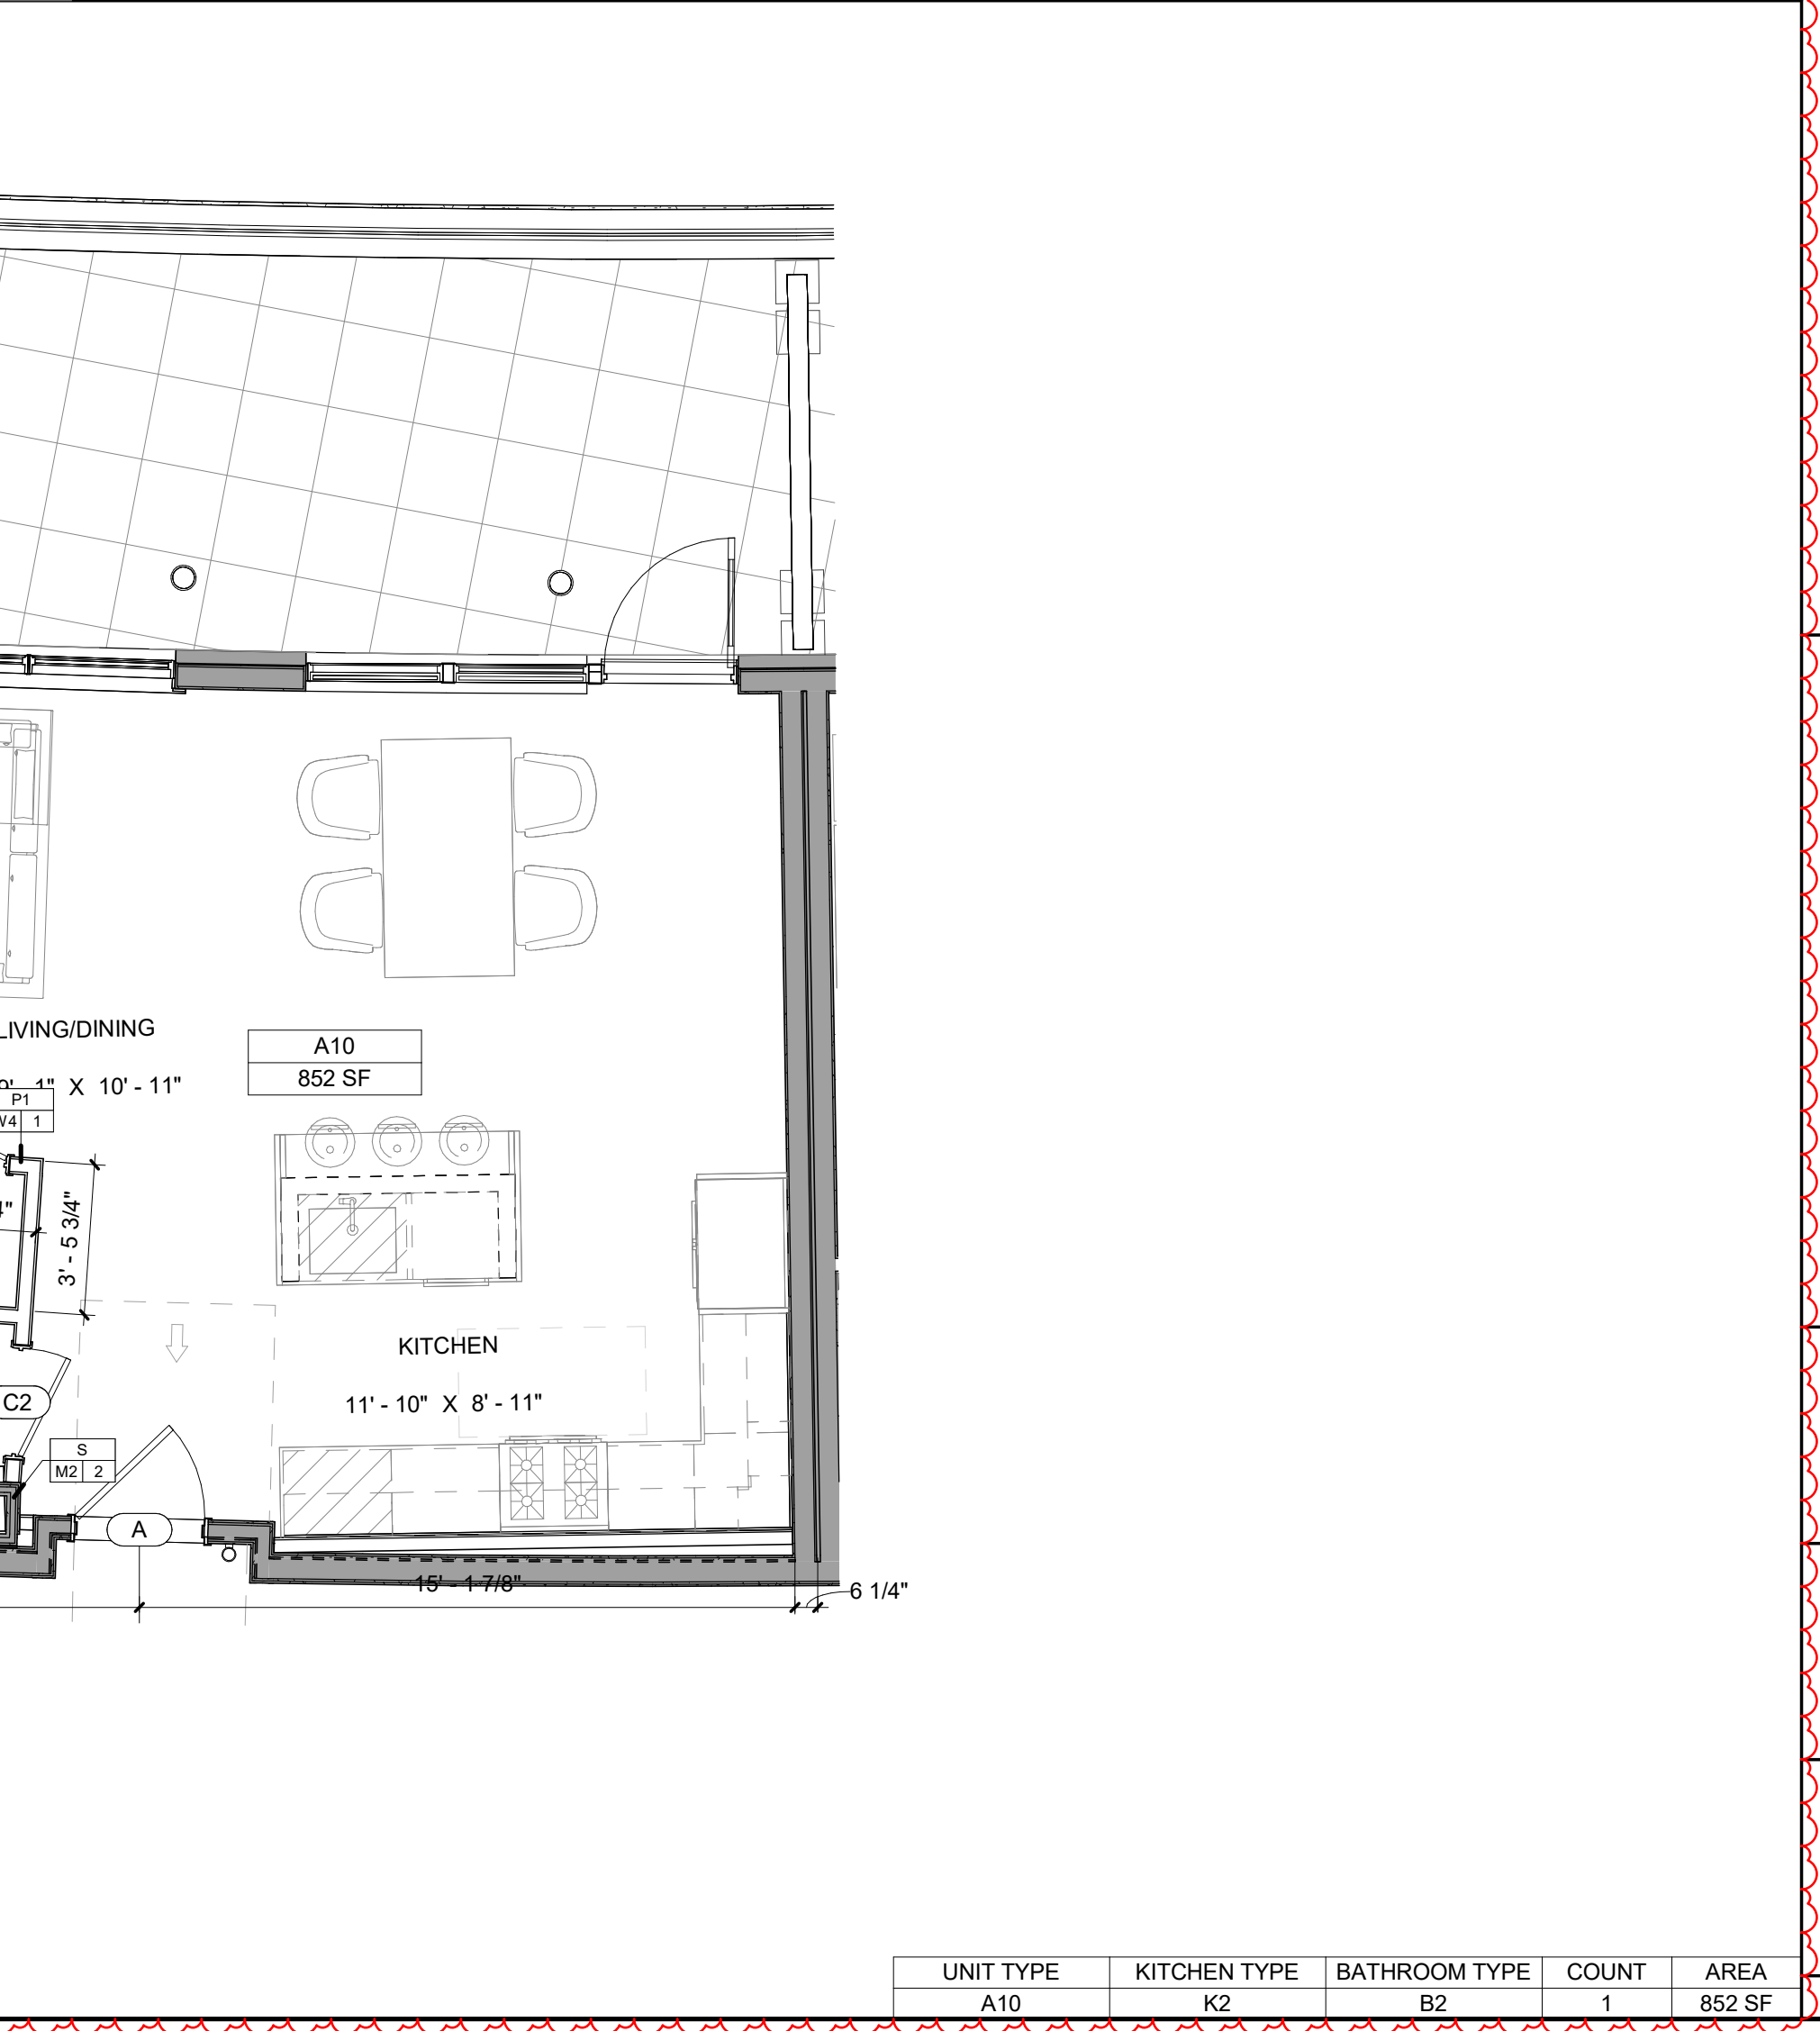
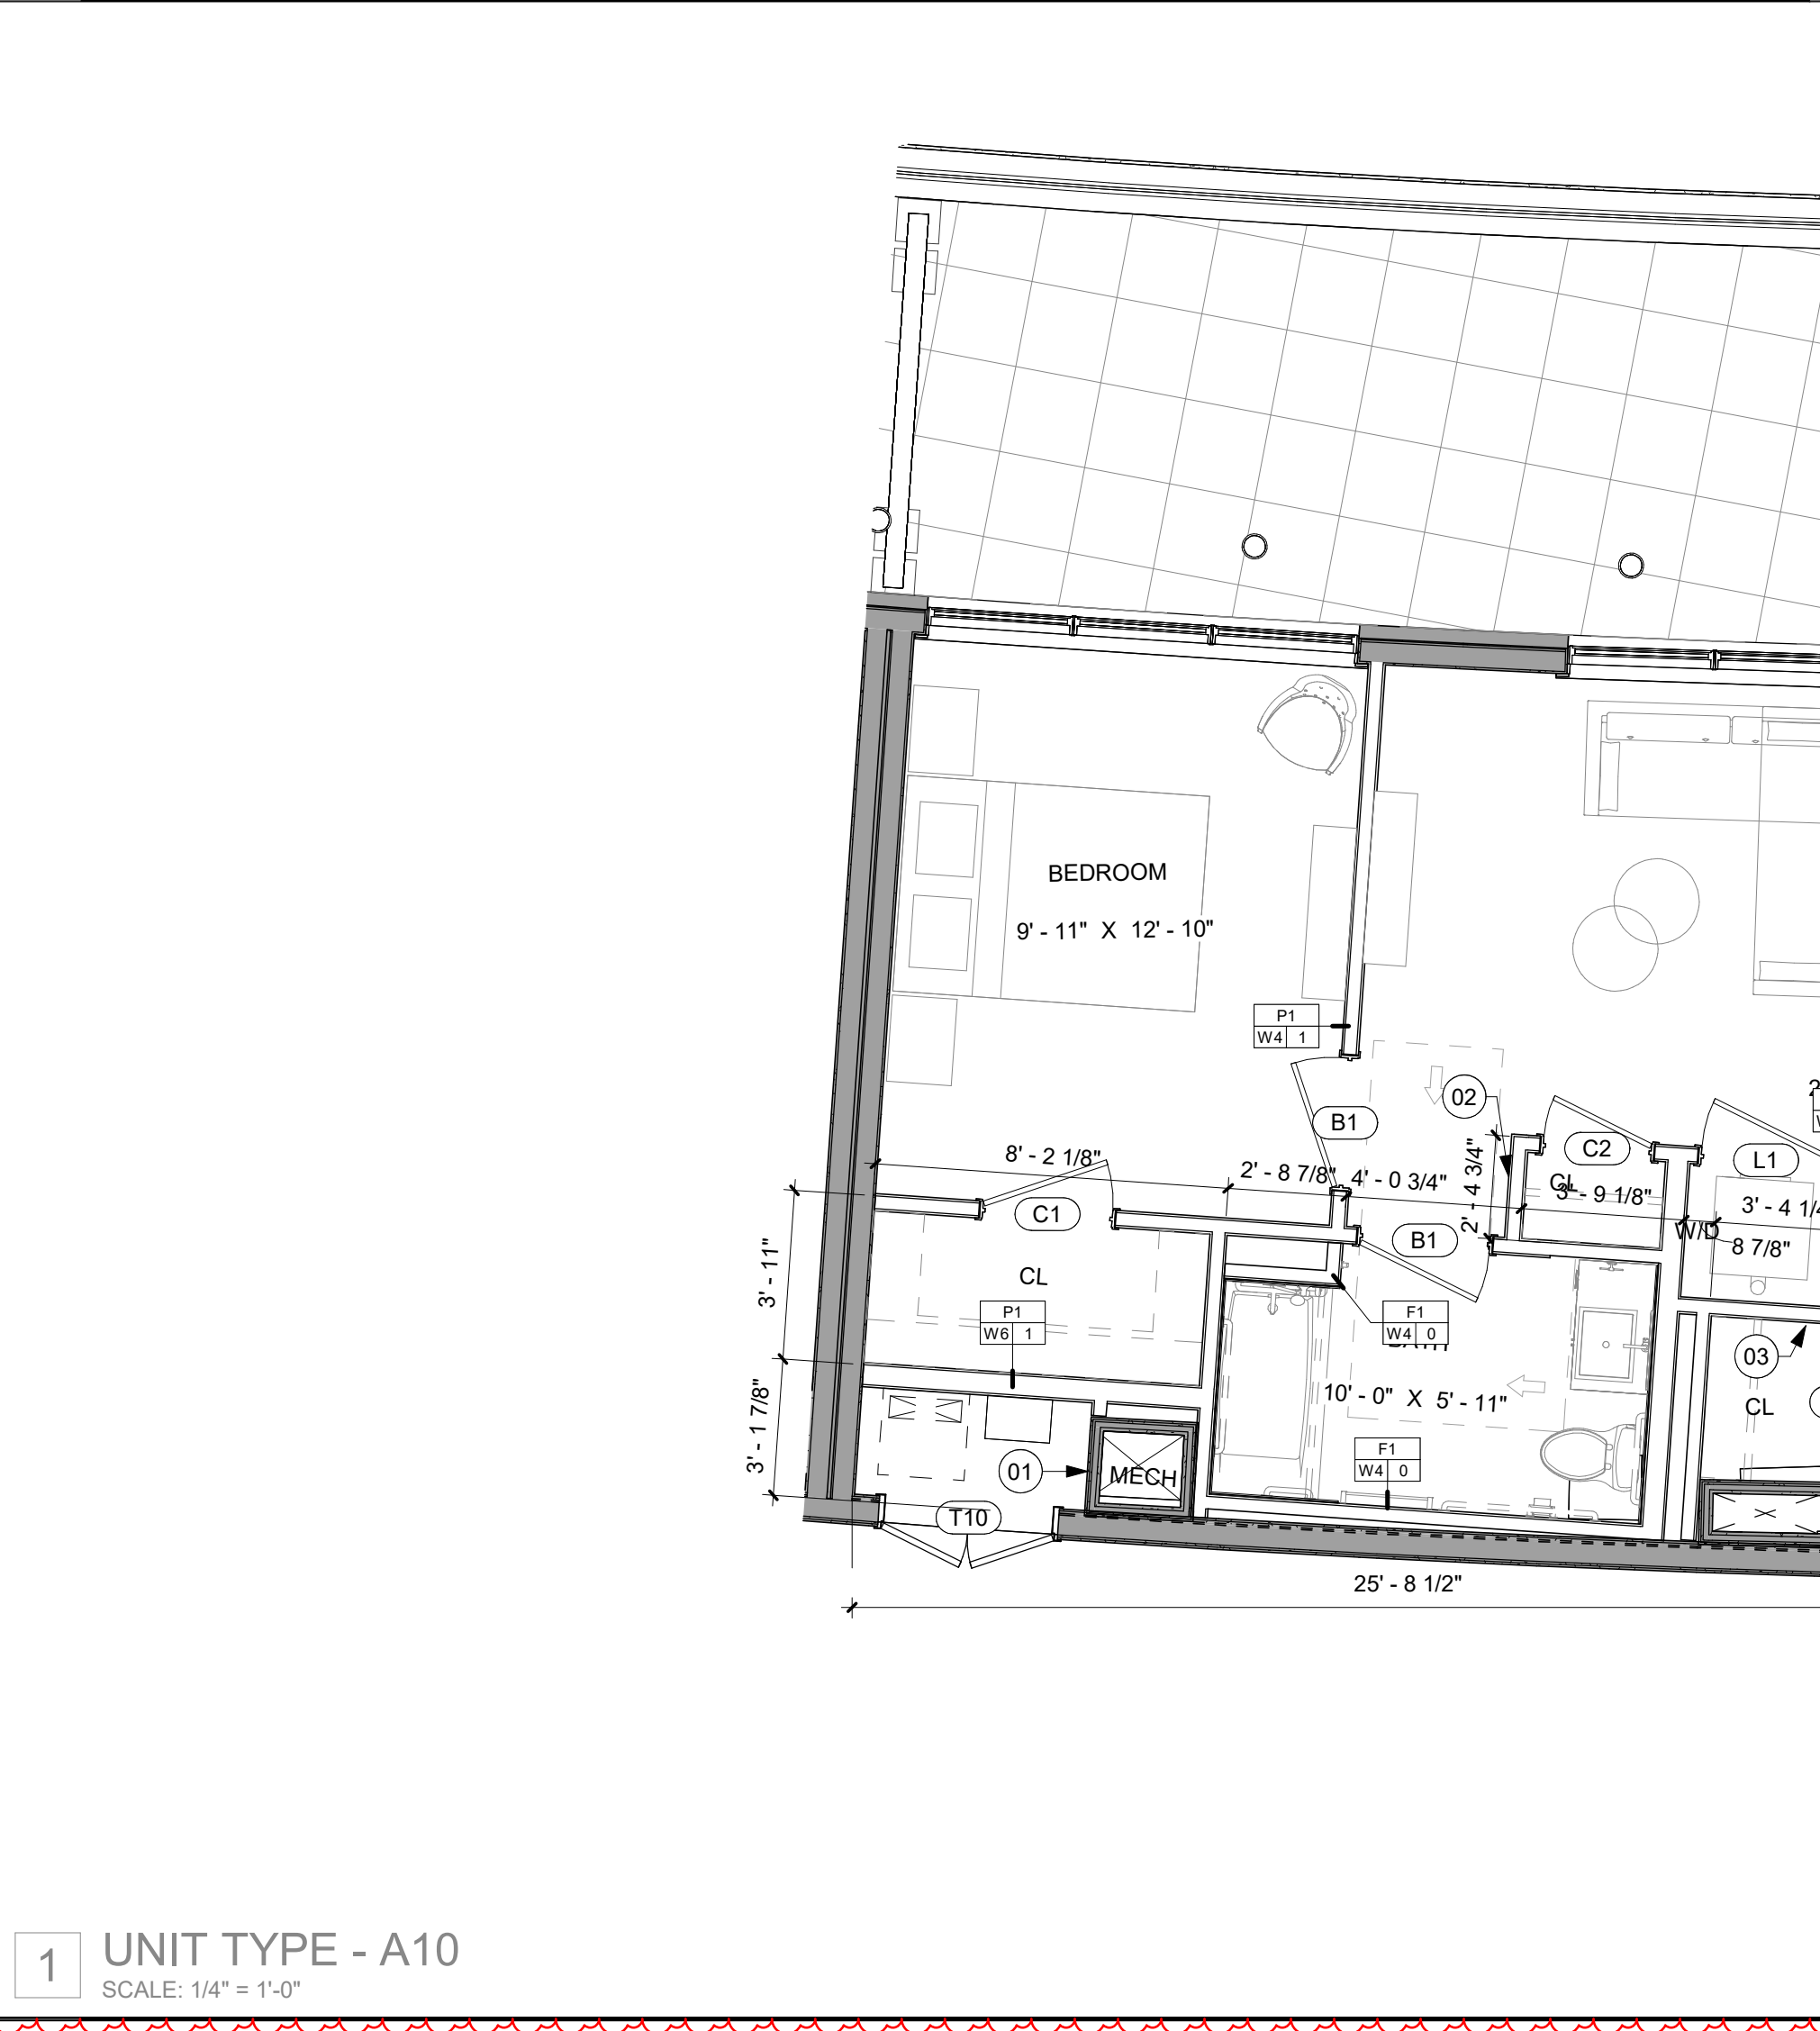
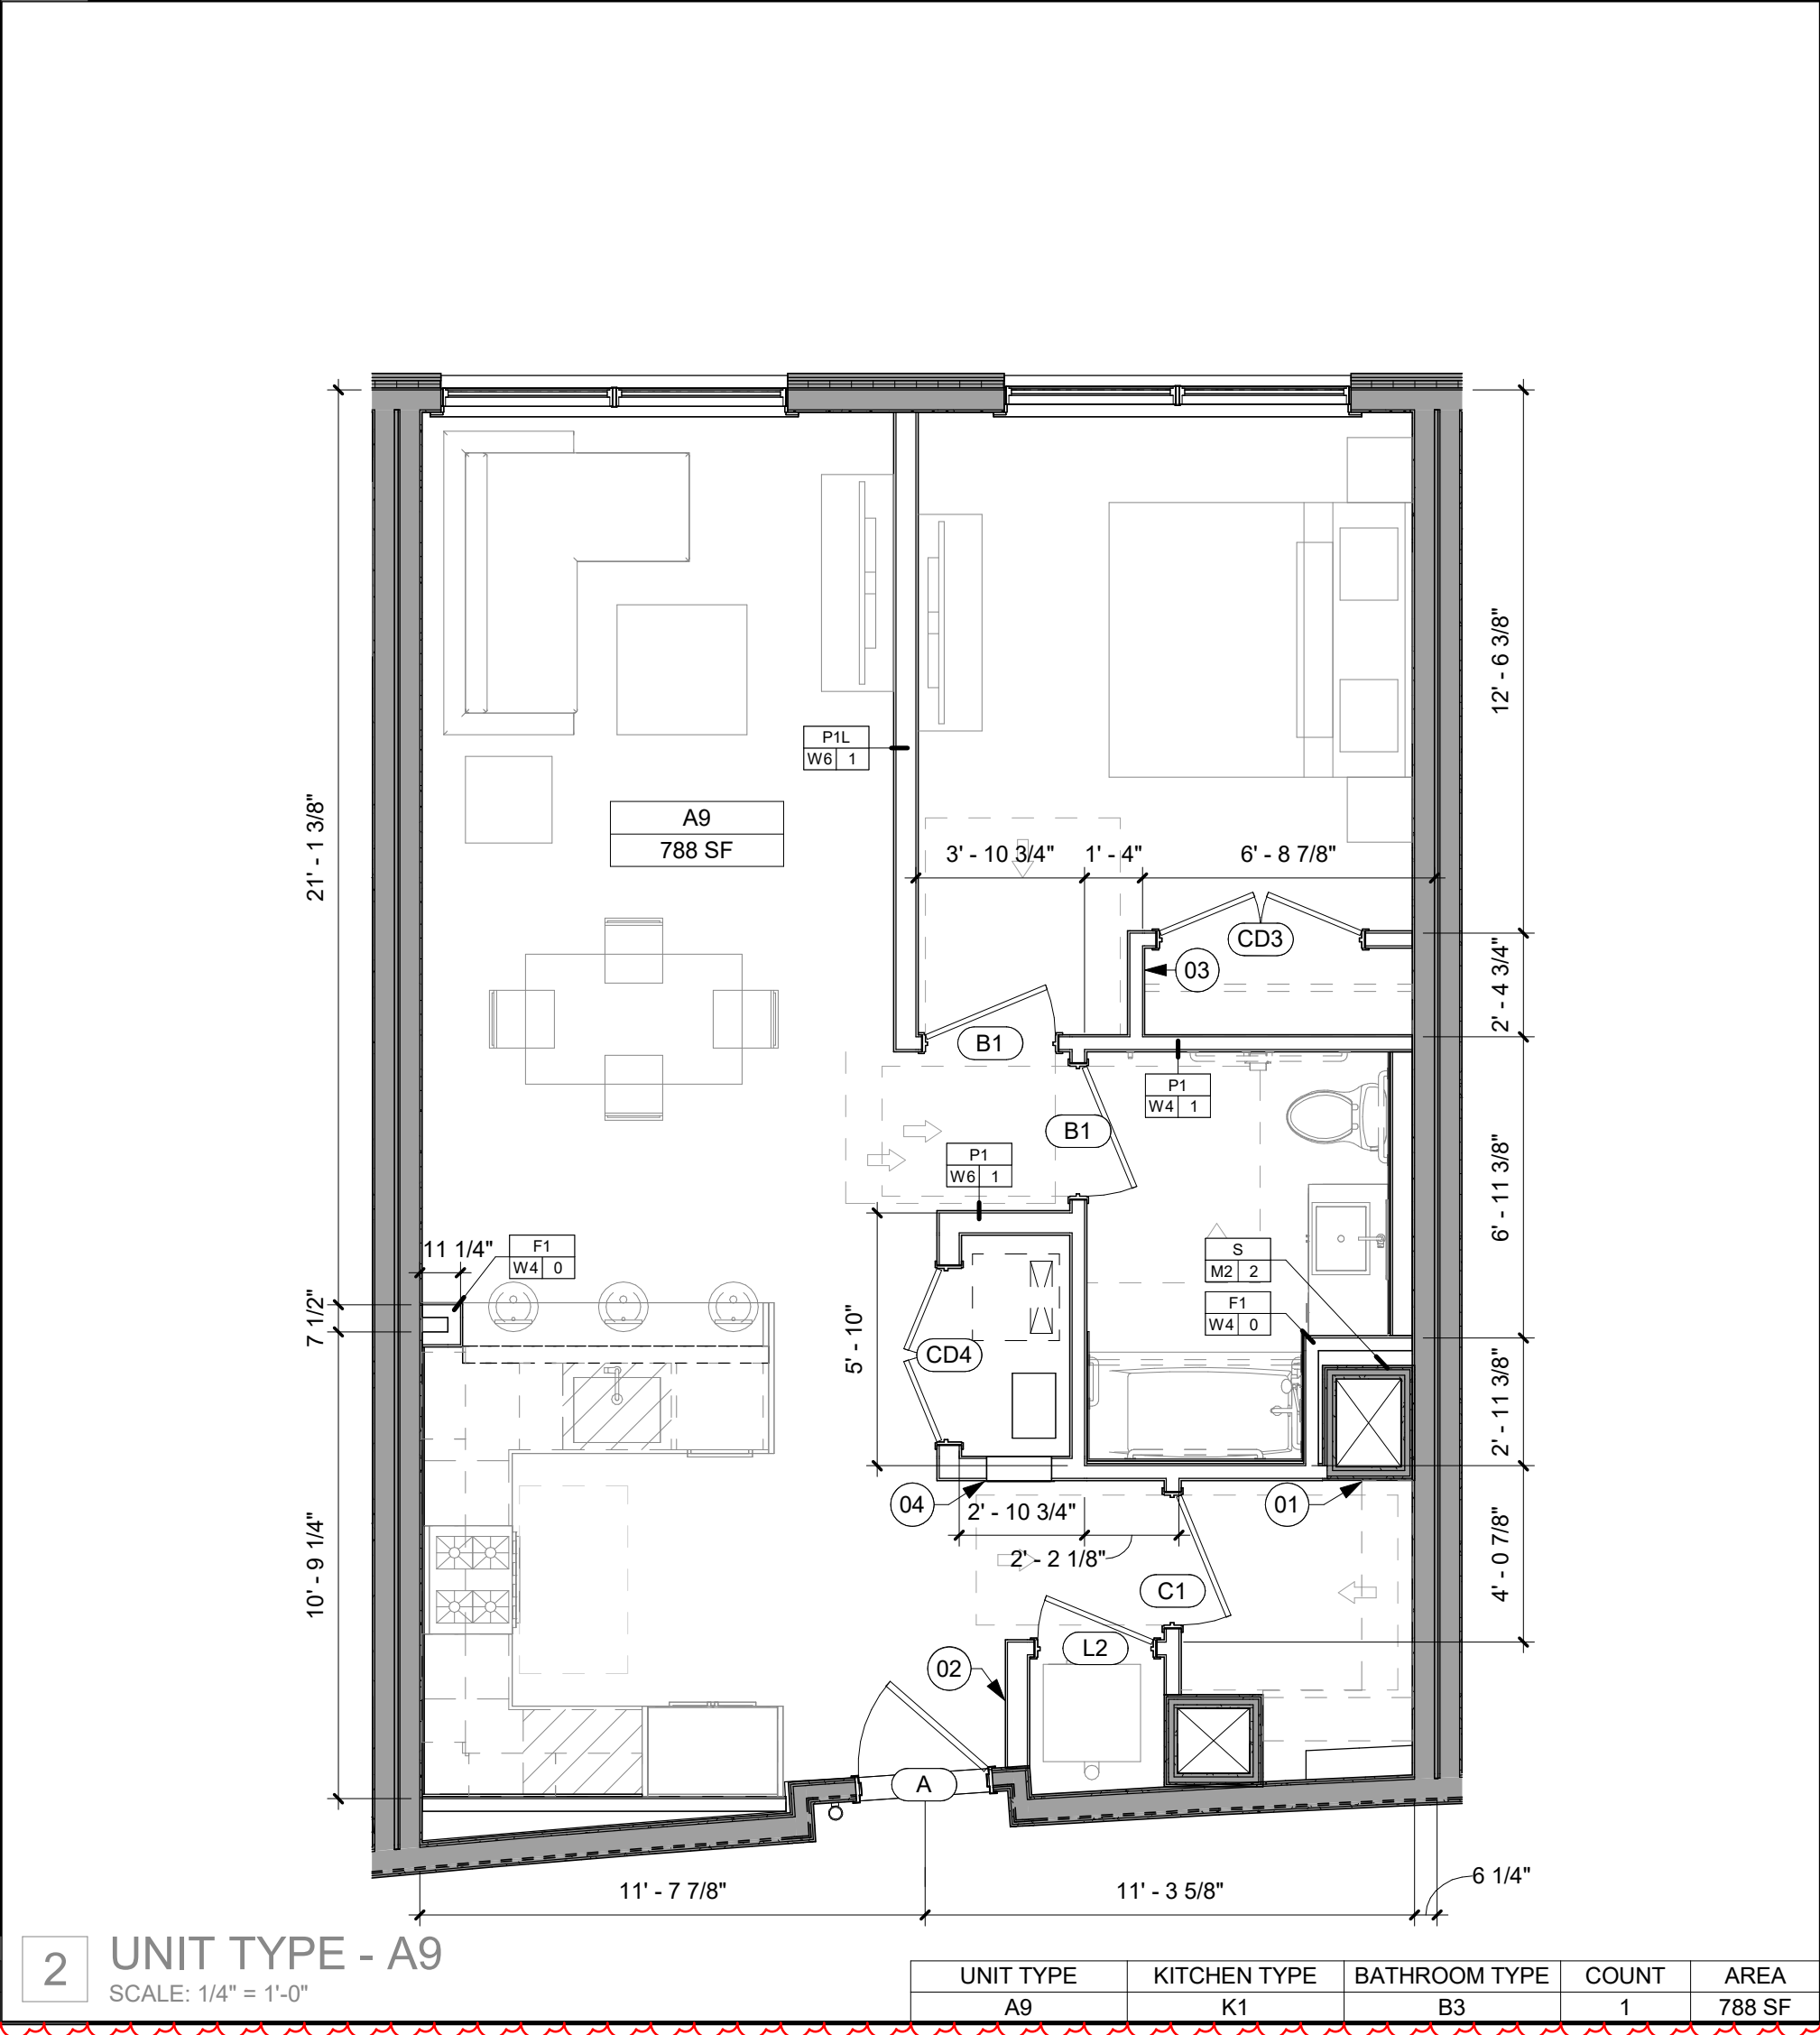
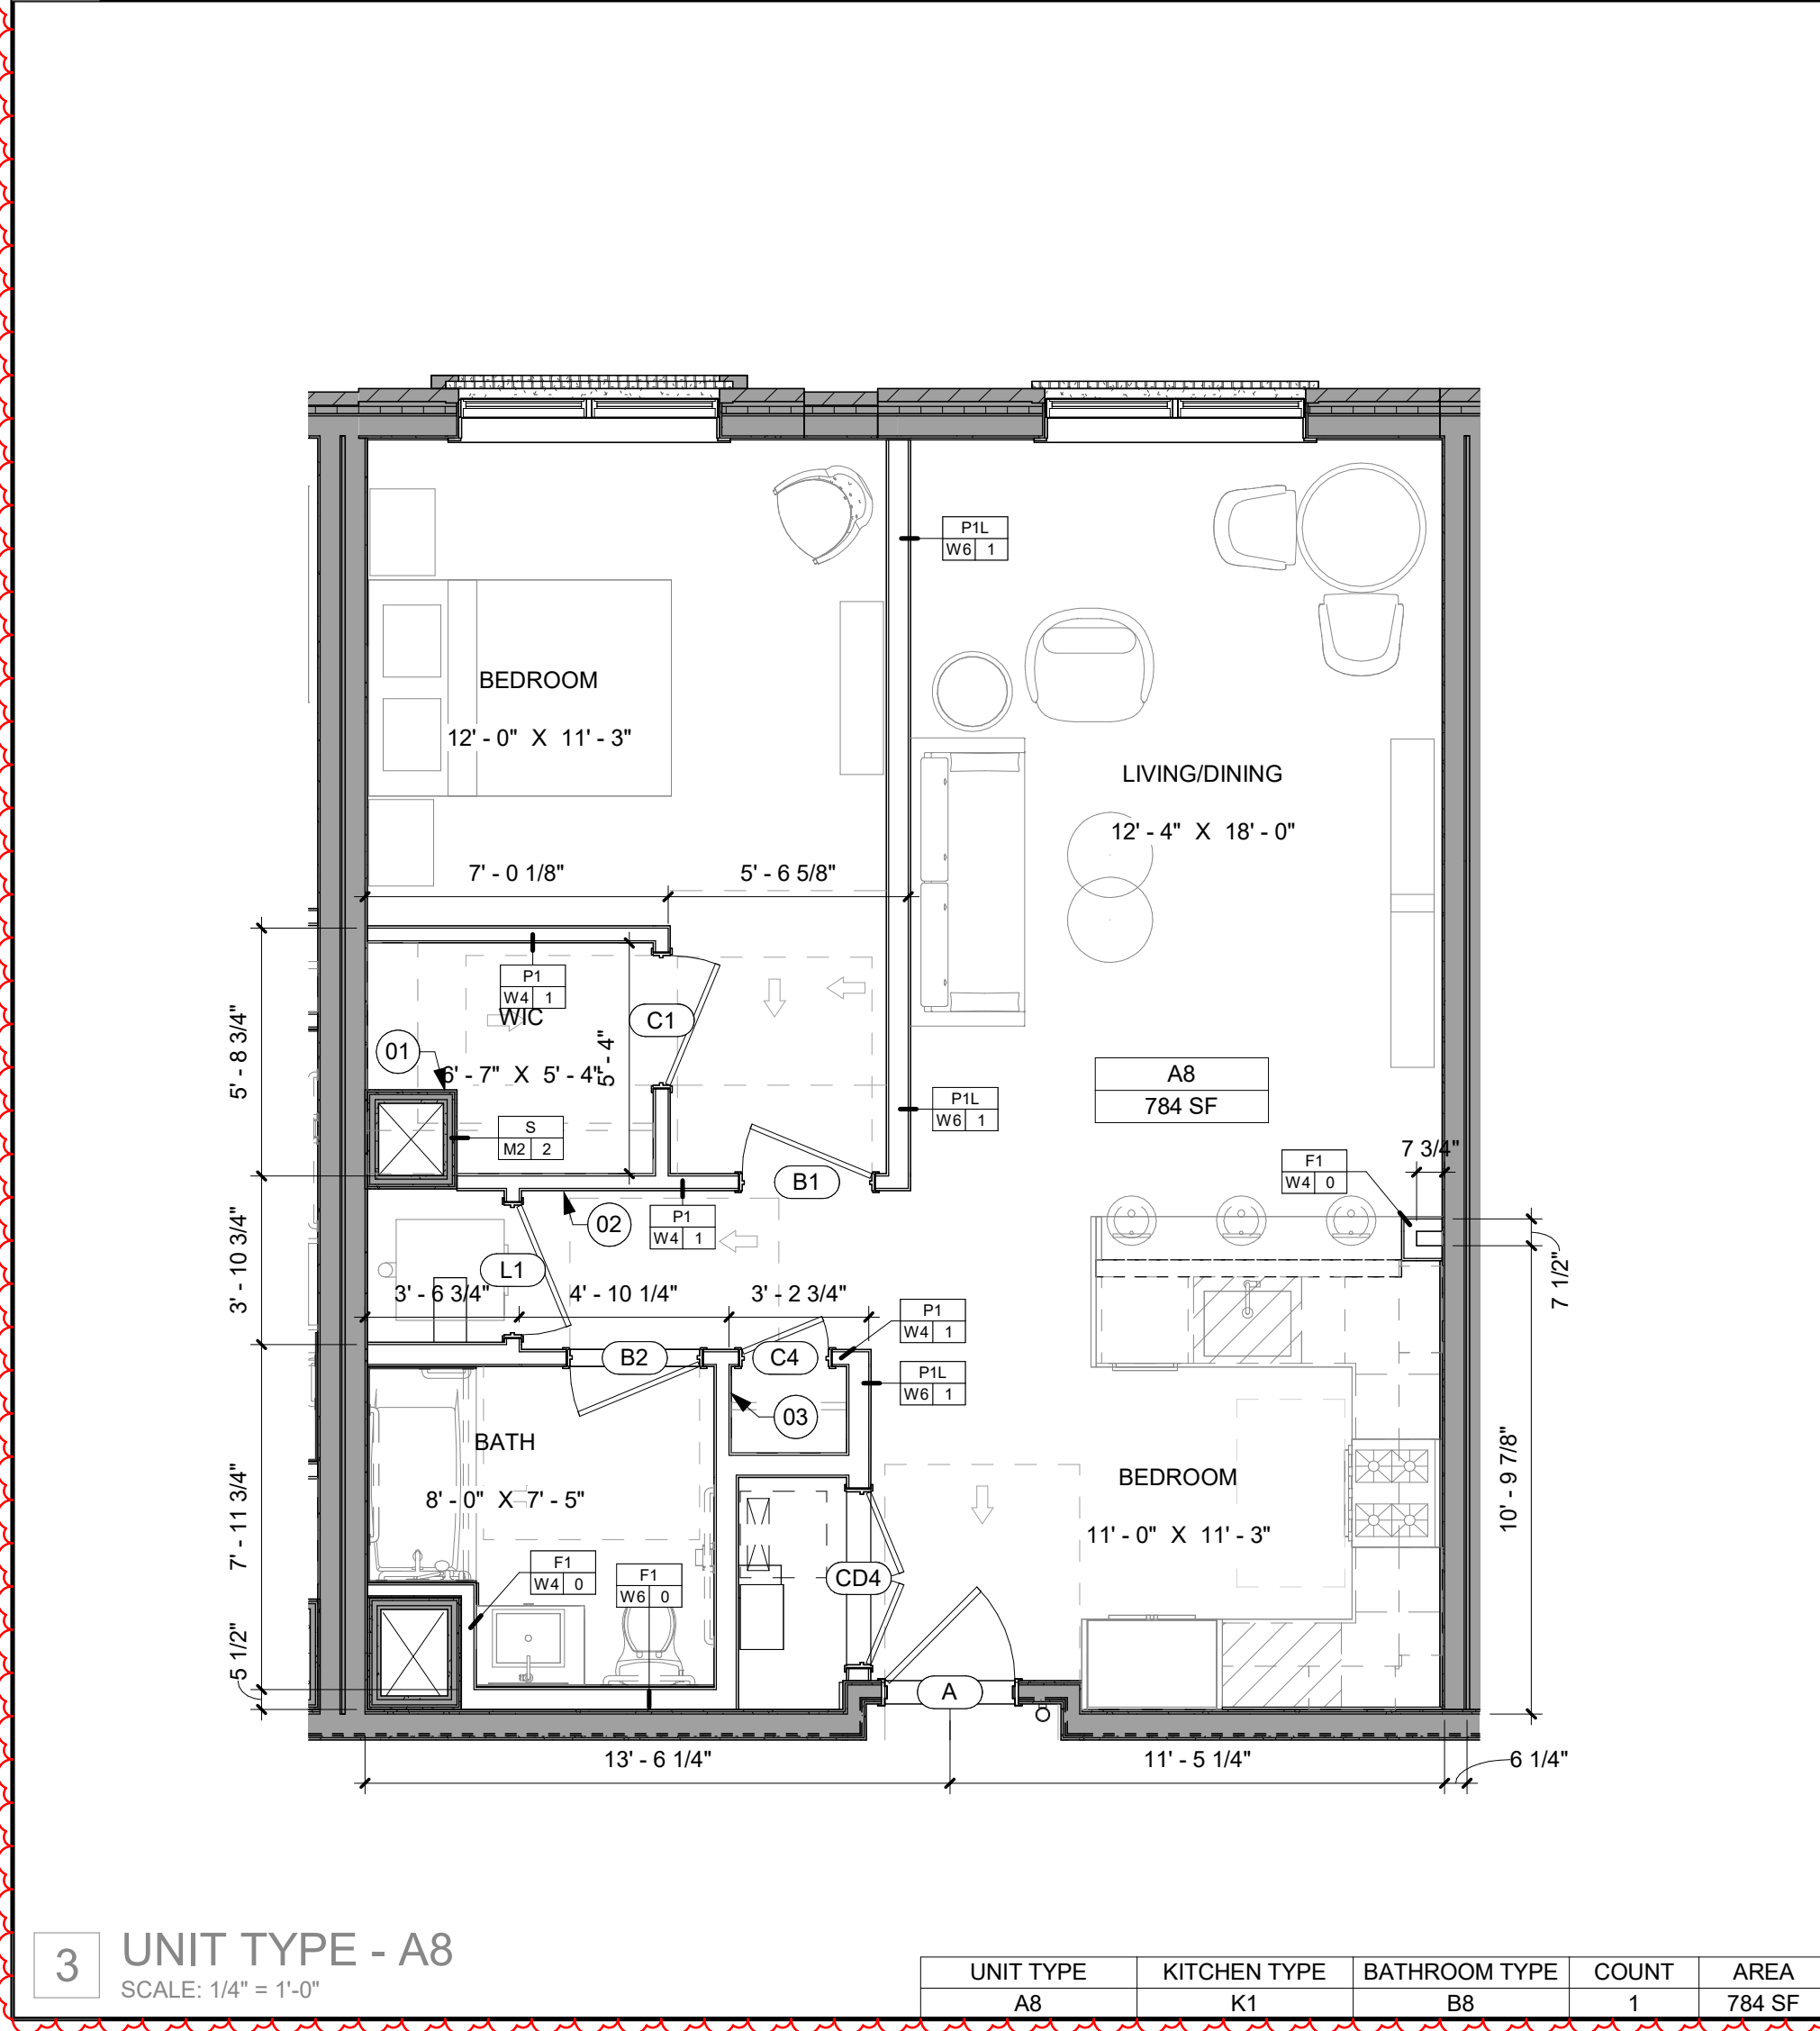
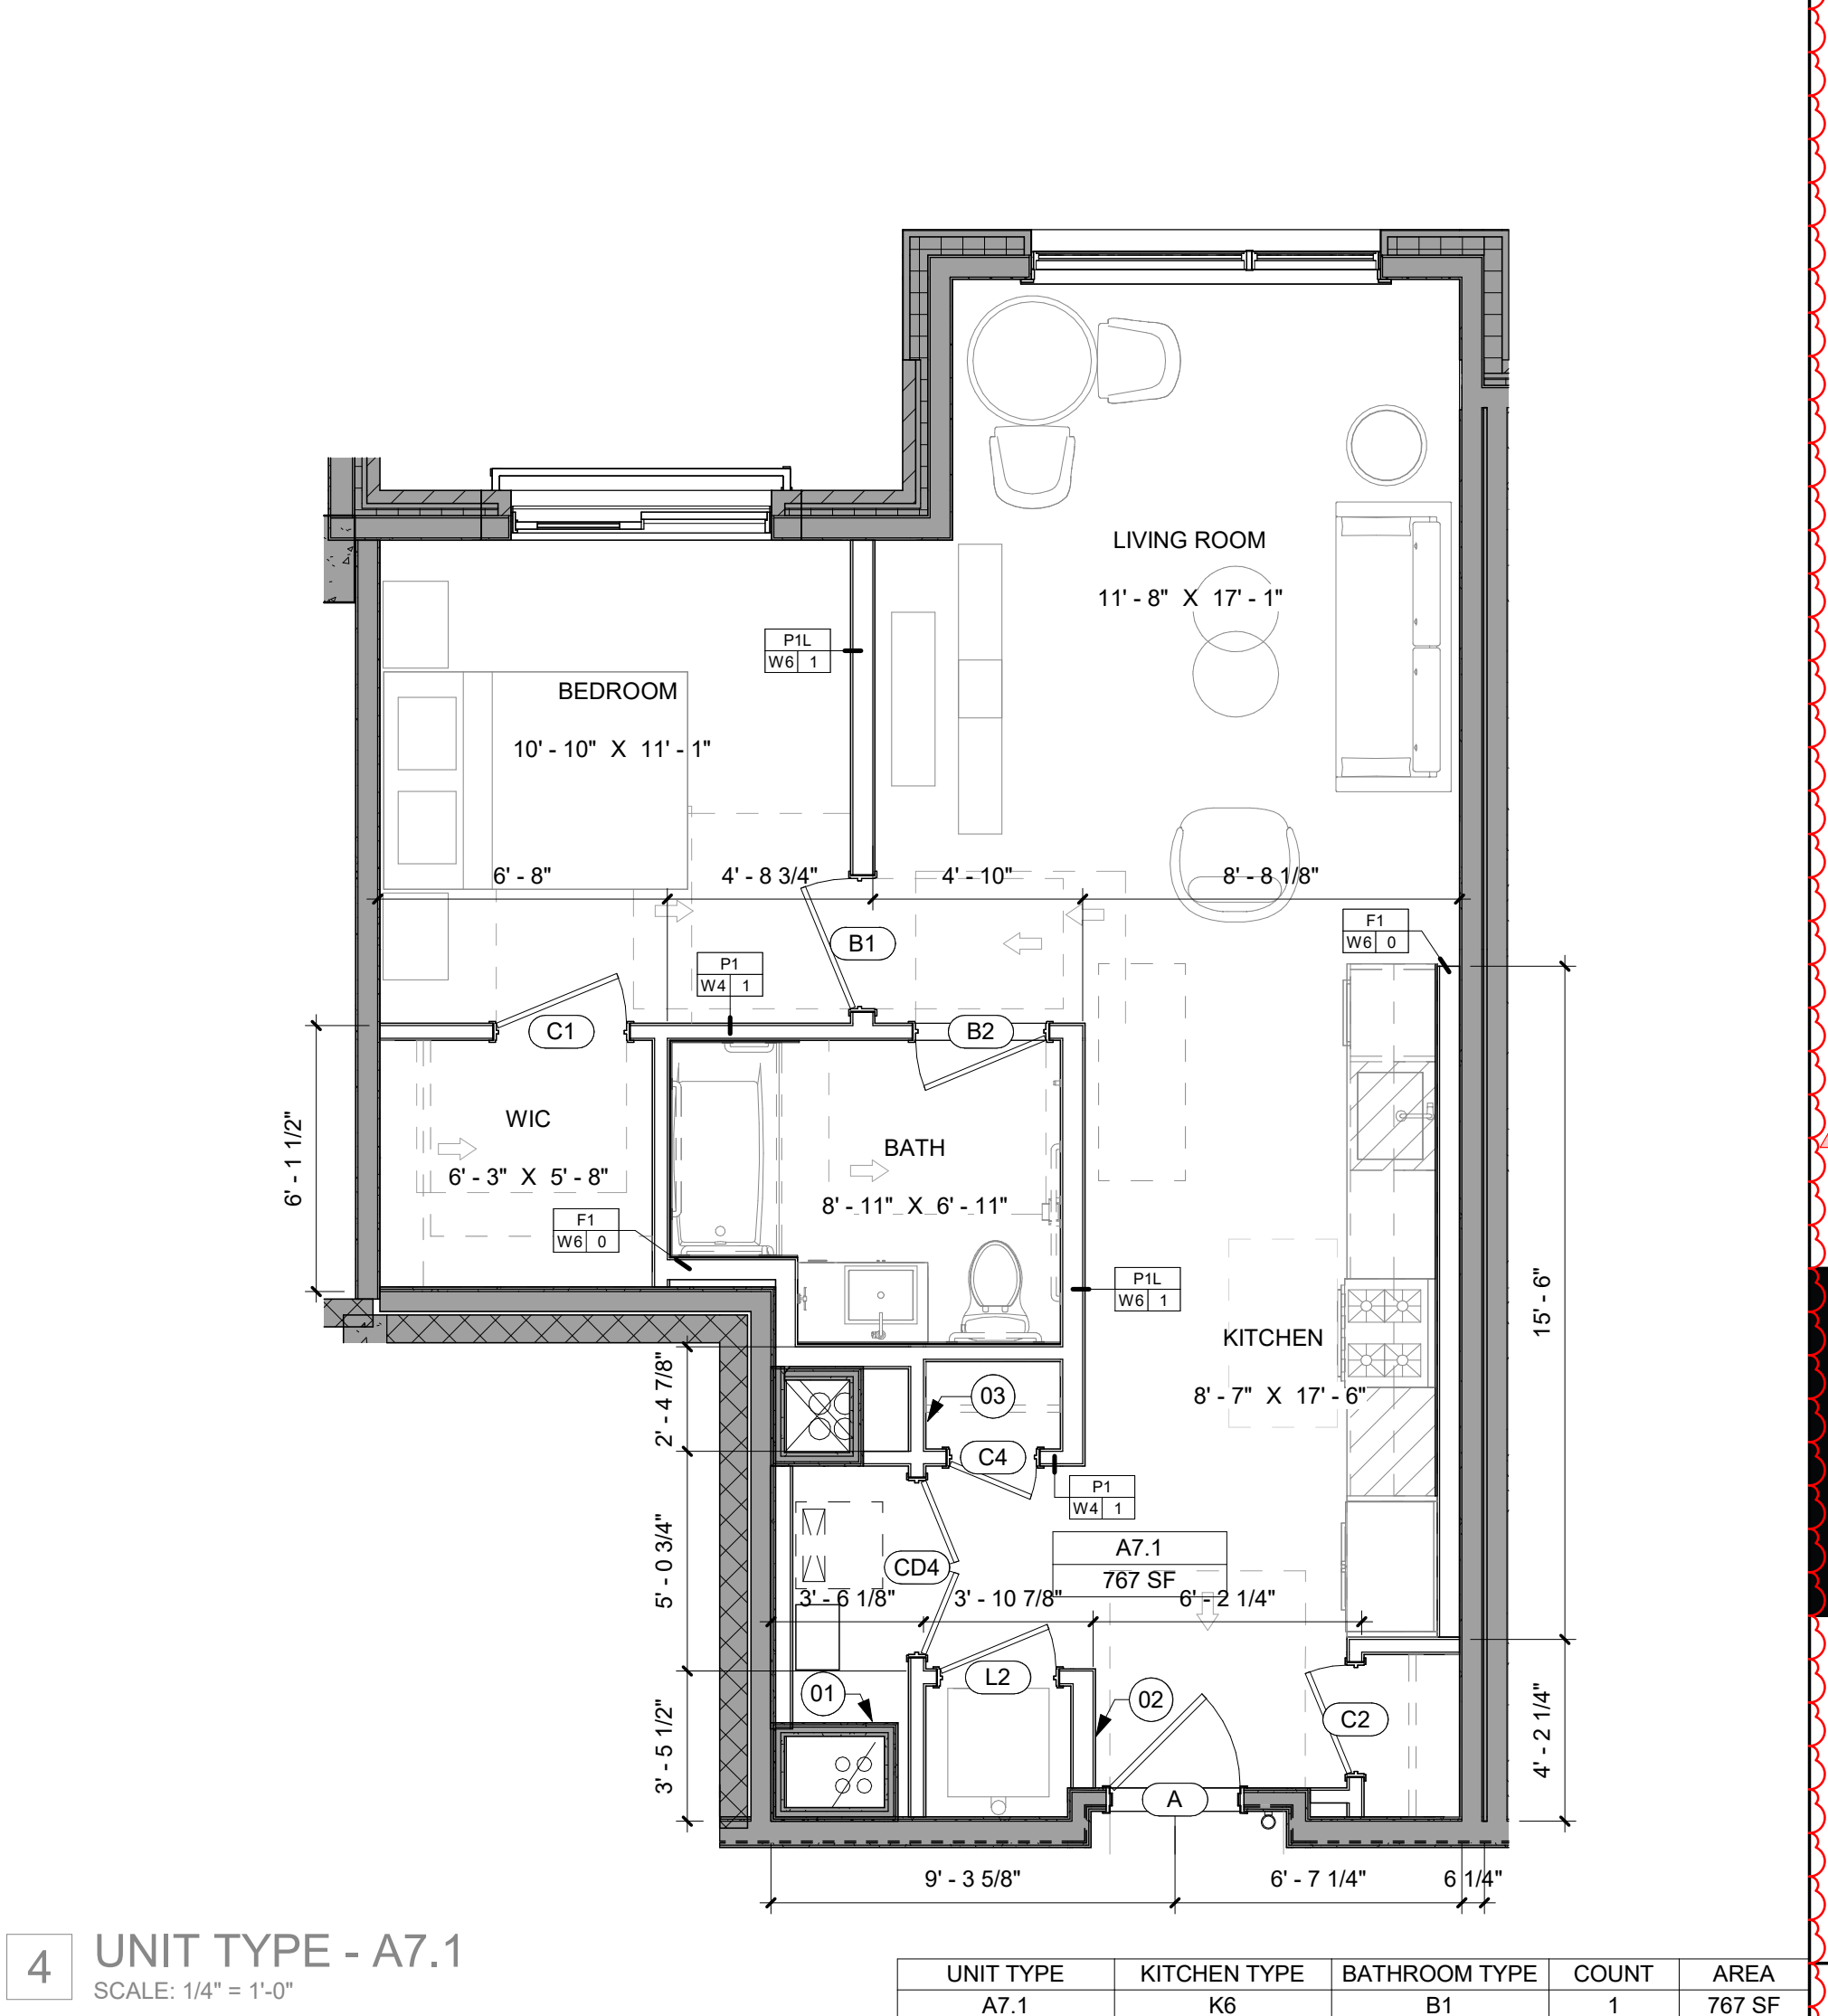
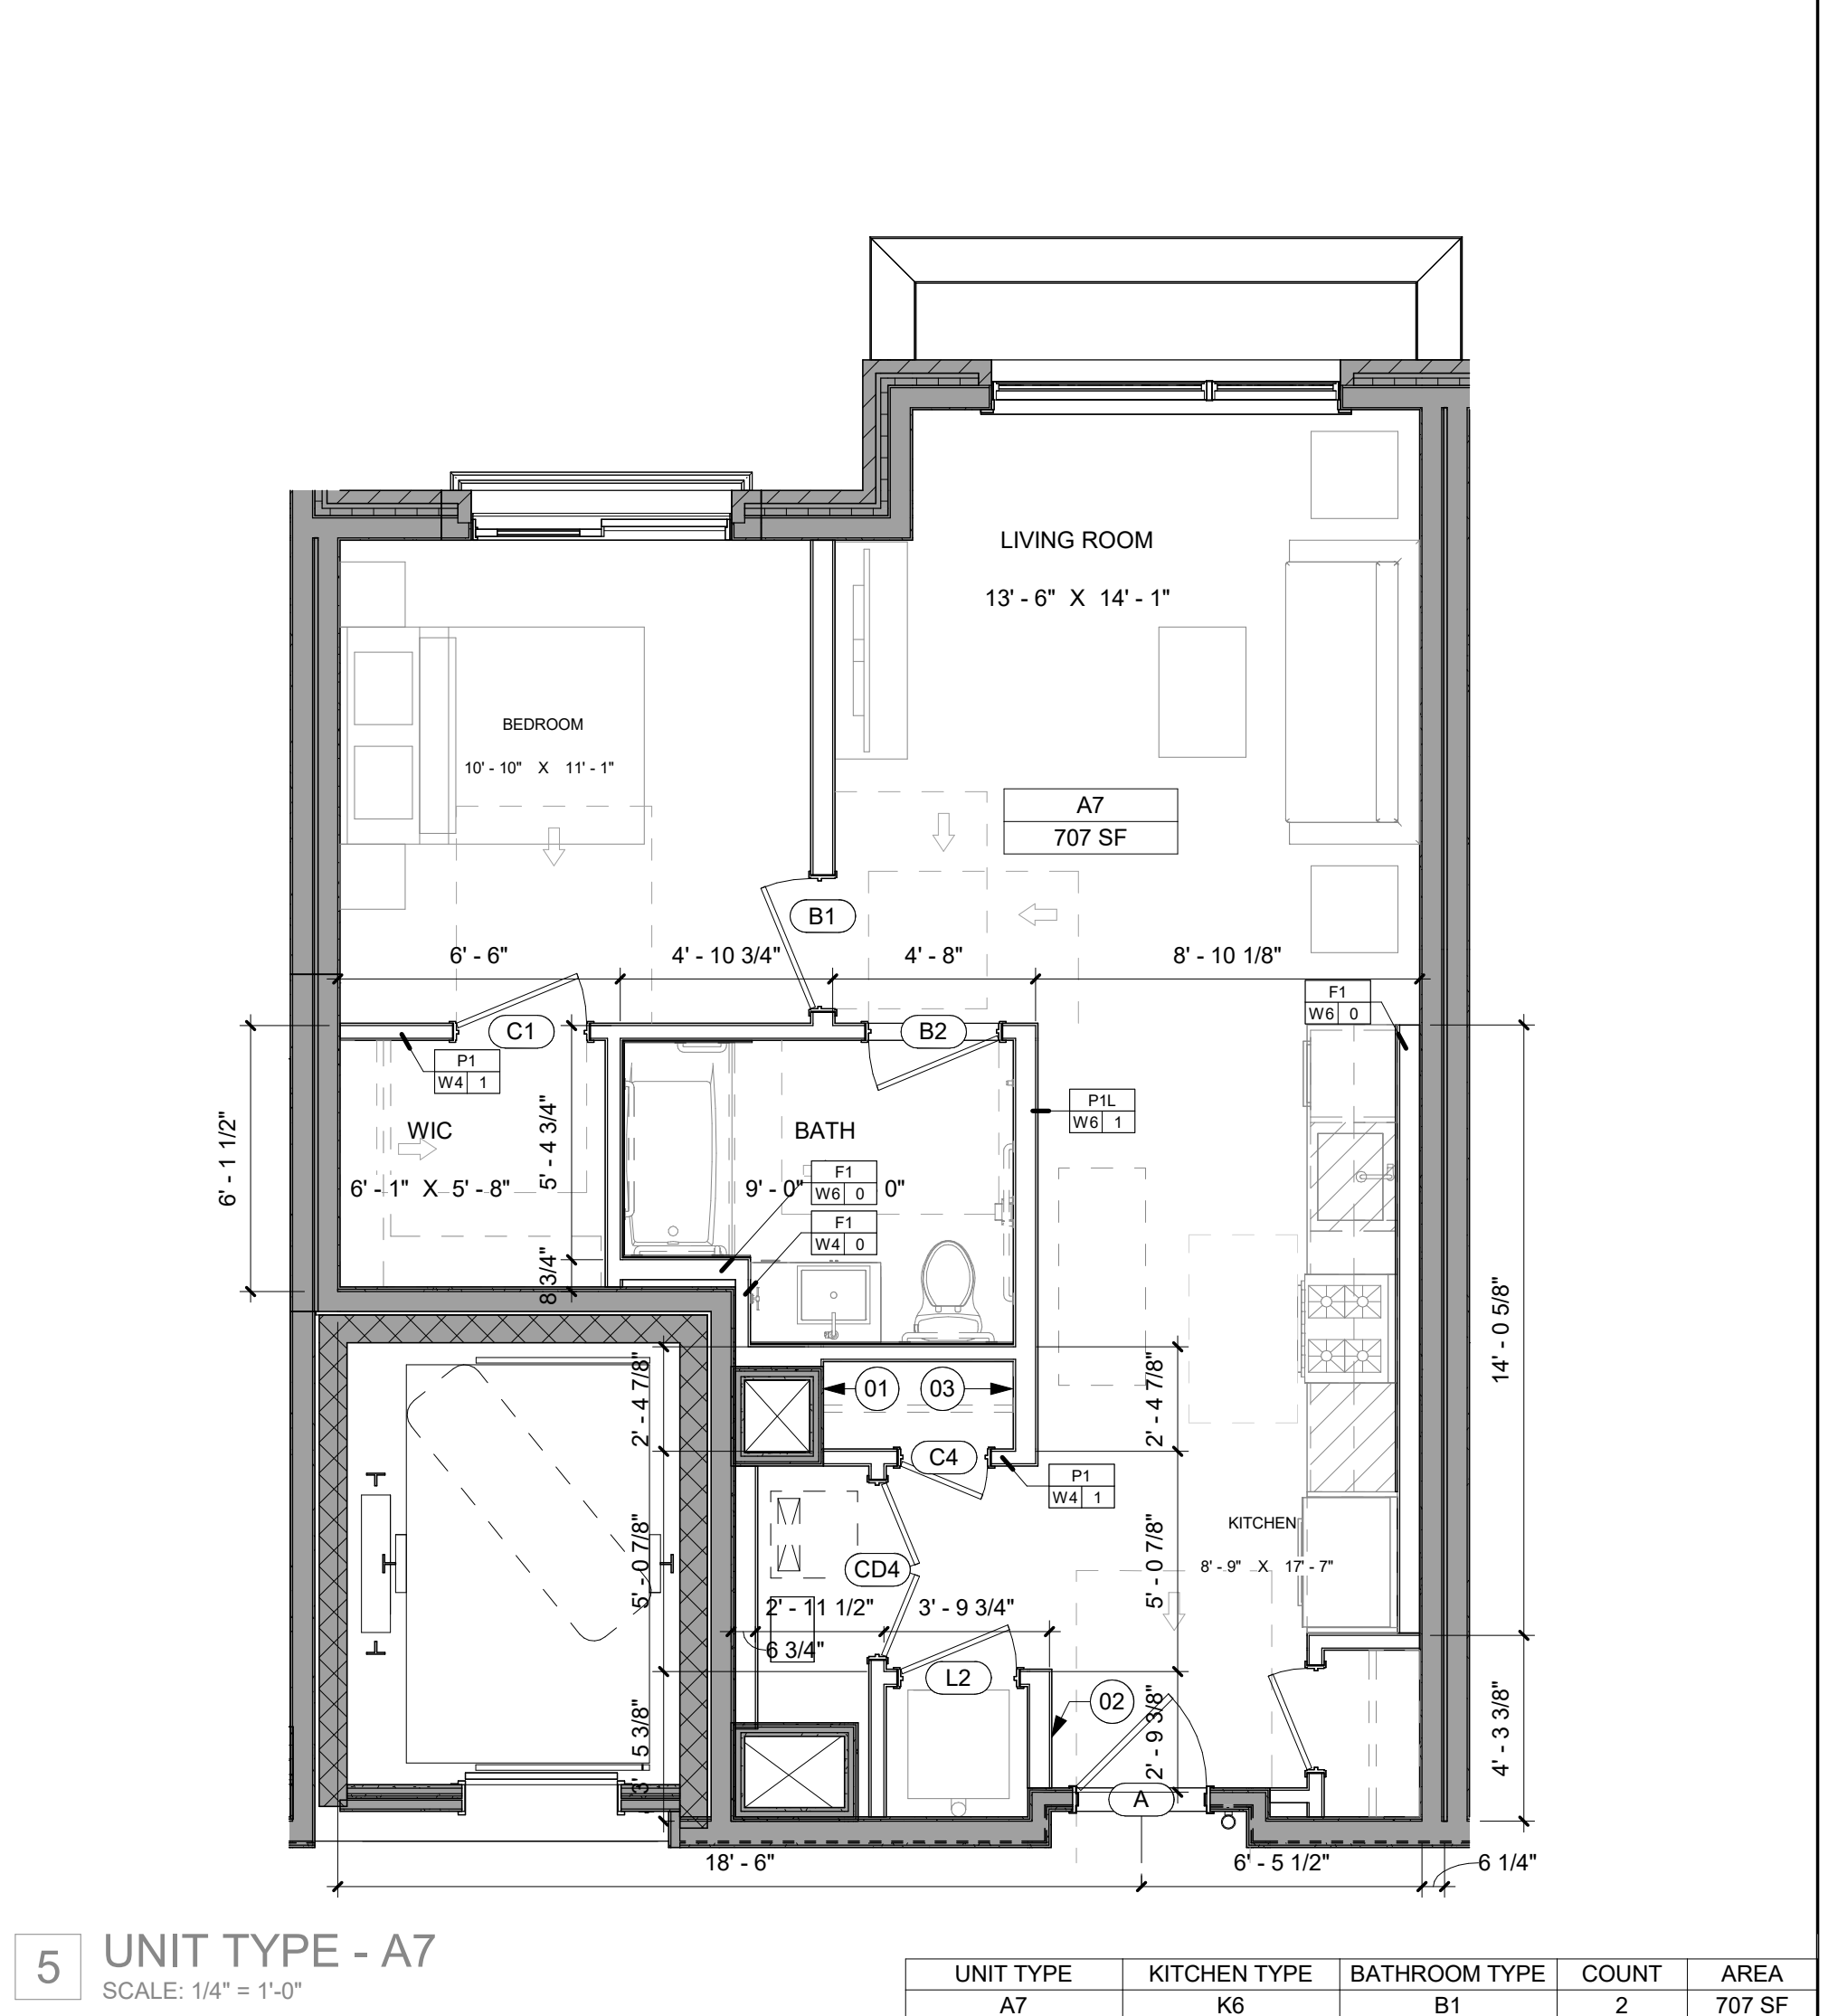
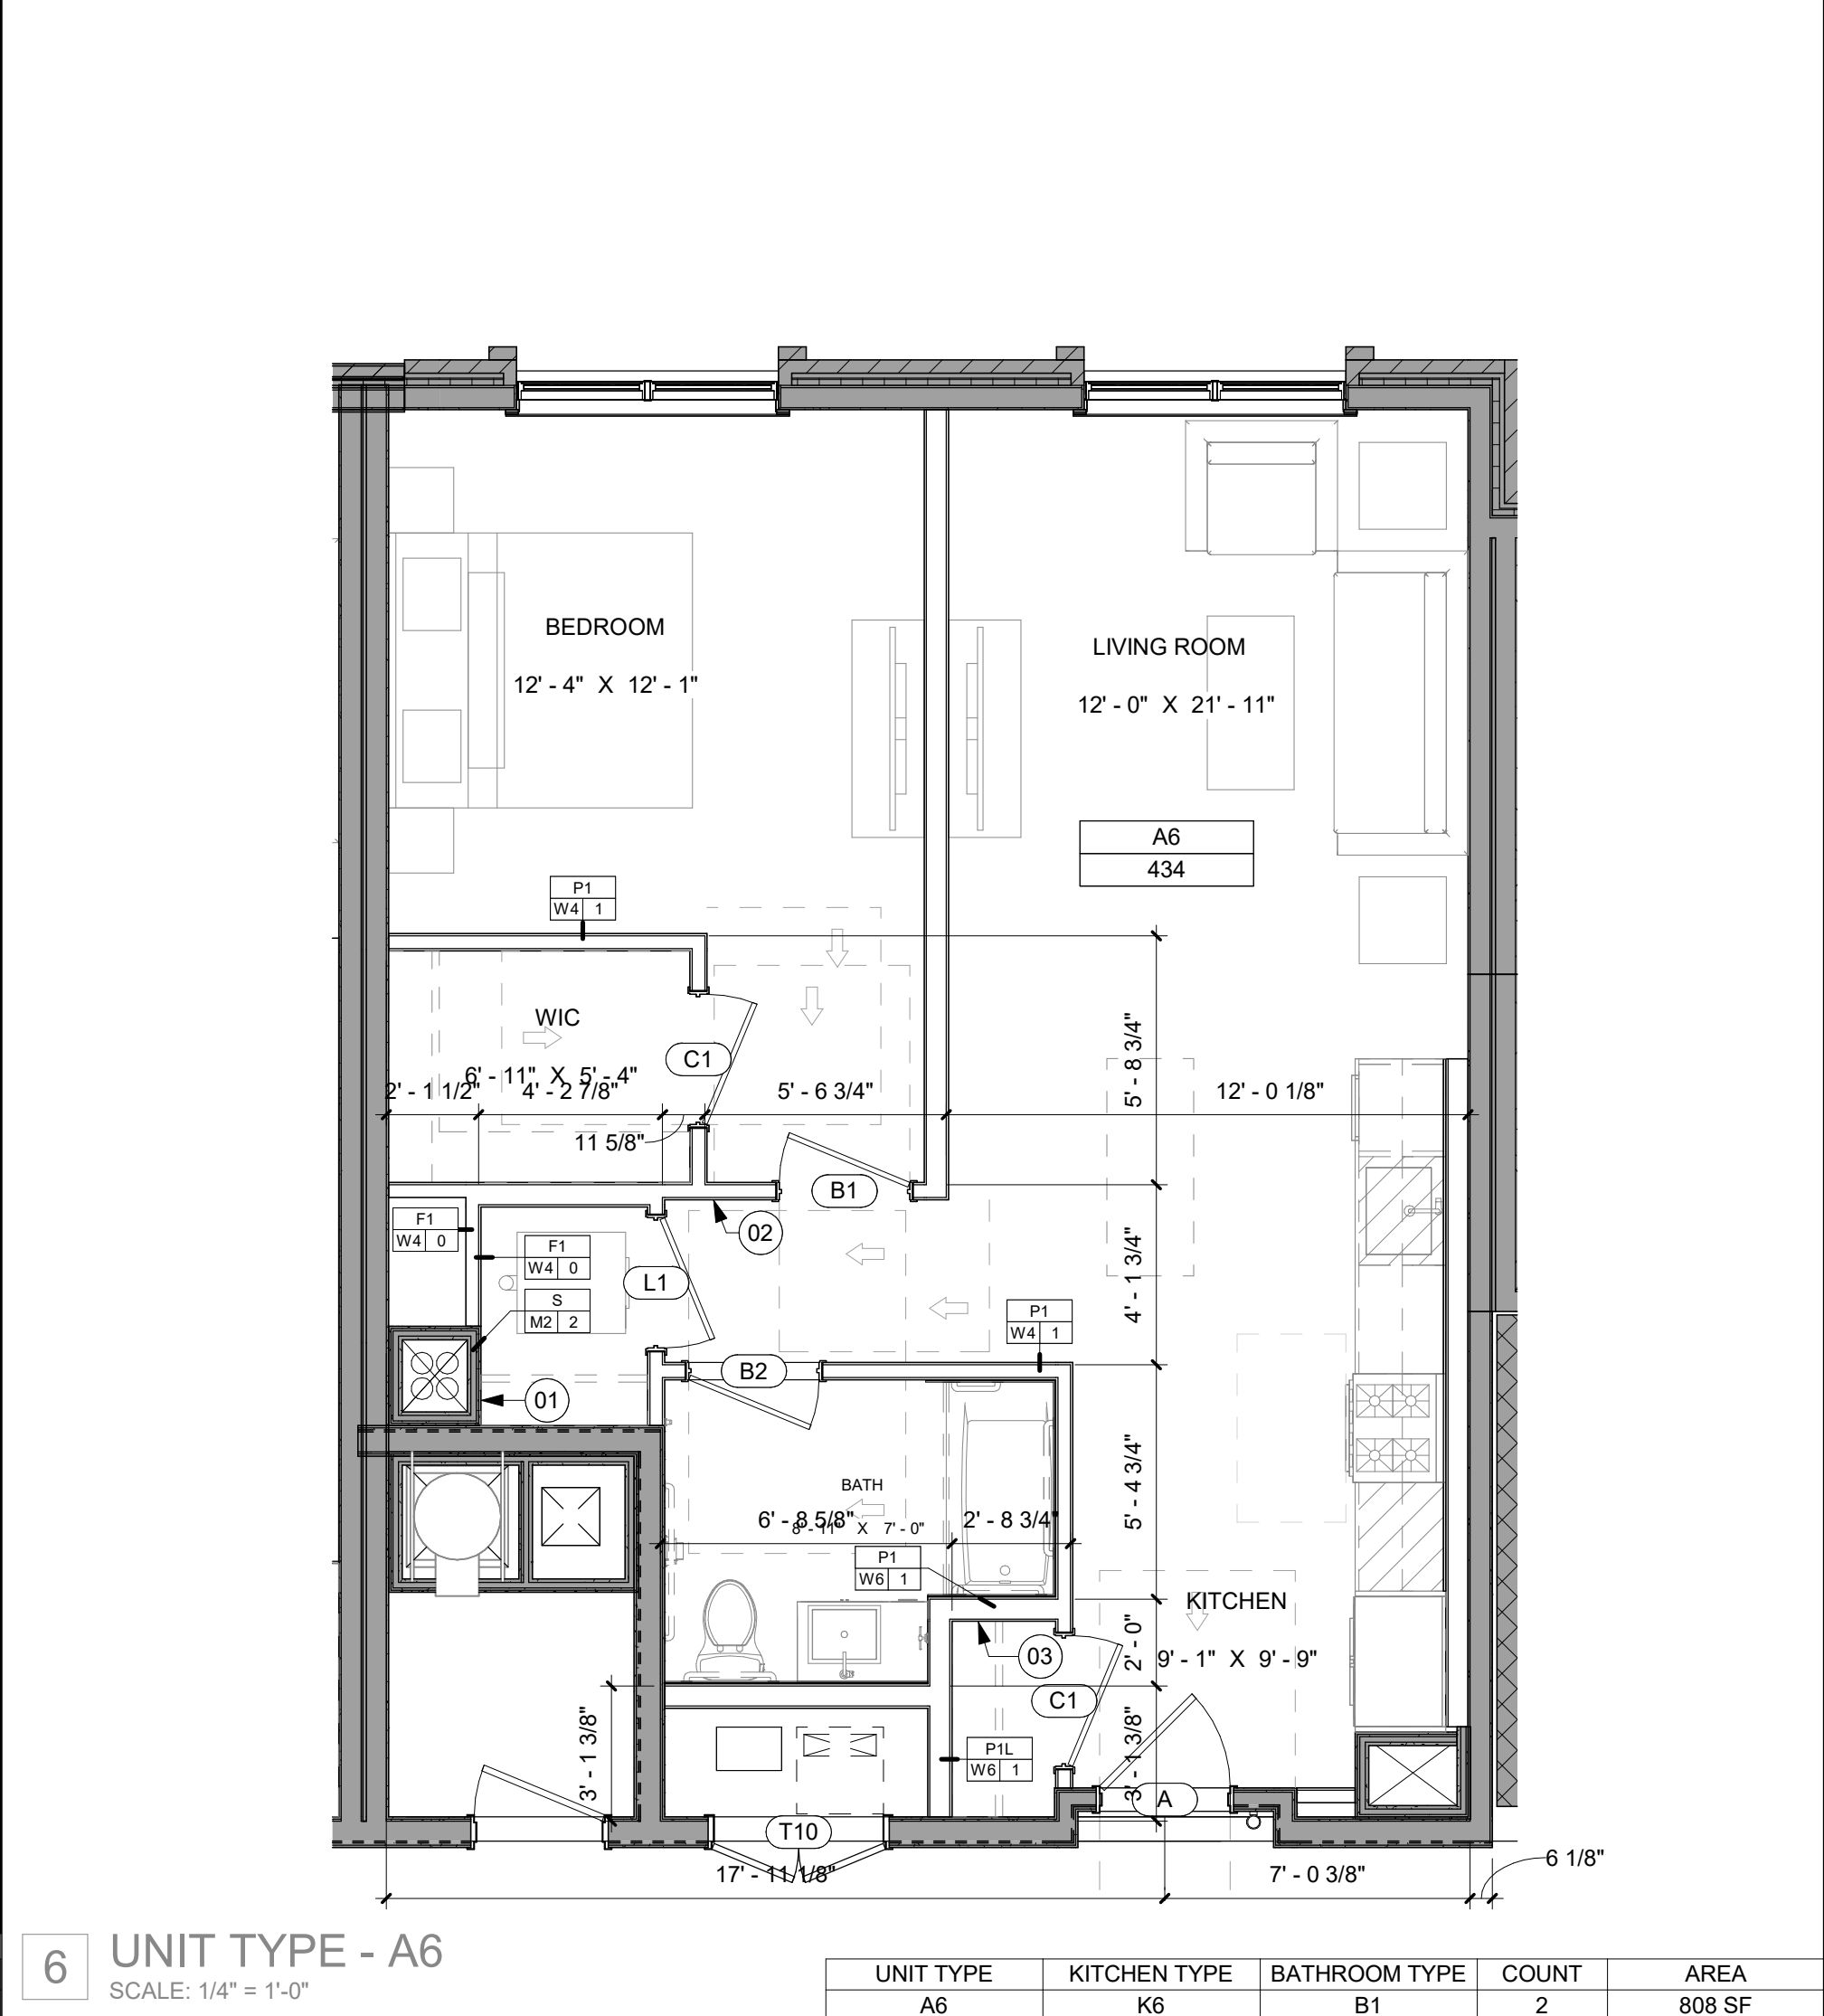
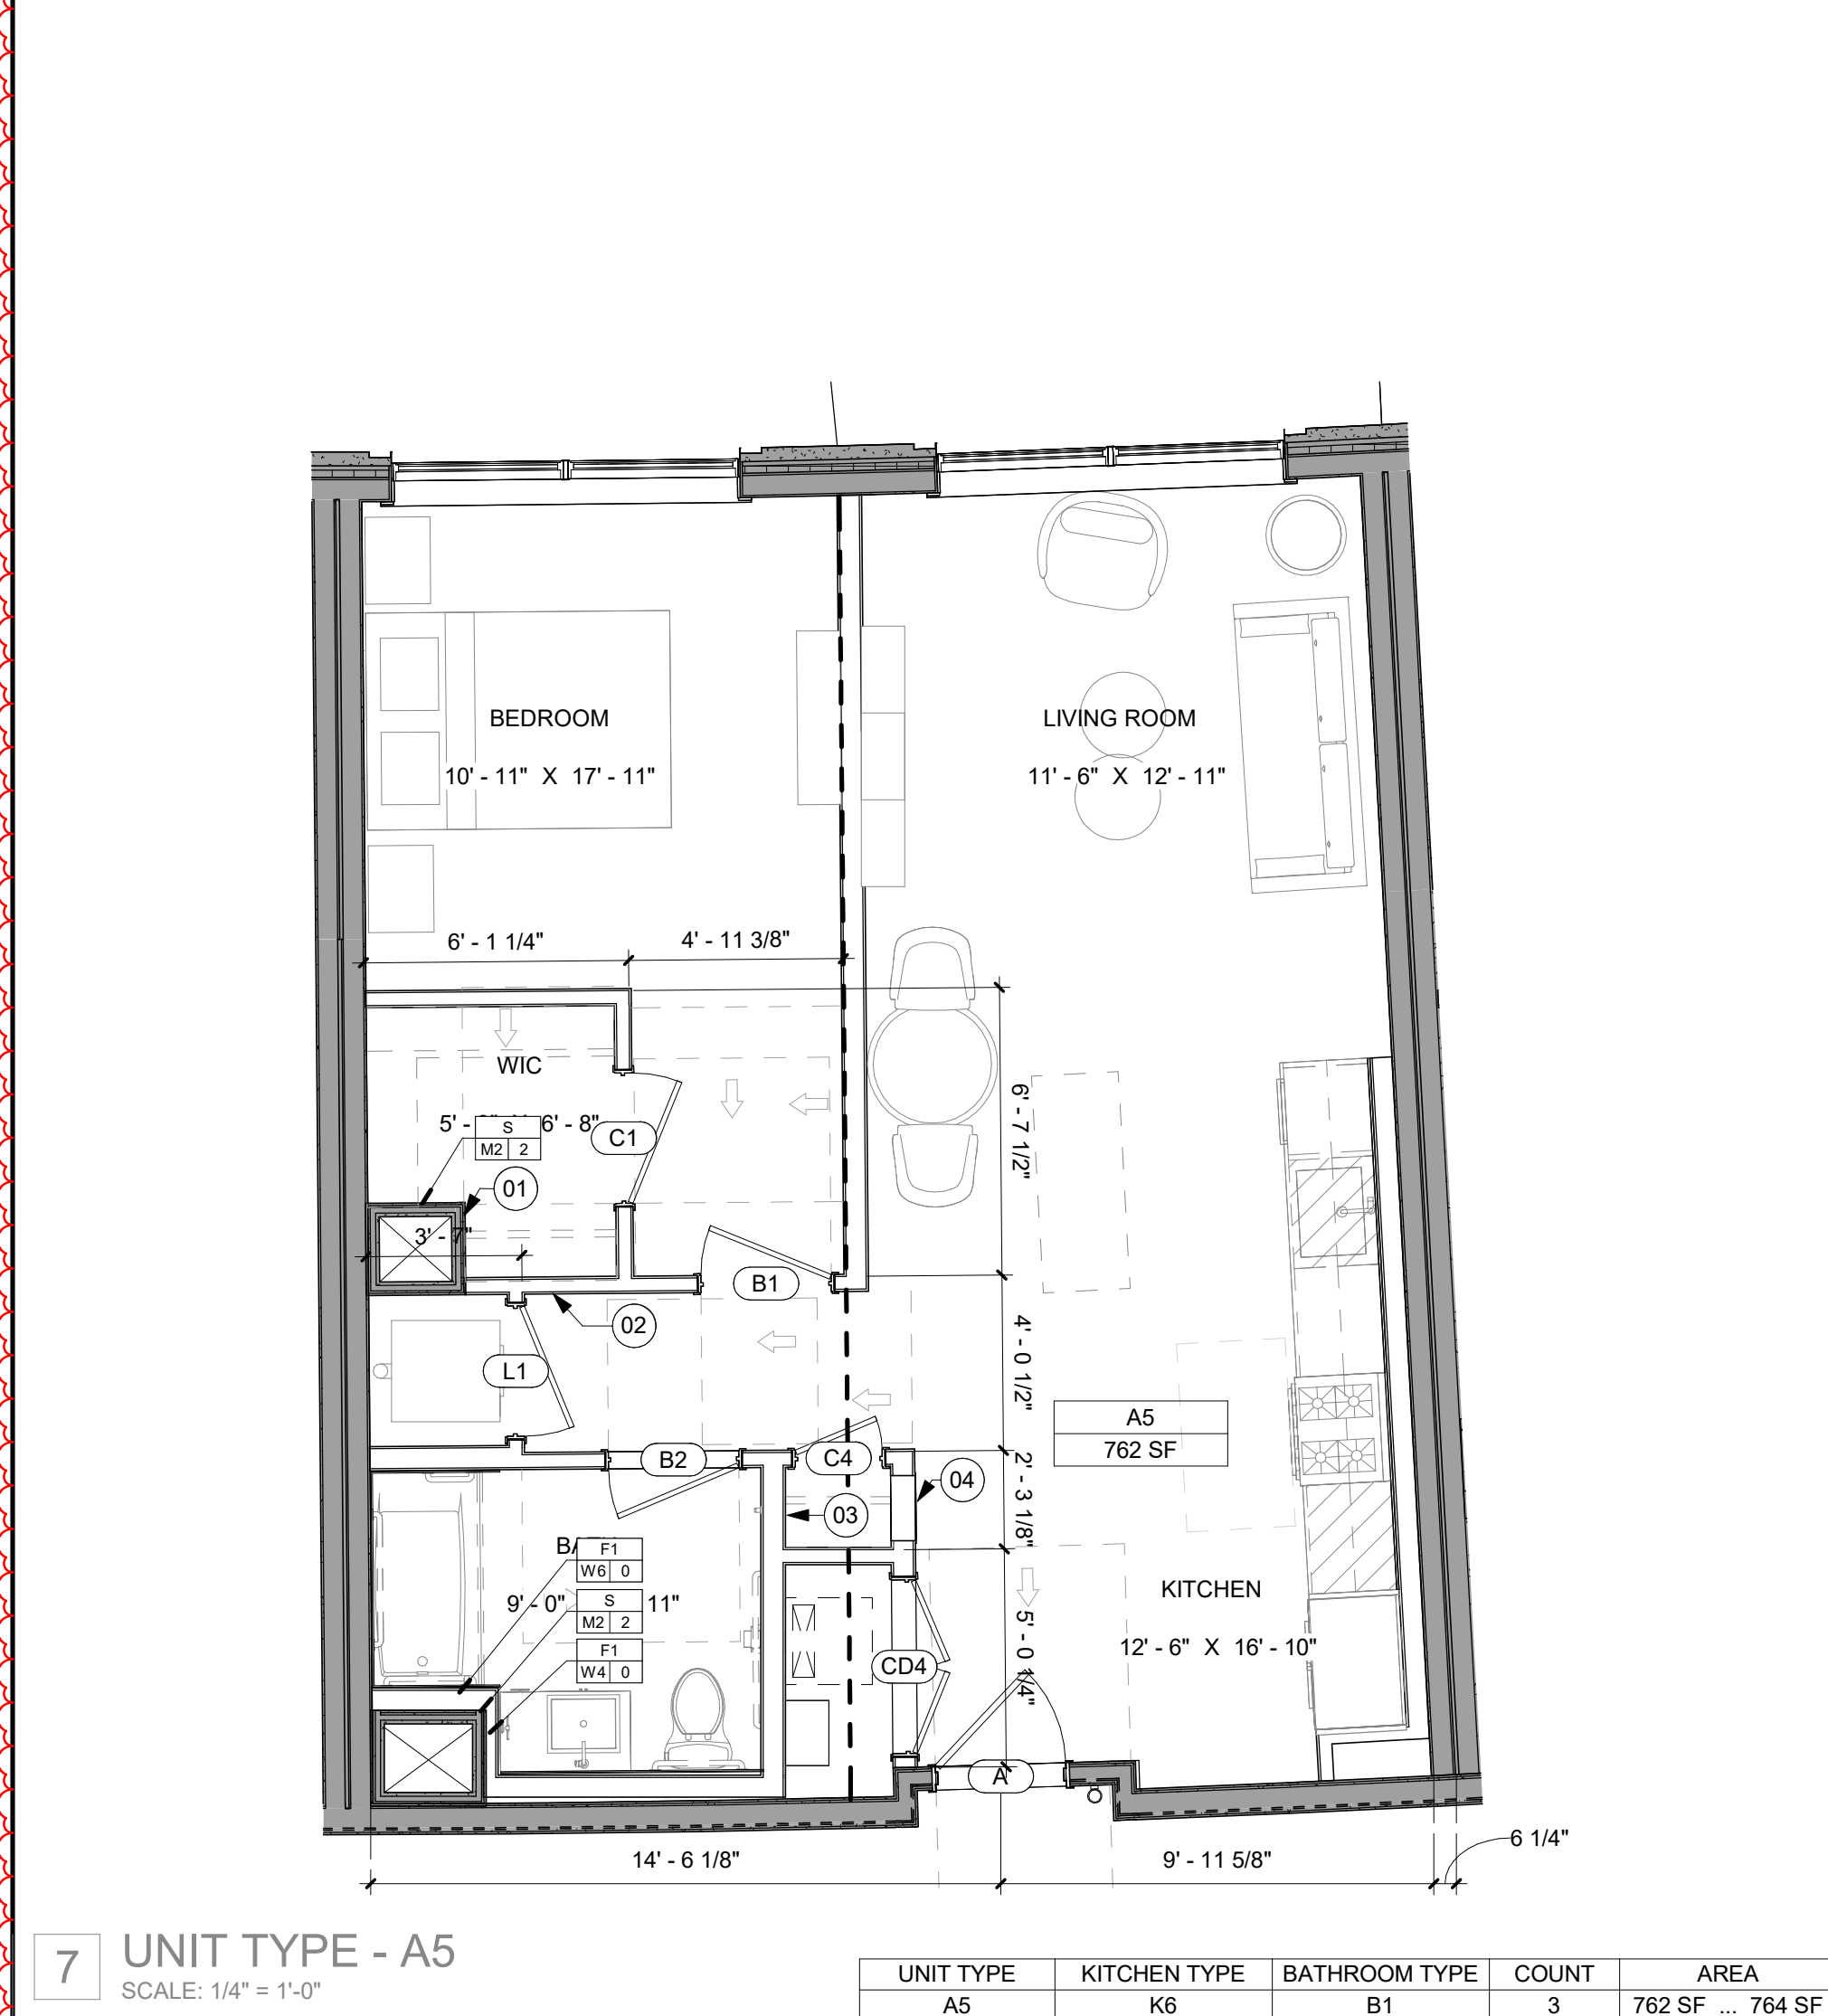
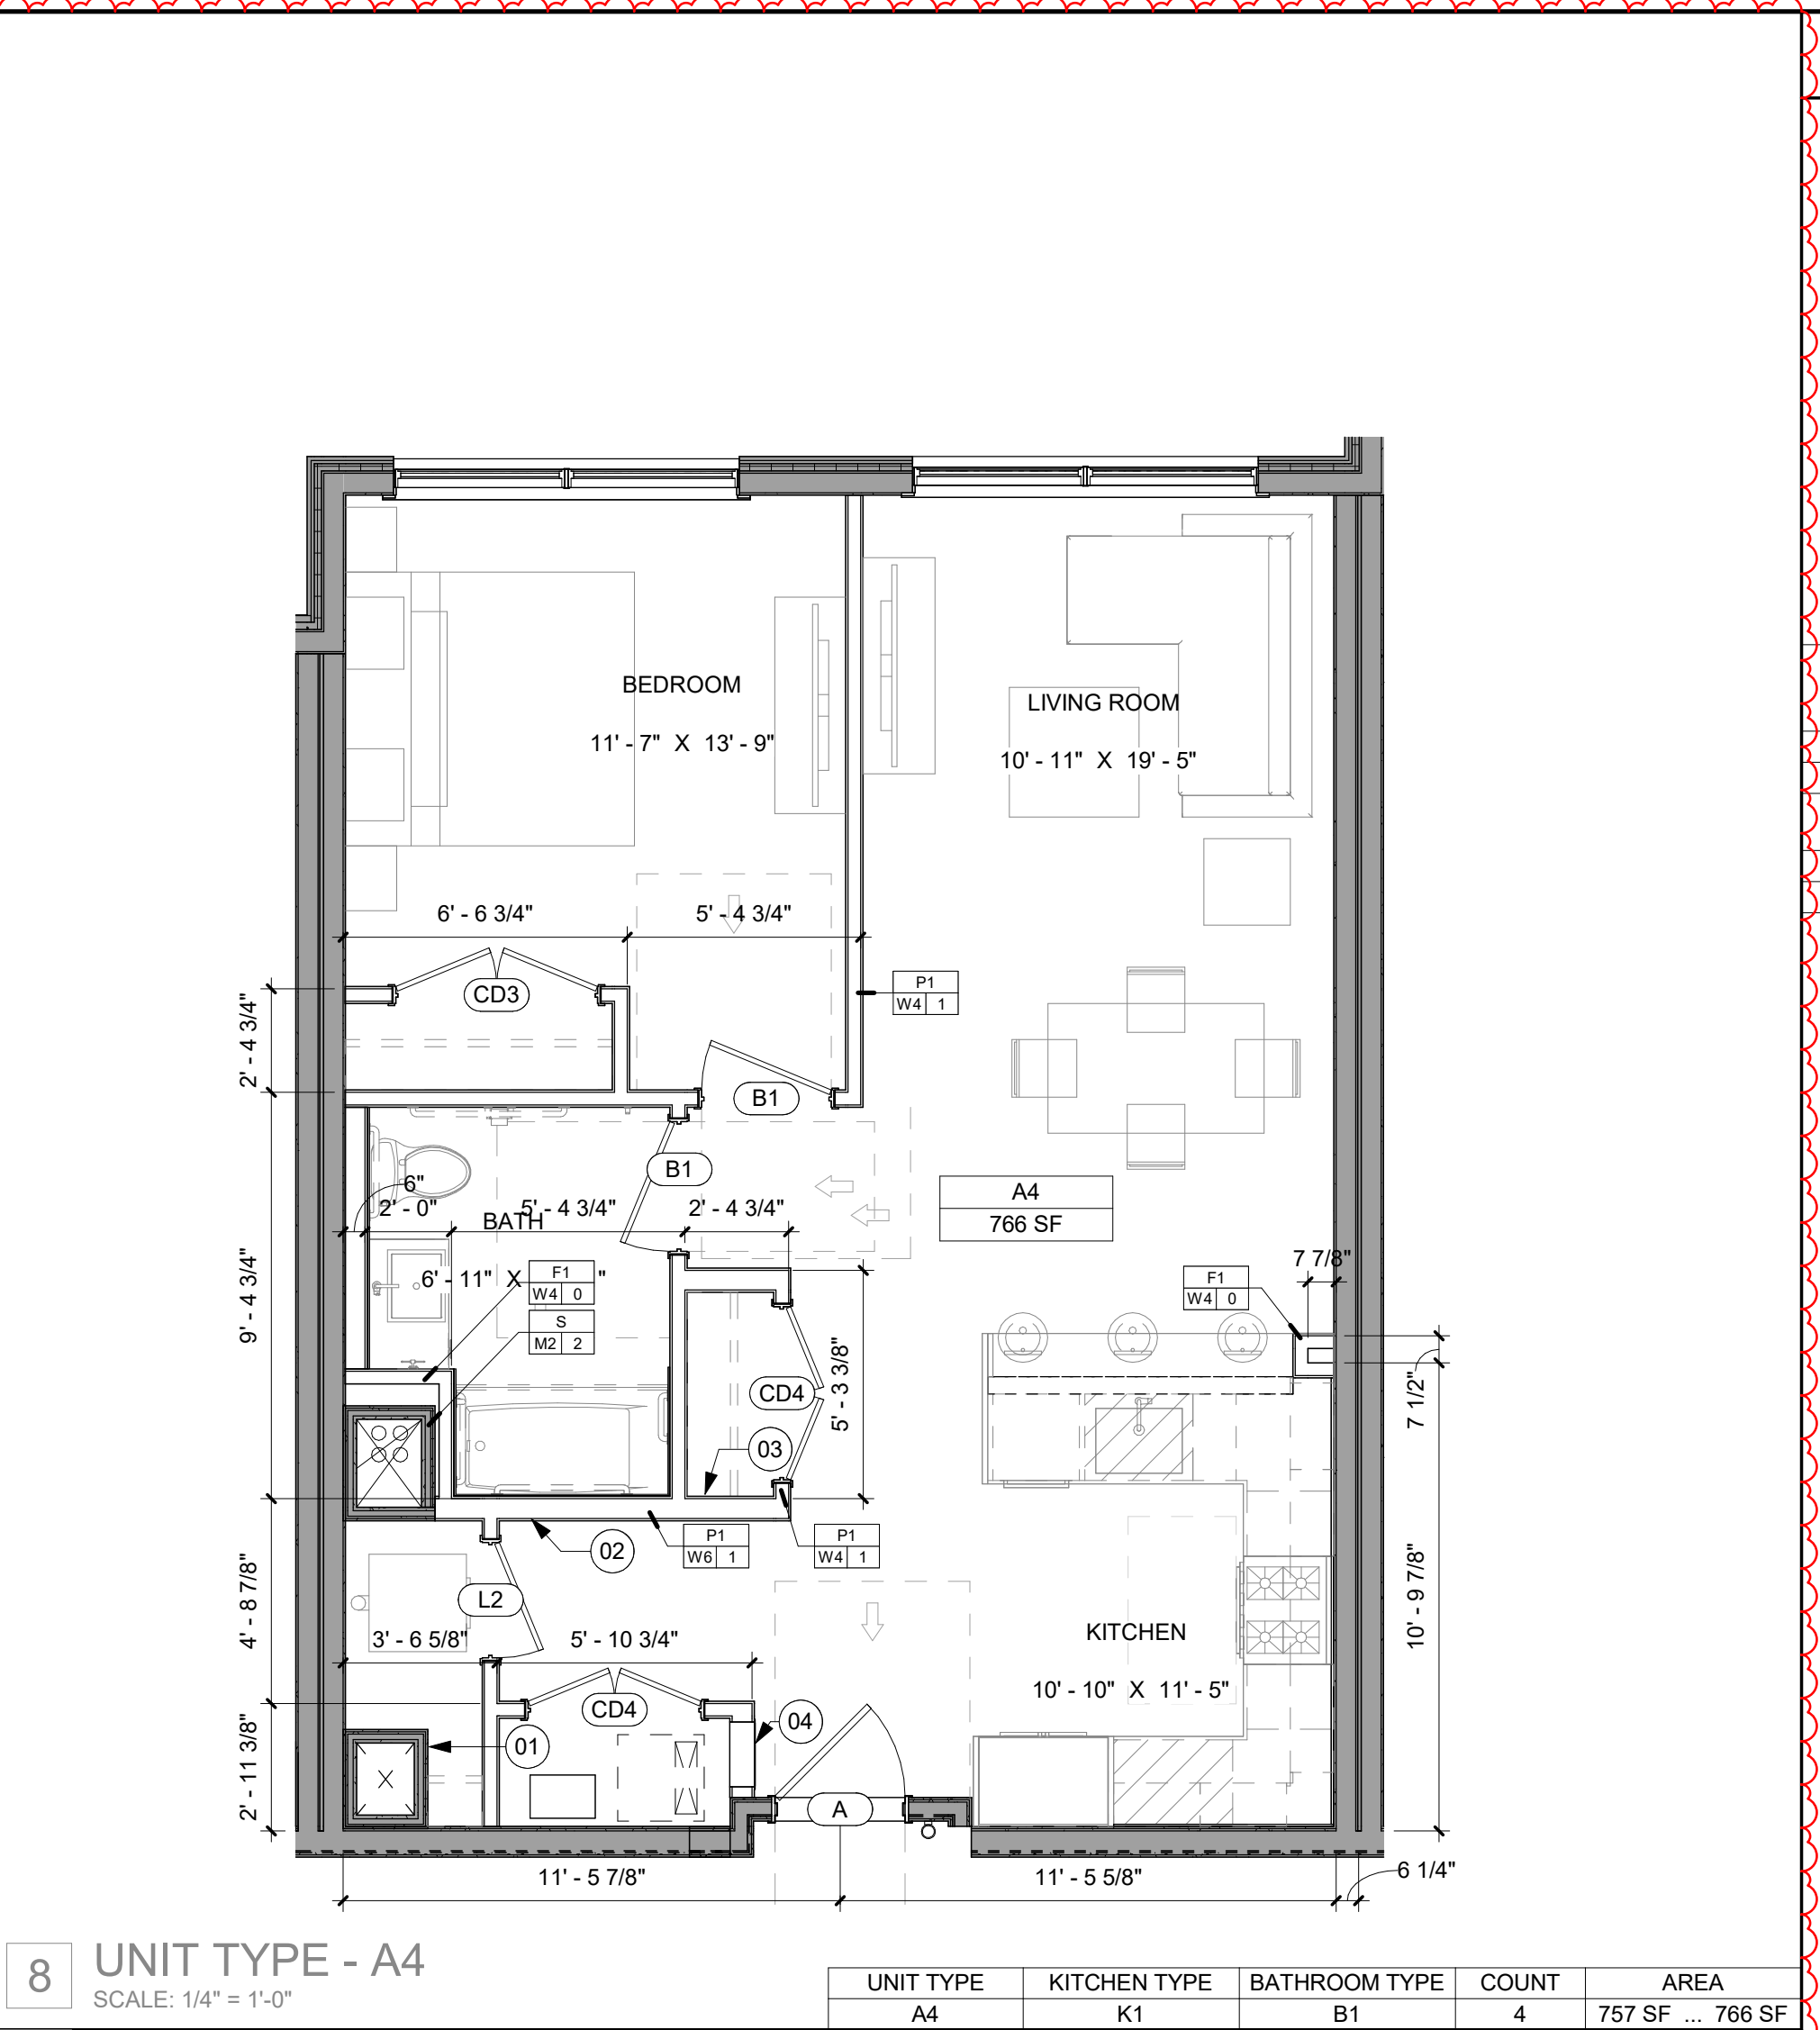
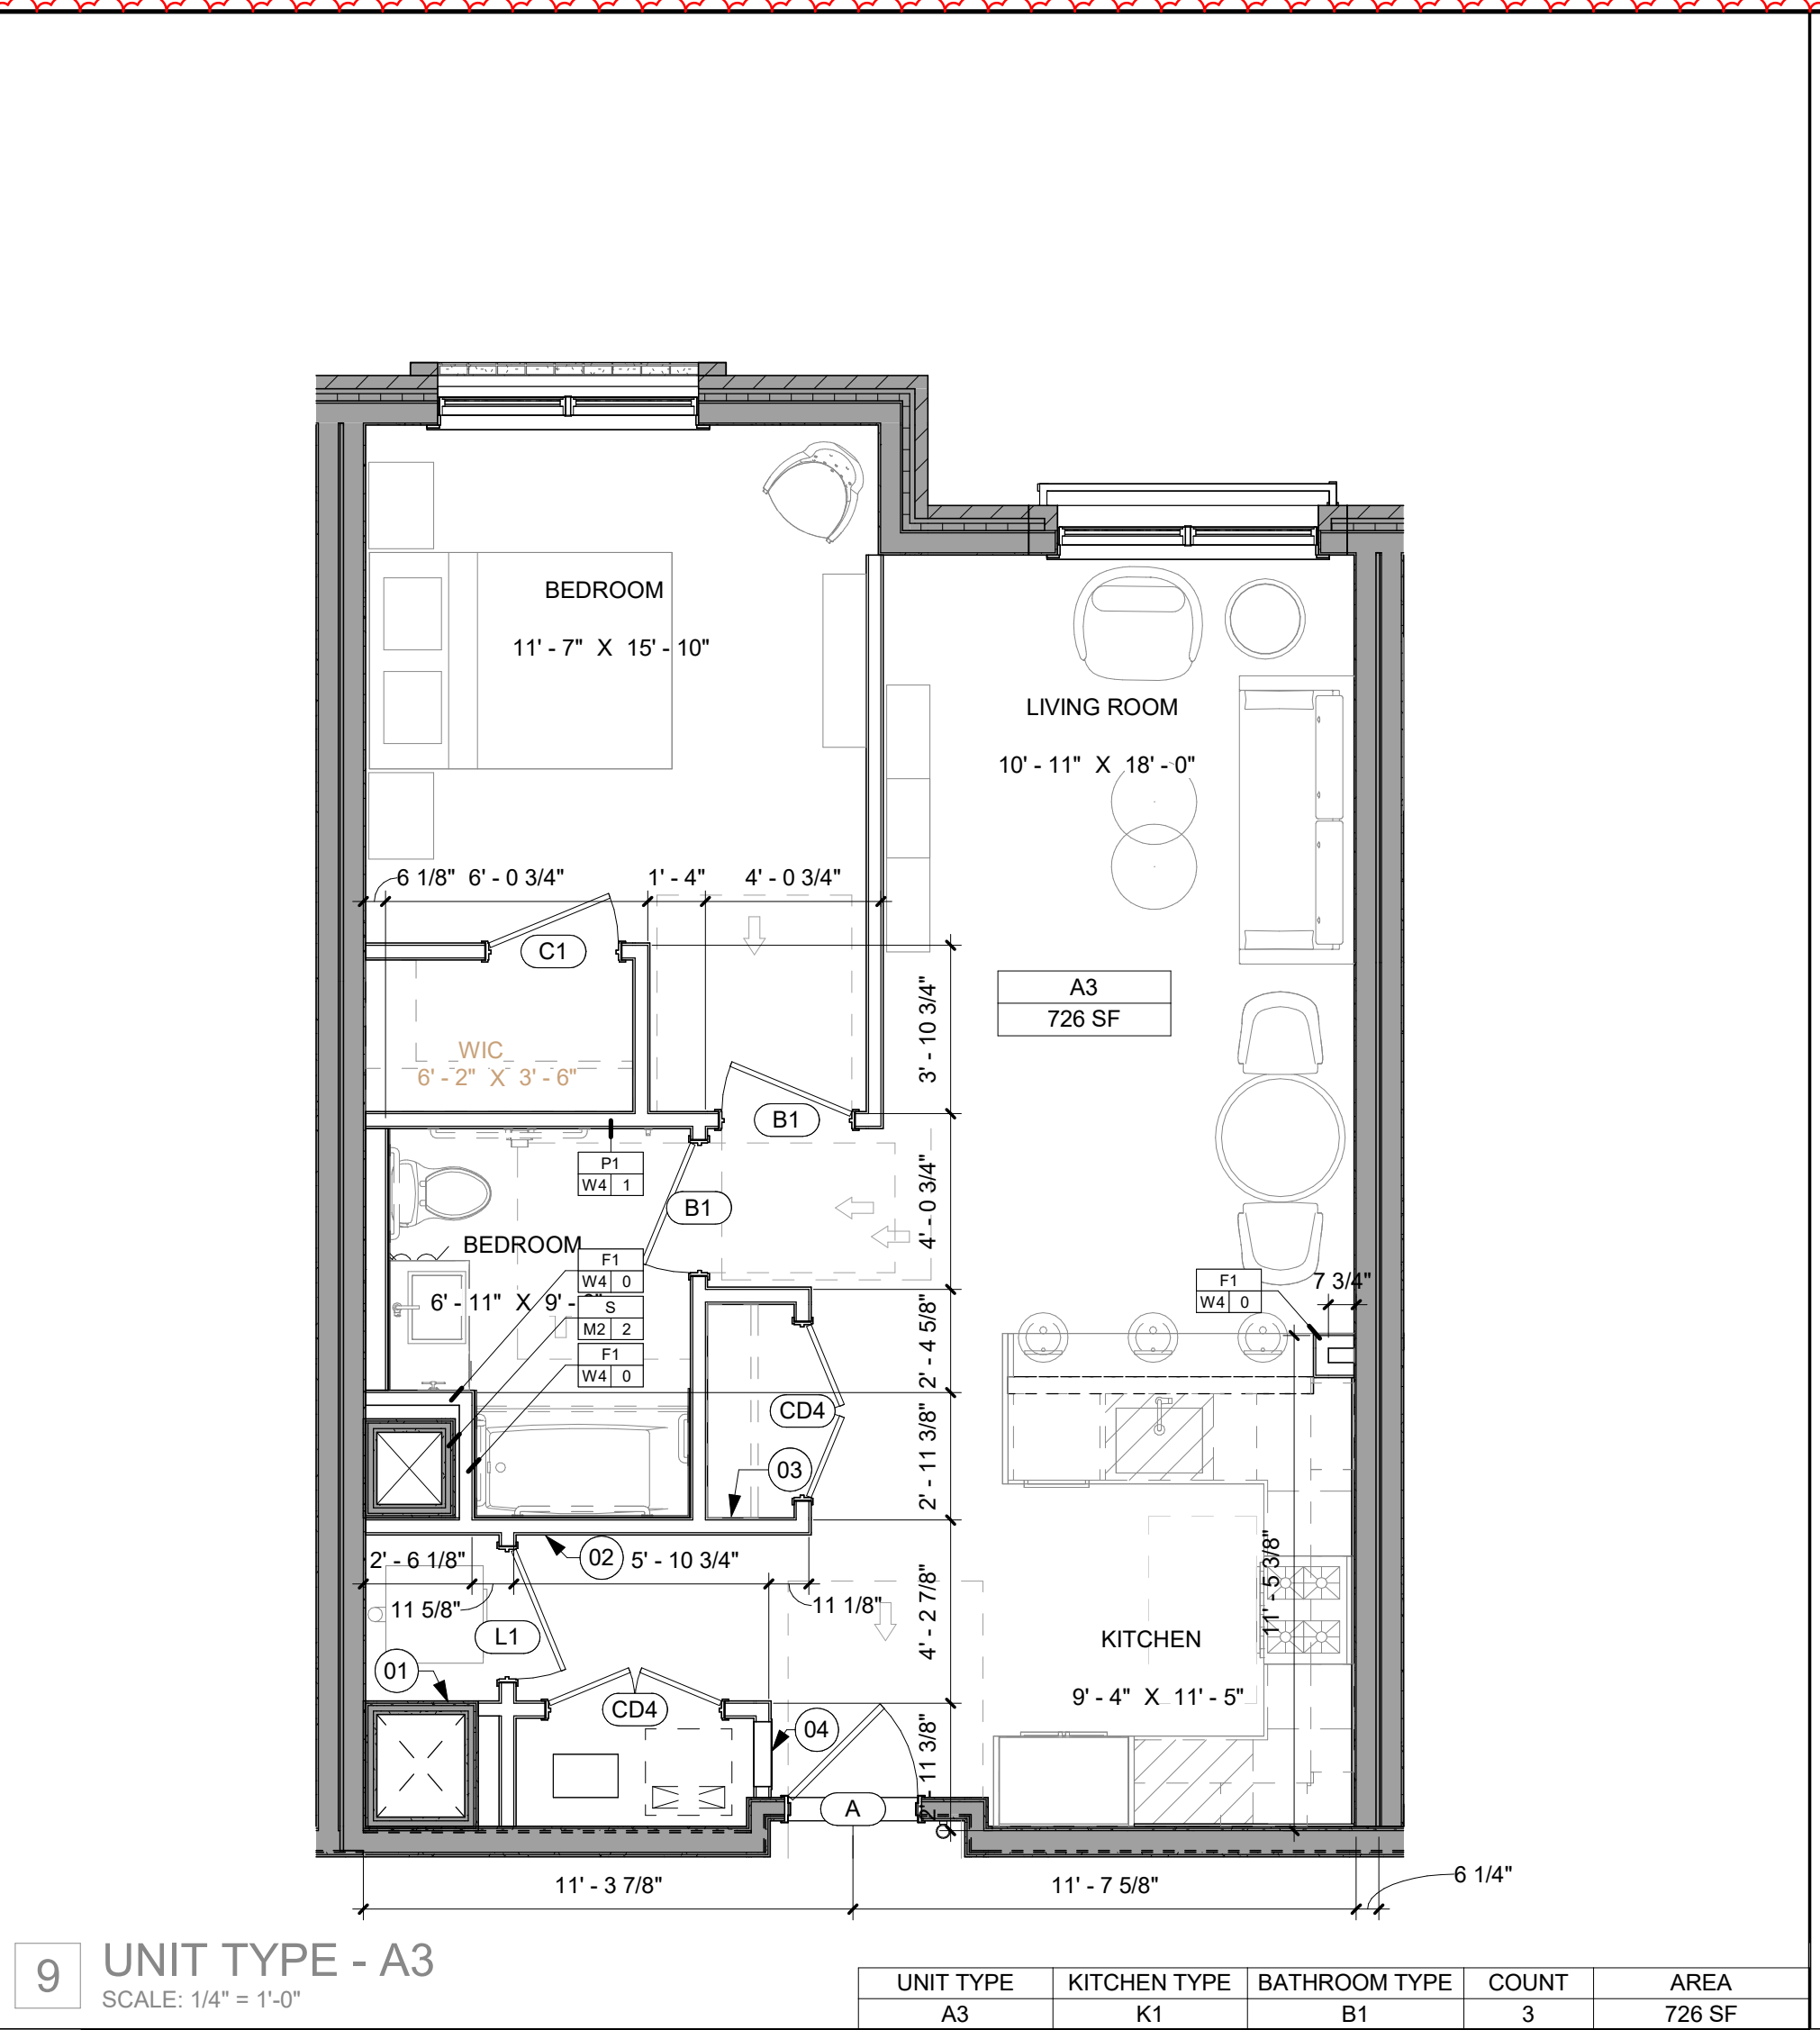
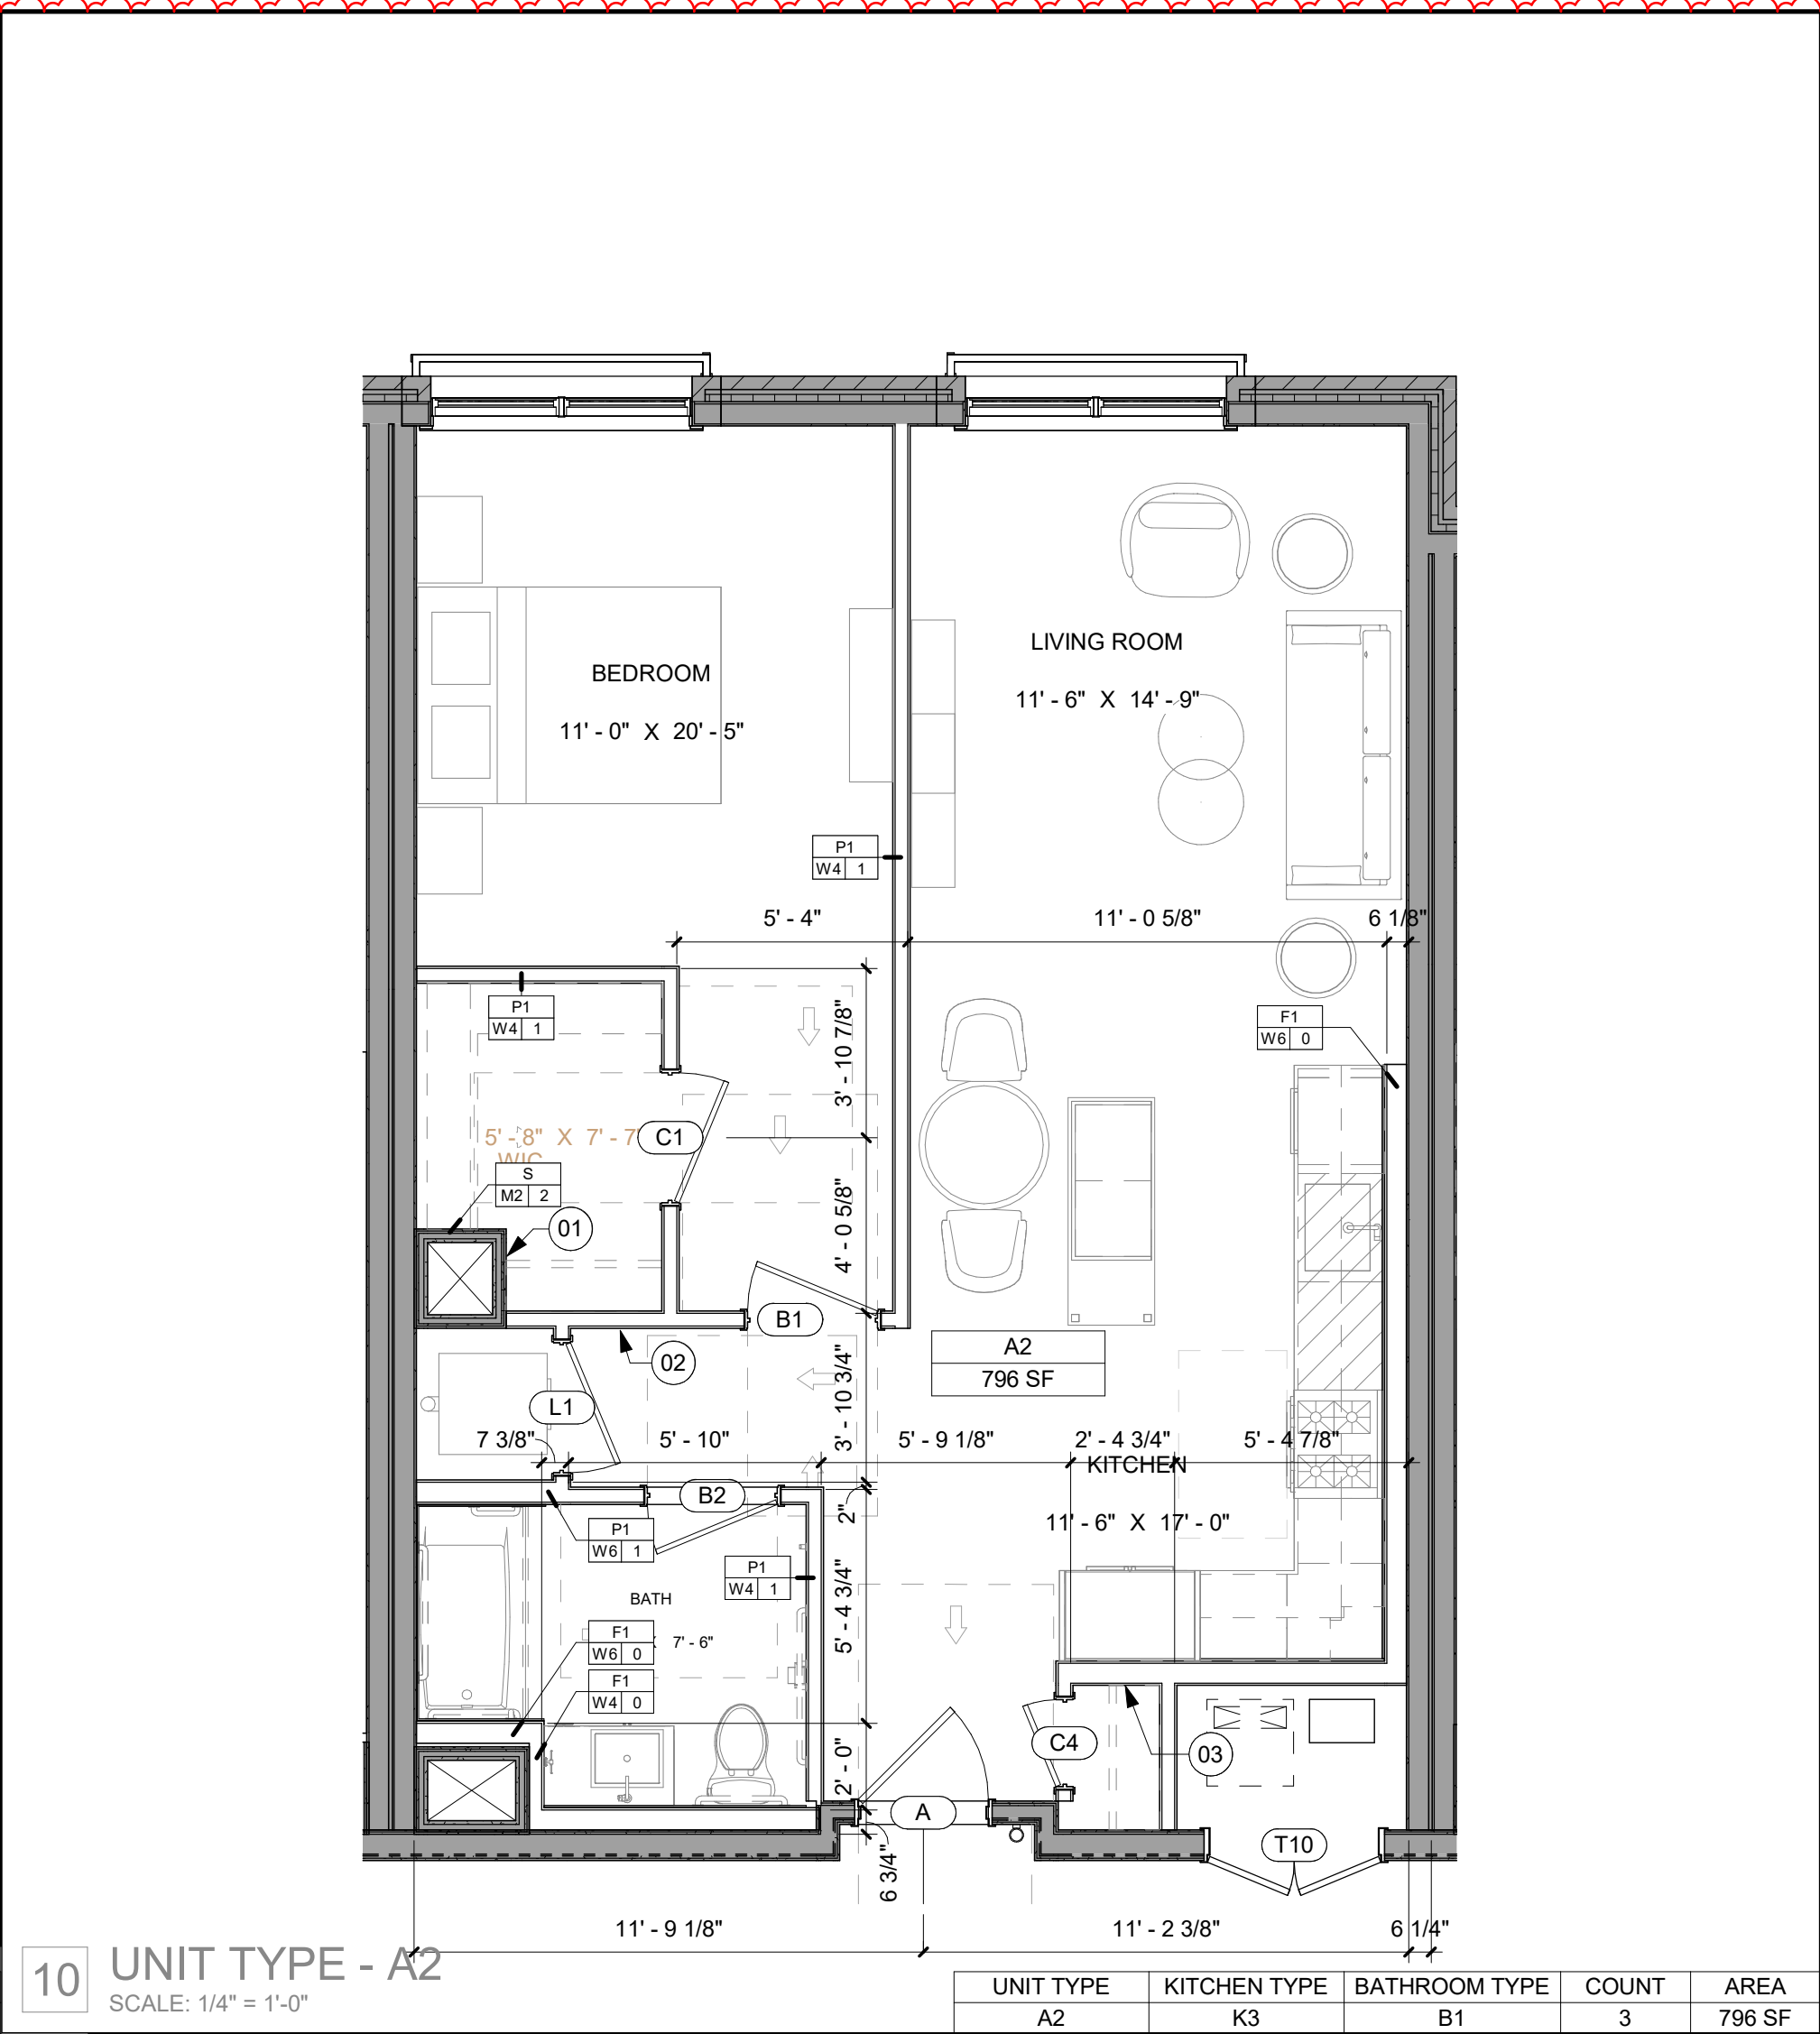


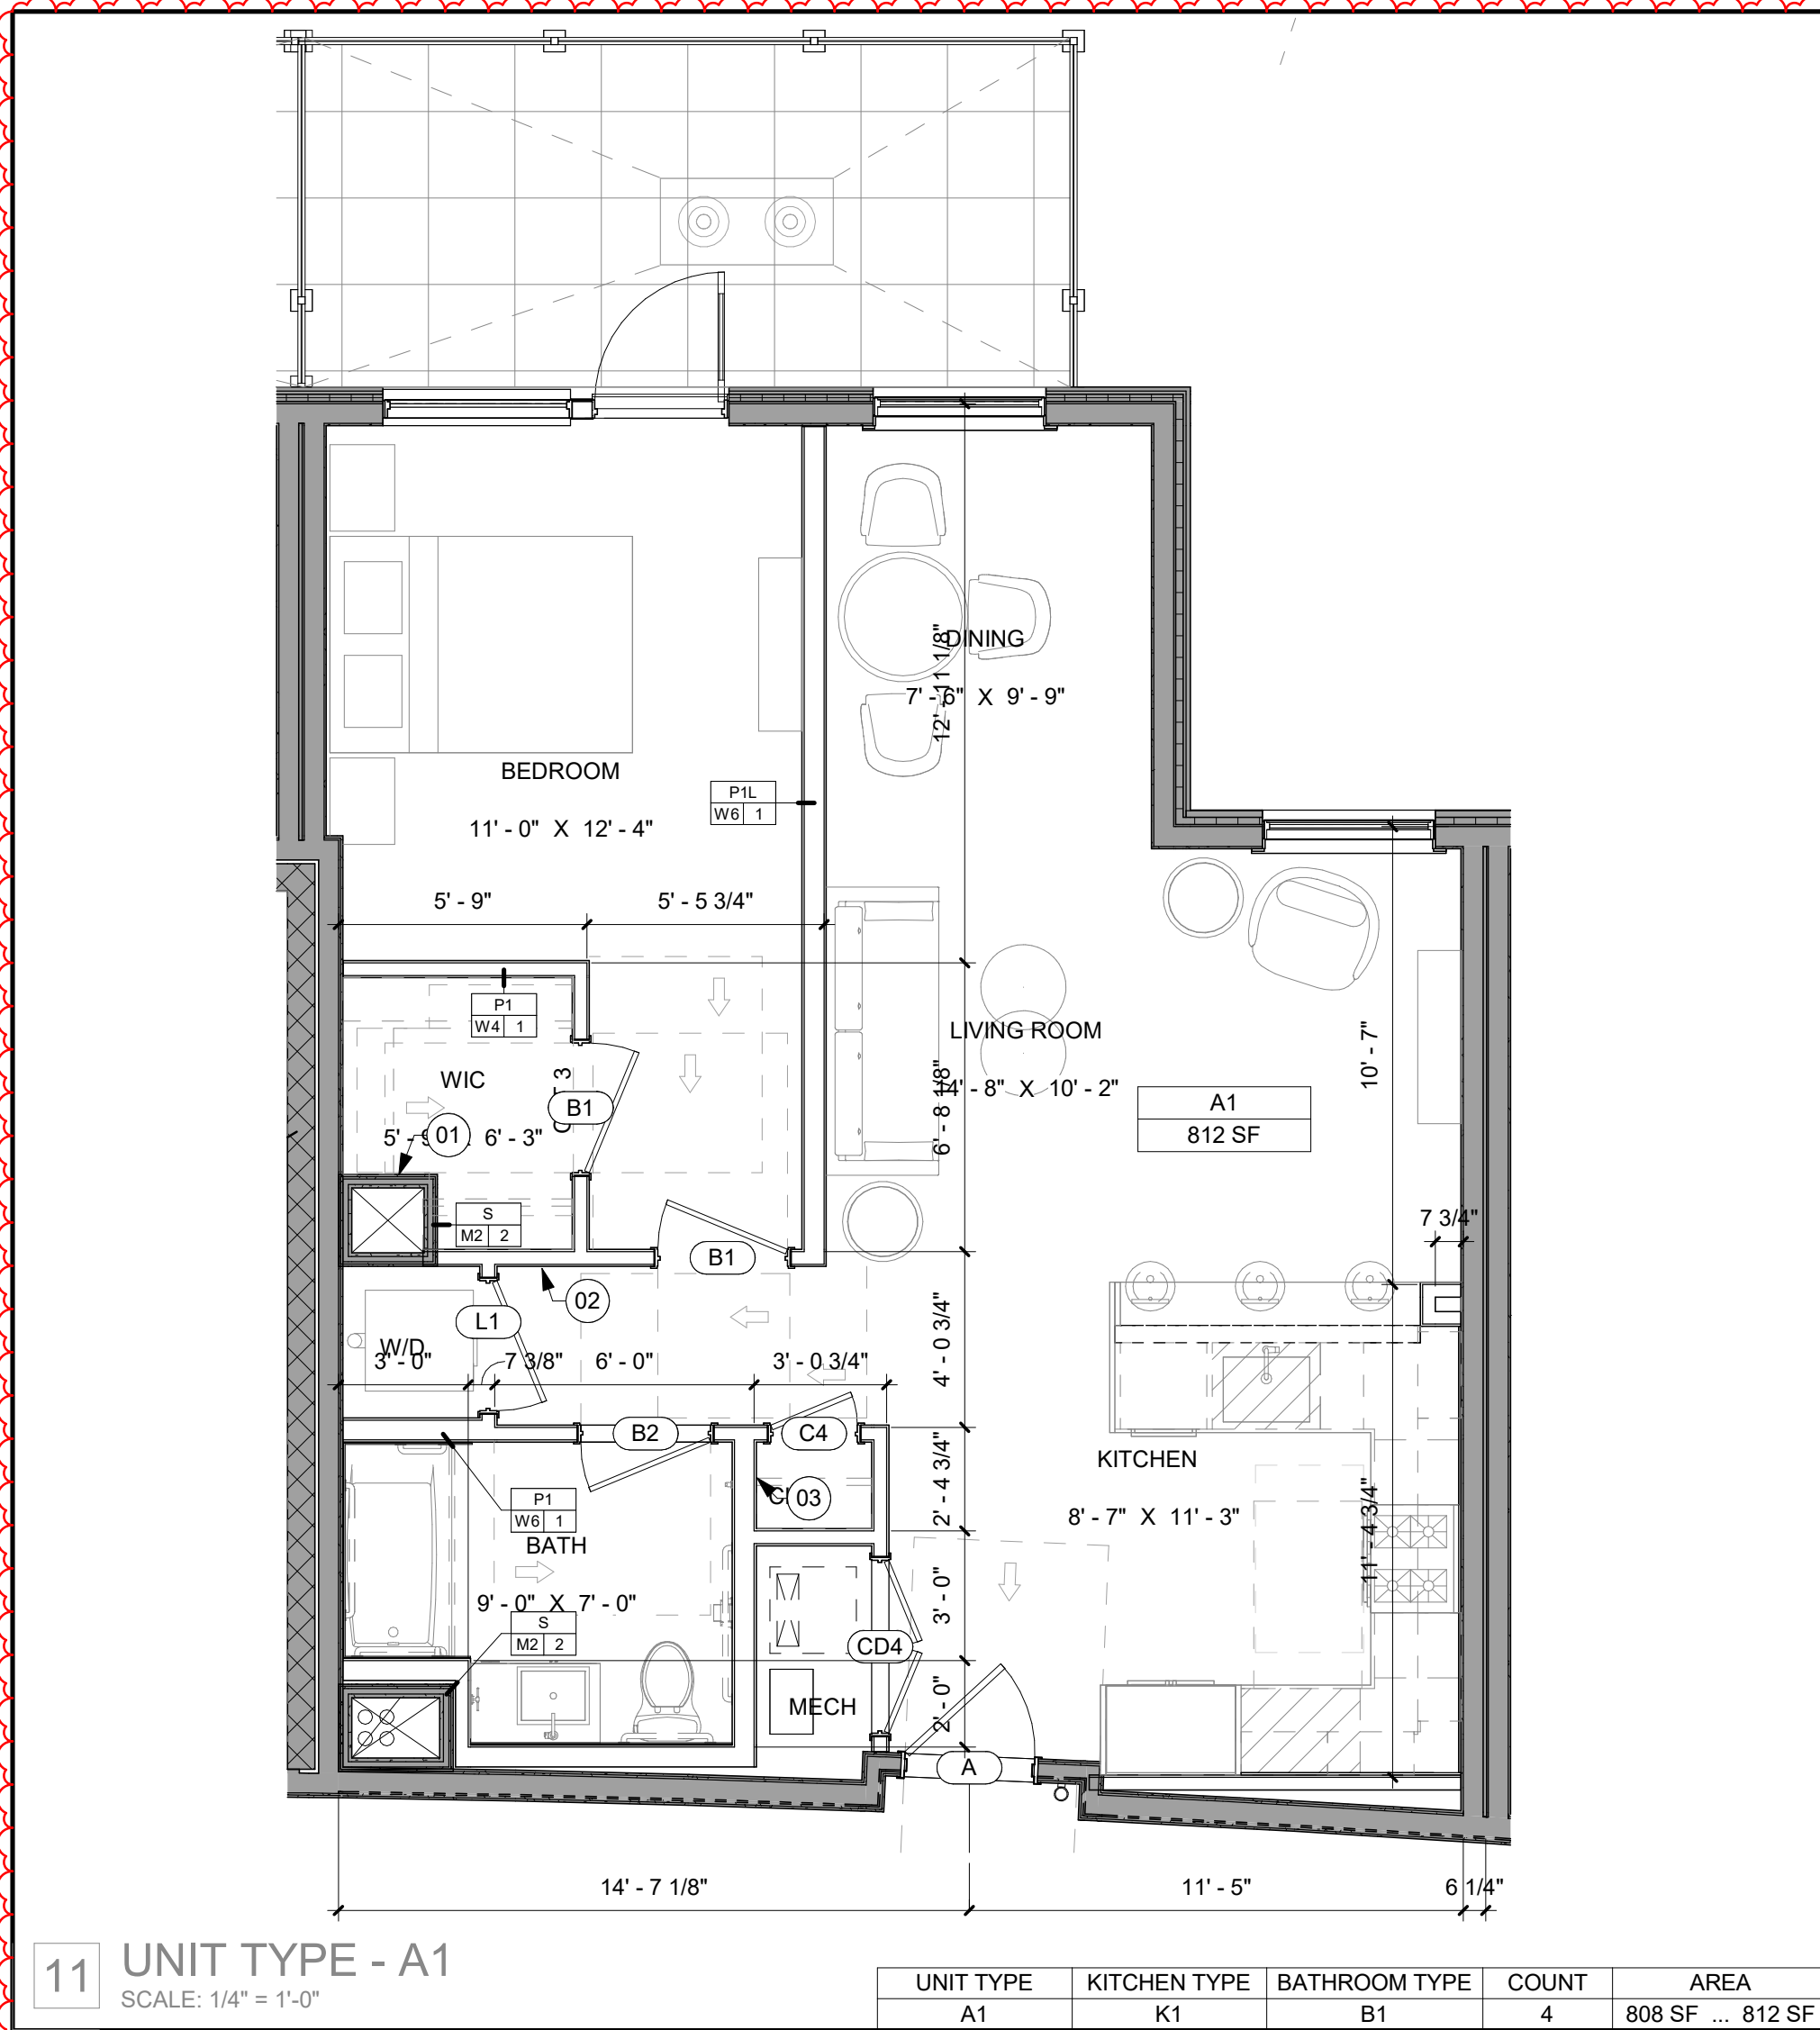

- UNIT PLAN NOTES
- ALL INTERIOR DIMENSIONS TO WOOD FRAME PARTITIONS ARE TO FACE OF FRAMING. ALL INTERIOR DIMENSIONS TO METAL FRAME PARTITIONS ARE TO FACE OF FINISH AND ARE NOTED WITH ASTERISKS "X.X". ALL OTHER DIMENSIONS ARE AS SHOWN.
 - ALL UNIT INTERIOR PARTITIONS TO BE WALL TYPE XX UNLESS OTHERWISE NOTED.
 - LOCATE DOOR OPENINGS 4" FROM ADJACENT WALL UNLESS OTHERWISE NOTED.
 - SEE MECHANICAL AND PLUMBING DRAWINGS FOR EQUIPMENT SPECIFICATIONS.
 - SEE ELECTRICAL AND LOW VOLTAGE DRAWINGS FOR POWER AND LOW VOLTAGE PLANS.

KEYNOTES

#	DESCRIPTION
01	MECH. CHASE REF. MEP DRAWINGS
02	ELECTRICAL LOAD CENTER. REFER TO ELEC. DRAWINGS
03	IND. BOX REF. TO ELEC. FOR MORE INFO
04	WALL RETURN REF. TO ELEC. DRAWINGS

Dean Marchetto, FAIA, PP
NJ 07045
Michael Higgins, AIA, LEED
NJ21A0130830
Bruce A. Shreve, AIA
NJ21A0137710
Michael Buldo, AIA
NJ21A01708300
NY 03561
Vincent Marchetto, AIA
NJ21A02151000

MHS ARCHITECTURE

1422 Grand Street
Suite 5b
Hoboken, NJ 07030
T.201-795-1505
MHSArchitecture.com

PROJECT NAME:
MORRISTOWN GREEN APARTMENTS
22 LAFAYETTE AVENUE
TOWN OF MORRISTOWN, NEW JERSEY

PREPARED FOR:
MORRISTOWN ASSOCIATES LLC
4 CUNNINGHAM DRIVE
WEST ORANGE, NJ

ISSUE

#	DATE	FOR:
1	06/03/2026	BID SET
1	07/09/26	ADDENDUM #1

ENLARGED UNIT PLANS - 1 BR

PROJECT NUMBER: 2202
SCALE: As indicated
DRAWN BY: CM / TM / JE
CHECKED BY: FT / MB