



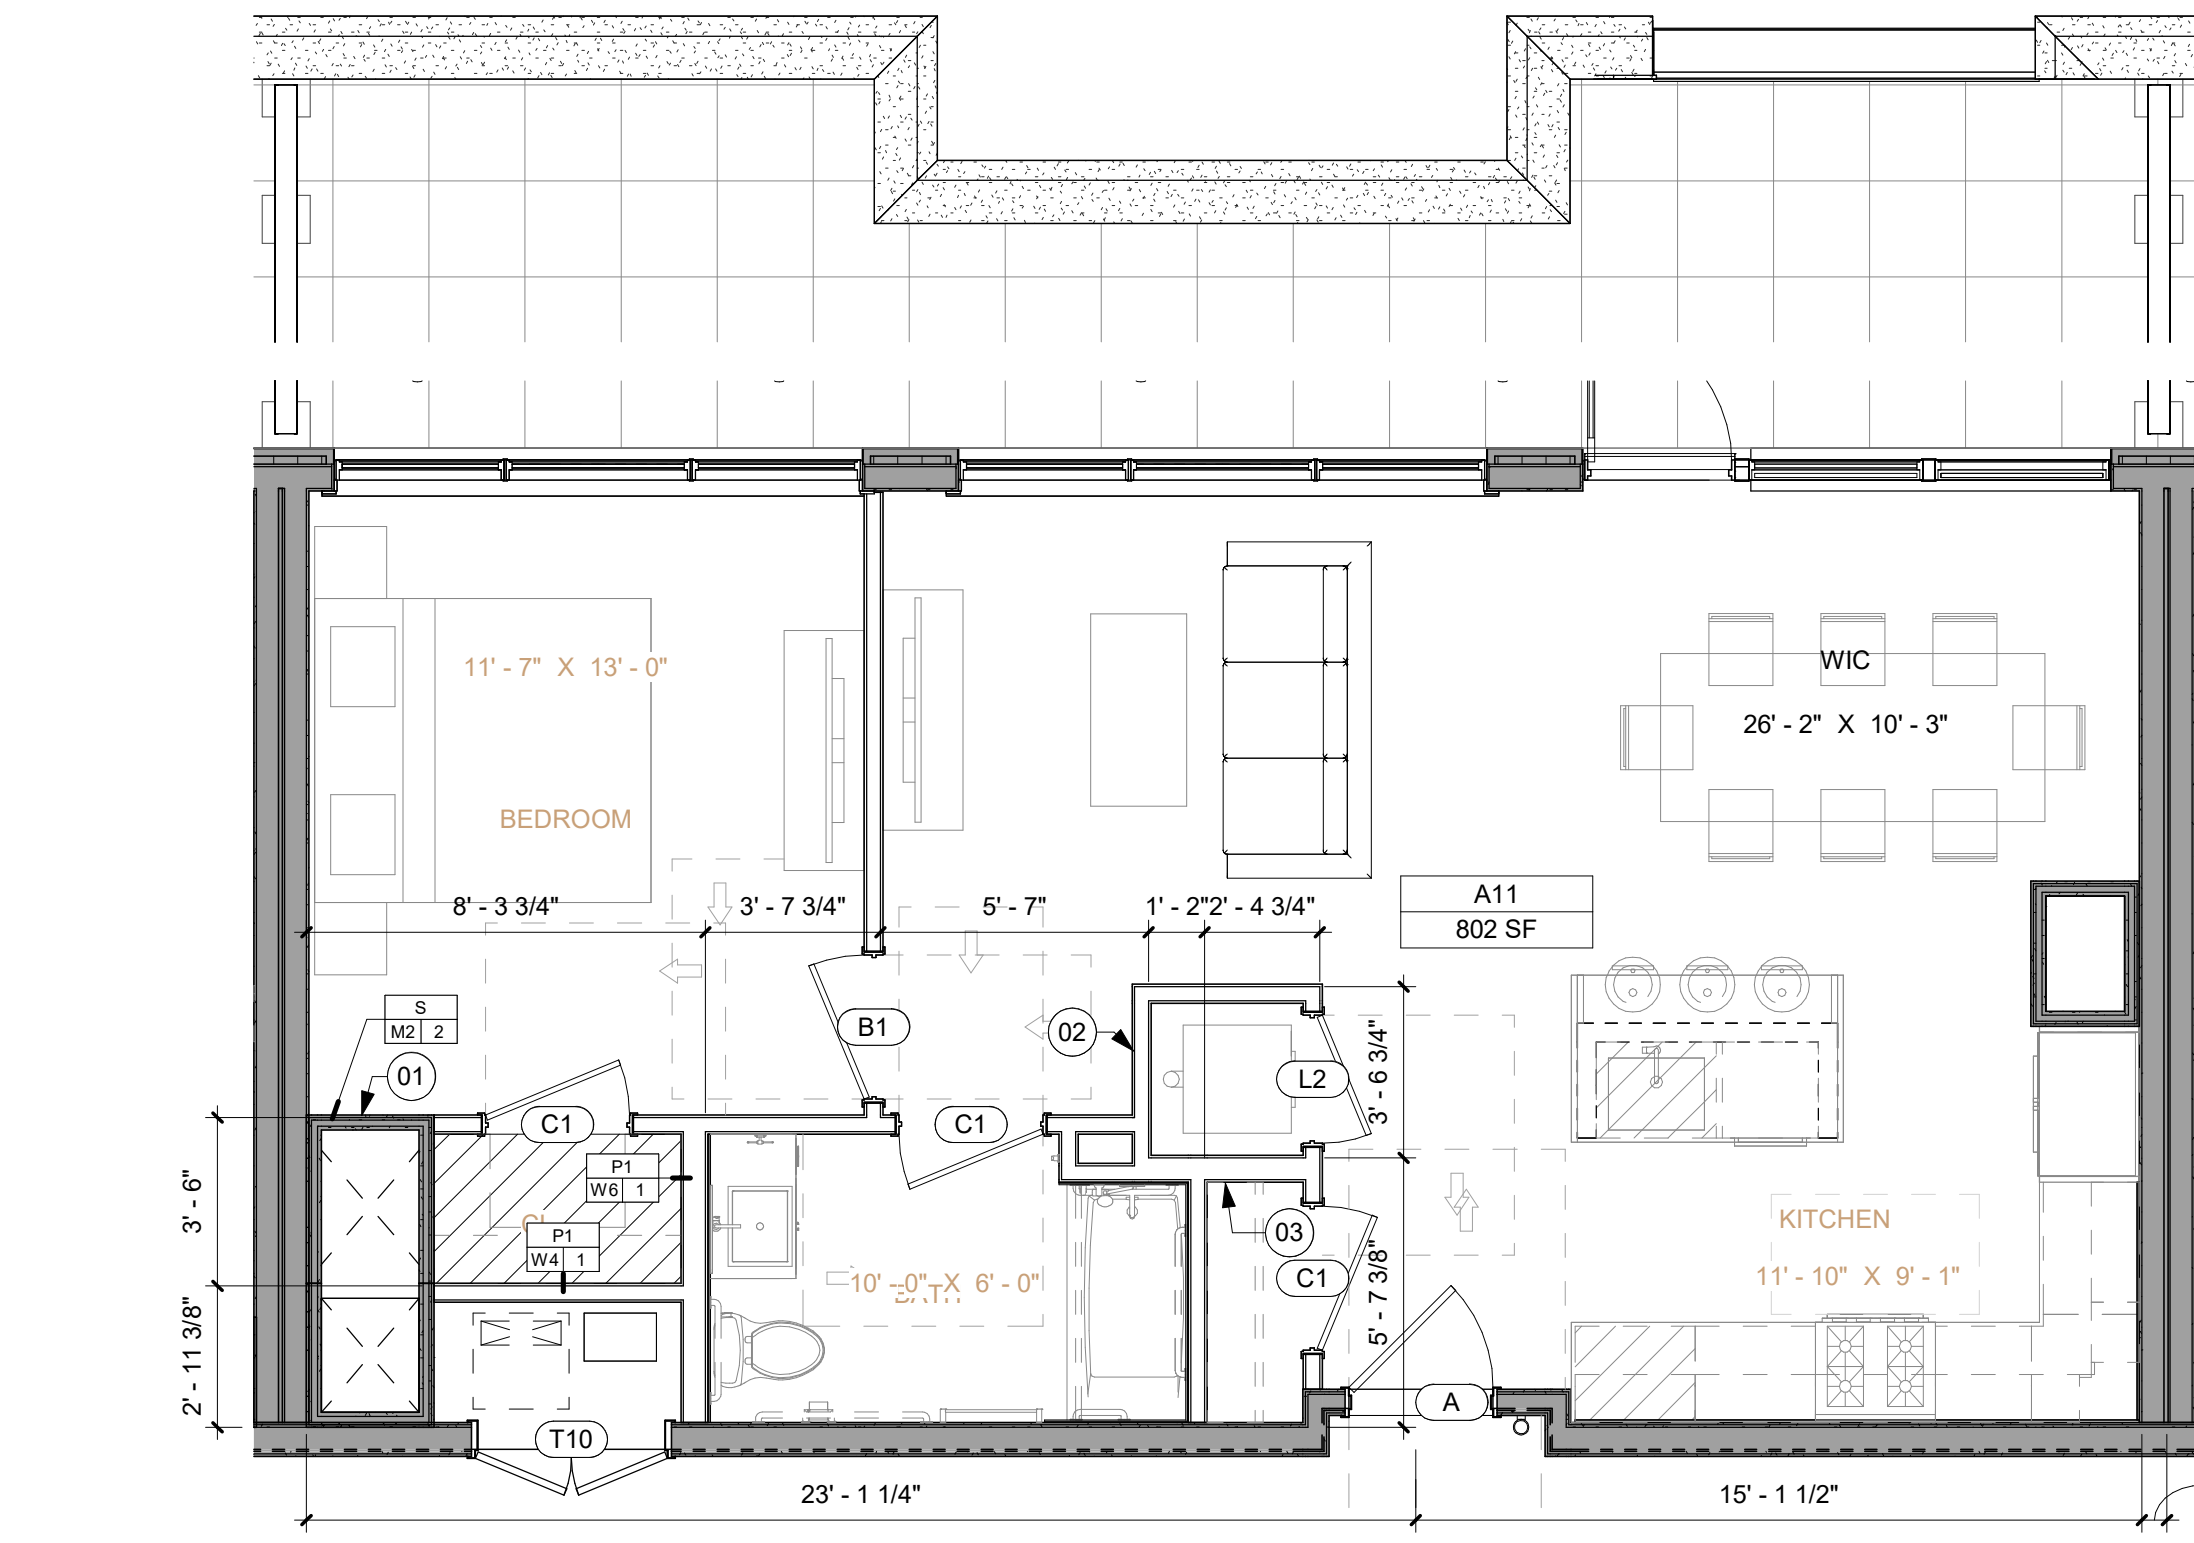


11 UNIT TYPE - A11
SCALE: 1/4" = 1'-0"

UNIT TYPE	KITCHEN TYPE	BATHROOM TYPE	COUNT	AREA
A11	K2	B2	1	802 SF

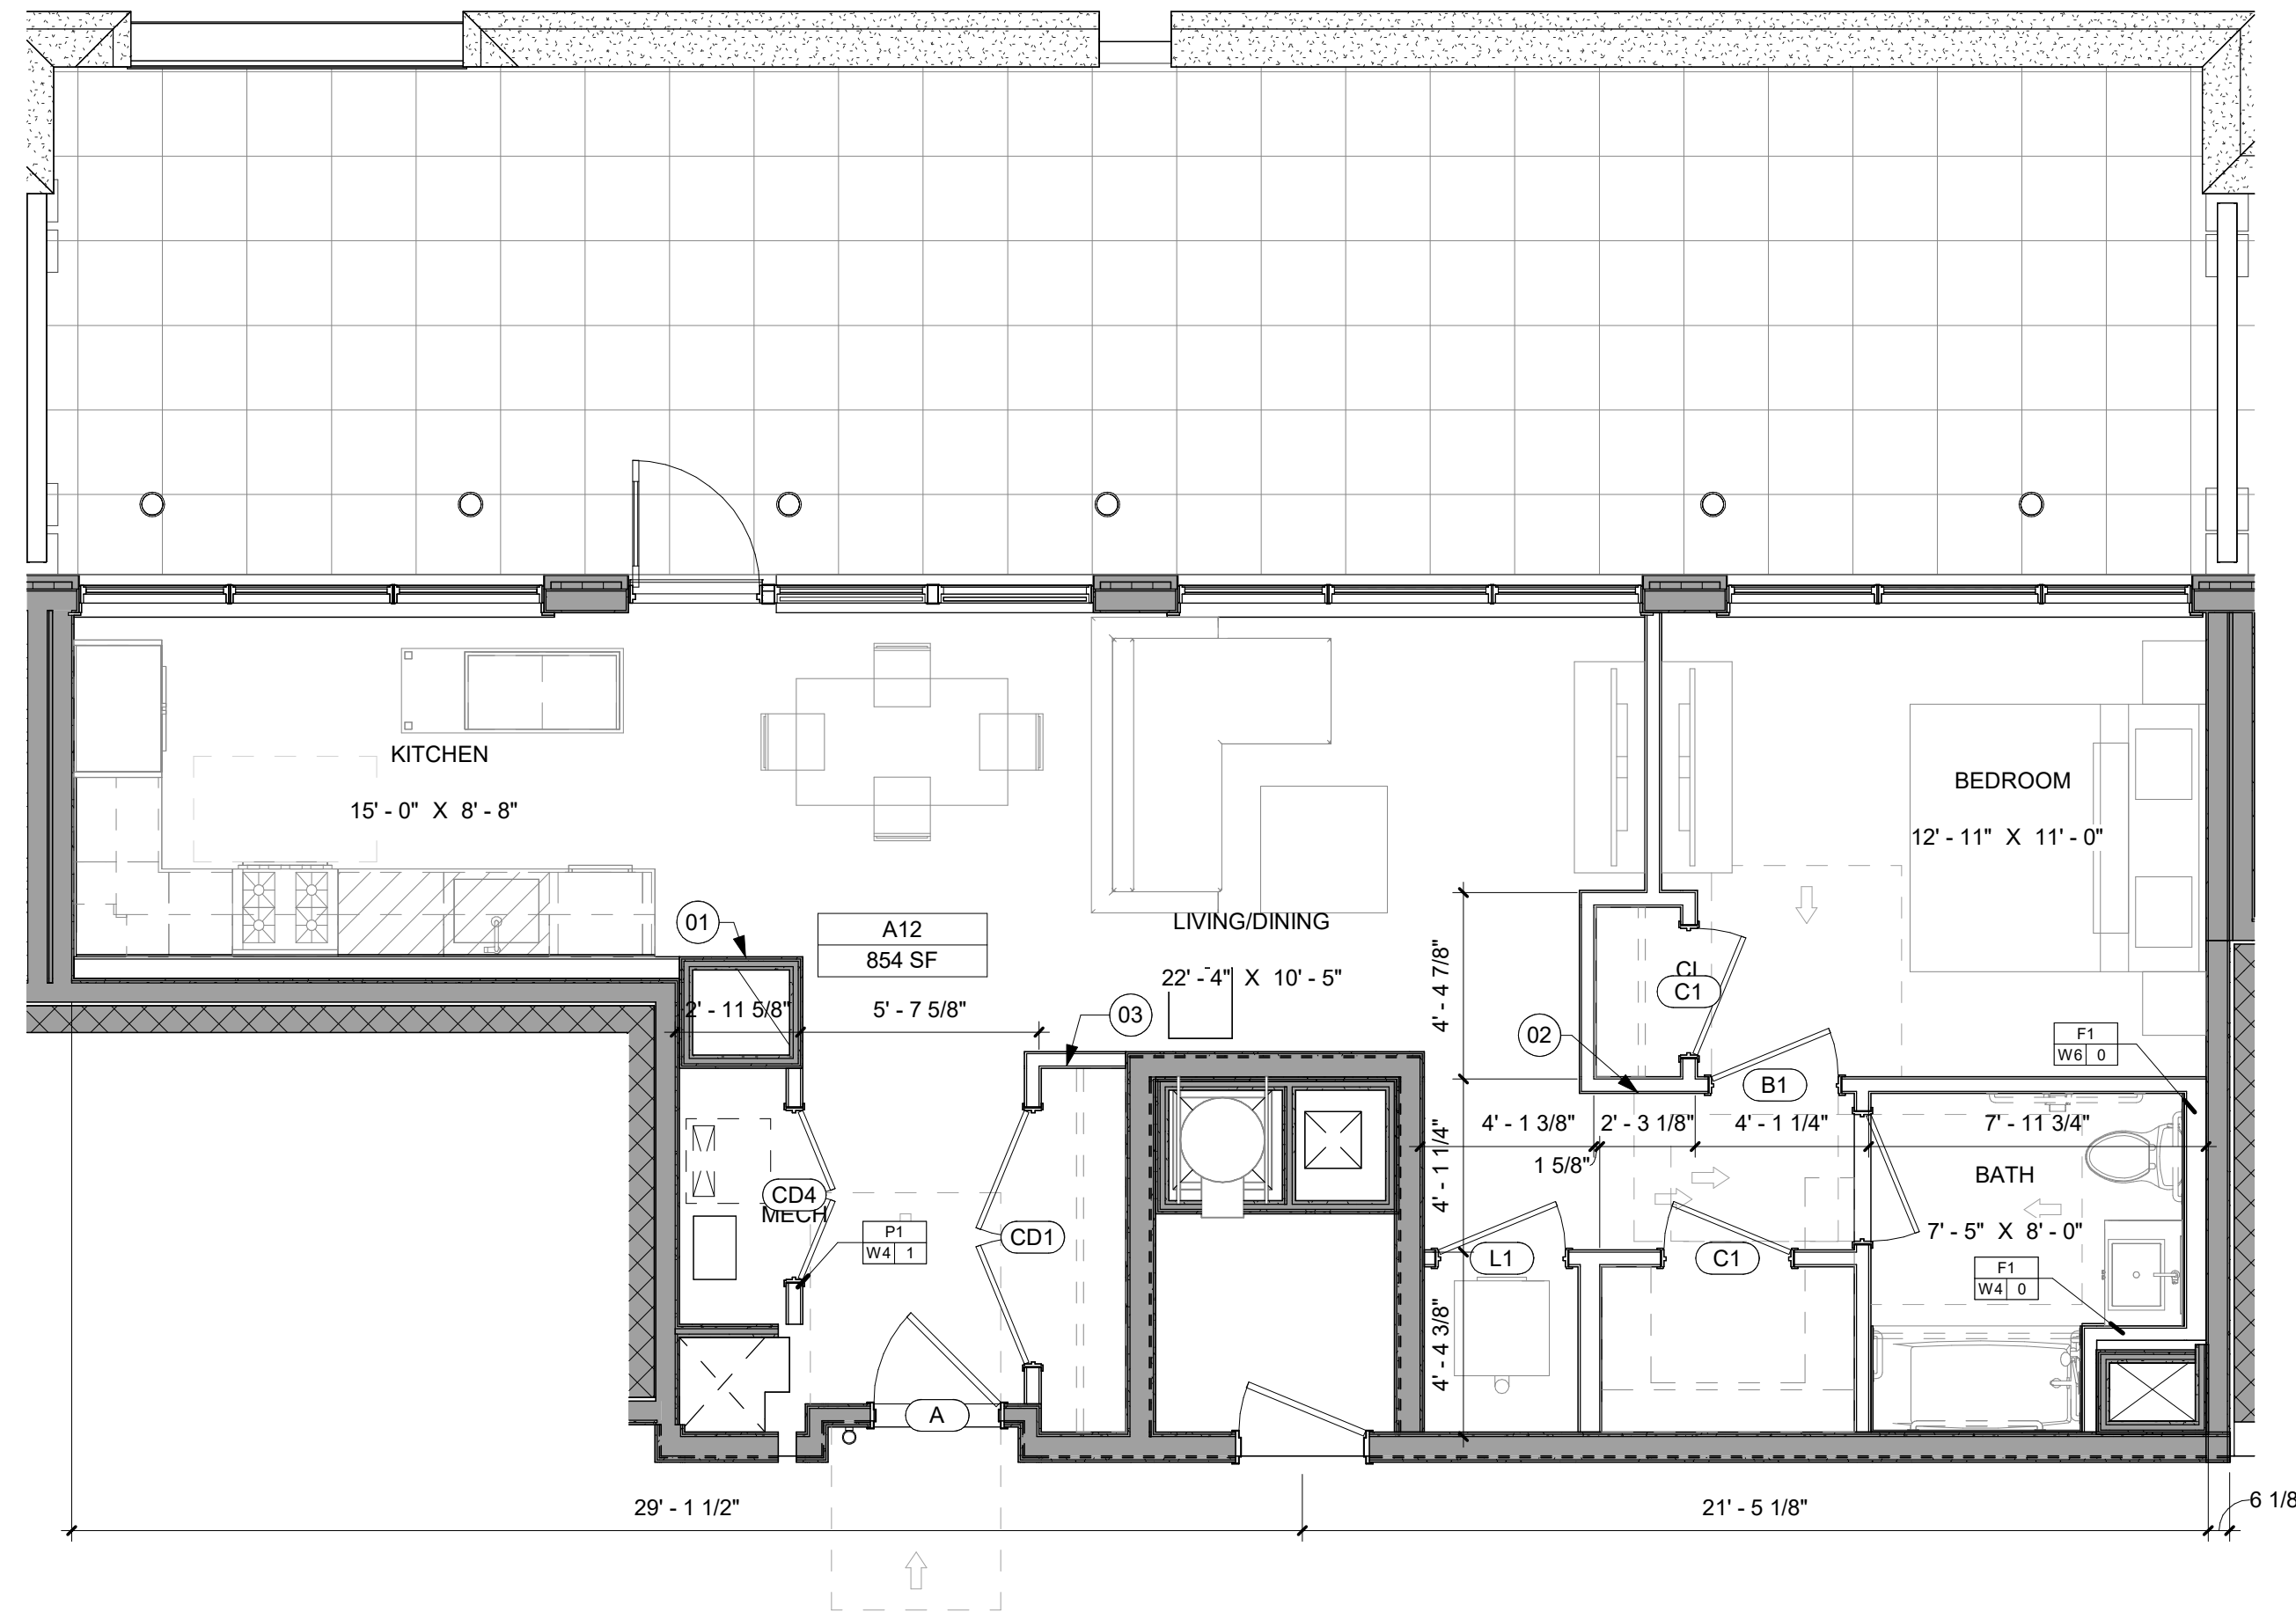


10 UNIT TYPE - A12
SCALE: 1/4" = 1'-0"

UNIT TYPE	KITCHEN TYPE	BATHROOM TYPE	COUNT	AREA
A12	K3	B3	1	854 SF

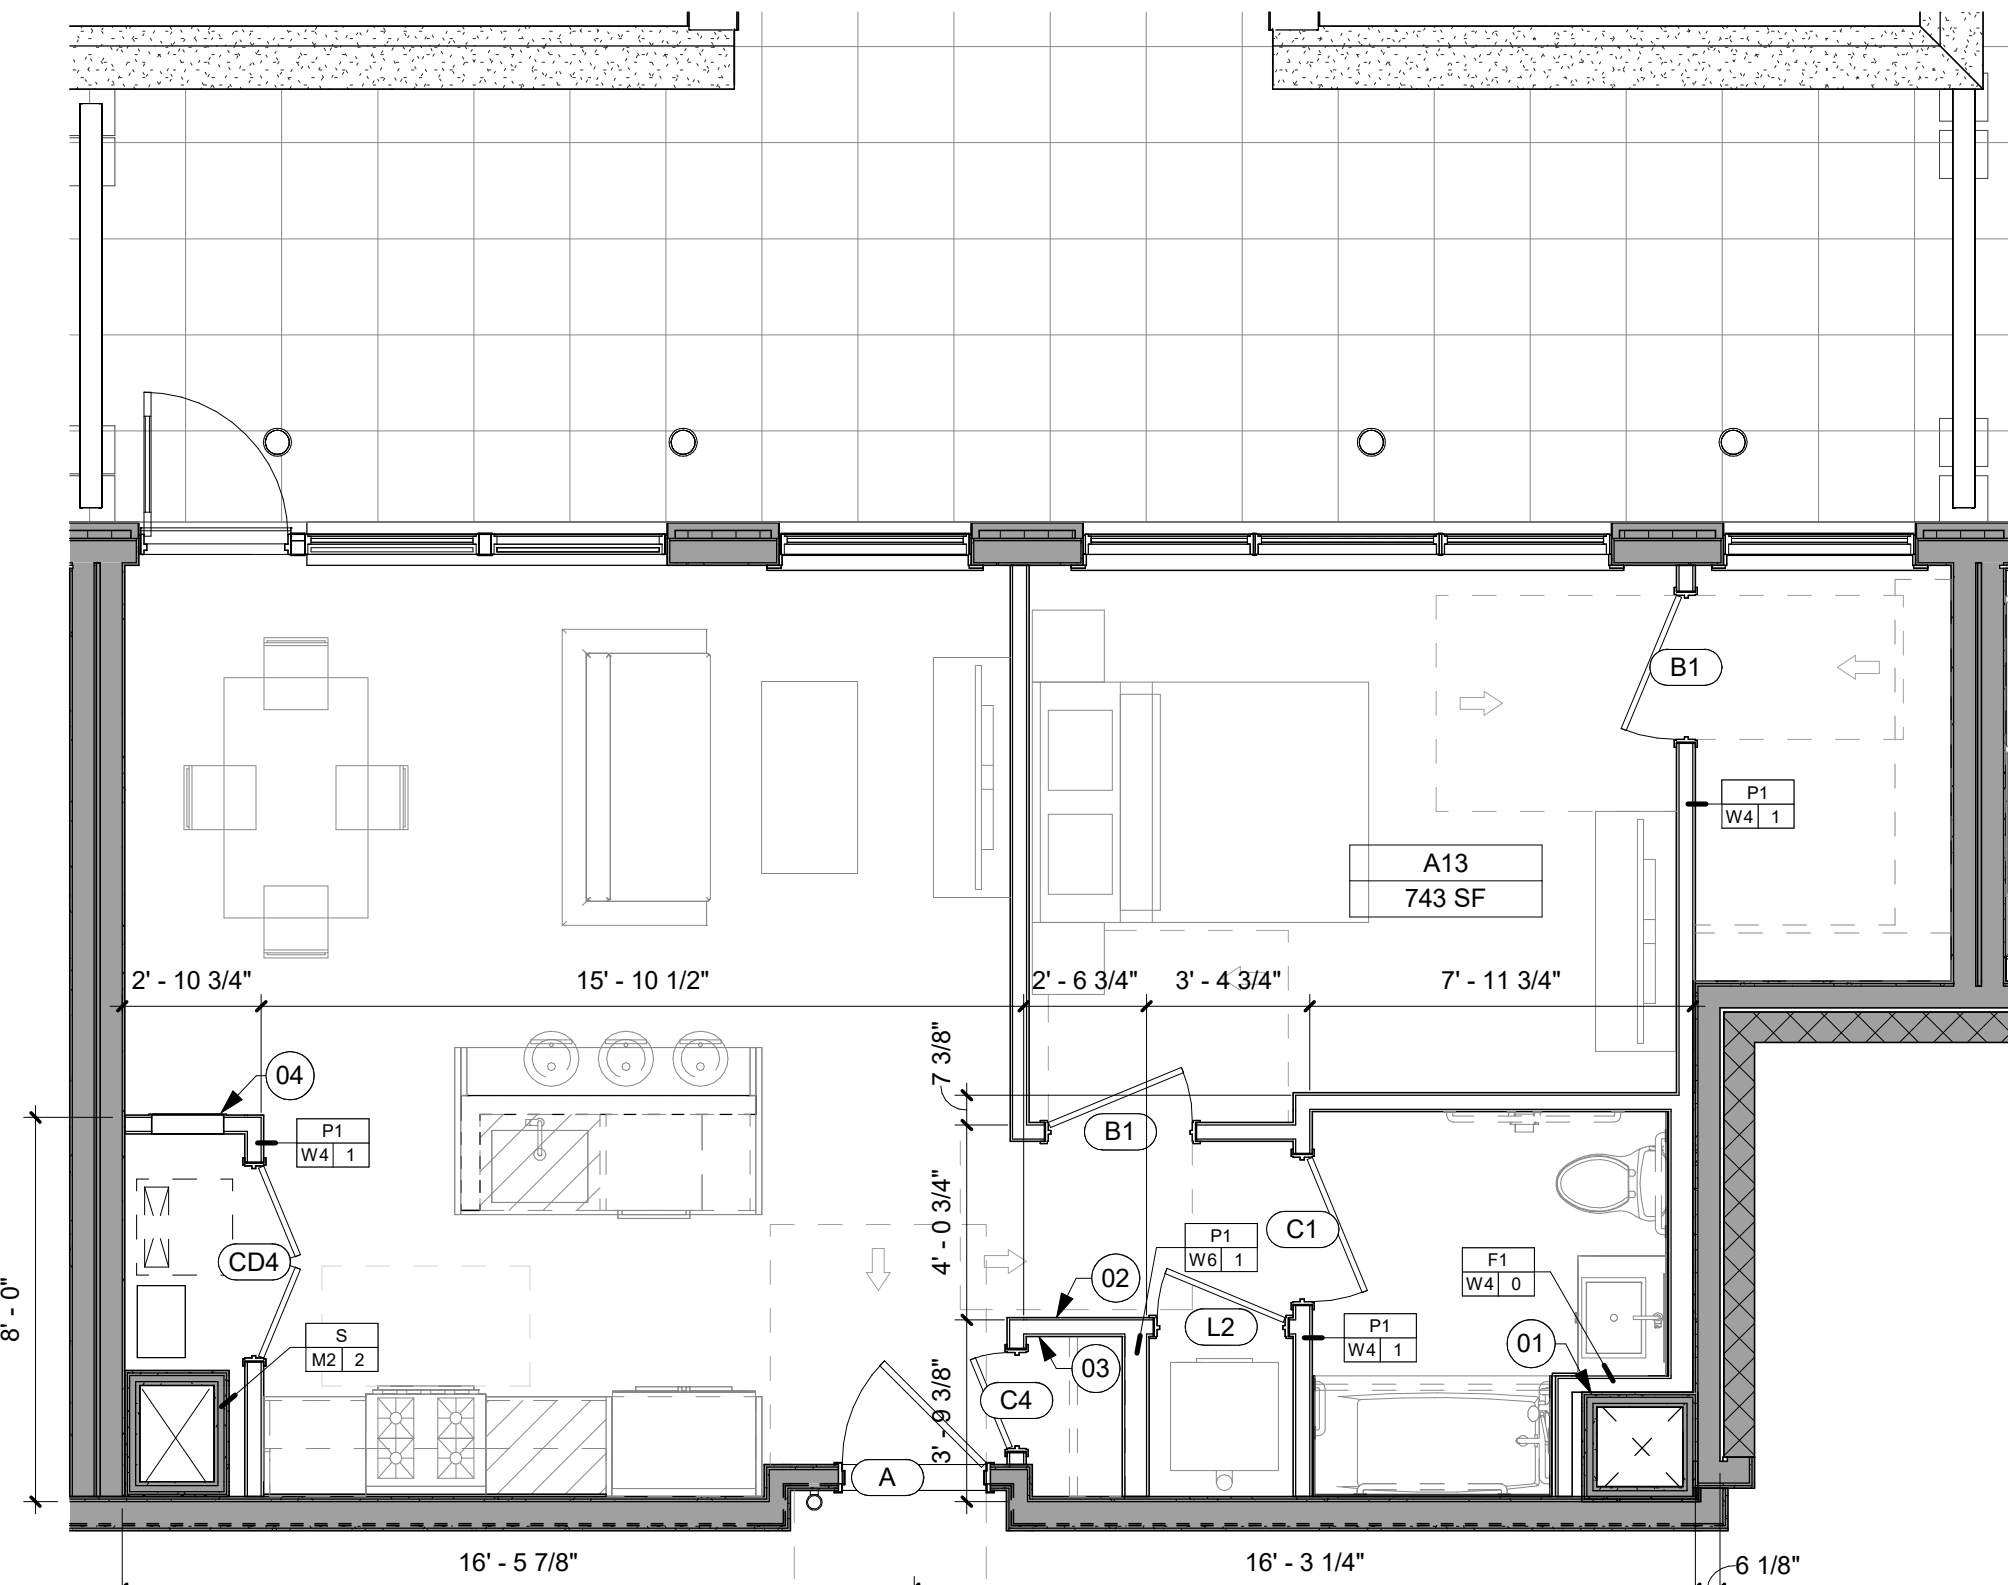


9 UNIT TYPE - A13
SCALE: 1/4" = 1'-0"

UNIT TYPE	KITCHEN TYPE	BATHROOM TYPE	COUNT	AREA
A13	K3	B3	1	743 SF

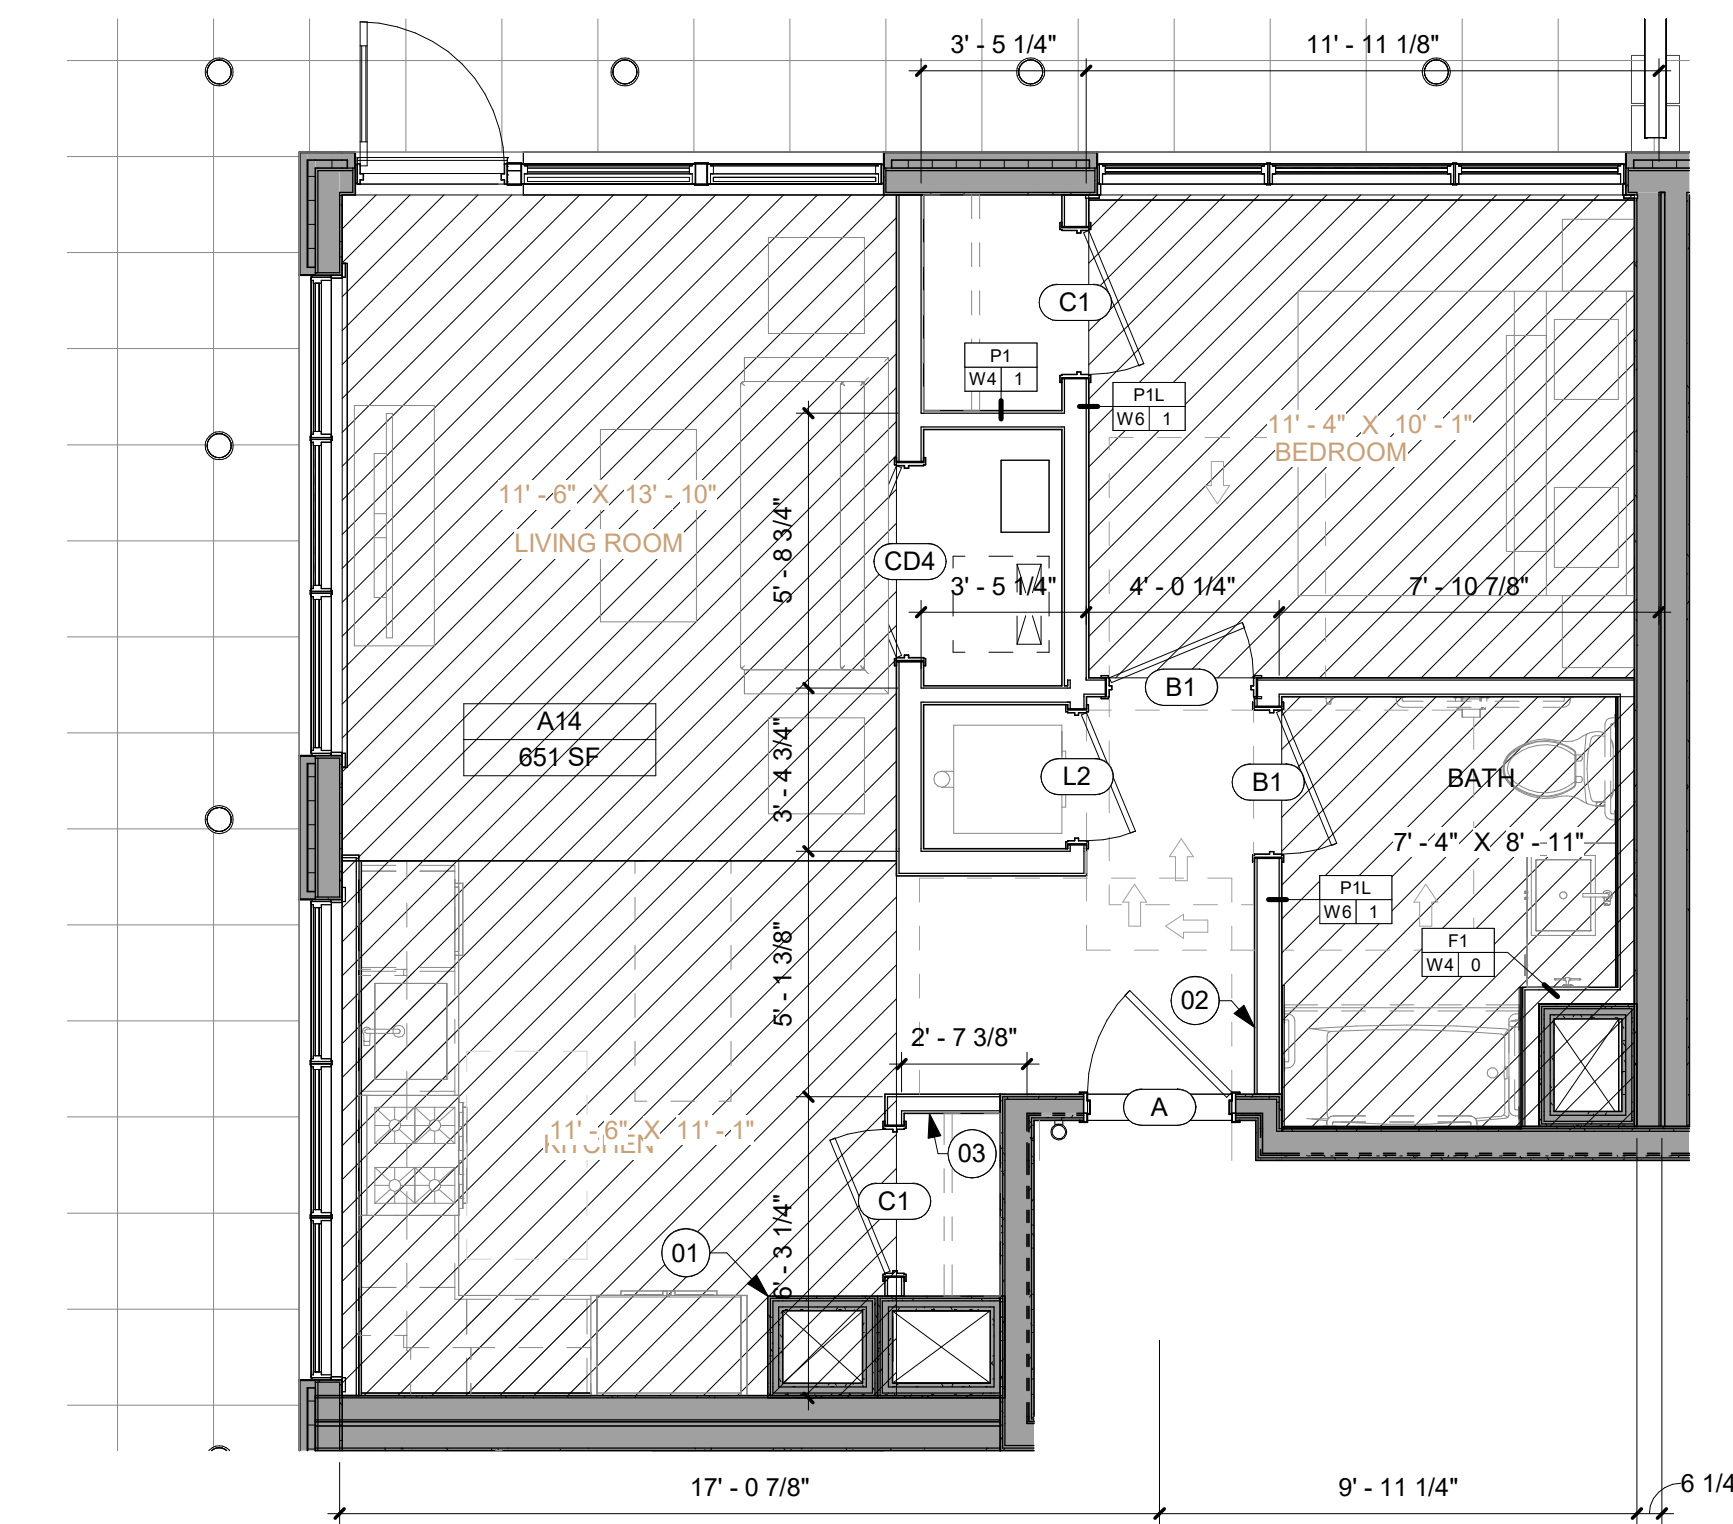


8 UNIT TYPE - A14
SCALE: 1/4" = 1'-0"

UNIT TYPE	KITCHEN TYPE	BATHROOM TYPE	COUNT	AREA
A14	K4	B1	1	651 SF

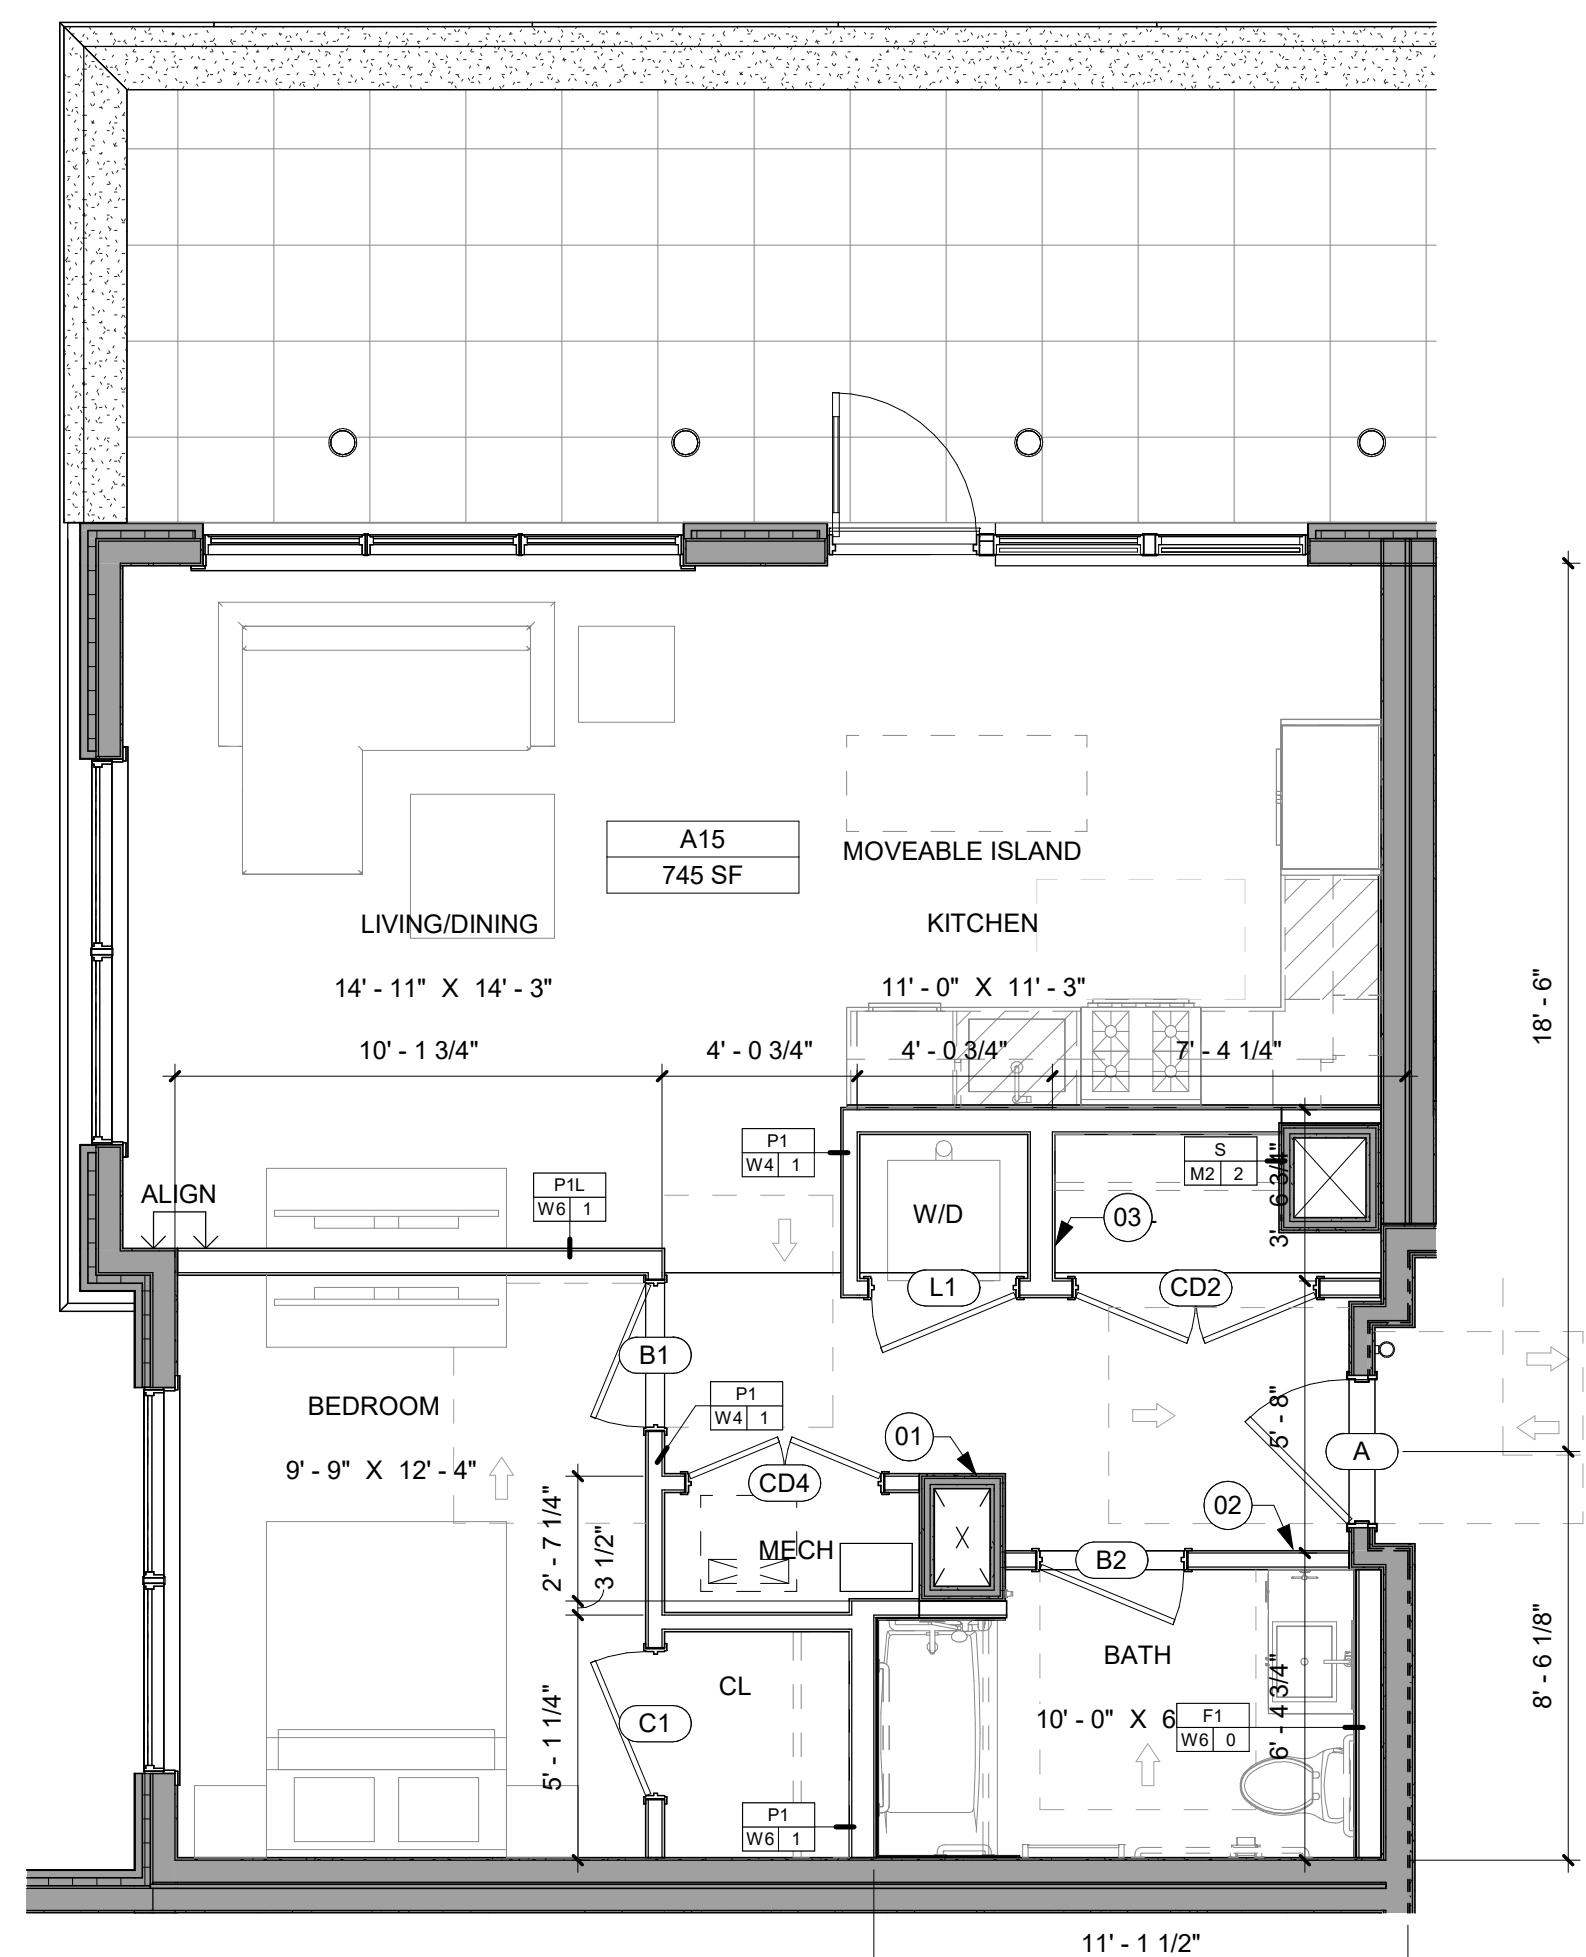


7 UNIT TYPE - A15
SCALE: 1/4" = 1'-0"

UNIT TYPE	KITCHEN TYPE	BATHROOM TYPE	COUNT	AREA
A15	K4	B2	1	745 SF

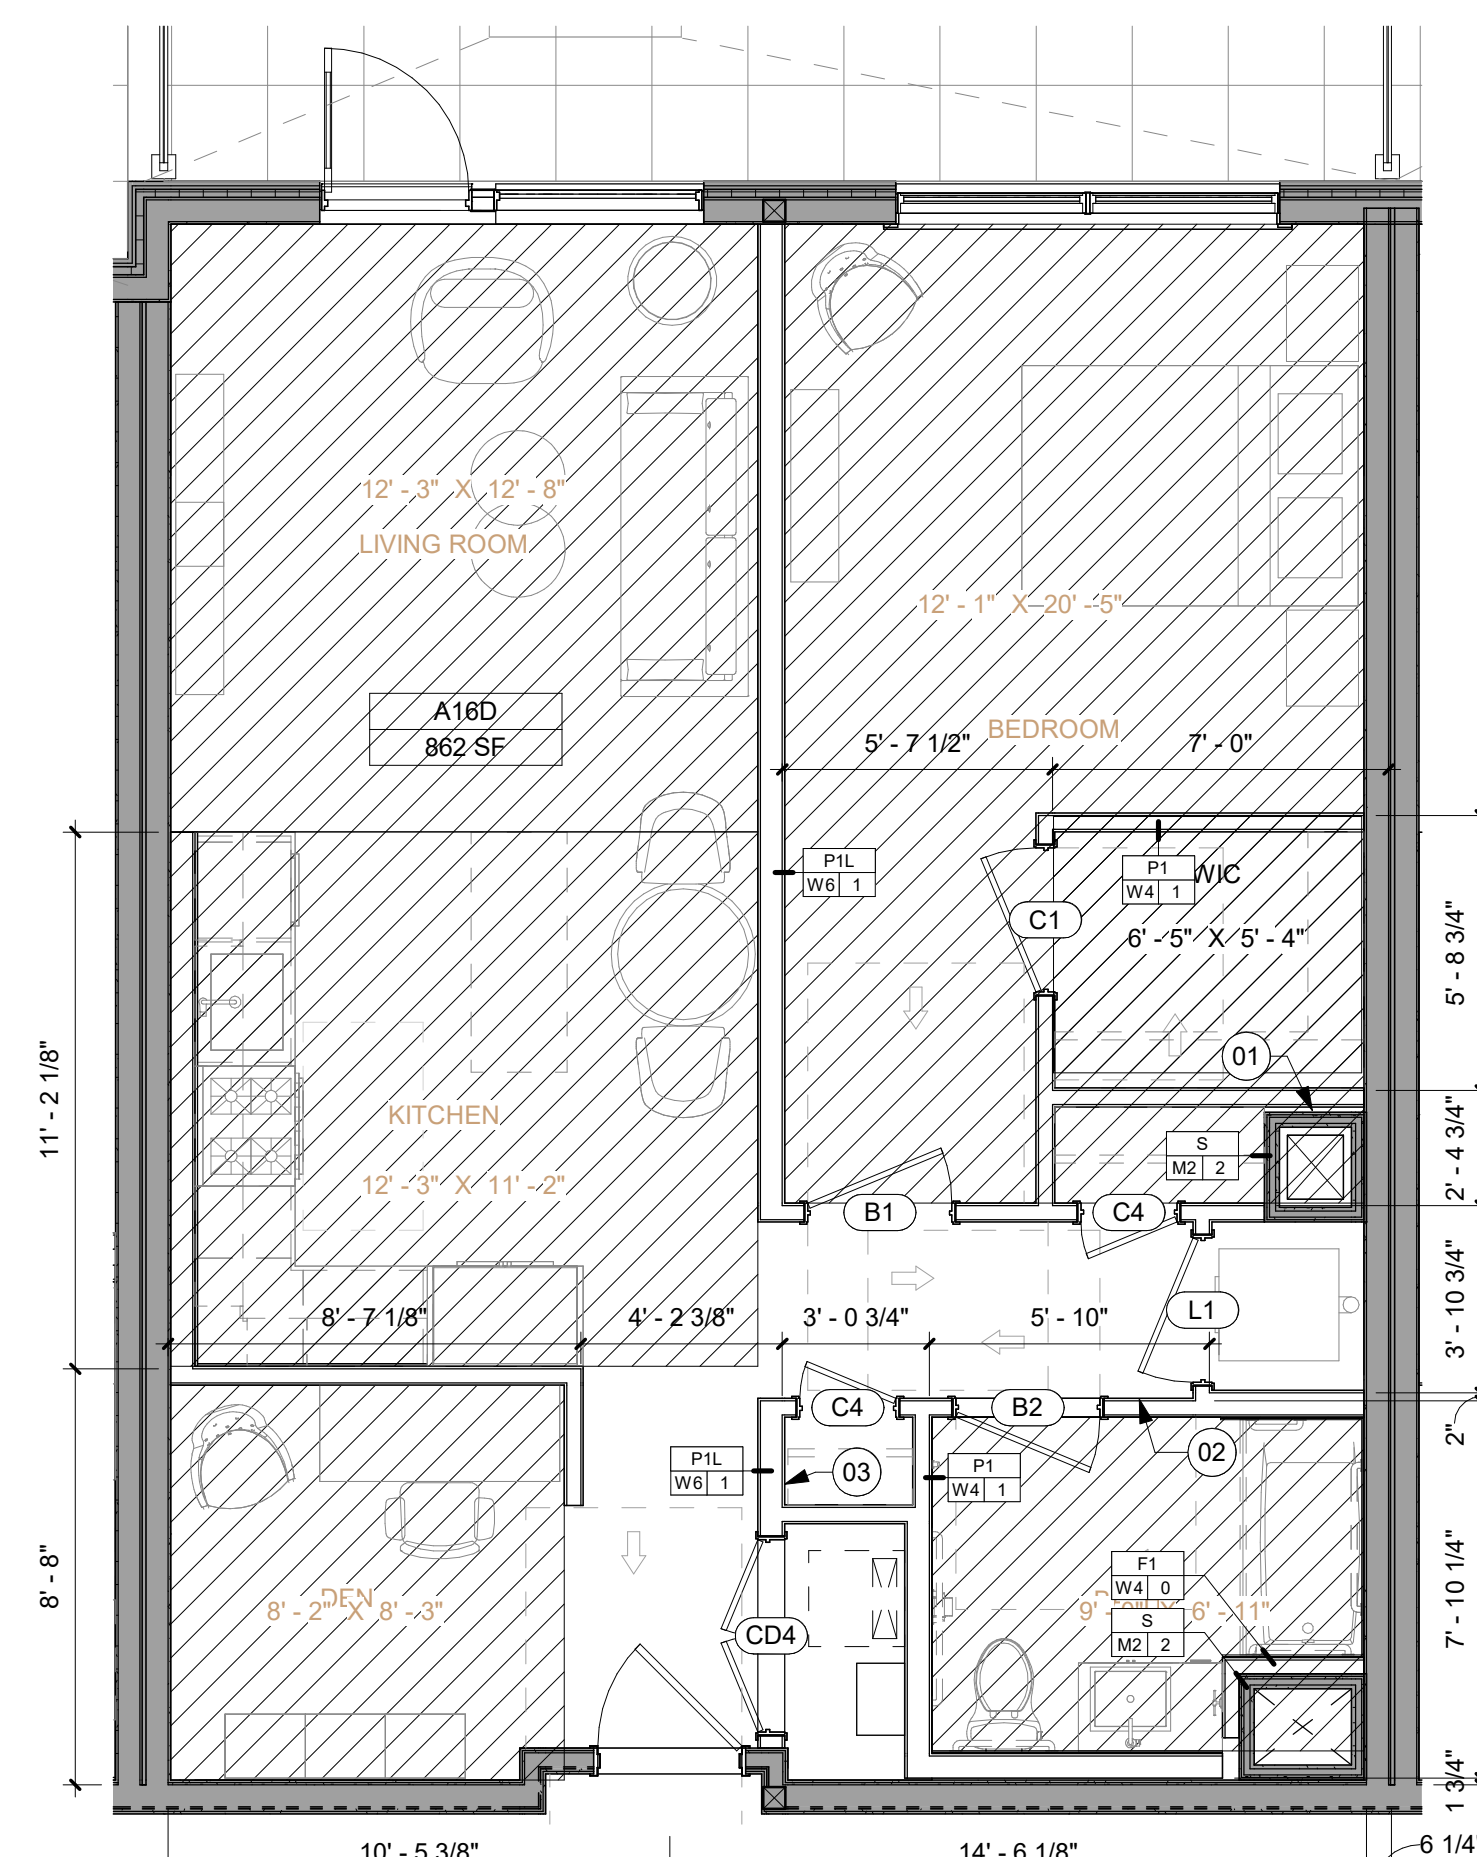


6 UNIT TYPE - A16D
SCALE: 1/4" = 1'-0"

UNIT TYPE	KITCHEN TYPE	BATHROOM TYPE	COUNT	AREA
A16D	K4	B1	18	859 SF - 870 SF

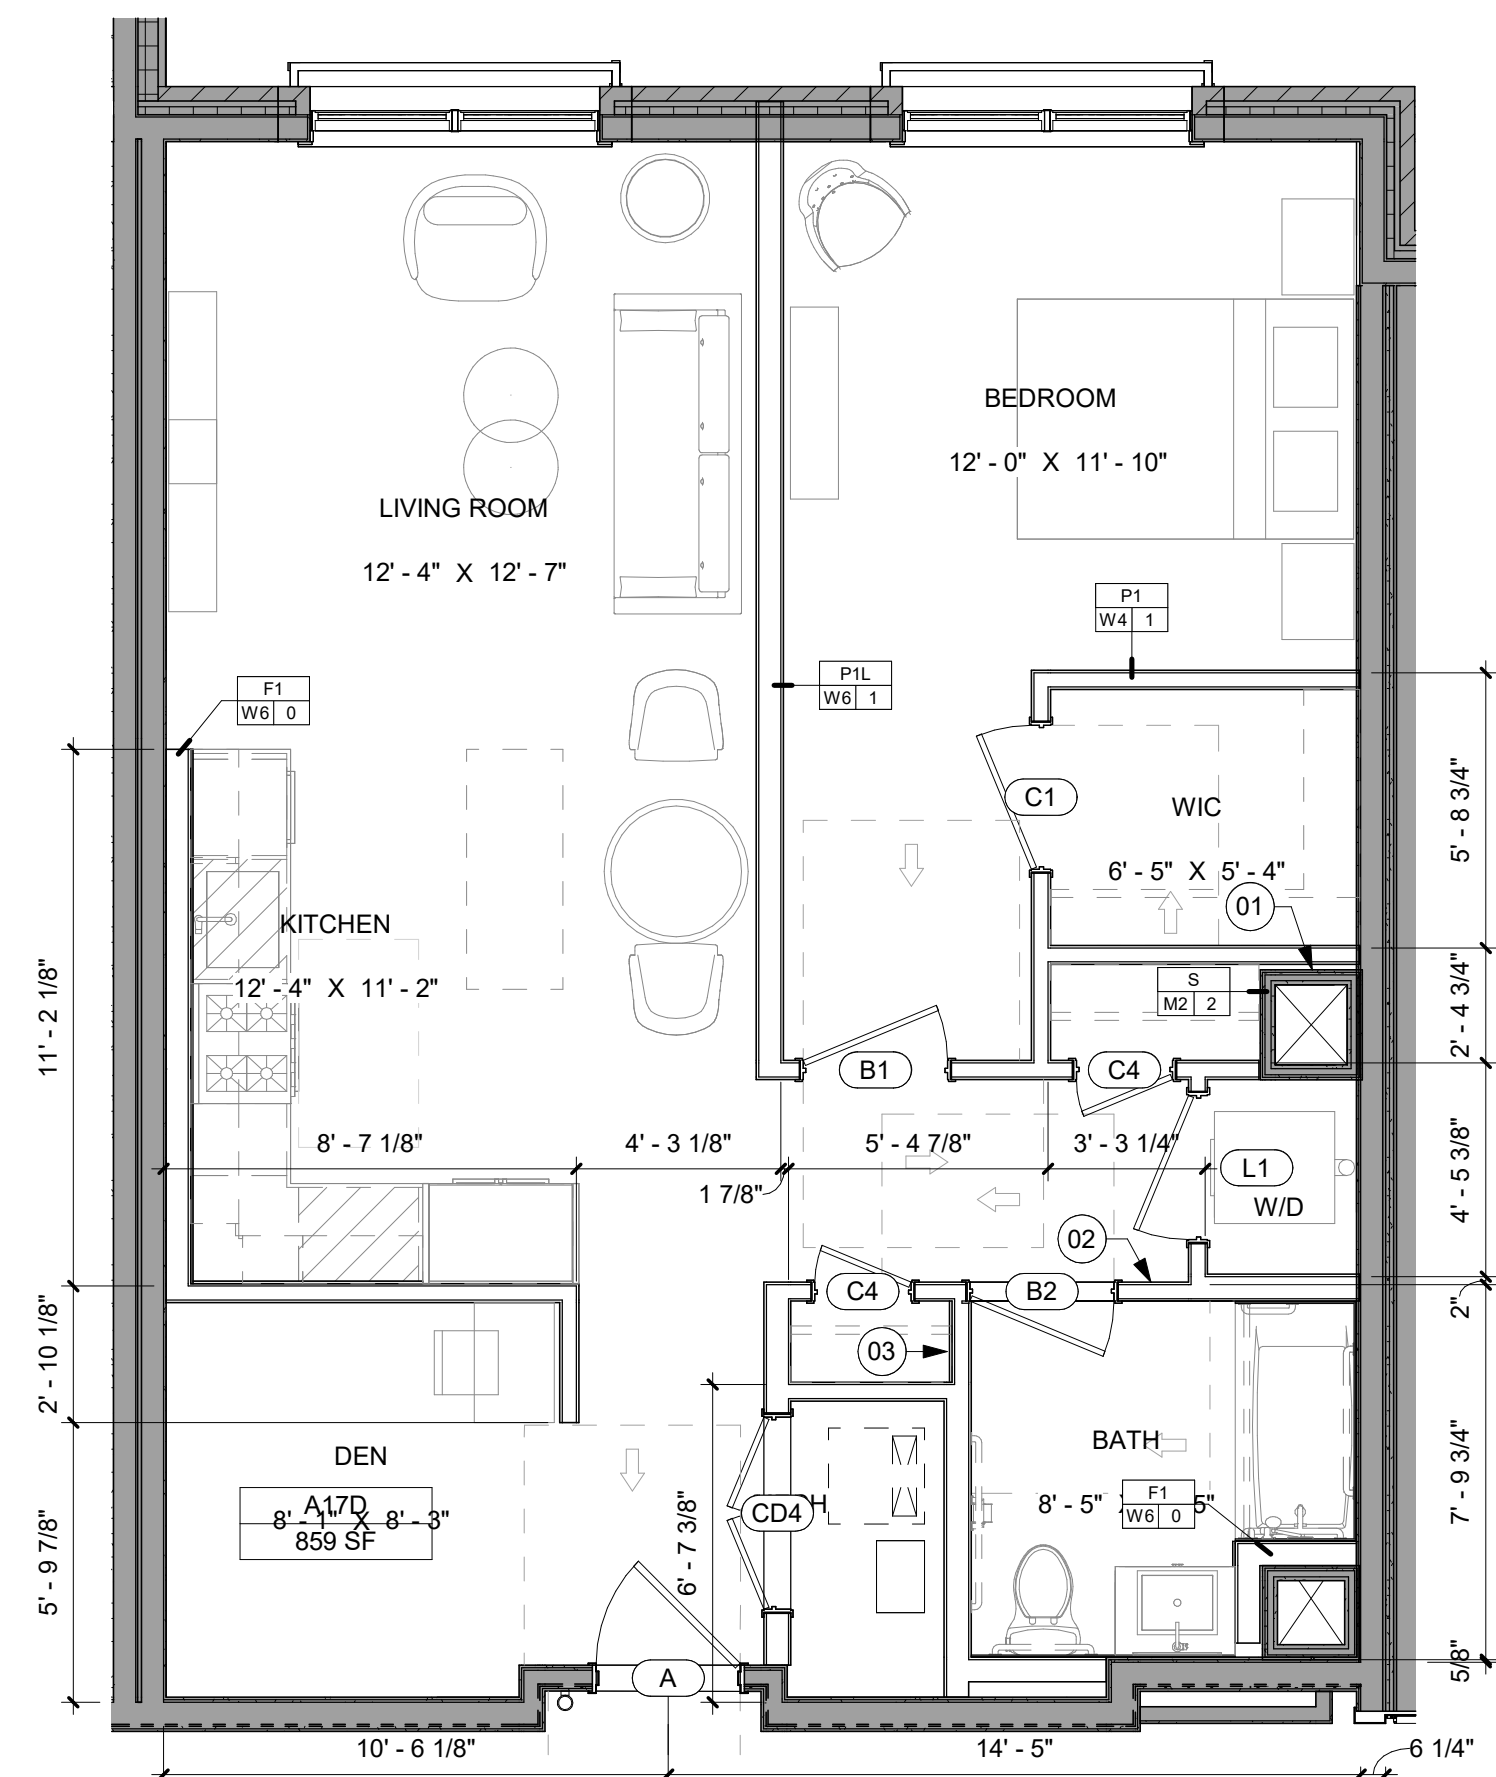


5 UNIT TYPE - A17D
SCALE: 1/4" = 1'-0"

UNIT TYPE	KITCHEN TYPE	BATHROOM TYPE	COUNT	AREA
A17D	K4	B3	3	859 SF

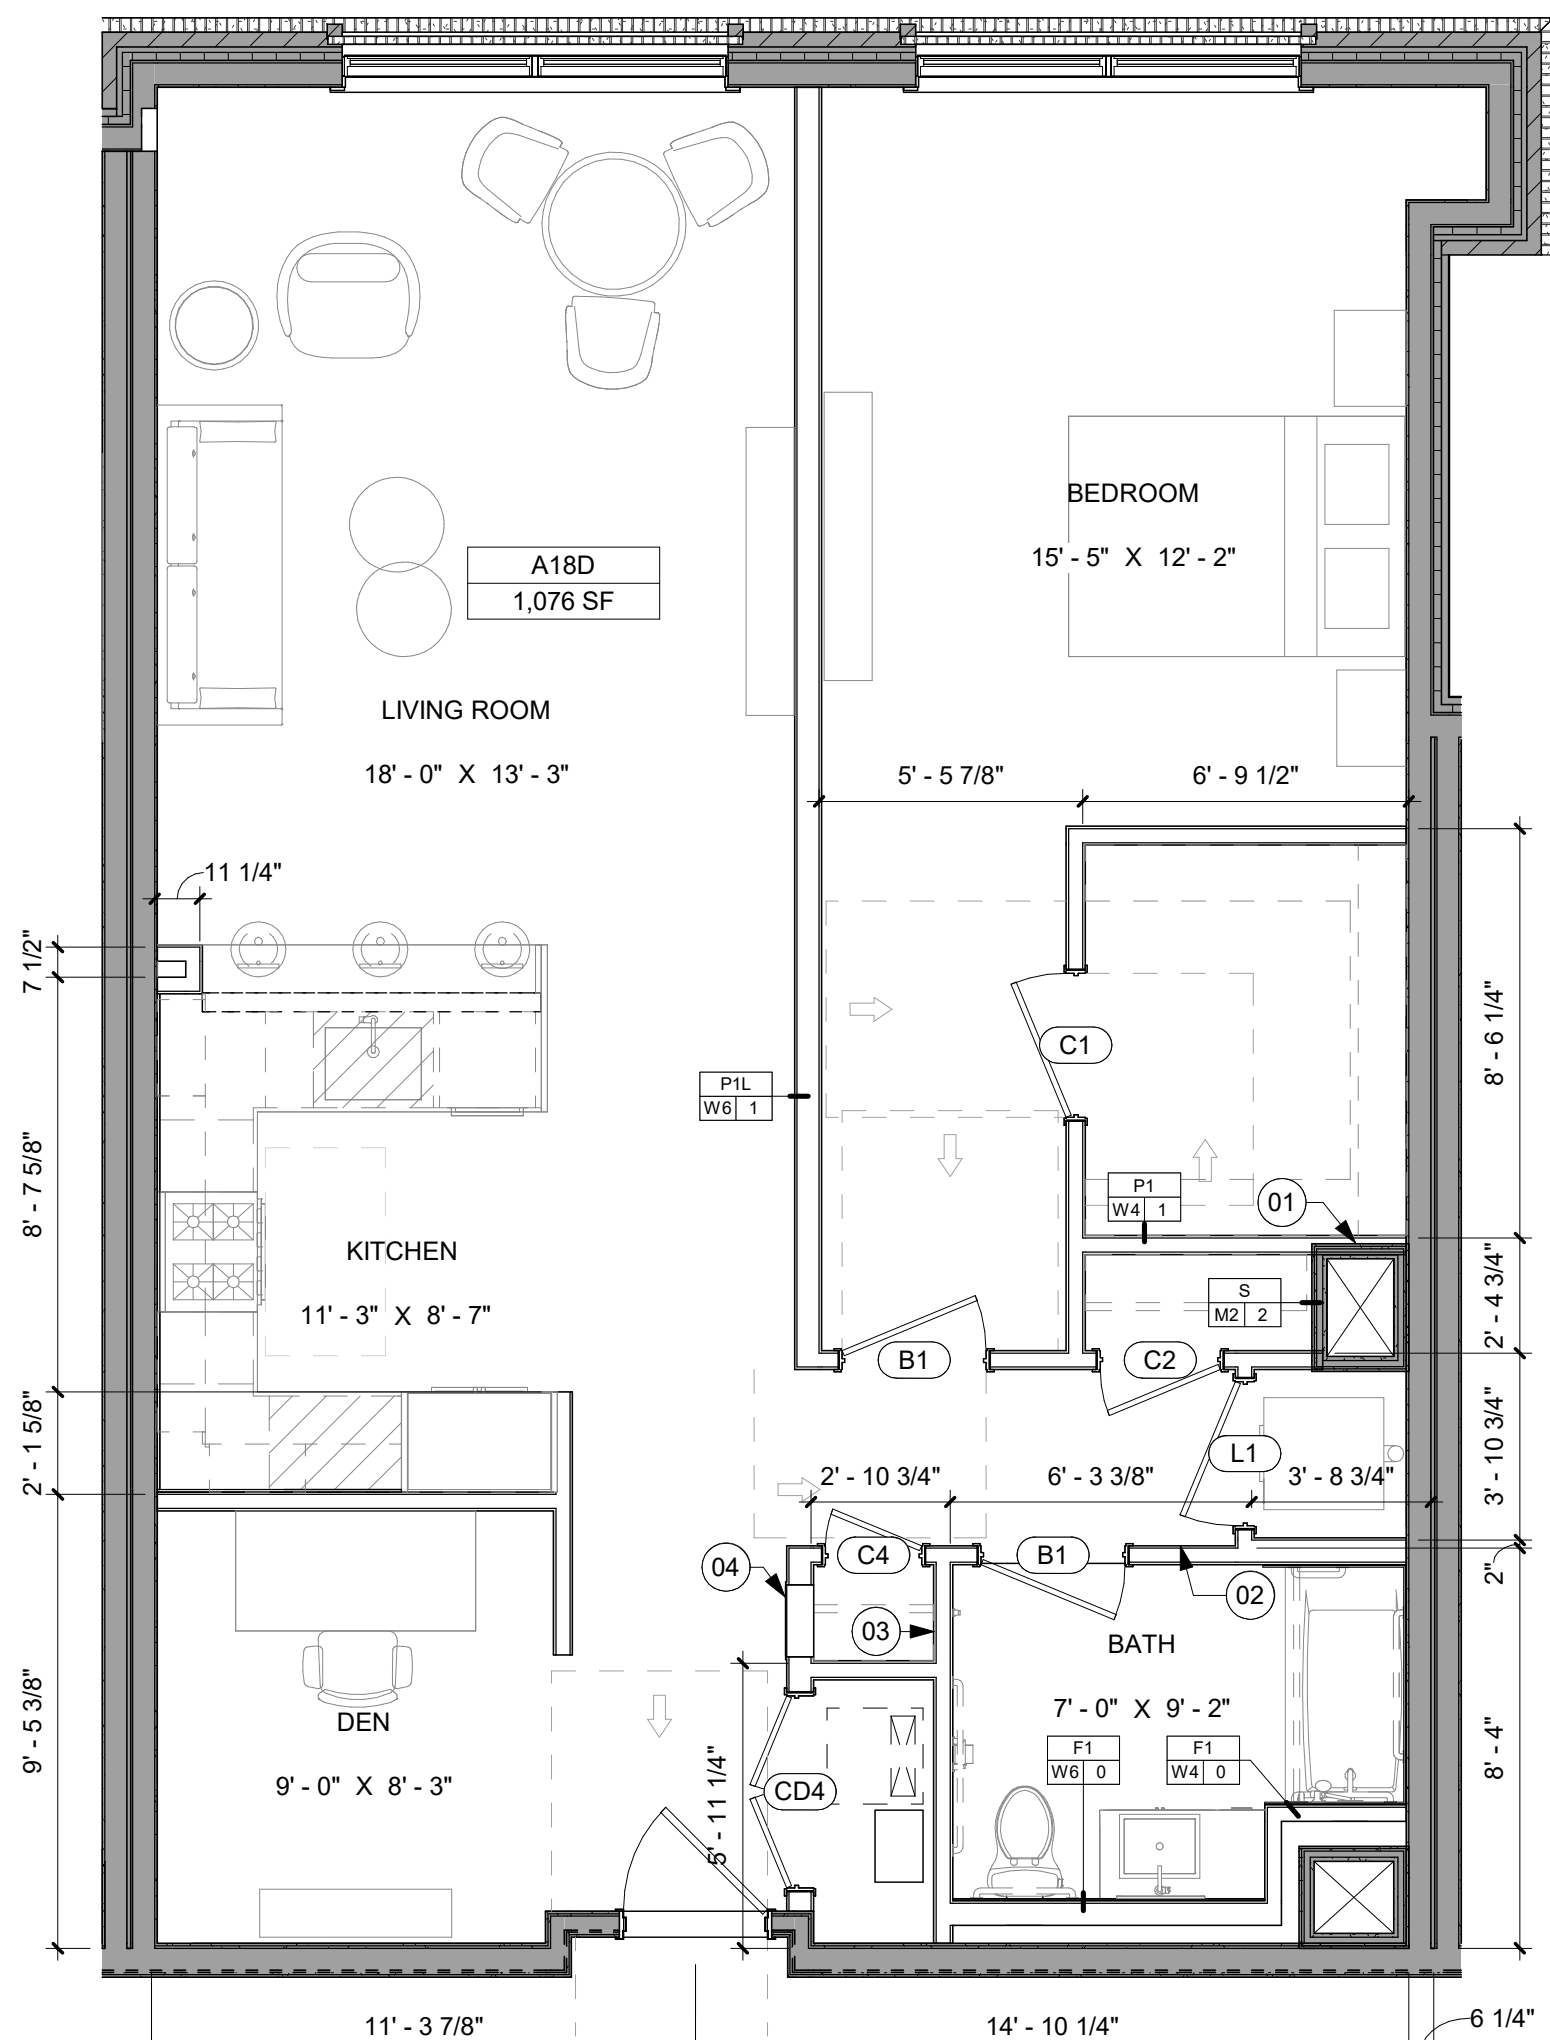


4 UNIT TYPE - A18D
SCALE: 1/4" = 1'-0"

NAME	KITCHEN TYPE	BATHROOM TYPE	COUNT	AREA
A18D	K1	B3	2	1,076 SF - 1,082 SF

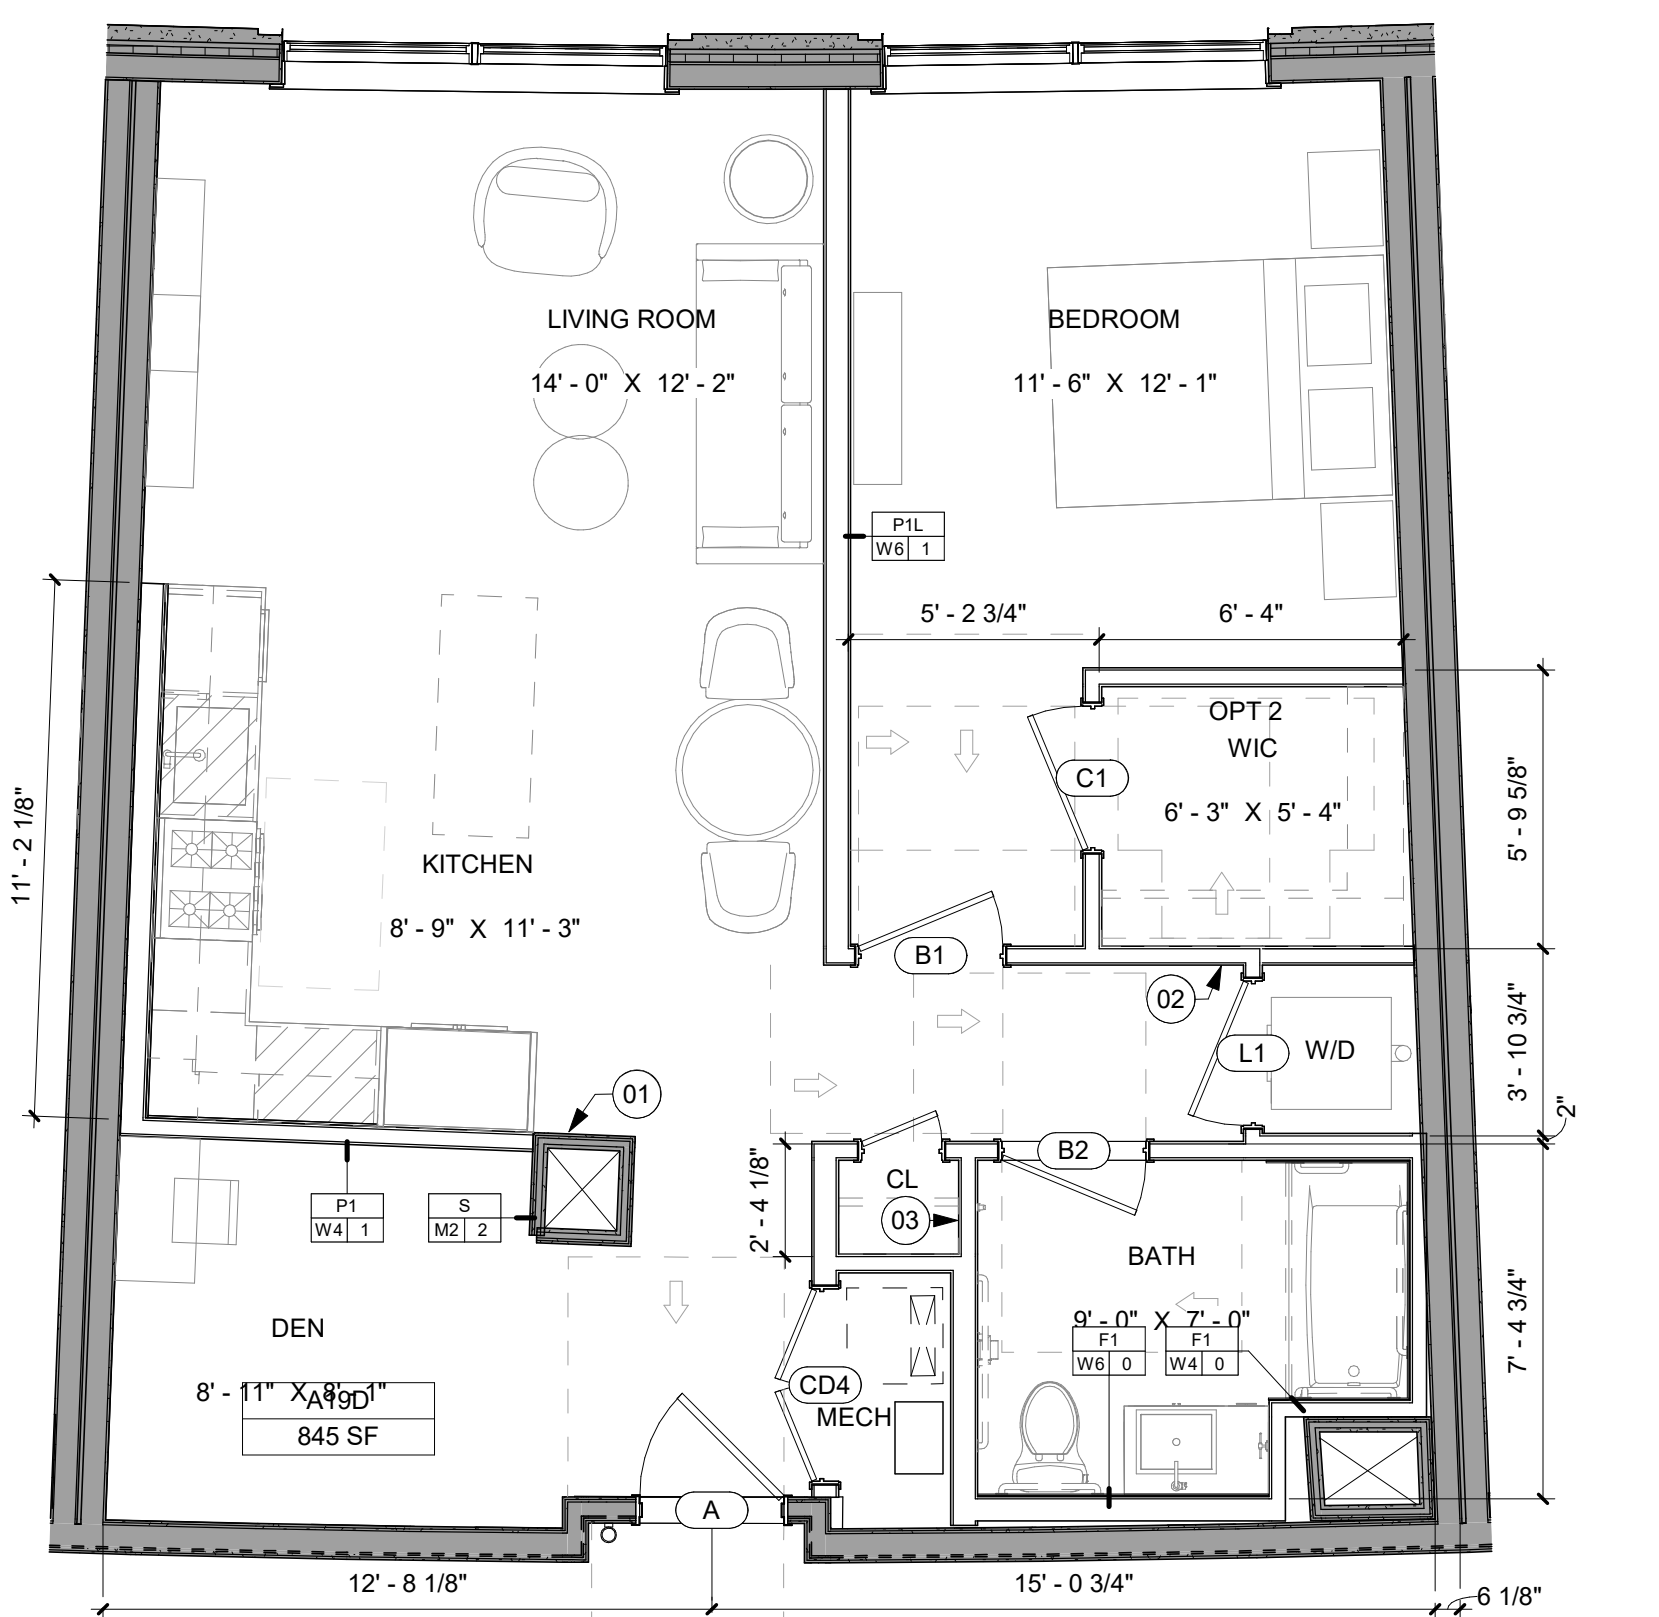


3 UNIT TYPE - A19D
SCALE: 1/4" = 1'-0"

NAME	KITCHEN TYPE	BATHROOM TYPE	COUNT	AREA
A19D	K4	B1	3	845 SF - 847 SF

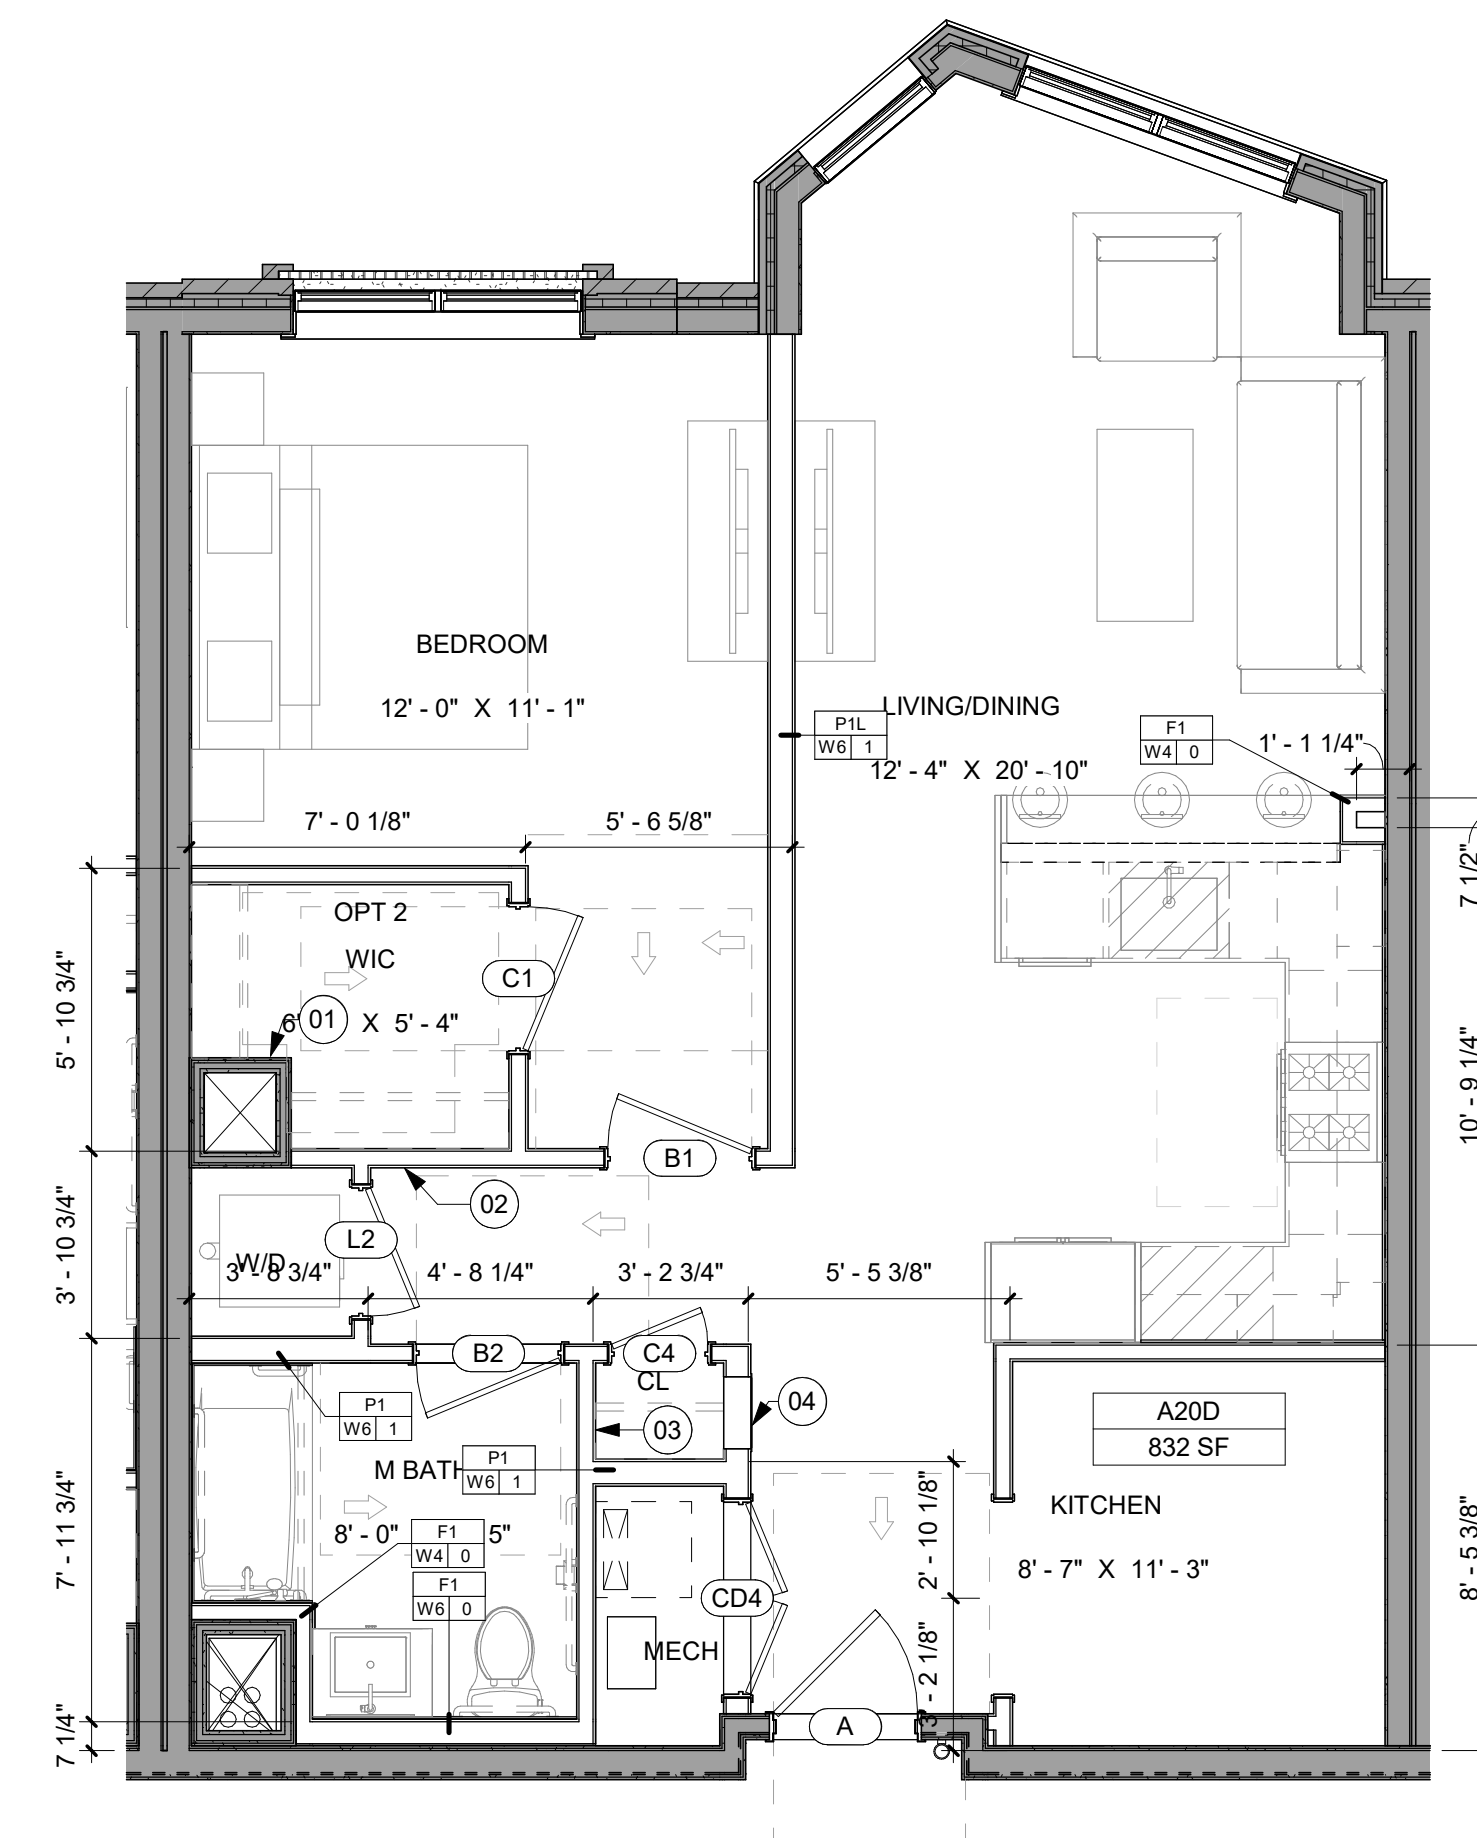

2 UNIT TYPE - A20D
SCALE: 1/4" = 1'-0"

UNIT TYPE	KITCHEN TYPE	BATHROOM TYPE	COUNT	AREA
A20D	K1	B3	2	832 SF

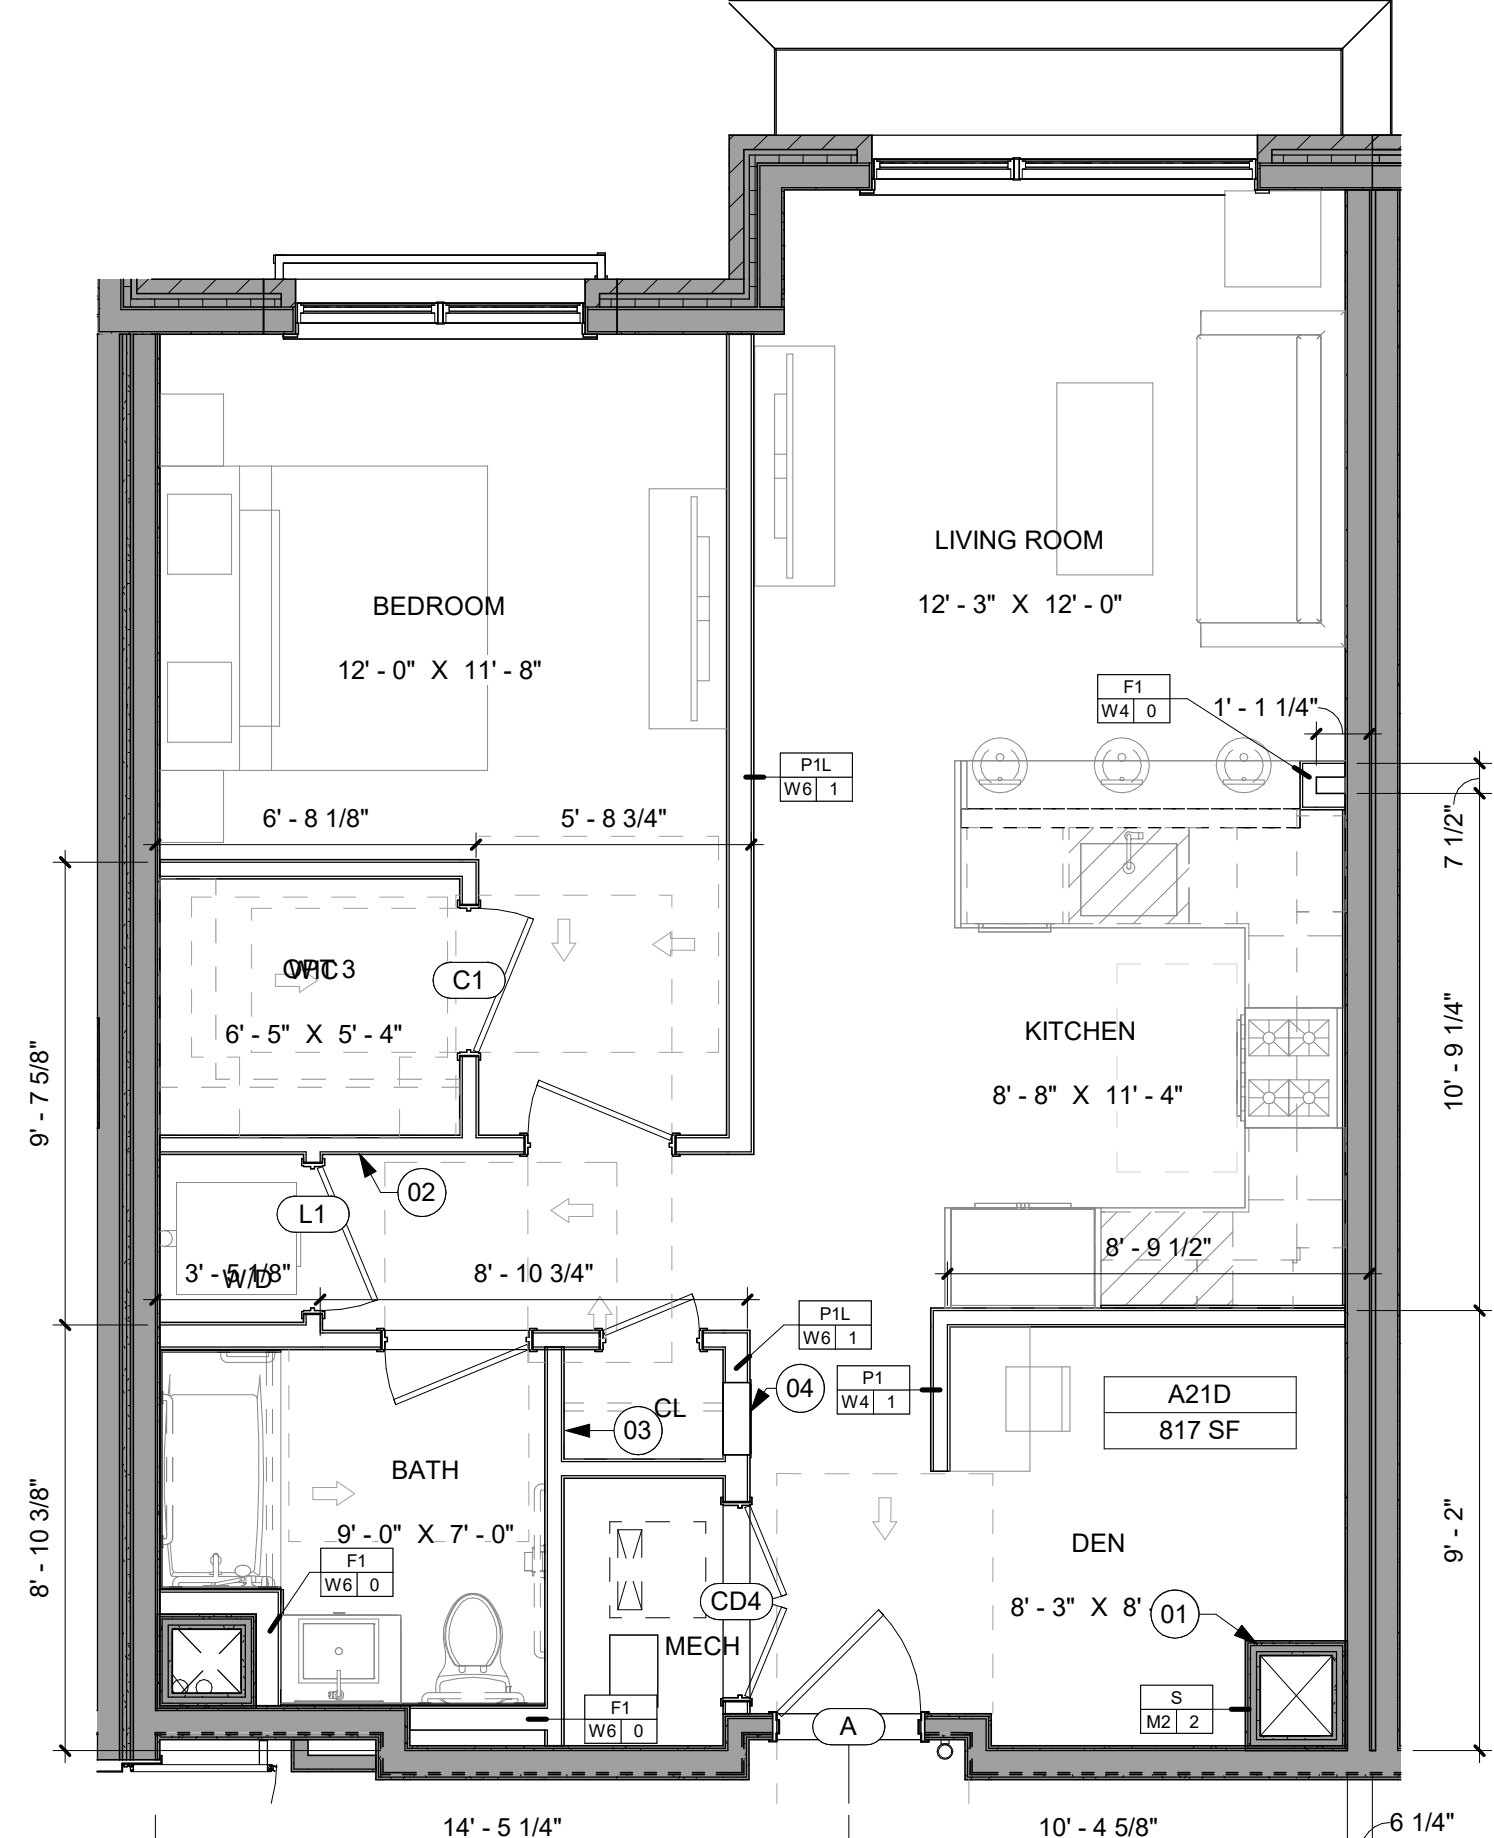

1 UNIT TYPE - A21D
SCALE: 1/4" = 1'-0"

UNIT TYPE	KITCHEN TYPE	BATHROOM TYPE	COUNT	AREA
A21D	K1	B3	2	817 SF

UNIT PLAN NOTES

- ALL INTERIOR DIMENSIONS TO WOOD FRAME PARTITIONS ARE TO FACE OF FRAMING. ALL INTERIOR DIMENSIONS TO METAL FRAME PARTITIONS ARE TO FACE OF FINISH AND ARE NOTED WITH ASTERISKS "X". ALL OTHER DIMENSIONS ARE AS SHOWN.
- ALL UNIT INTERIOR PARTITIONS TO BE WALL TYPE XX UNLESS OTHERWISE NOTED.
- LOCATE DOOR OPENINGS 4" FROM ADJACENT WALL UNLESS OTHERWISE NOTED.
- SEE MECHANICAL AND PLUMBING DRAWINGS FOR EQUIPMENT SPECIFICATIONS.
- SEE ELECTRICAL AND LOW VOLTAGE DRAWINGS FOR POWER AND LOW VOLTAGE PLANS.

KEYNOTES

#	DESCRIPTION
01	MECH. CHASE REF. MEP DRAWINGS
02	ELECTRICAL LOAD CENTER. REFER TO ELEC. DRAWINGS
03	IND BOX REF. TO ELEC. FOR MORE INFO
04	WALL RETURN REF. TO ELEC. DRAWINGS

Dean Marchetto, FAIA, PP
NJ 07045
Michael Higgins, AIA, LEED
NJ 07045
Bruce A. Silver, AIA
NJ 07045
Michael Baldo, AIA
NJ 07045
Vincent Marchetto, AIA
NJ 07045

1422 Grand Street
Suite 5b
Hoboken, NJ 07030
T.201-795-1505
MHSArchitecture.com

PROJECT NAME:
**MORRISTOWN GREEN
APARTMENTS**
22 LAFAYETTE AVENUE
TOWN OF MORRISTOWN, NEW JERSEY

PREPARED FOR:
**MORRISTOWN
ASSOCIATES LLC**
4 CUNNINGHAM DRIVE
WEST ORANGE, NJ

ISSUE	#	DATE	FOR:
	1	06/03/2026	BID SET
	1	07/09/26	ADDENDUM #1

ENLARGED UNIT PLANS - 1
BR

PROJECT NUMBER:	2202
SCALE:	As indicated
DRAWN BY:	CM / TM / JE
CHECKED BY:	FT / MB

A09.04