




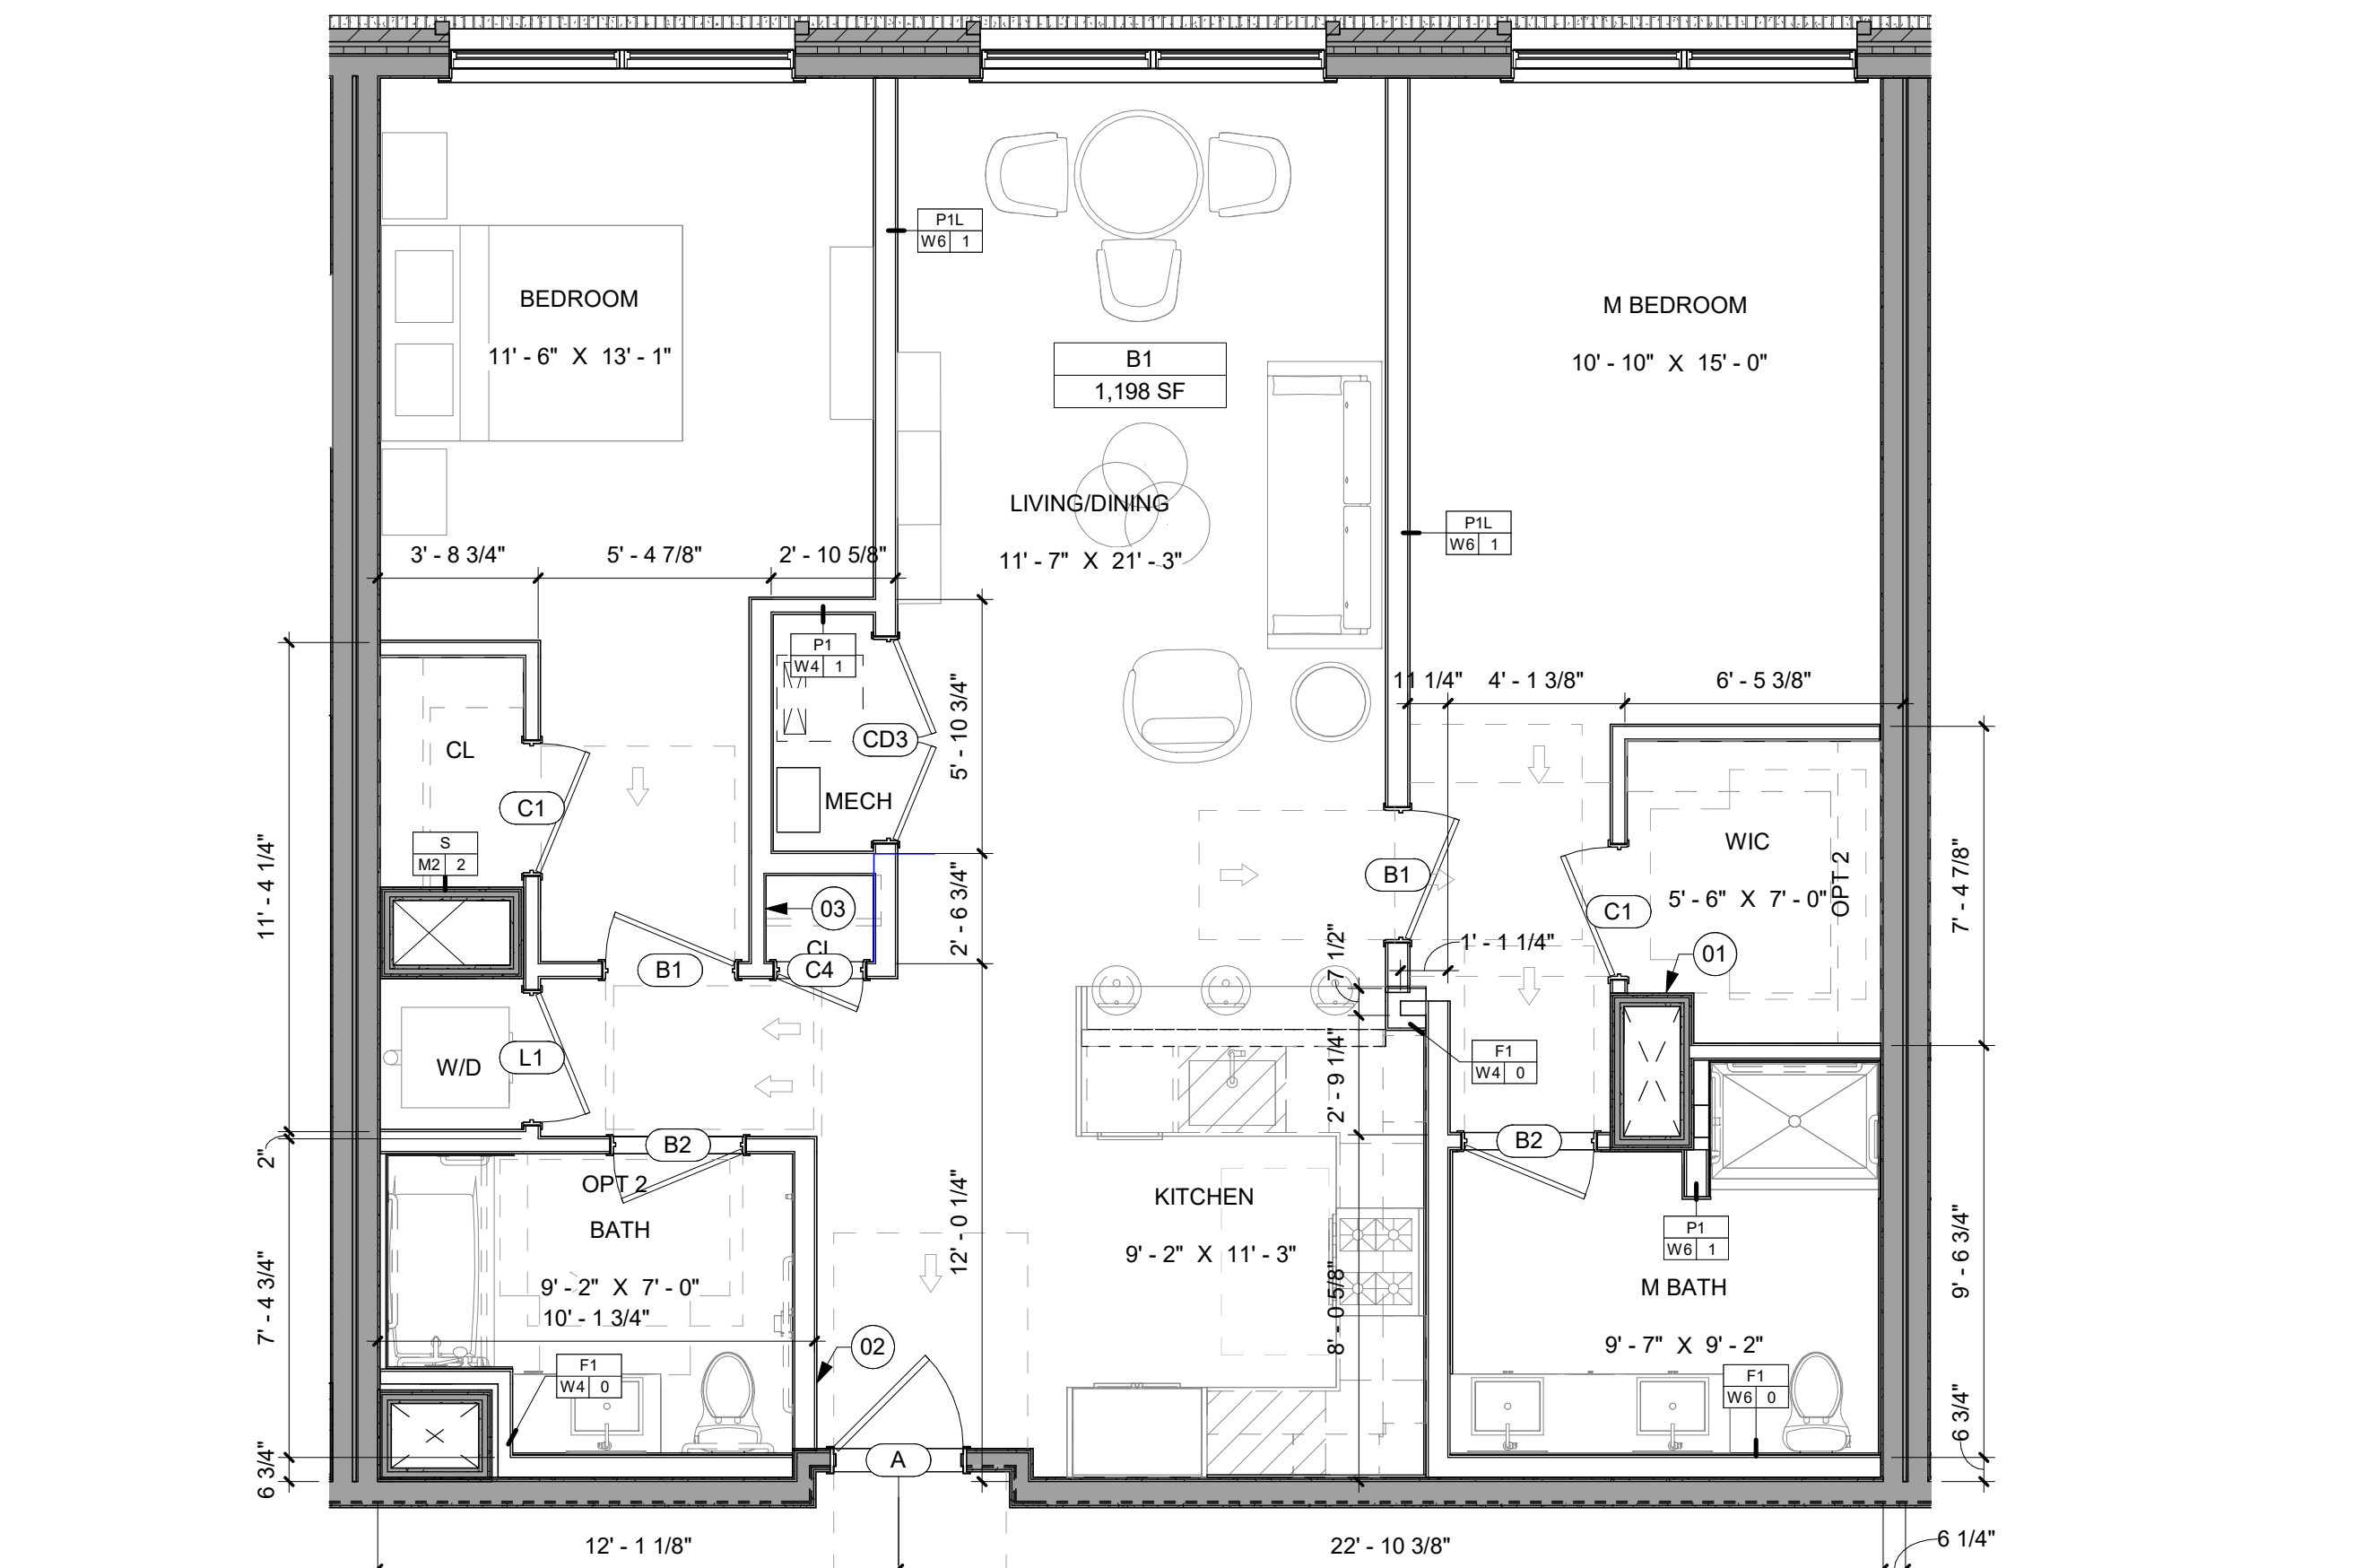


37 UNIT TYPE - B1
SCALE: 1/4" = 1'-0"

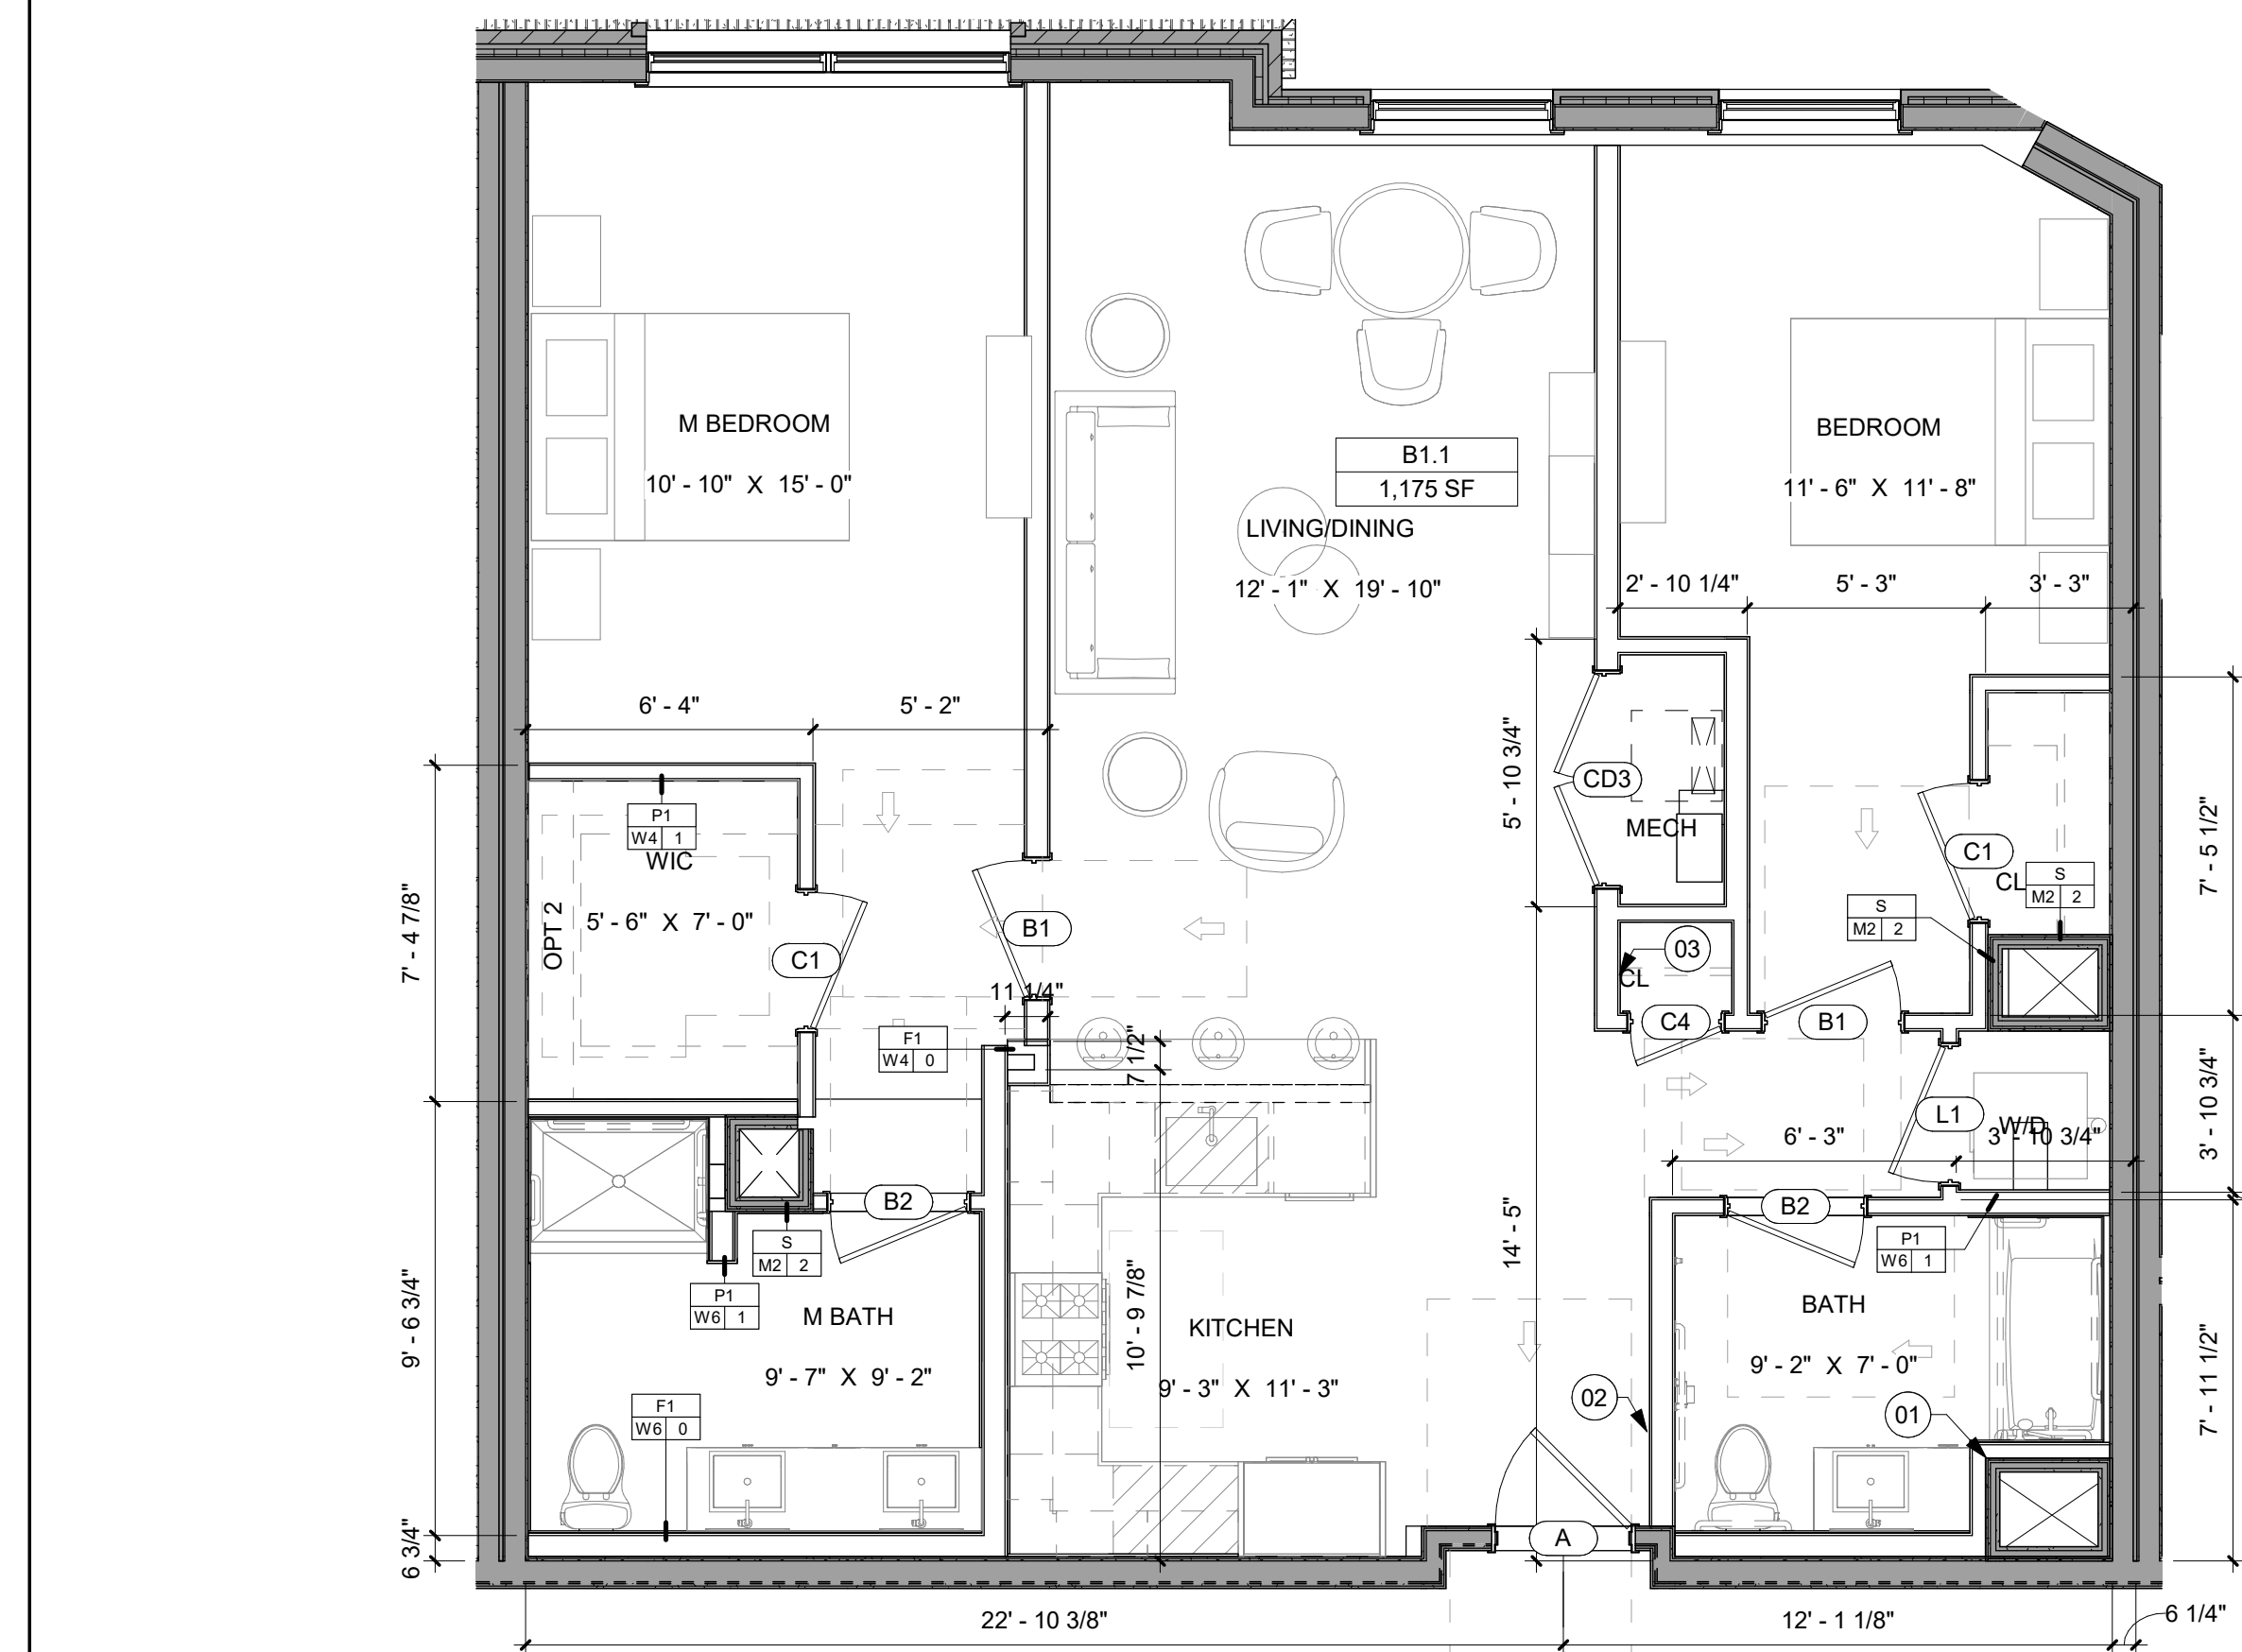


8 UNIT TYPE - B1.1
SCALE: 1/4" = 1'-0"

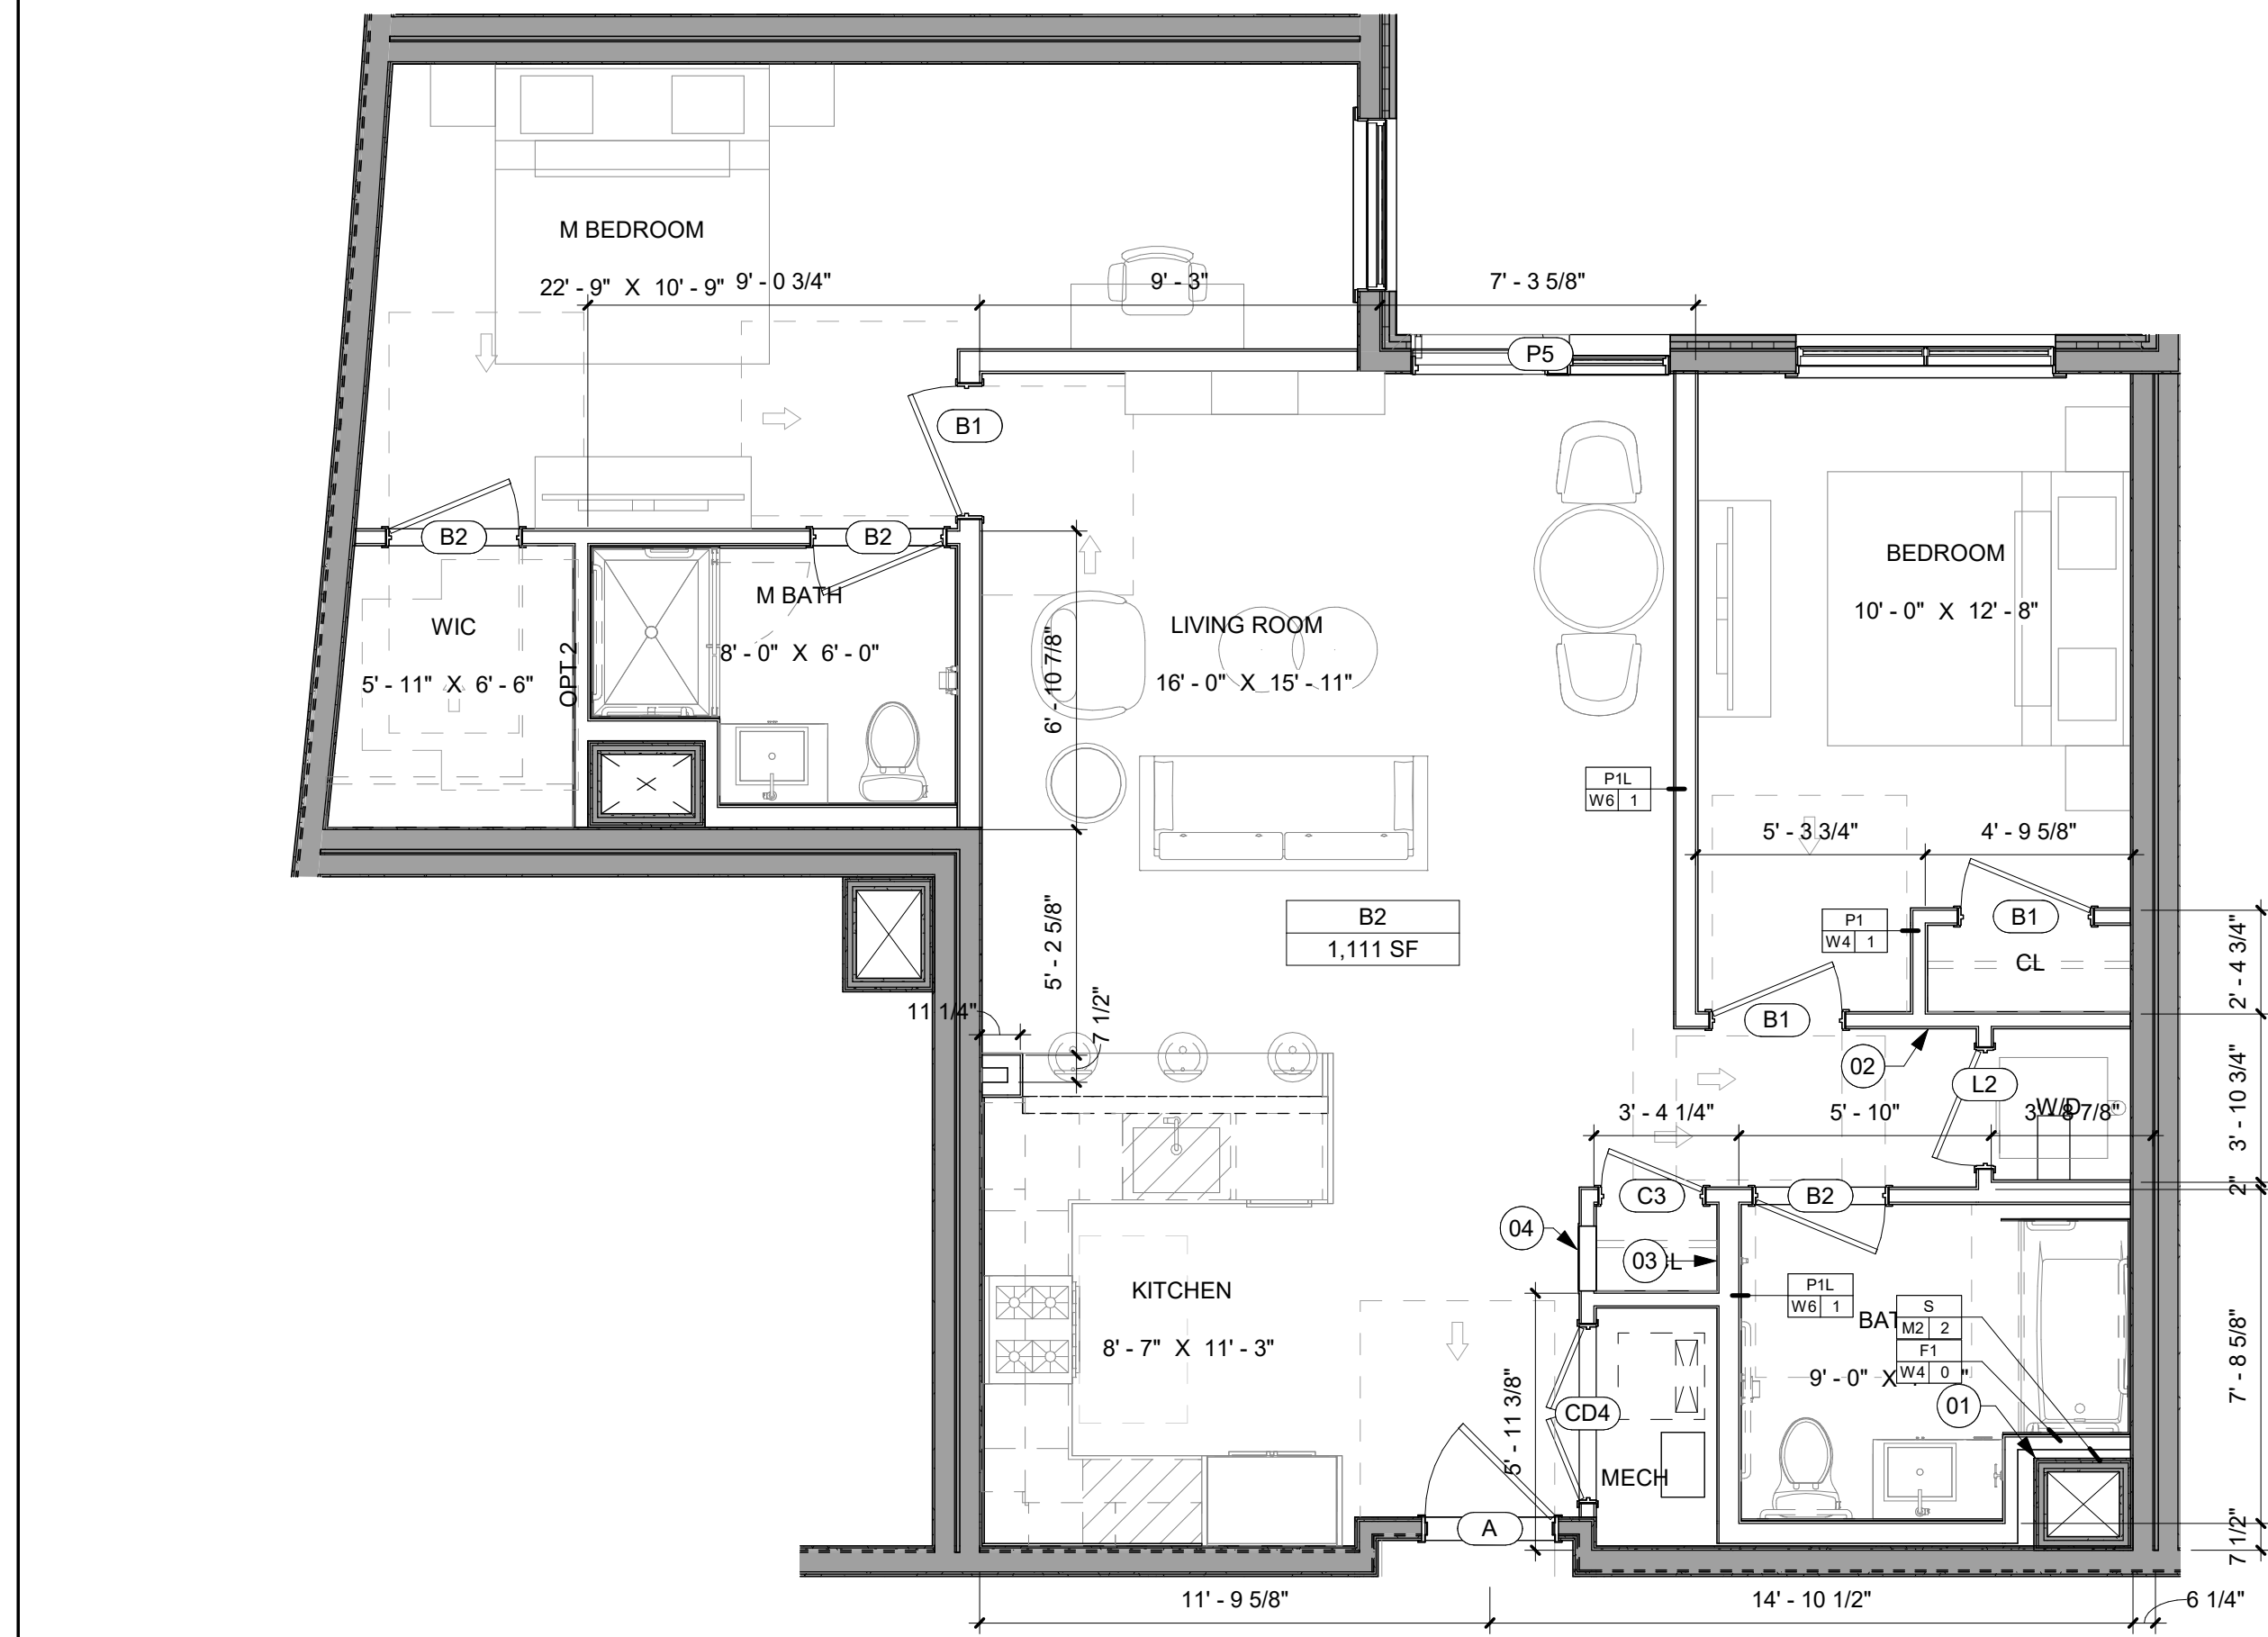


7 UNIT TYPE - B2
SCALE: 1/4" = 1'-0"

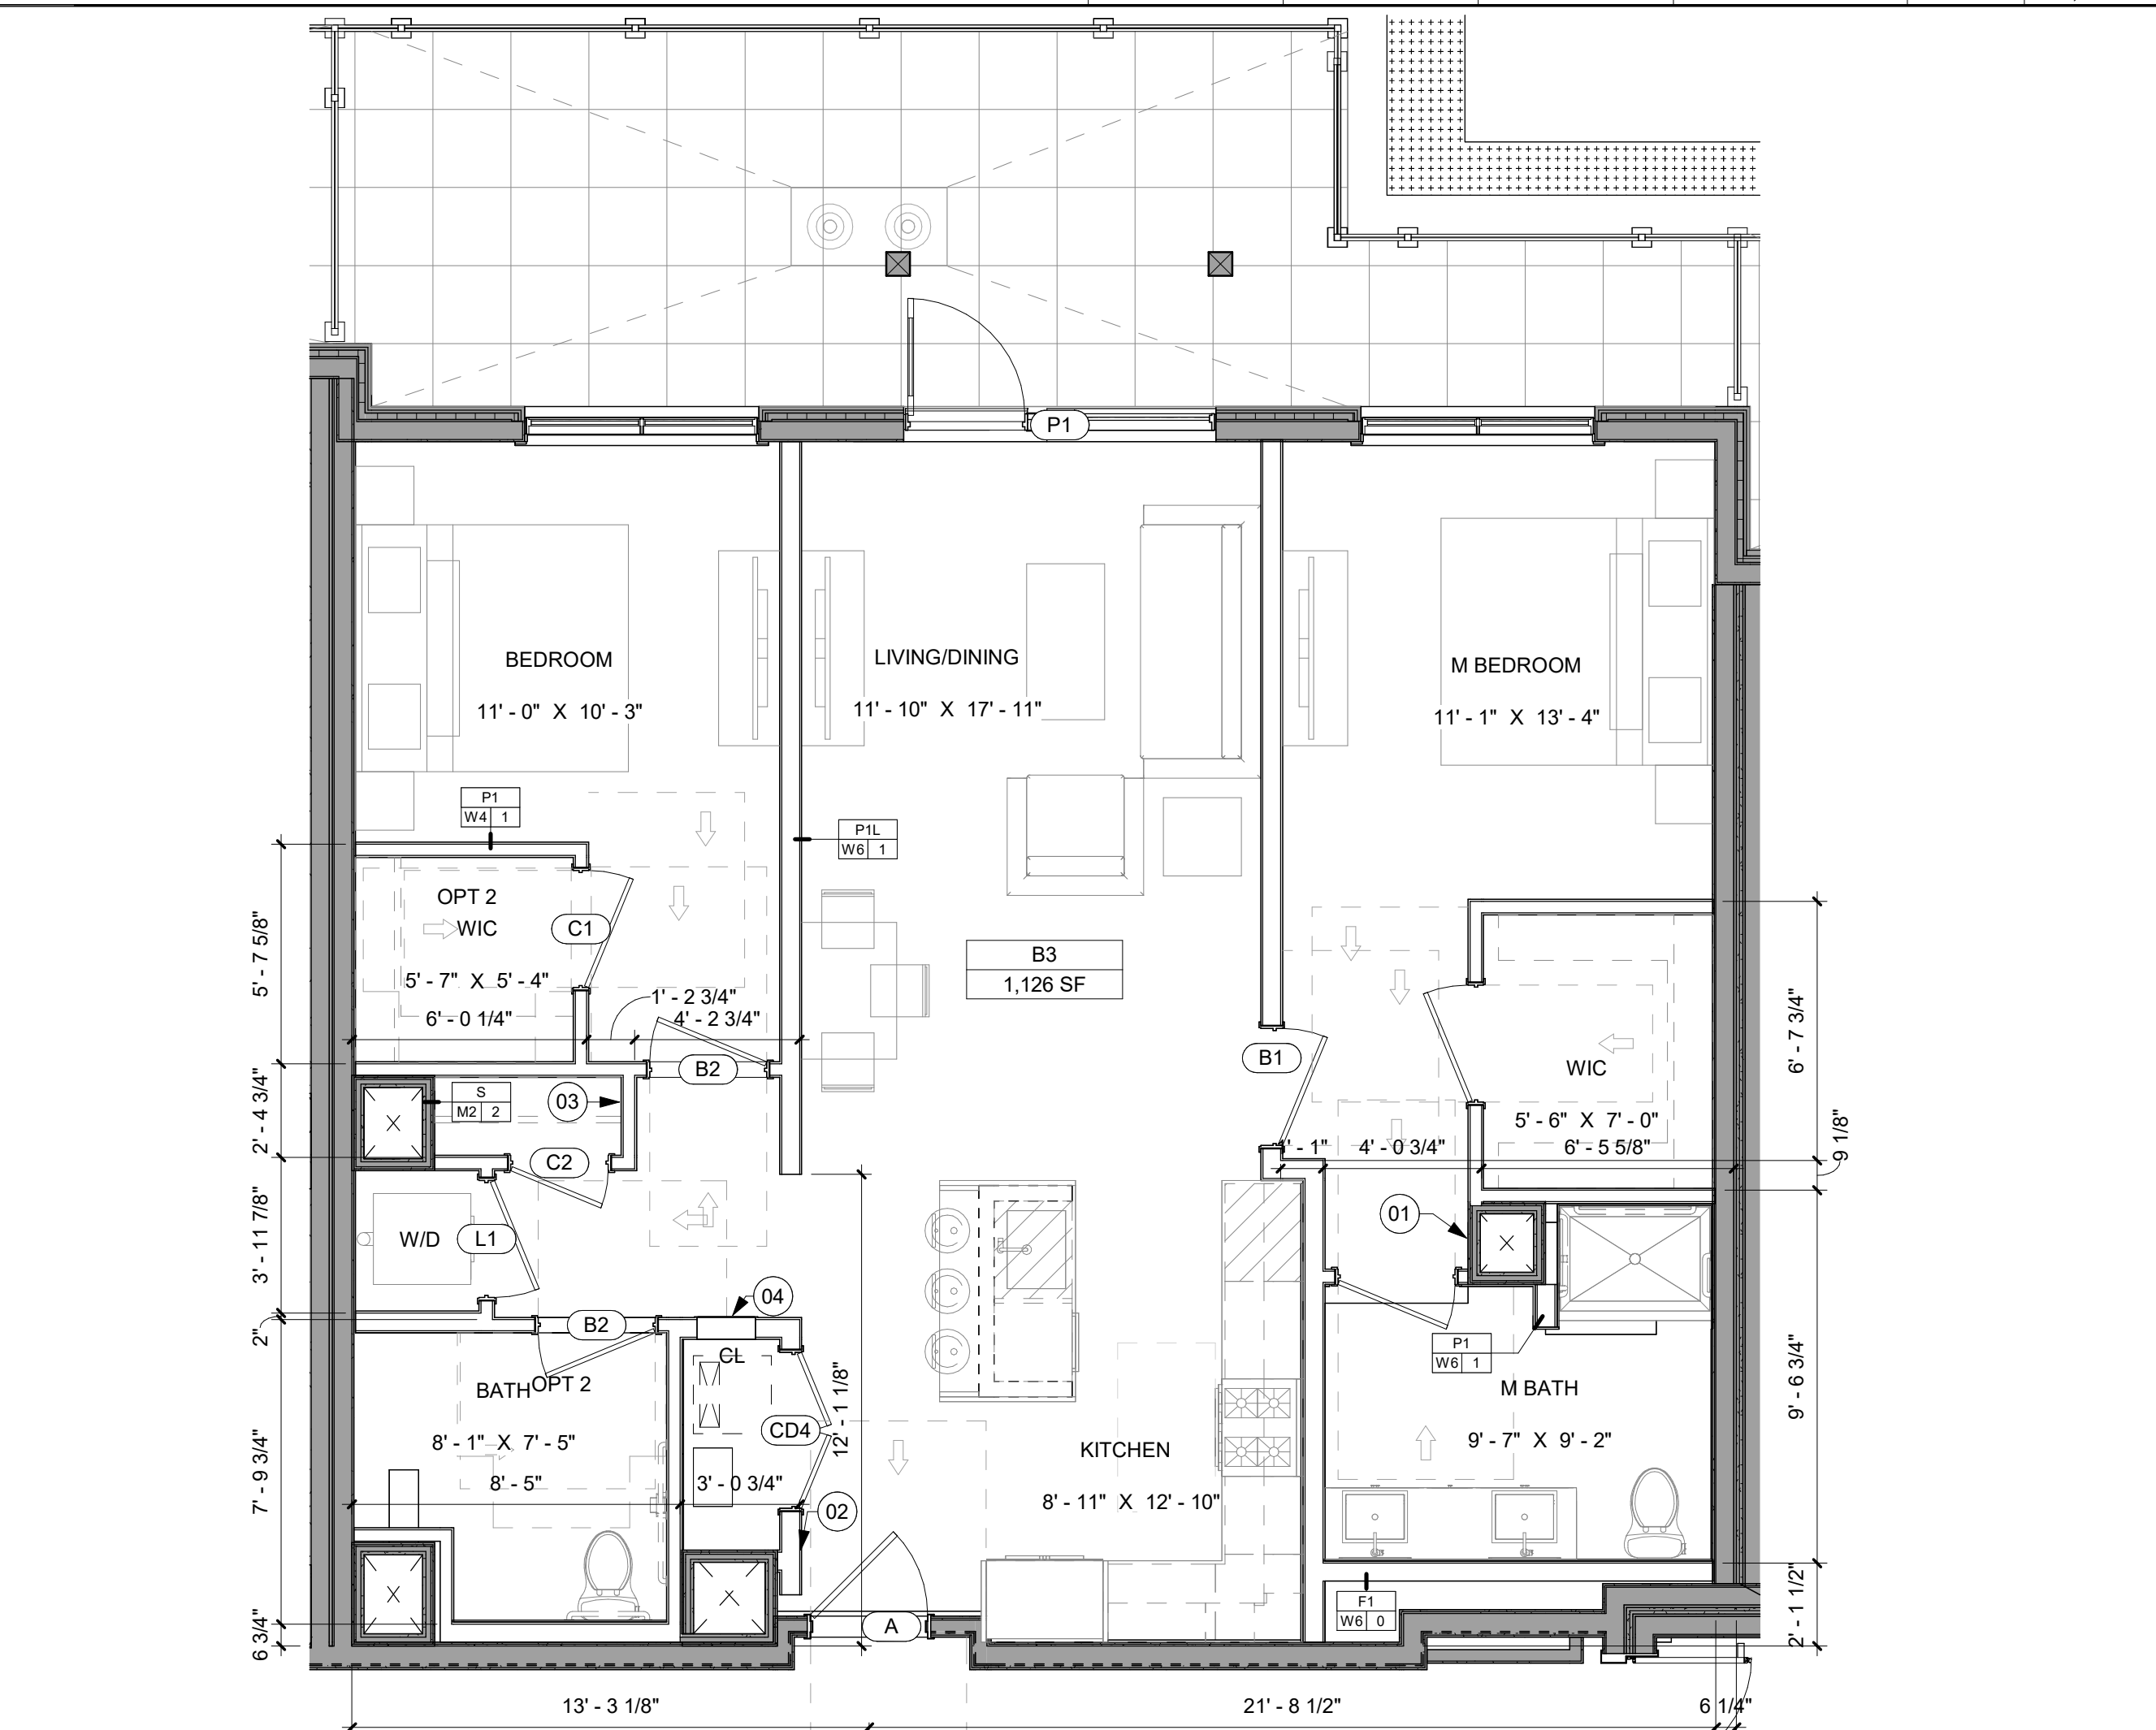


6 UNIT TYPE - B3
SCALE: 1/4" = 1'-0"

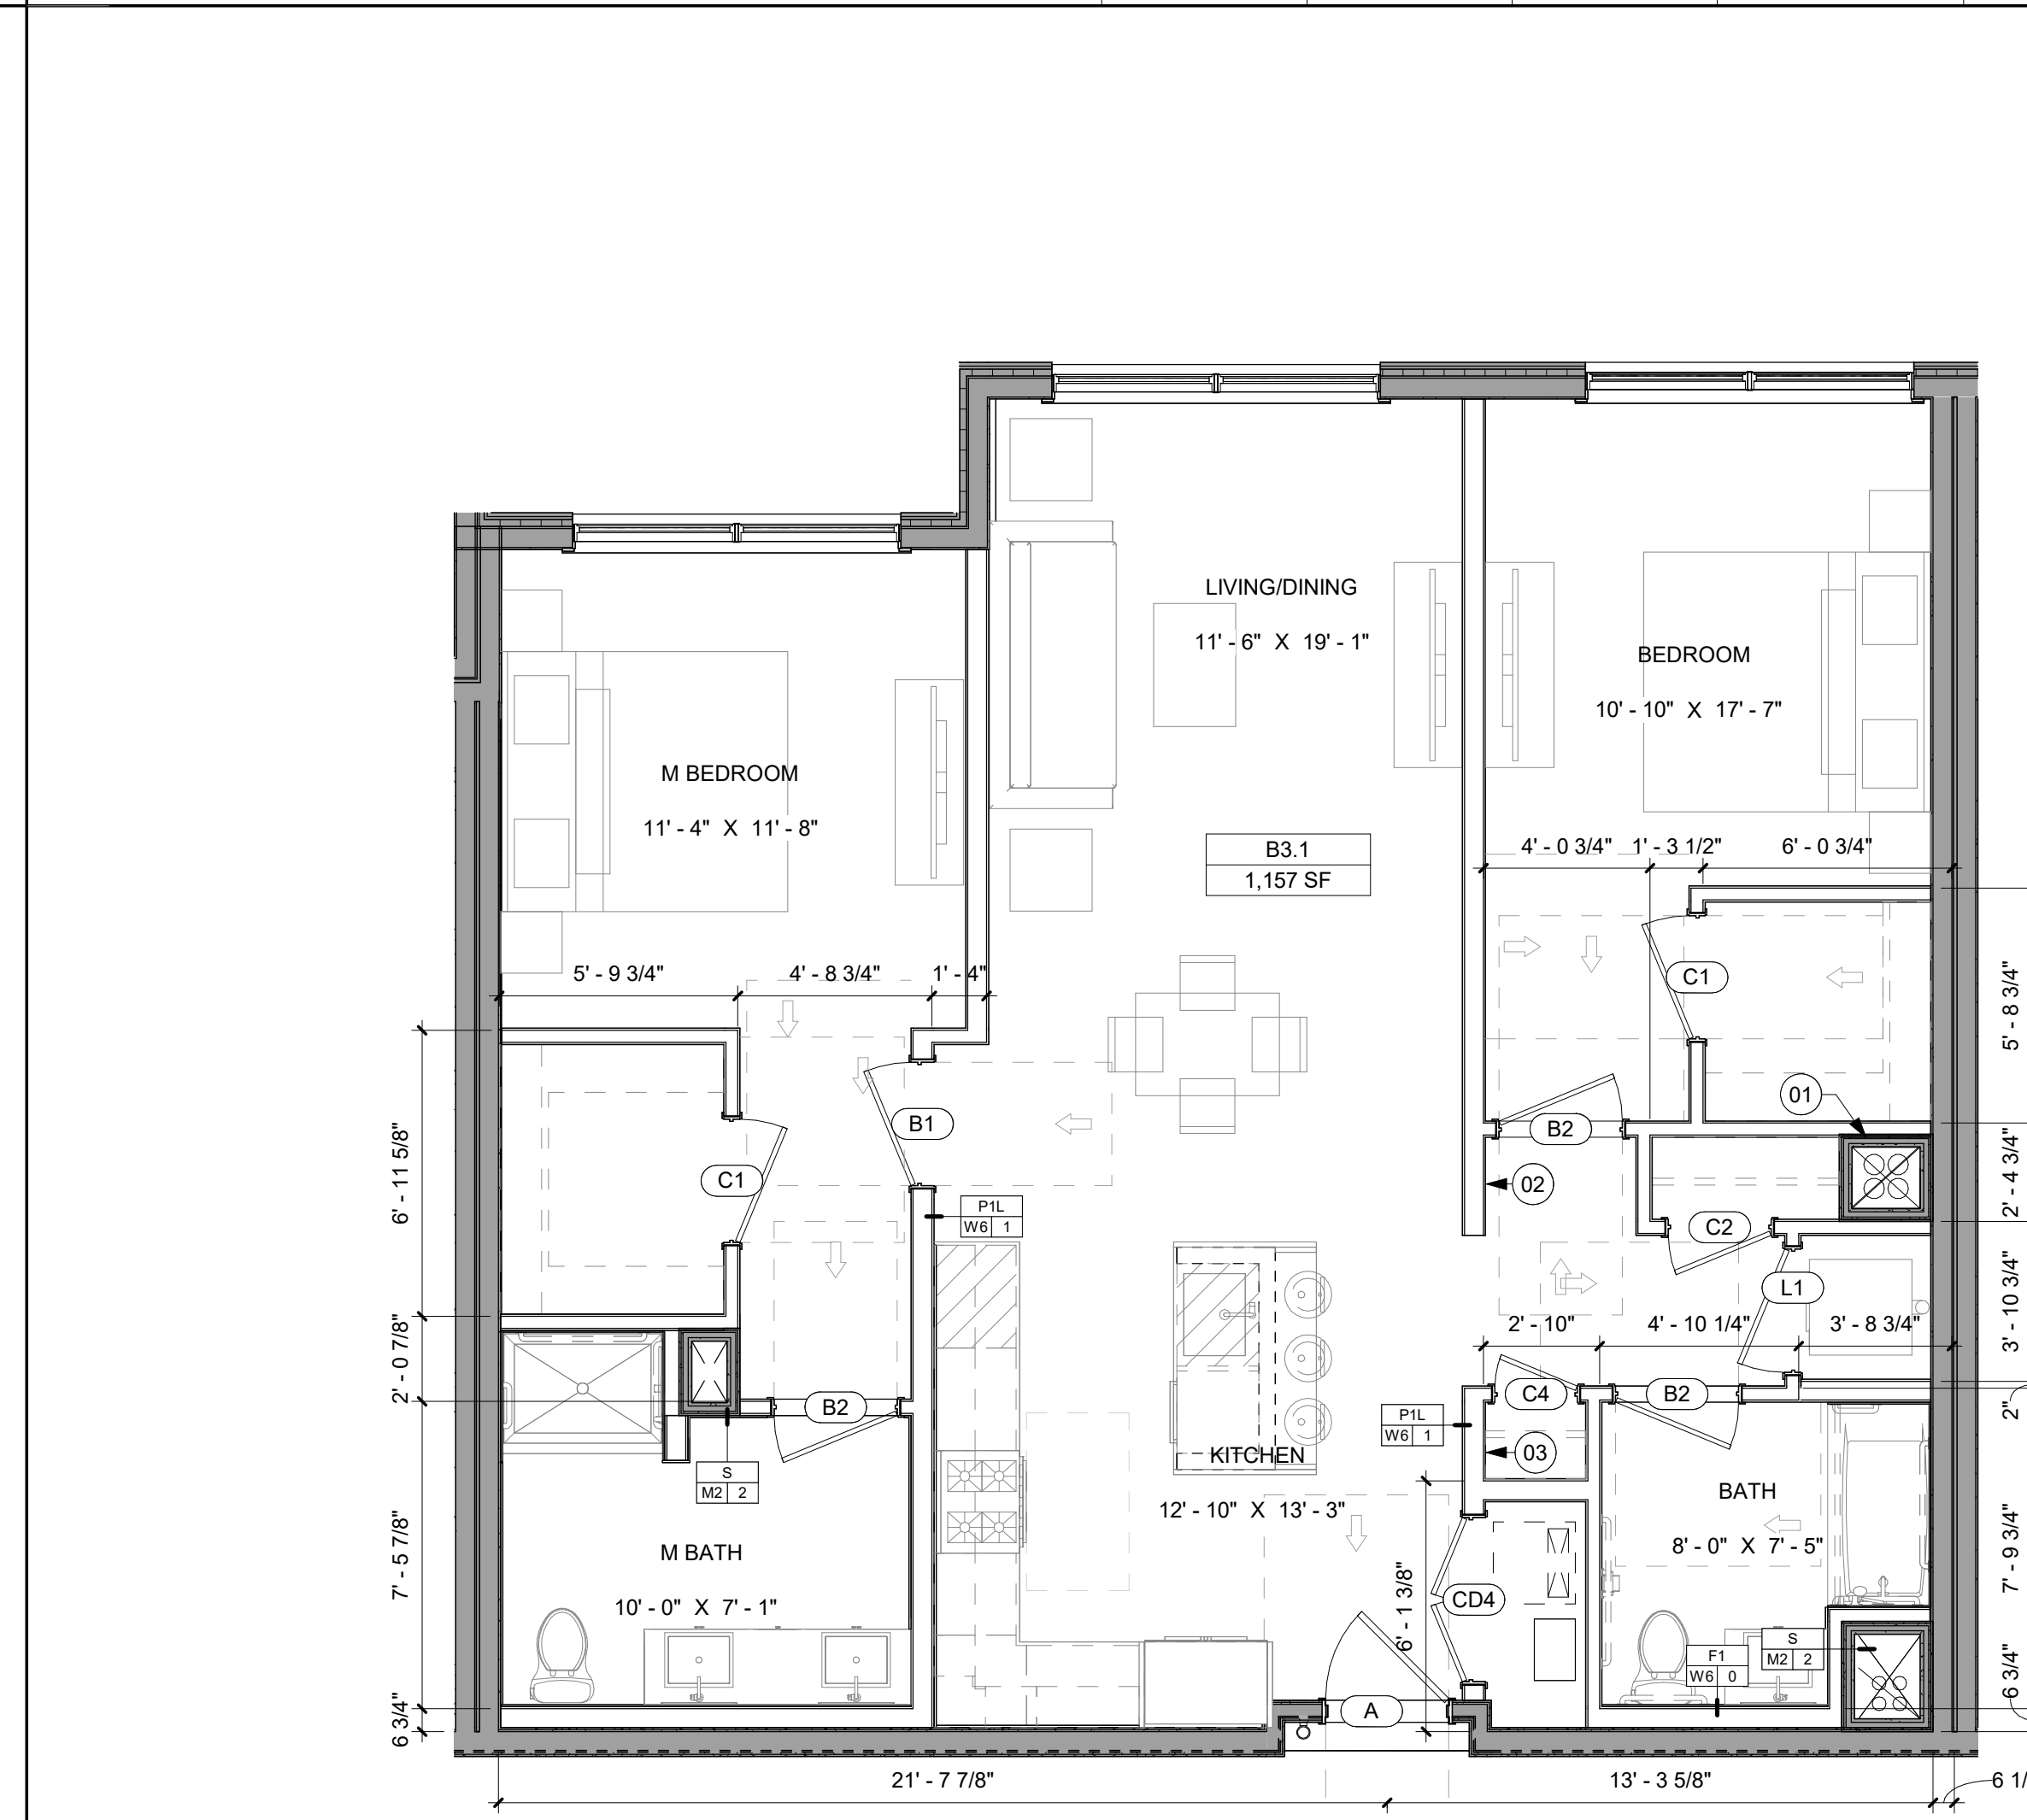


5 UPF - UNIT TYPE B3.1
SCALE: 1/4" = 1'-0"

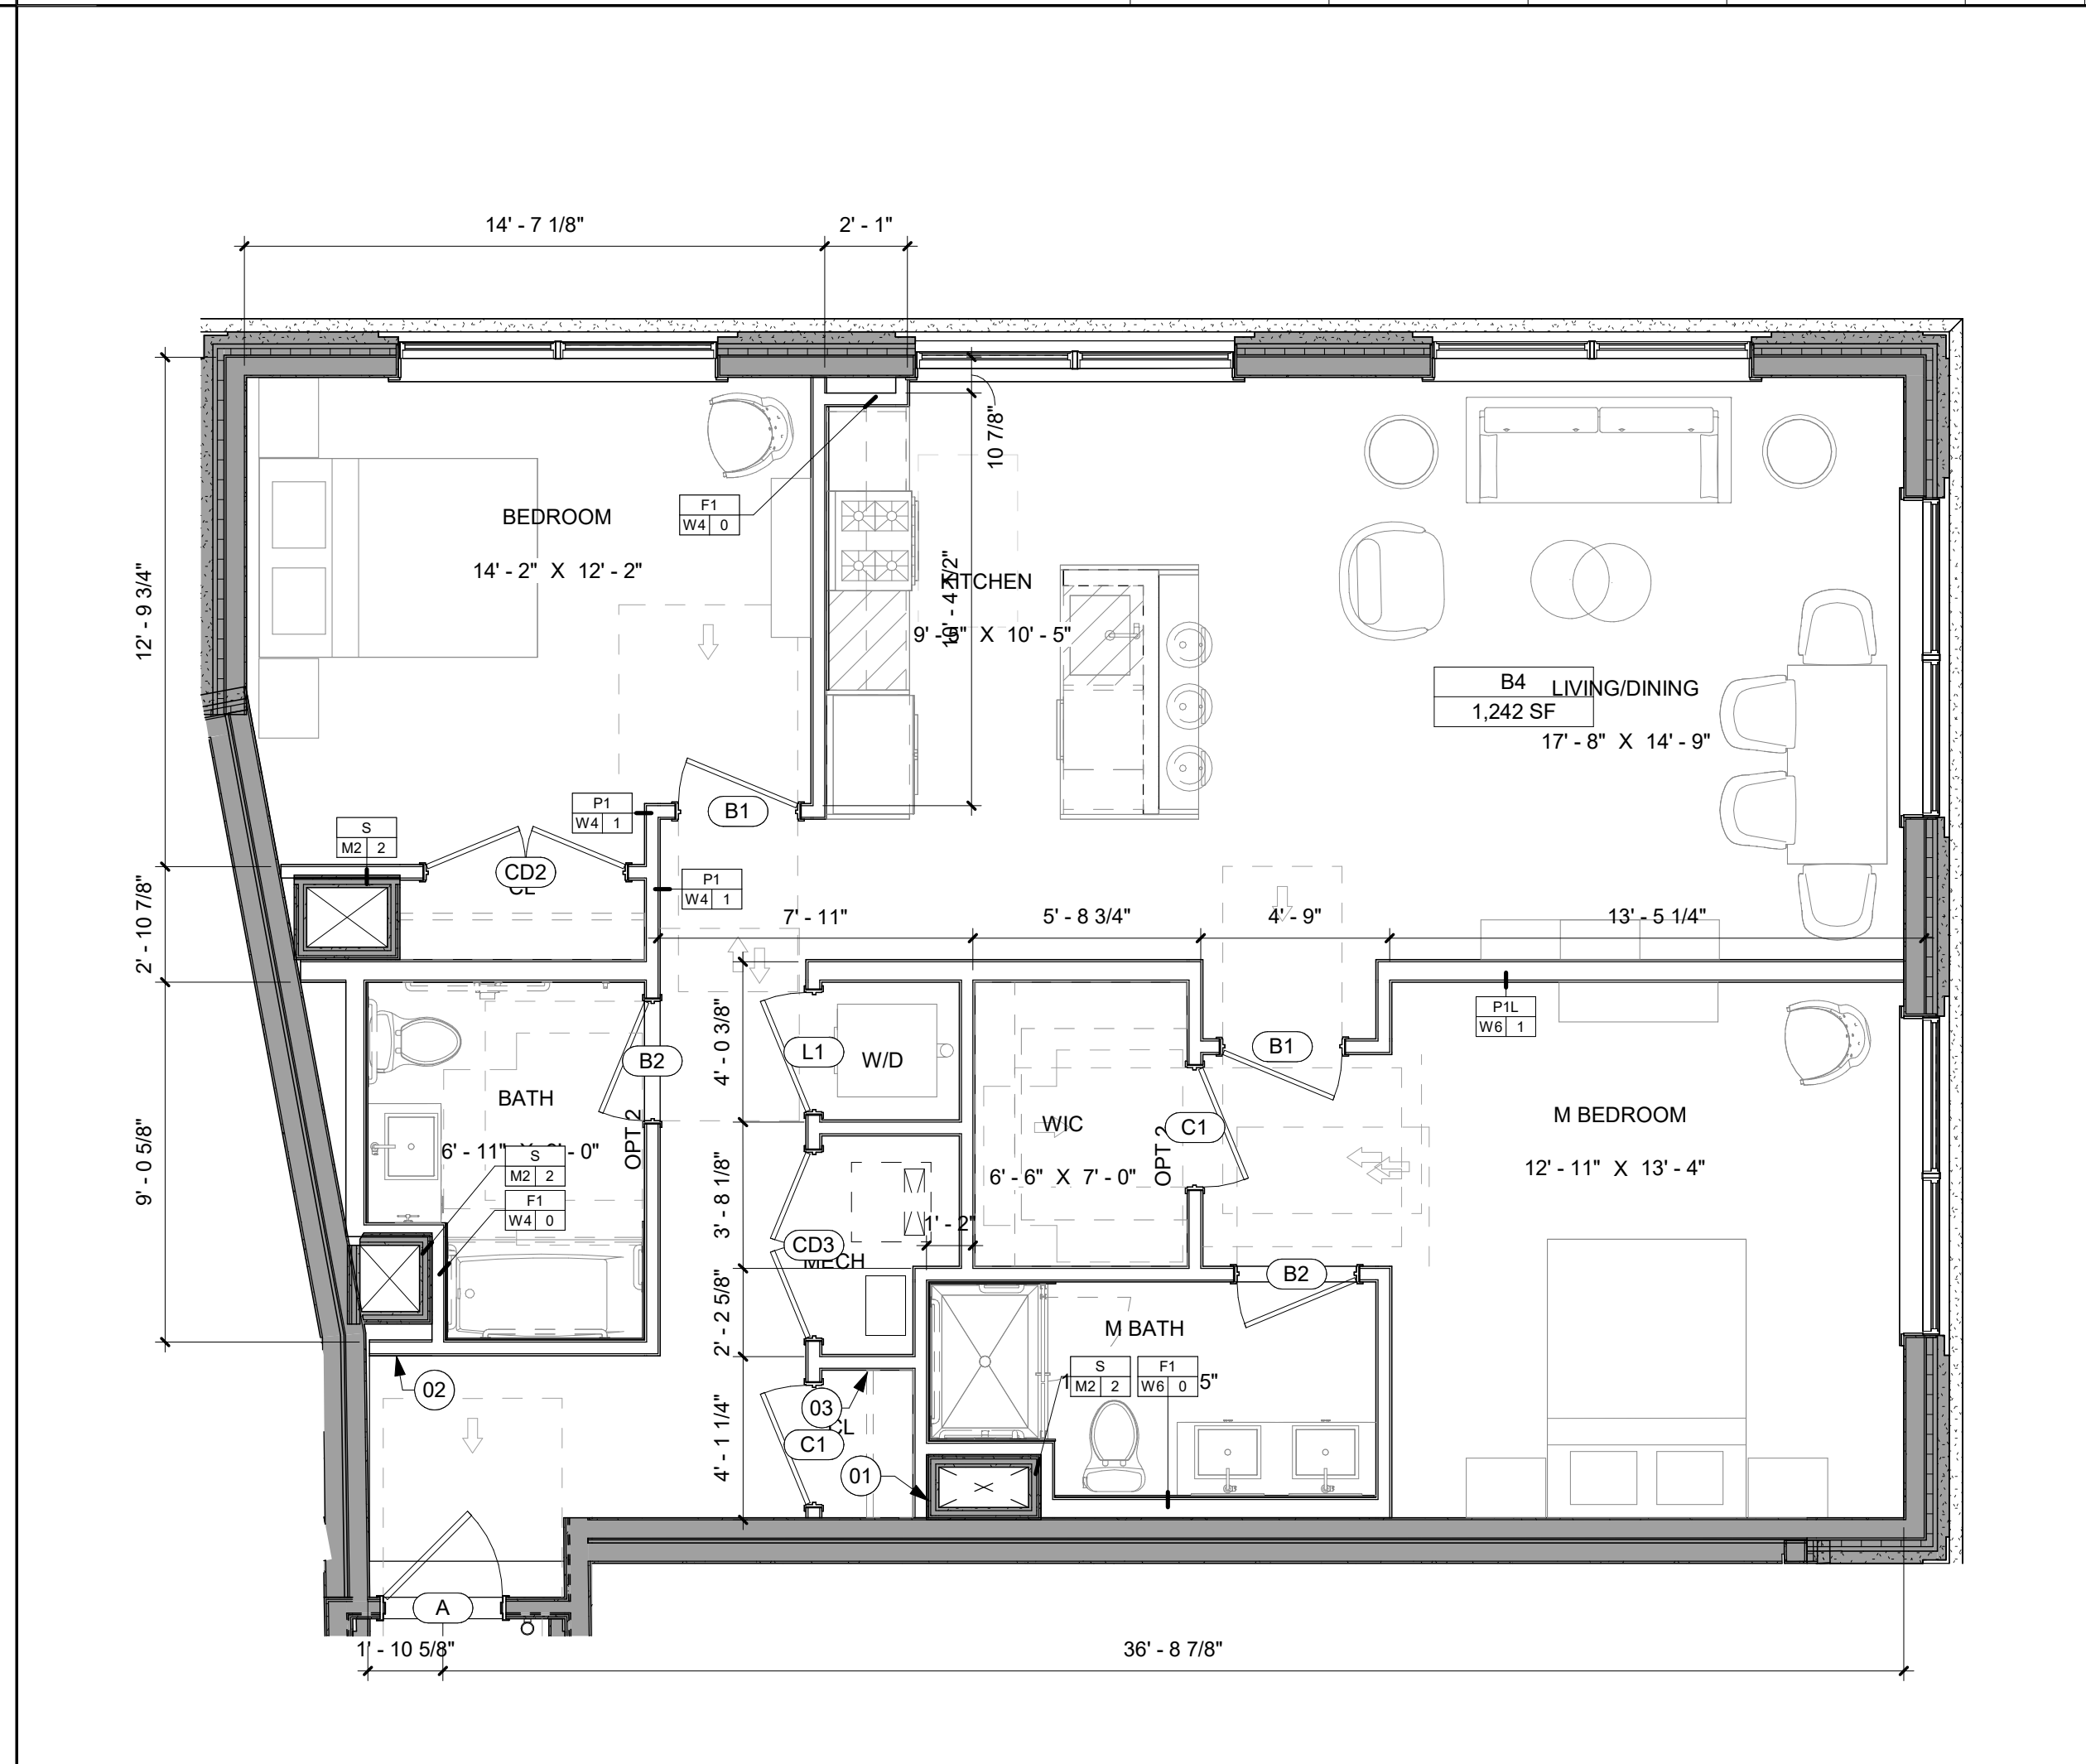


4 UNIT TYPE - B4
SCALE: 1/4" = 1'-0"

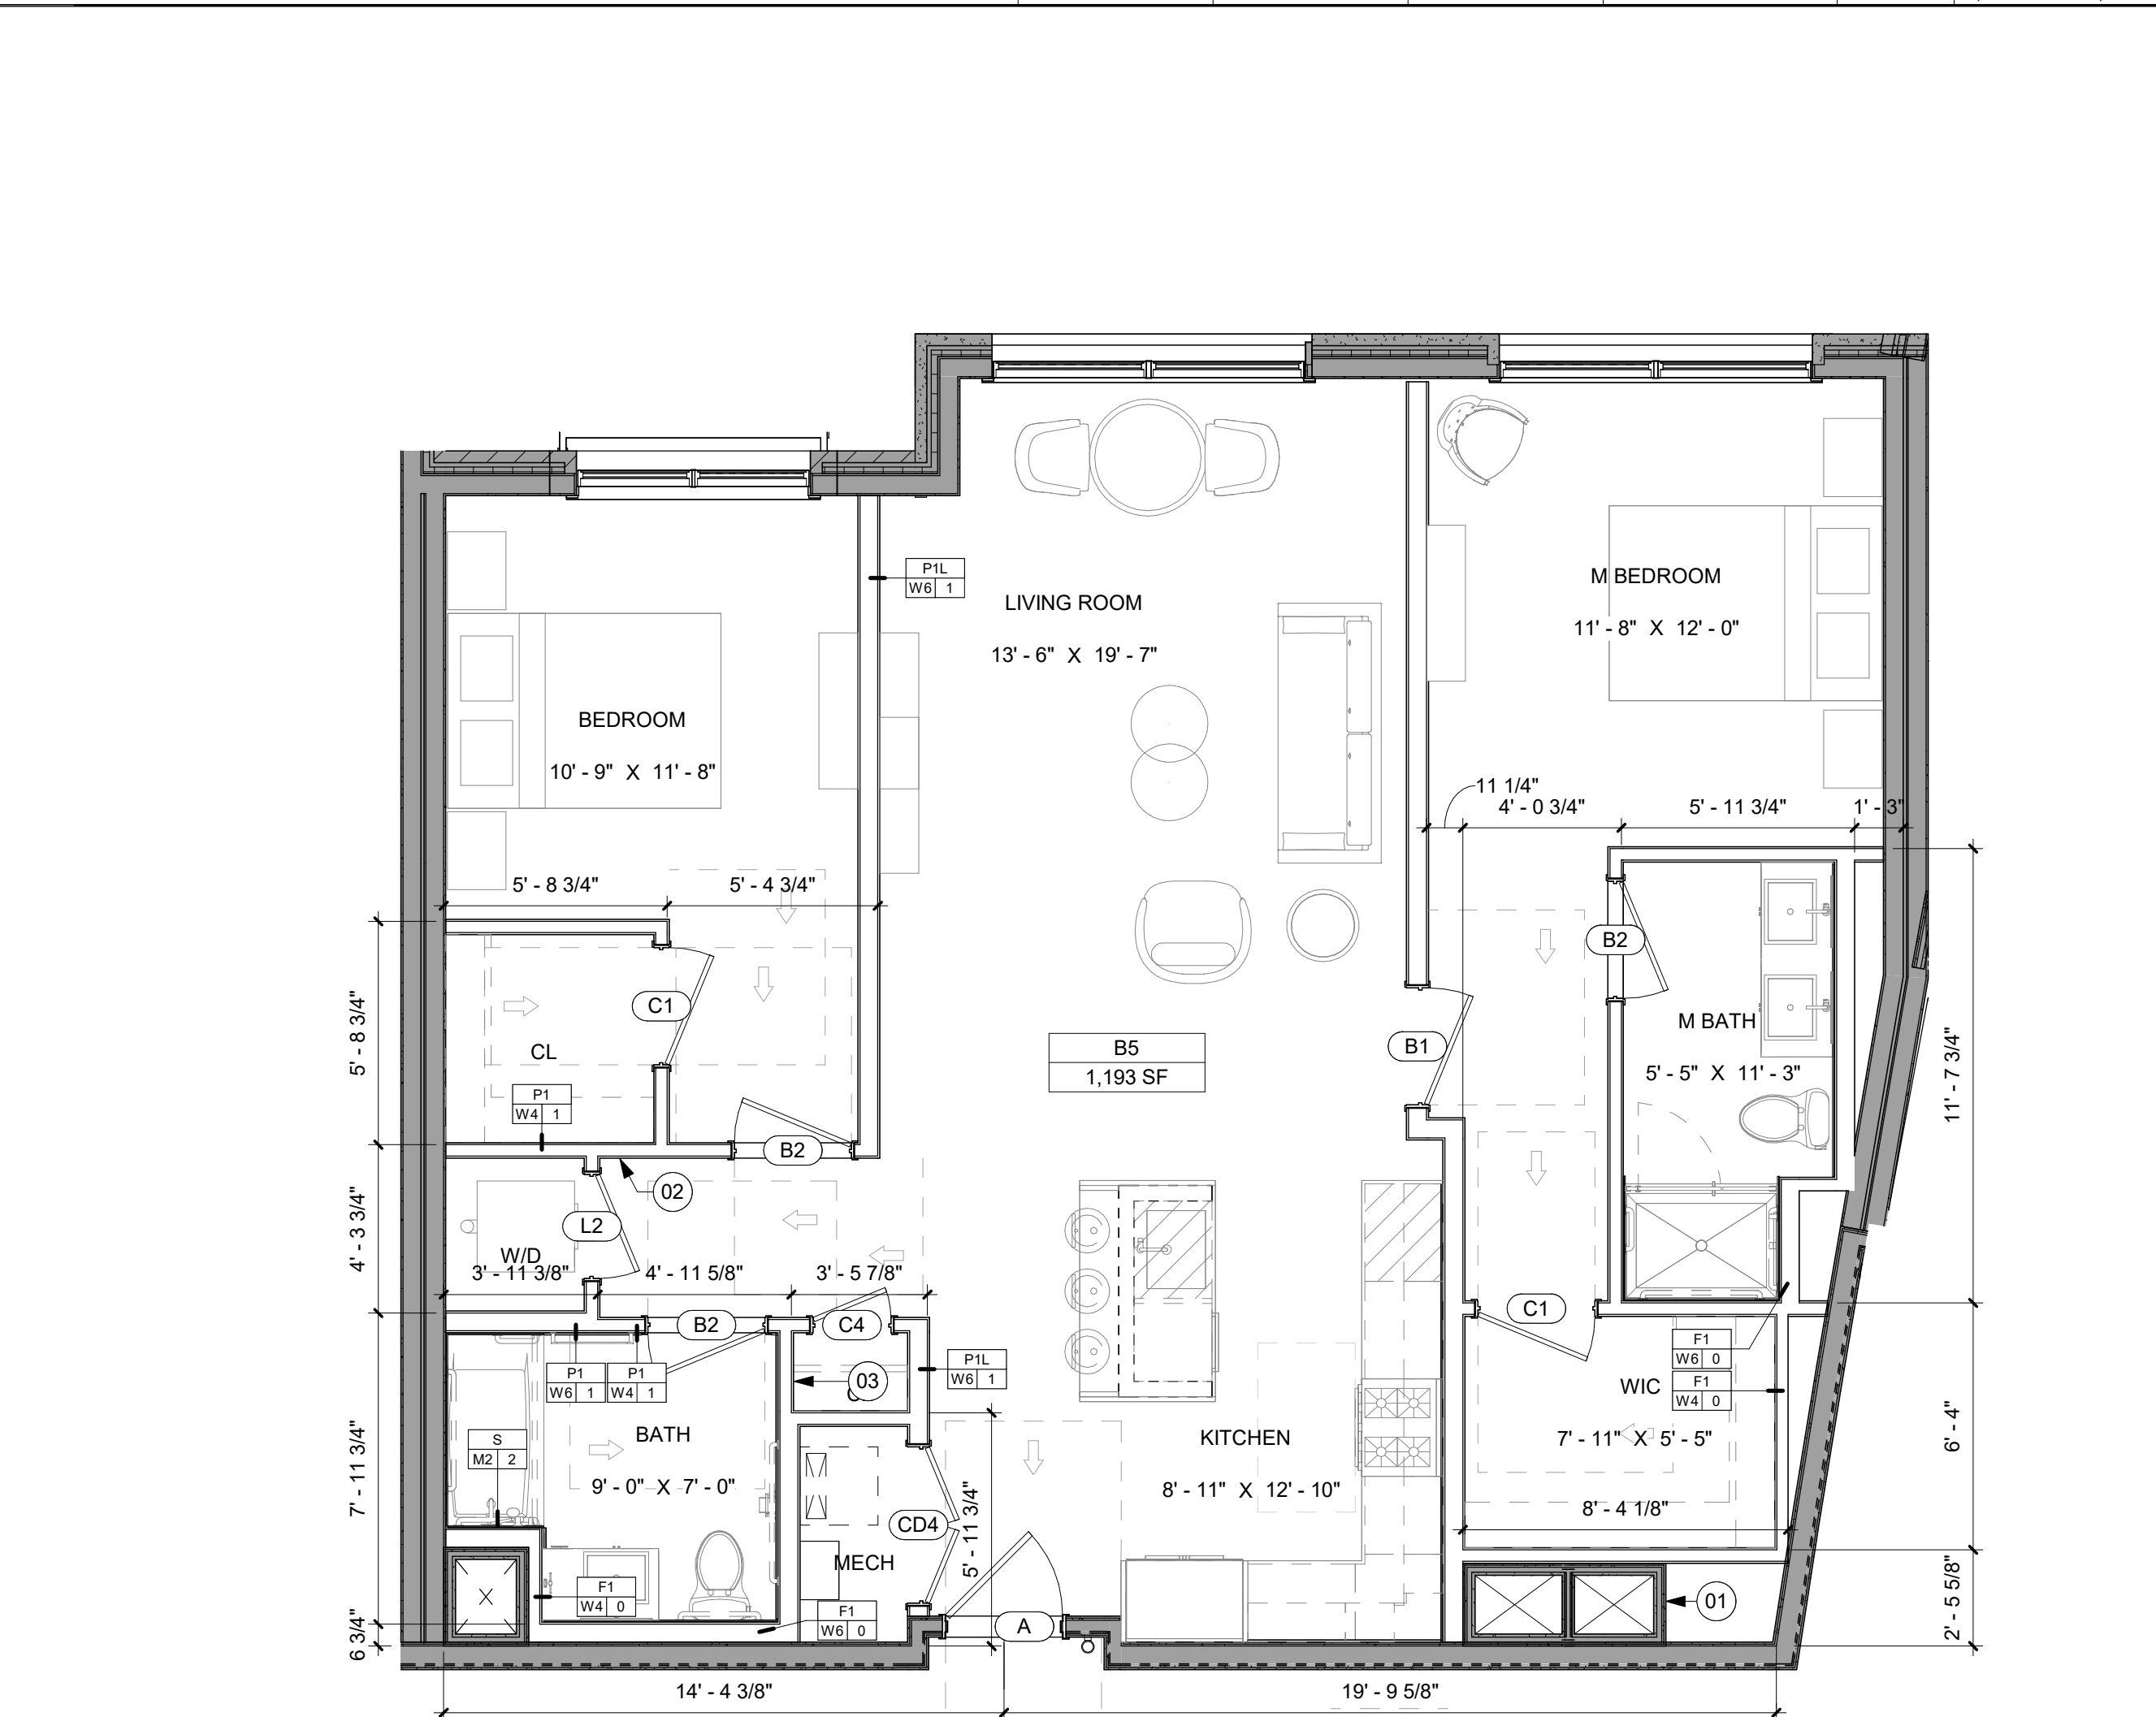

3 UNIT TYPE - B5
SCALE: 1/4" = 1'-0"

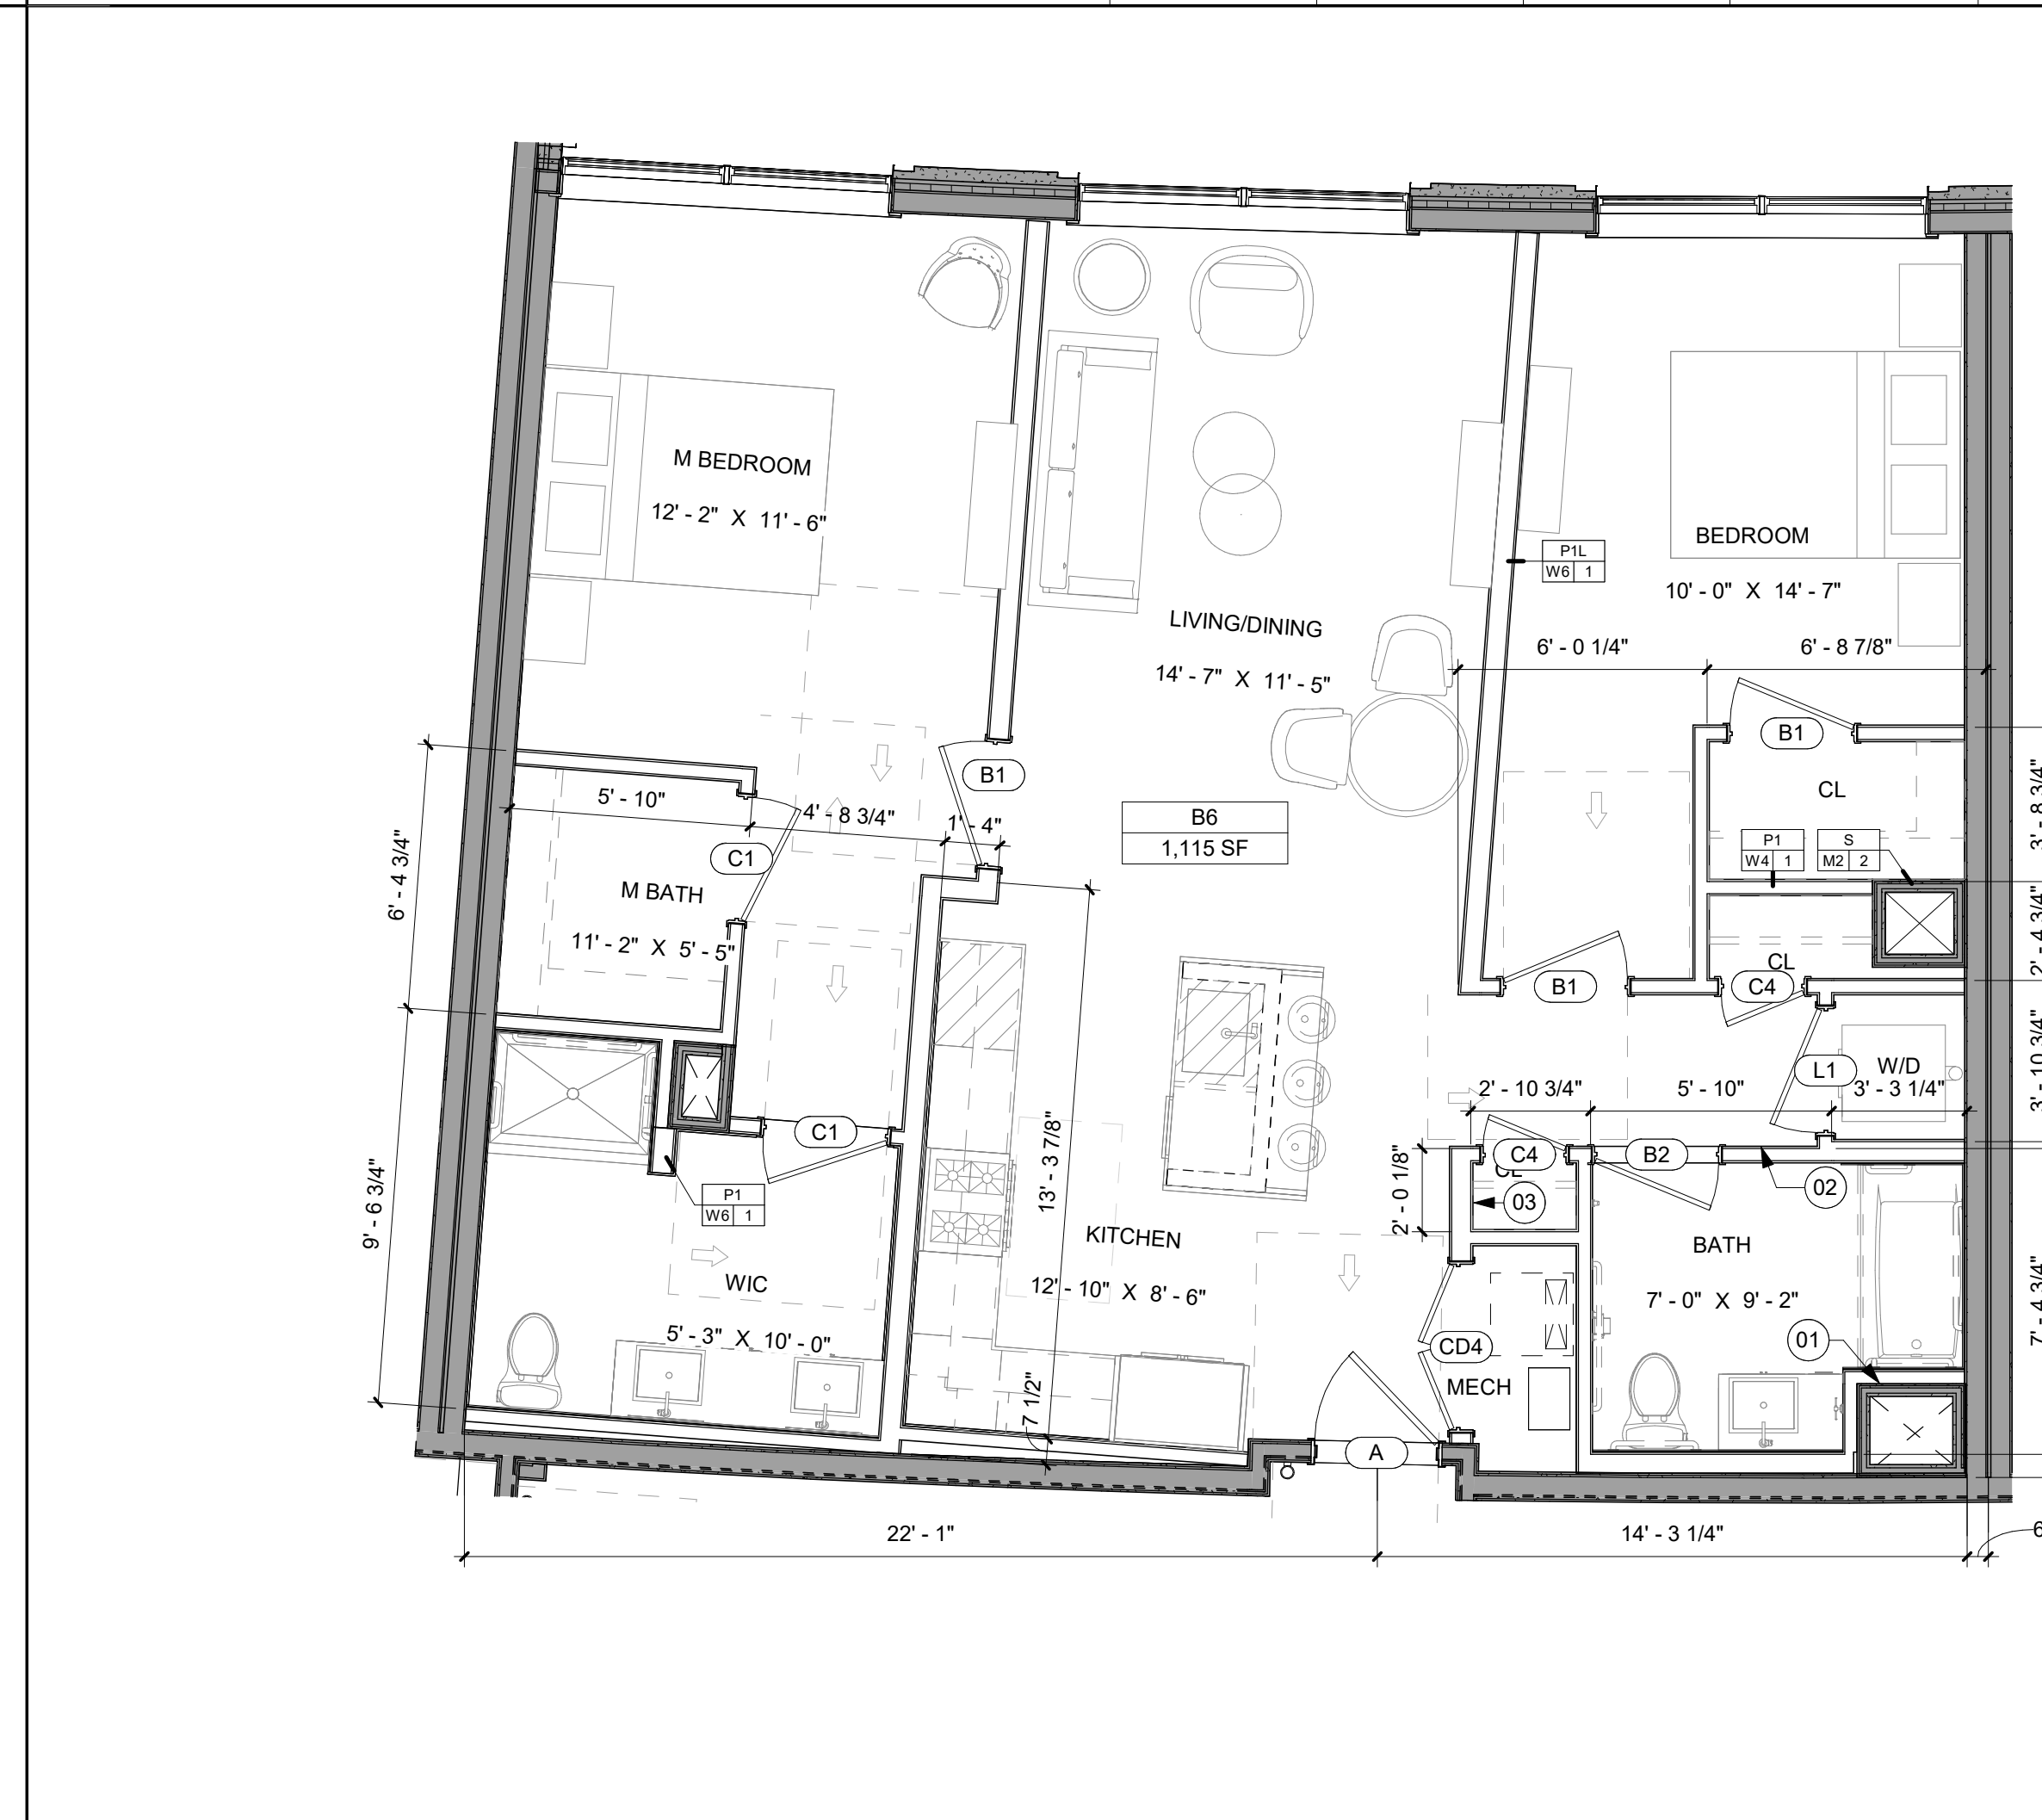

2 UNIT TYPE - B6
SCALE: 1/4" = 1'-0"

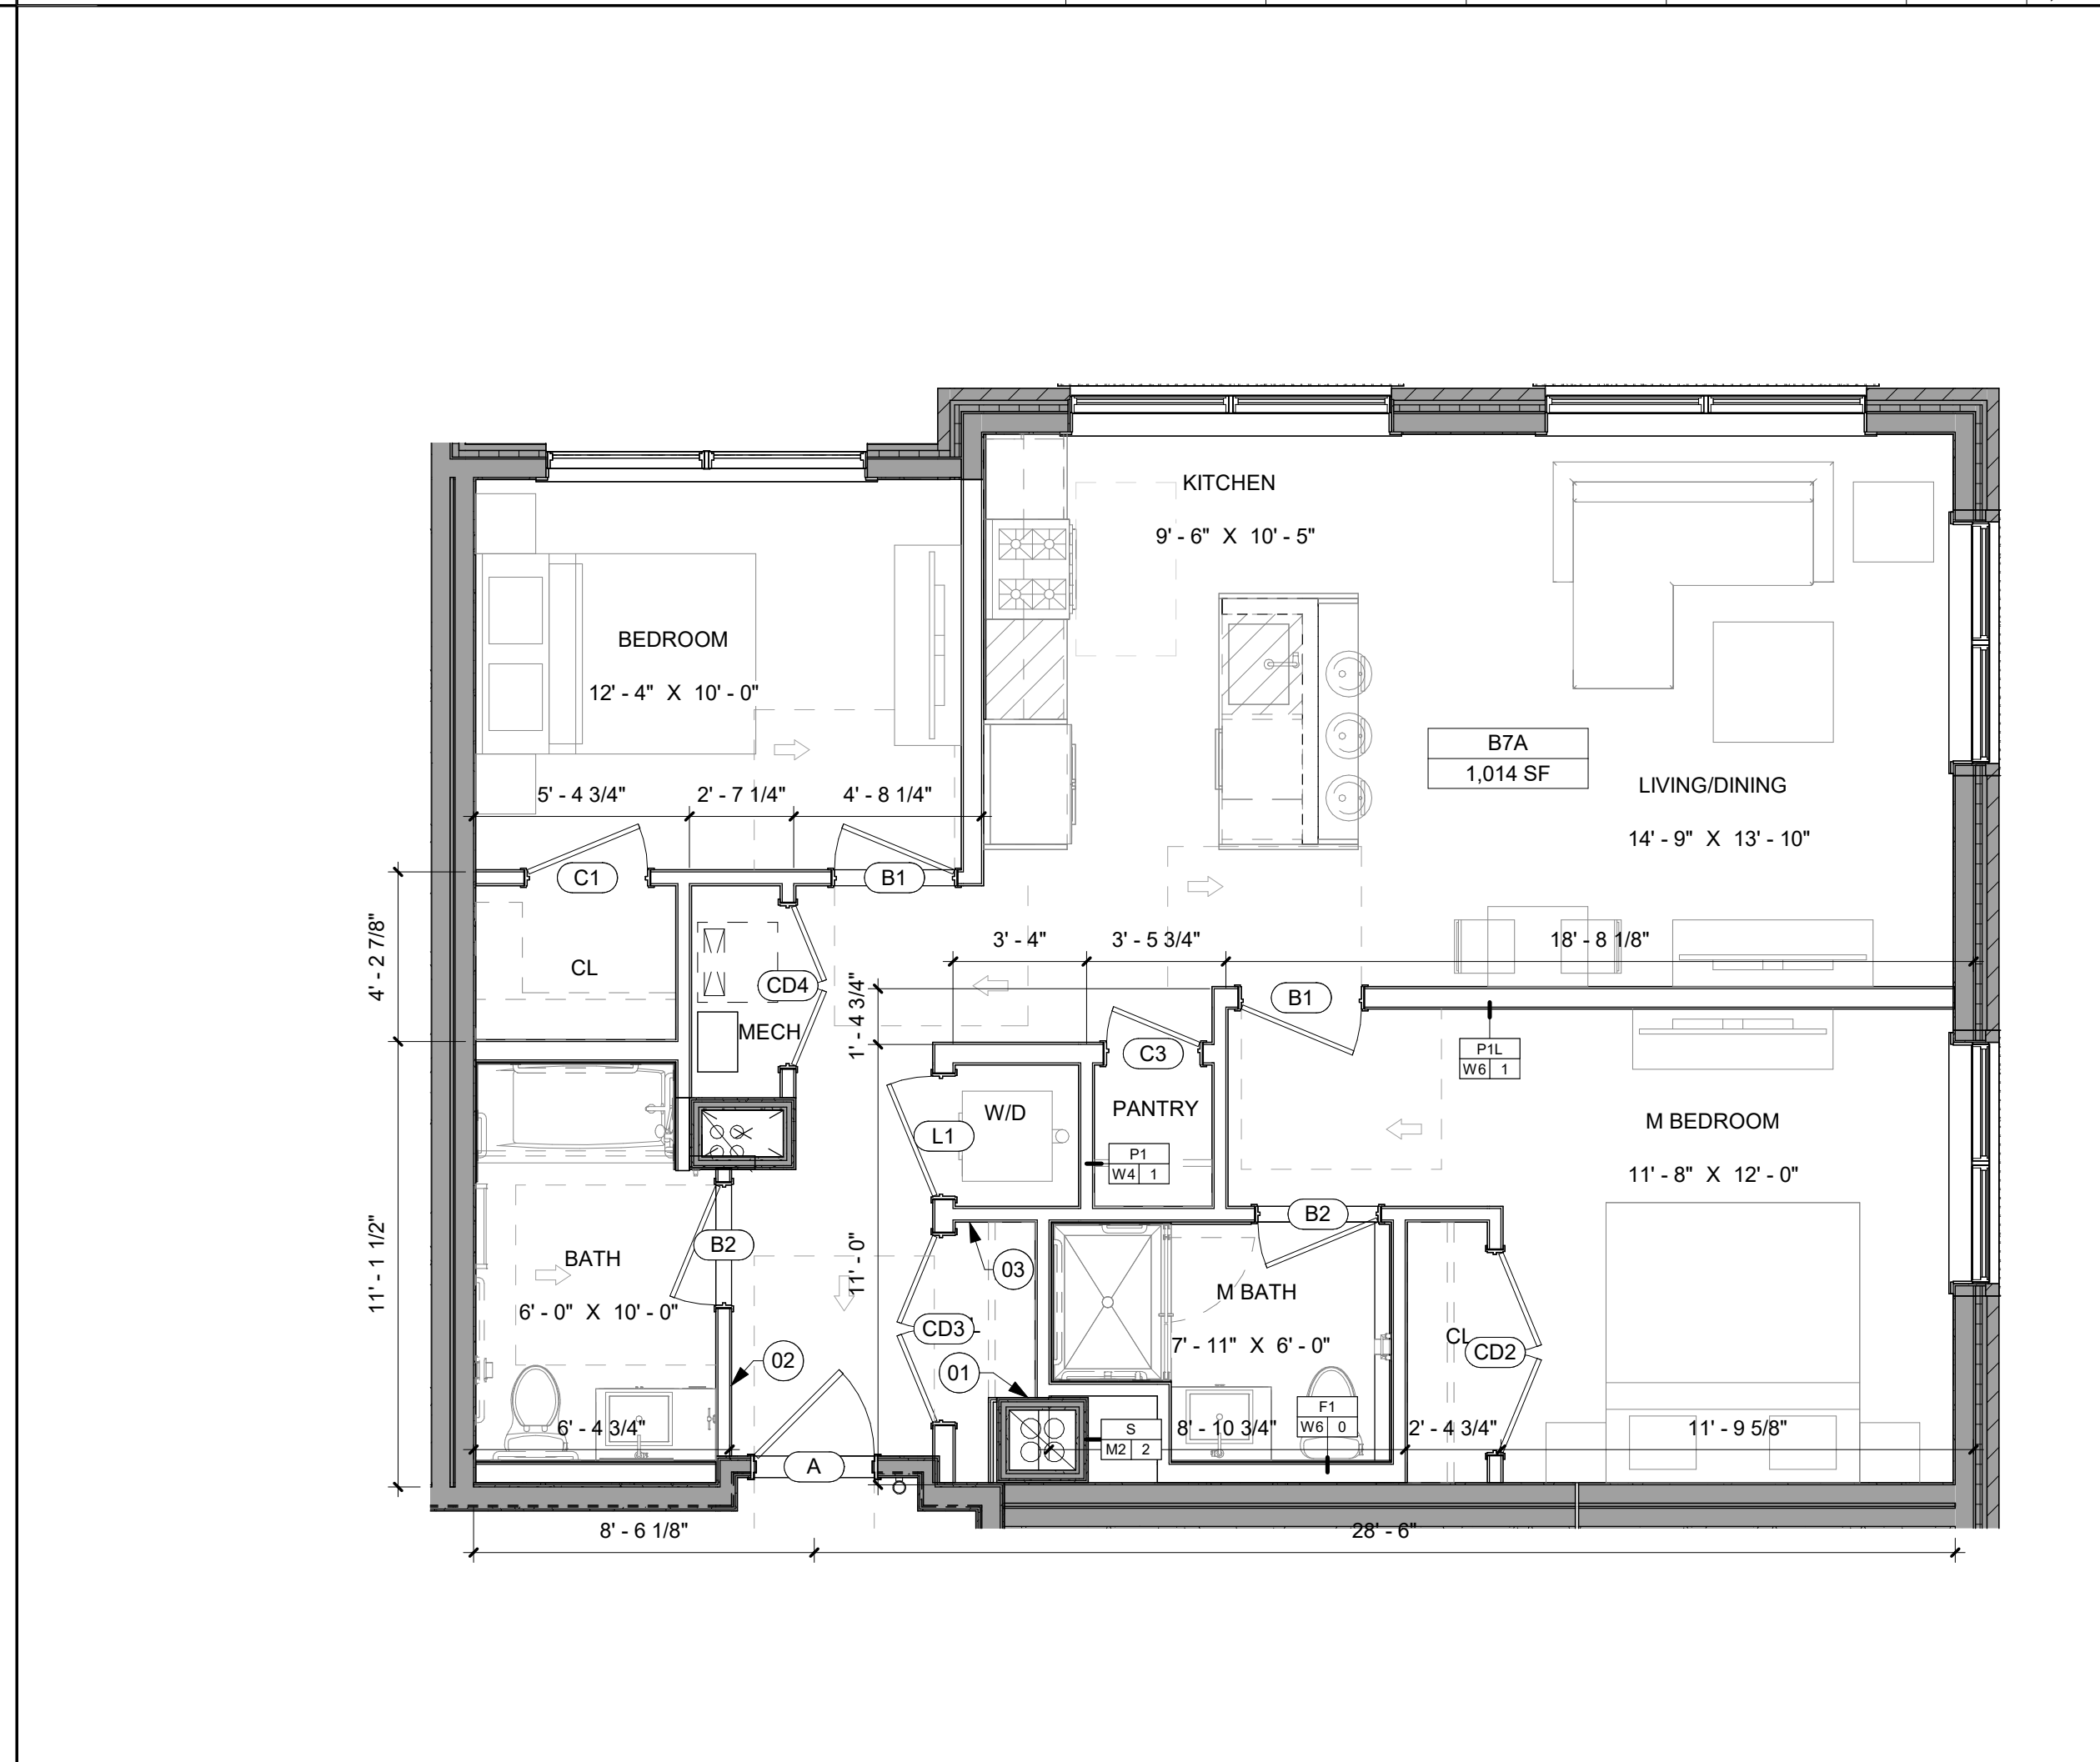

1 UNIT TYPE - B7A - AFF
SCALE: 1/4" = 1'-0"

- UNIT PLAN NOTES
- ALL INTERIOR DIMENSIONS TO WOOD FRAME PARTITIONS ARE TO FACE OF FRAMING. ALL INTERIOR DIMENSIONS TO METAL FRAME PARTITIONS ARE TO FACE OF FINISH AND ARE NOTED WITH ASTERISKS "X". ALL OTHER DIMENSIONS ARE AS SHOWN.
 - ALL UNIT INTERIOR PARTITIONS TO BE WALL TYPE XX UNLESS OTHERWISE NOTED.
 - LOCATE DOOR OPENINGS 4" FROM ADJACENT WALL UNLESS OTHERWISE NOTED.
 - SEE MECHANICAL AND PLUMBING DRAWINGS FOR EQUIPMENT SPECIFICATIONS.
 - SEE ELECTRICAL AND LOW VOLTAGE DRAWINGS FOR POWER AND LOW VOLTAGE PLANS.

KEYNOTES

#	DESCRIPTION
01	MECH. CHASE REF. MEP DRAWINGS
02	ELECTRICAL LOAD CENTER. REFER TO ELEC. DRAWINGS
03	IND BOX REF. TO ELEC. FOR MORE INFO
04	WALL RETURN REF. TO ELEC. DRAWINGS

Dean Marchetto, FAIA, PP
NJ 07045
Michael Higgins, AIA, LEED
NJ21AID135830
Bruce A. Stone, AIA
NJ21AID137110
Michael Buldo, AIA
NJ21AID1788800
NY 035161
Vincent Marchetto, AIA
NJ21AID2151600

1422 Grand Street
Suite 5b
Hoboken, NJ 07030
T.201-795-1505
MHSArchitecture.com

PROJECT NAME:
MORRISTOWN GREEN APARTMENTS
22 LAFAYETTE AVENUE
TOWN OF MORRISTOWN, NEW JERSEY

PREPARED FOR:
MORRISTOWN ASSOCIATES LLC
4 CUNNINGHAM DRIVE
WEST ORANGE, NJ

ISSUE

#	DATE	FOR:
1	06/03/2026	BID SET
2	07/09/26	ADDENDUM #1

ENLARGED UNIT PLANS - 2 BR

PROJECT NUMBER:	2202
SCALE:	As indicated
DRAWN BY:	CM / TM / JE
CHECKED BY:	FT / MB

A09.06

Copyright © 2026 MHS Architecture