
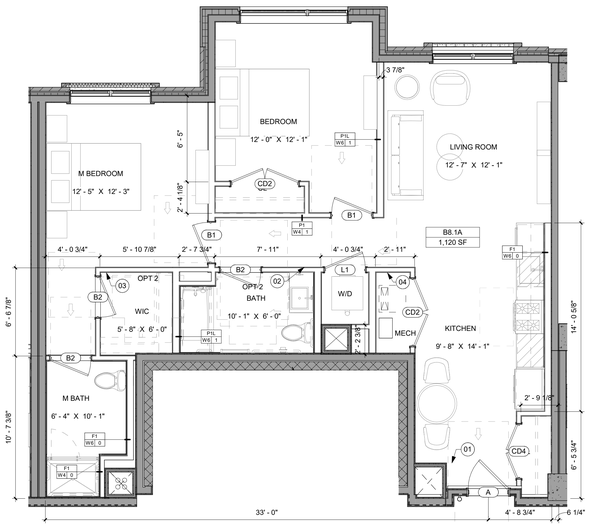



8 RCP - UNIT TYPE B8.1A
SCALE: 1/4" = 1'-0"

UNIT TYPE	KITCHEN TYPE	BATHROOM TYPE	M BATHROOM TYPE	COUNT	AREA
B8.1A	K8	B2	B12	1	1,120 SF

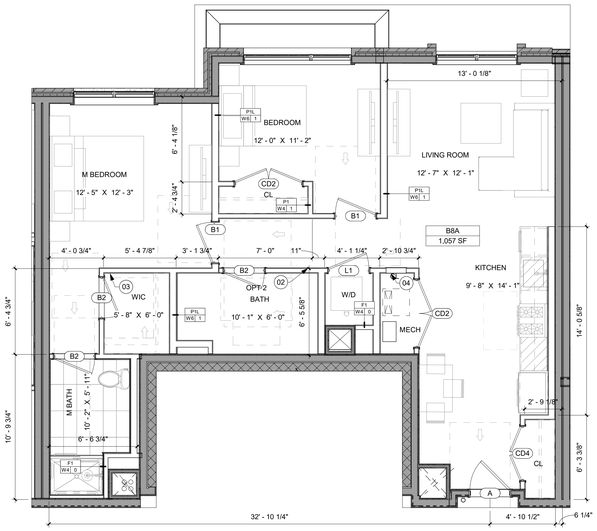

7 UNIT TYPE - B8A
SCALE: 1/4" = 1'-0"

UNIT TYPE	KITCHEN TYPE	BATHROOM TYPE	M BATHROOM TYPE	COUNT	AREA
B8A	K8	B2	B12	2	1,056 SF ... 1,057 SF

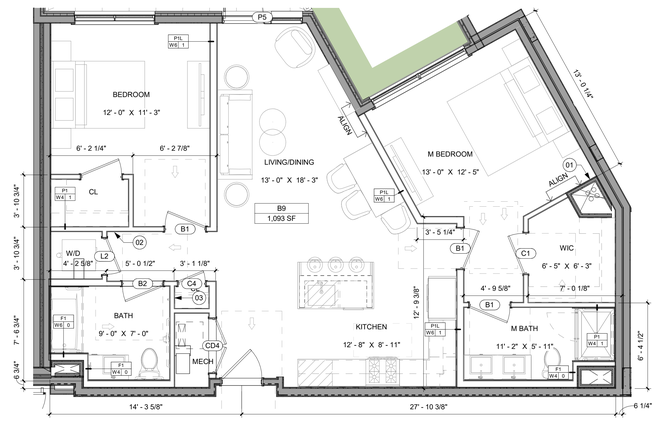

6 UNIT TYPE - B9
SCALE: 1/4" = 1'-0"


UNIT TYPE	KITCHEN TYPE	BATHROOM TYPE	M BATHROOM TYPE	COUNT	AREA
B9	K2	B1	B5	1	1,093 SF

UNIT PLAN NOTES

1. ALL INTERIOR DIMENSIONS TO WOOD FRAME PARTITIONS ARE TO FACE OF FRAMING. ALL INTERIOR DIMENSIONS TO METAL FRAME PARTITIONS ARE TO FACE OF FINISH AND ARE NOTED WITH ASTERIKS "X" - X"". ALL OTHER DIMENSIONS ARE AS SHOWN.
2. ALL UNIT INTERIOR PARTITIONS TO BE WALL TYPE XX UNLESS OTHERWISE NOTED.
3. LOCATE DOOR OPENINGS 4" FROM ADJACENT WALL UNLESS OTHERWISE NOTED.
4. SEE MECHANICAL AND PLUMBING DRAWINGS FOR EQUIPMENT SPECIFICATIONS.
5. SEE ELECTRICAL AND LOW VOLTAGE DRAWINGS FOR POWER AND LOW VOLTAGE PLANS.


KEYNOTES

#	DESCRIPTION
01	MECH. CHASE REF. M/P DRAWINGS
02	ELECTRICAL LOAD CENTER. REFER TO ELEC. DRAWINGS
03	NID BOX REF. TO ELEC. FOR MORE INFO.
04	WALL RETURN REF TO ELEC. DRAWINGS

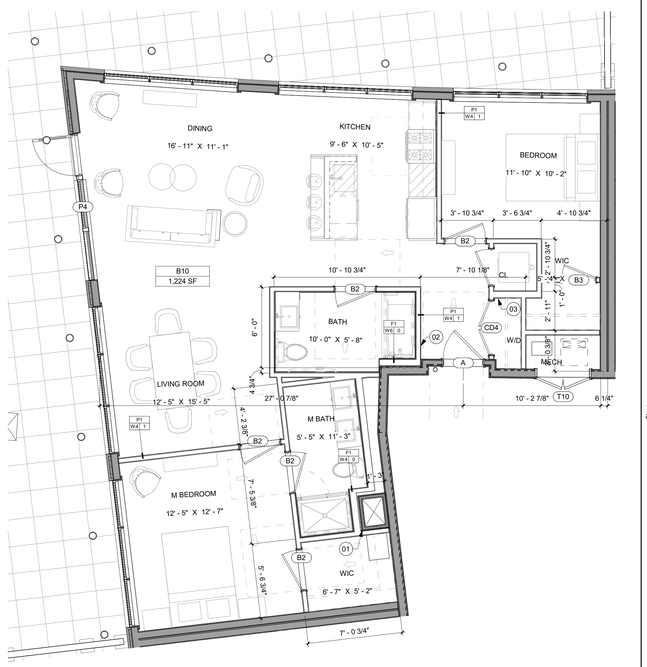


5 UNIT TYPE - B10
SCALE: 1/4" = 1'-0"

UNIT TYPE	KITCHEN TYPE	BATHROOM TYPE	M BATHROOM TYPE	COUNT	AREA
B10	K9	B9	B5	1	1,224 SF

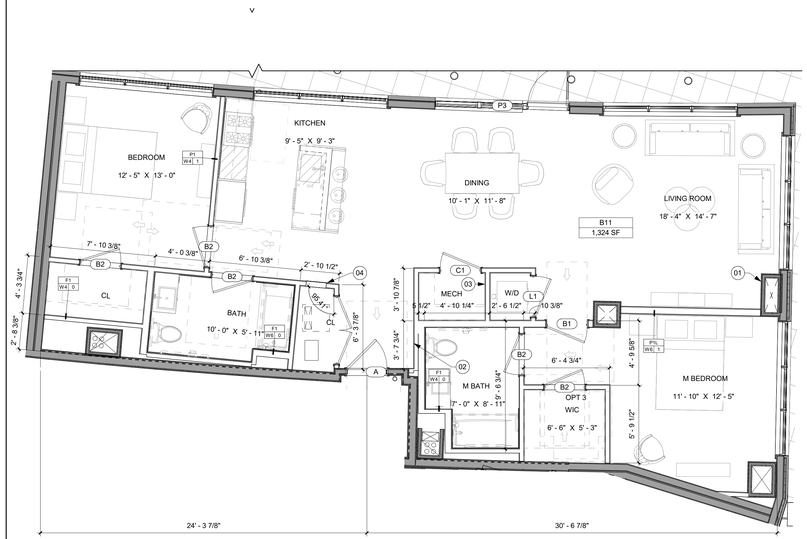


4 UNIT TYPE - B11
SCALE: 1/4" = 1'-0"

UNIT TYPE	KITCHEN TYPE	BATHROOM TYPE	M BATHROOM TYPE	COUNT	AREA
B11	K5	B9	B1	1	1,324 SF

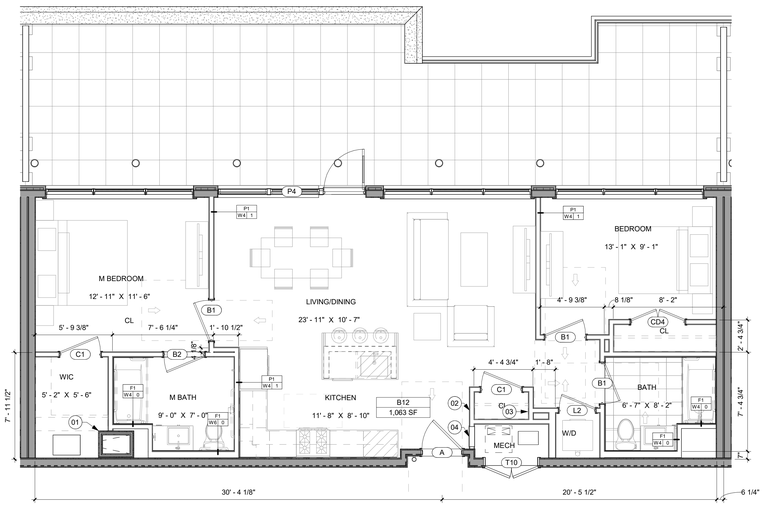


3 UNIT TYPE - B12
SCALE: 1/4" = 1'-0"

UNIT TYPE	KITCHEN TYPE	BATHROOM TYPE	M BATHROOM TYPE	COUNT	AREA
B12	K2	B8	B1	1	1,063 SF

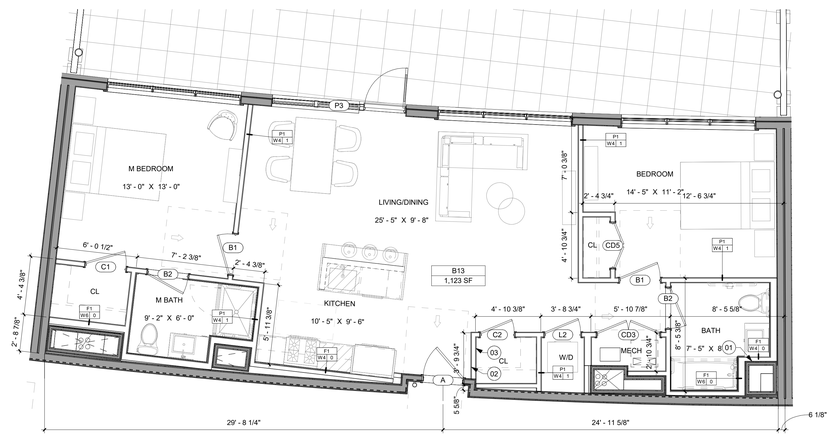

2 UNIT TYPE - B13
SCALE: 1/4" = 1'-0"

UNIT TYPE	KITCHEN TYPE	BATHROOM TYPE	M BATHROOM TYPE	COUNT	AREA
B13	K9	B10	B8	1	1,123 SF

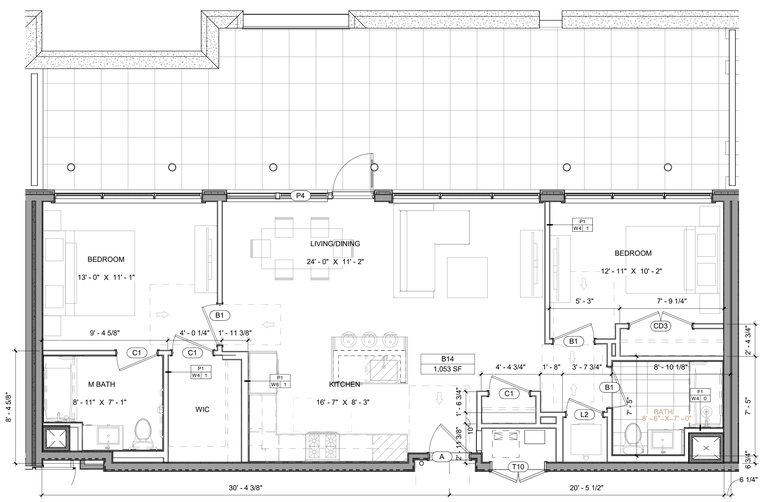

1 UNIT TYPE - B14
SCALE: 1/4" = 1'-0"

UNIT TYPE	KITCHEN TYPE	BATHROOM TYPE	M BATHROOM TYPE	COUNT	AREA
B14	K2	B8	B13	1	1,053 SF

MHS ARCHITECTURE

Dean Marchetto, FAIA, PP
NJ C07945
Michael Higgins, AIA, LEED
NJ21AI013083O
Bruce A Stieve, AIA
NJ21AI013710
Michael Buldo, AIA
NJ21AI01786800
NY 035161
Vincent Marchetto, AIA
NJ21AI02161600

1422 Grand Street
Suite 5b
Hoboken, NJ 07030

T 201-795-1505
MHSarchitecture.com

PROJECT NAME:
MORRISTOWN GREEN APARTMENTS
22 LAFAYETTE AVENUE
TOWN OF MORRISTOWN, NEW JERSEY

PREPARED FOR:
MORRISTOWN ASSOCIATES LLC
4 CUNNINGHAM DRIVE
WEST ORANGE, NJ

ISSUE

#	DATE:	FOR:
	06/03/2026	BID SET
1	07/09/26	ADDENDUM #1

ENLARGED UNIT PLANS - 2 BR

PROJECT NUMBER:	2202
SCALE:	As indicated
DRAWN BY:	CM / TM / JE
CHECKED BY:	FT / MB

A09.07

Copyright © 2026 MHS Architecture