



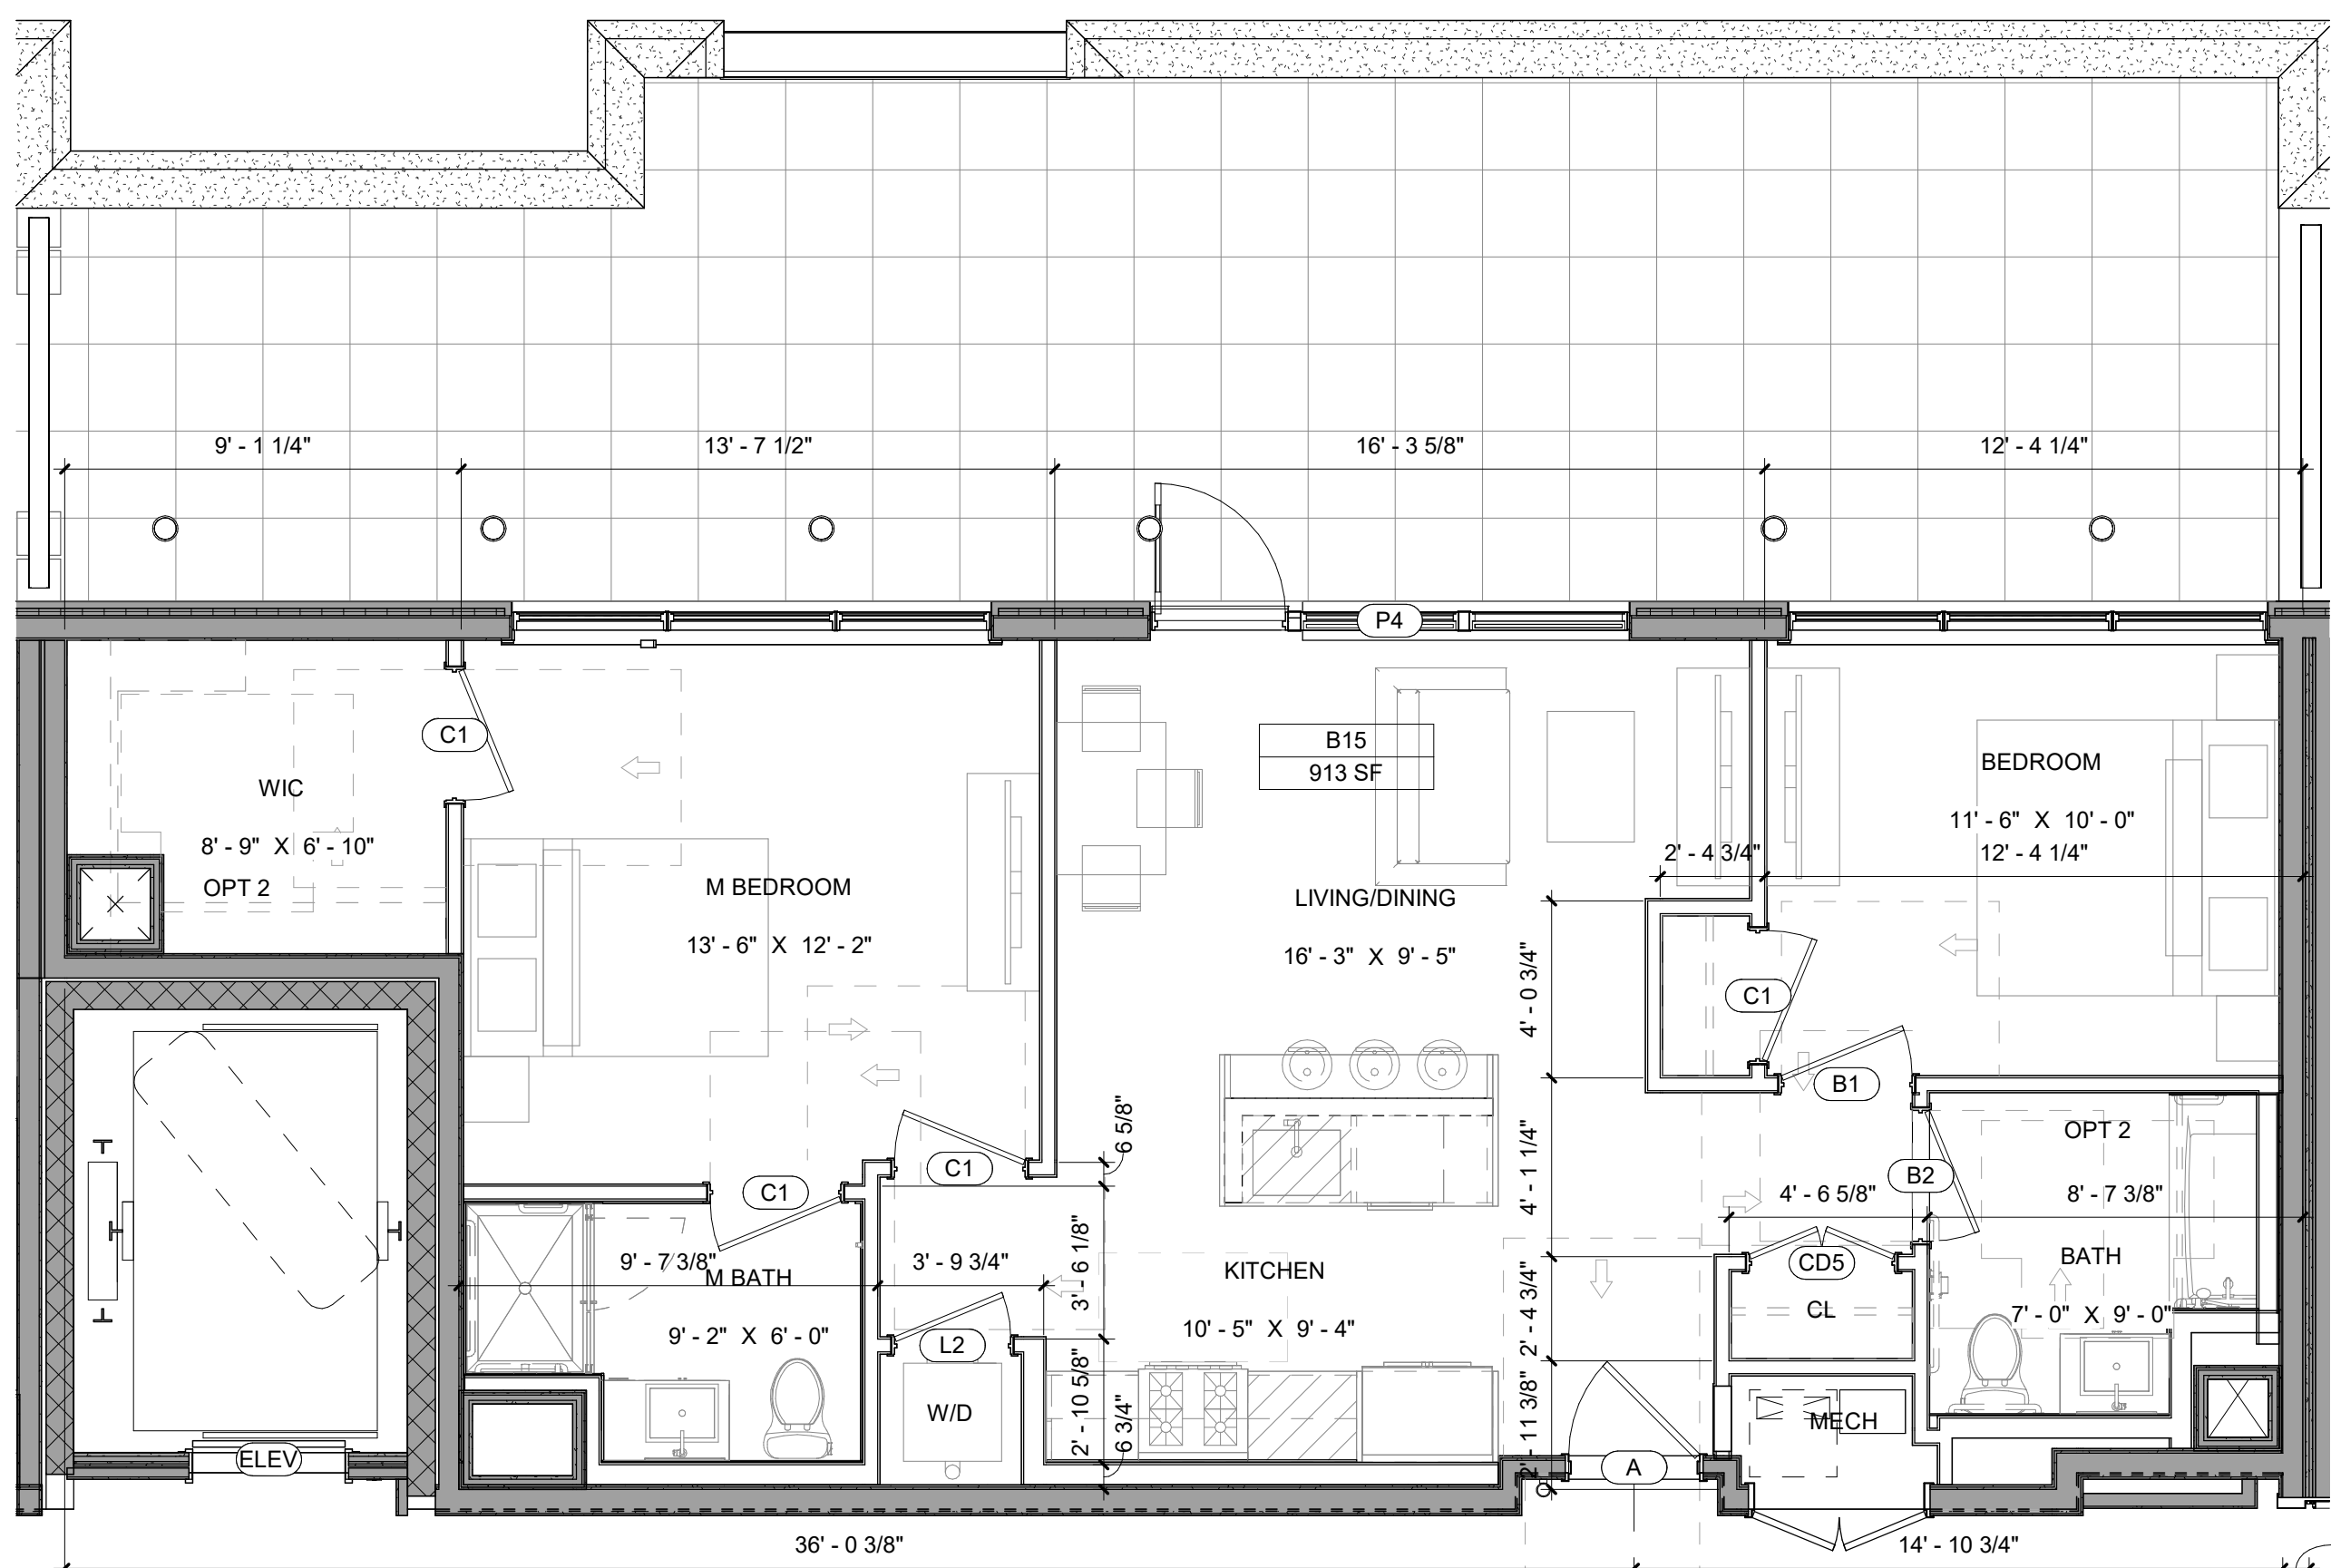


8 UNIT TYPE - B15
SCALE: 1/4" = 1'-0"

UNIT TYPE	KITCHEN TYPE	BATHROOM TYPE	M BATHROOM TYPE	COUNT	AREA
B15	K8	B6	B10	1	913 SF

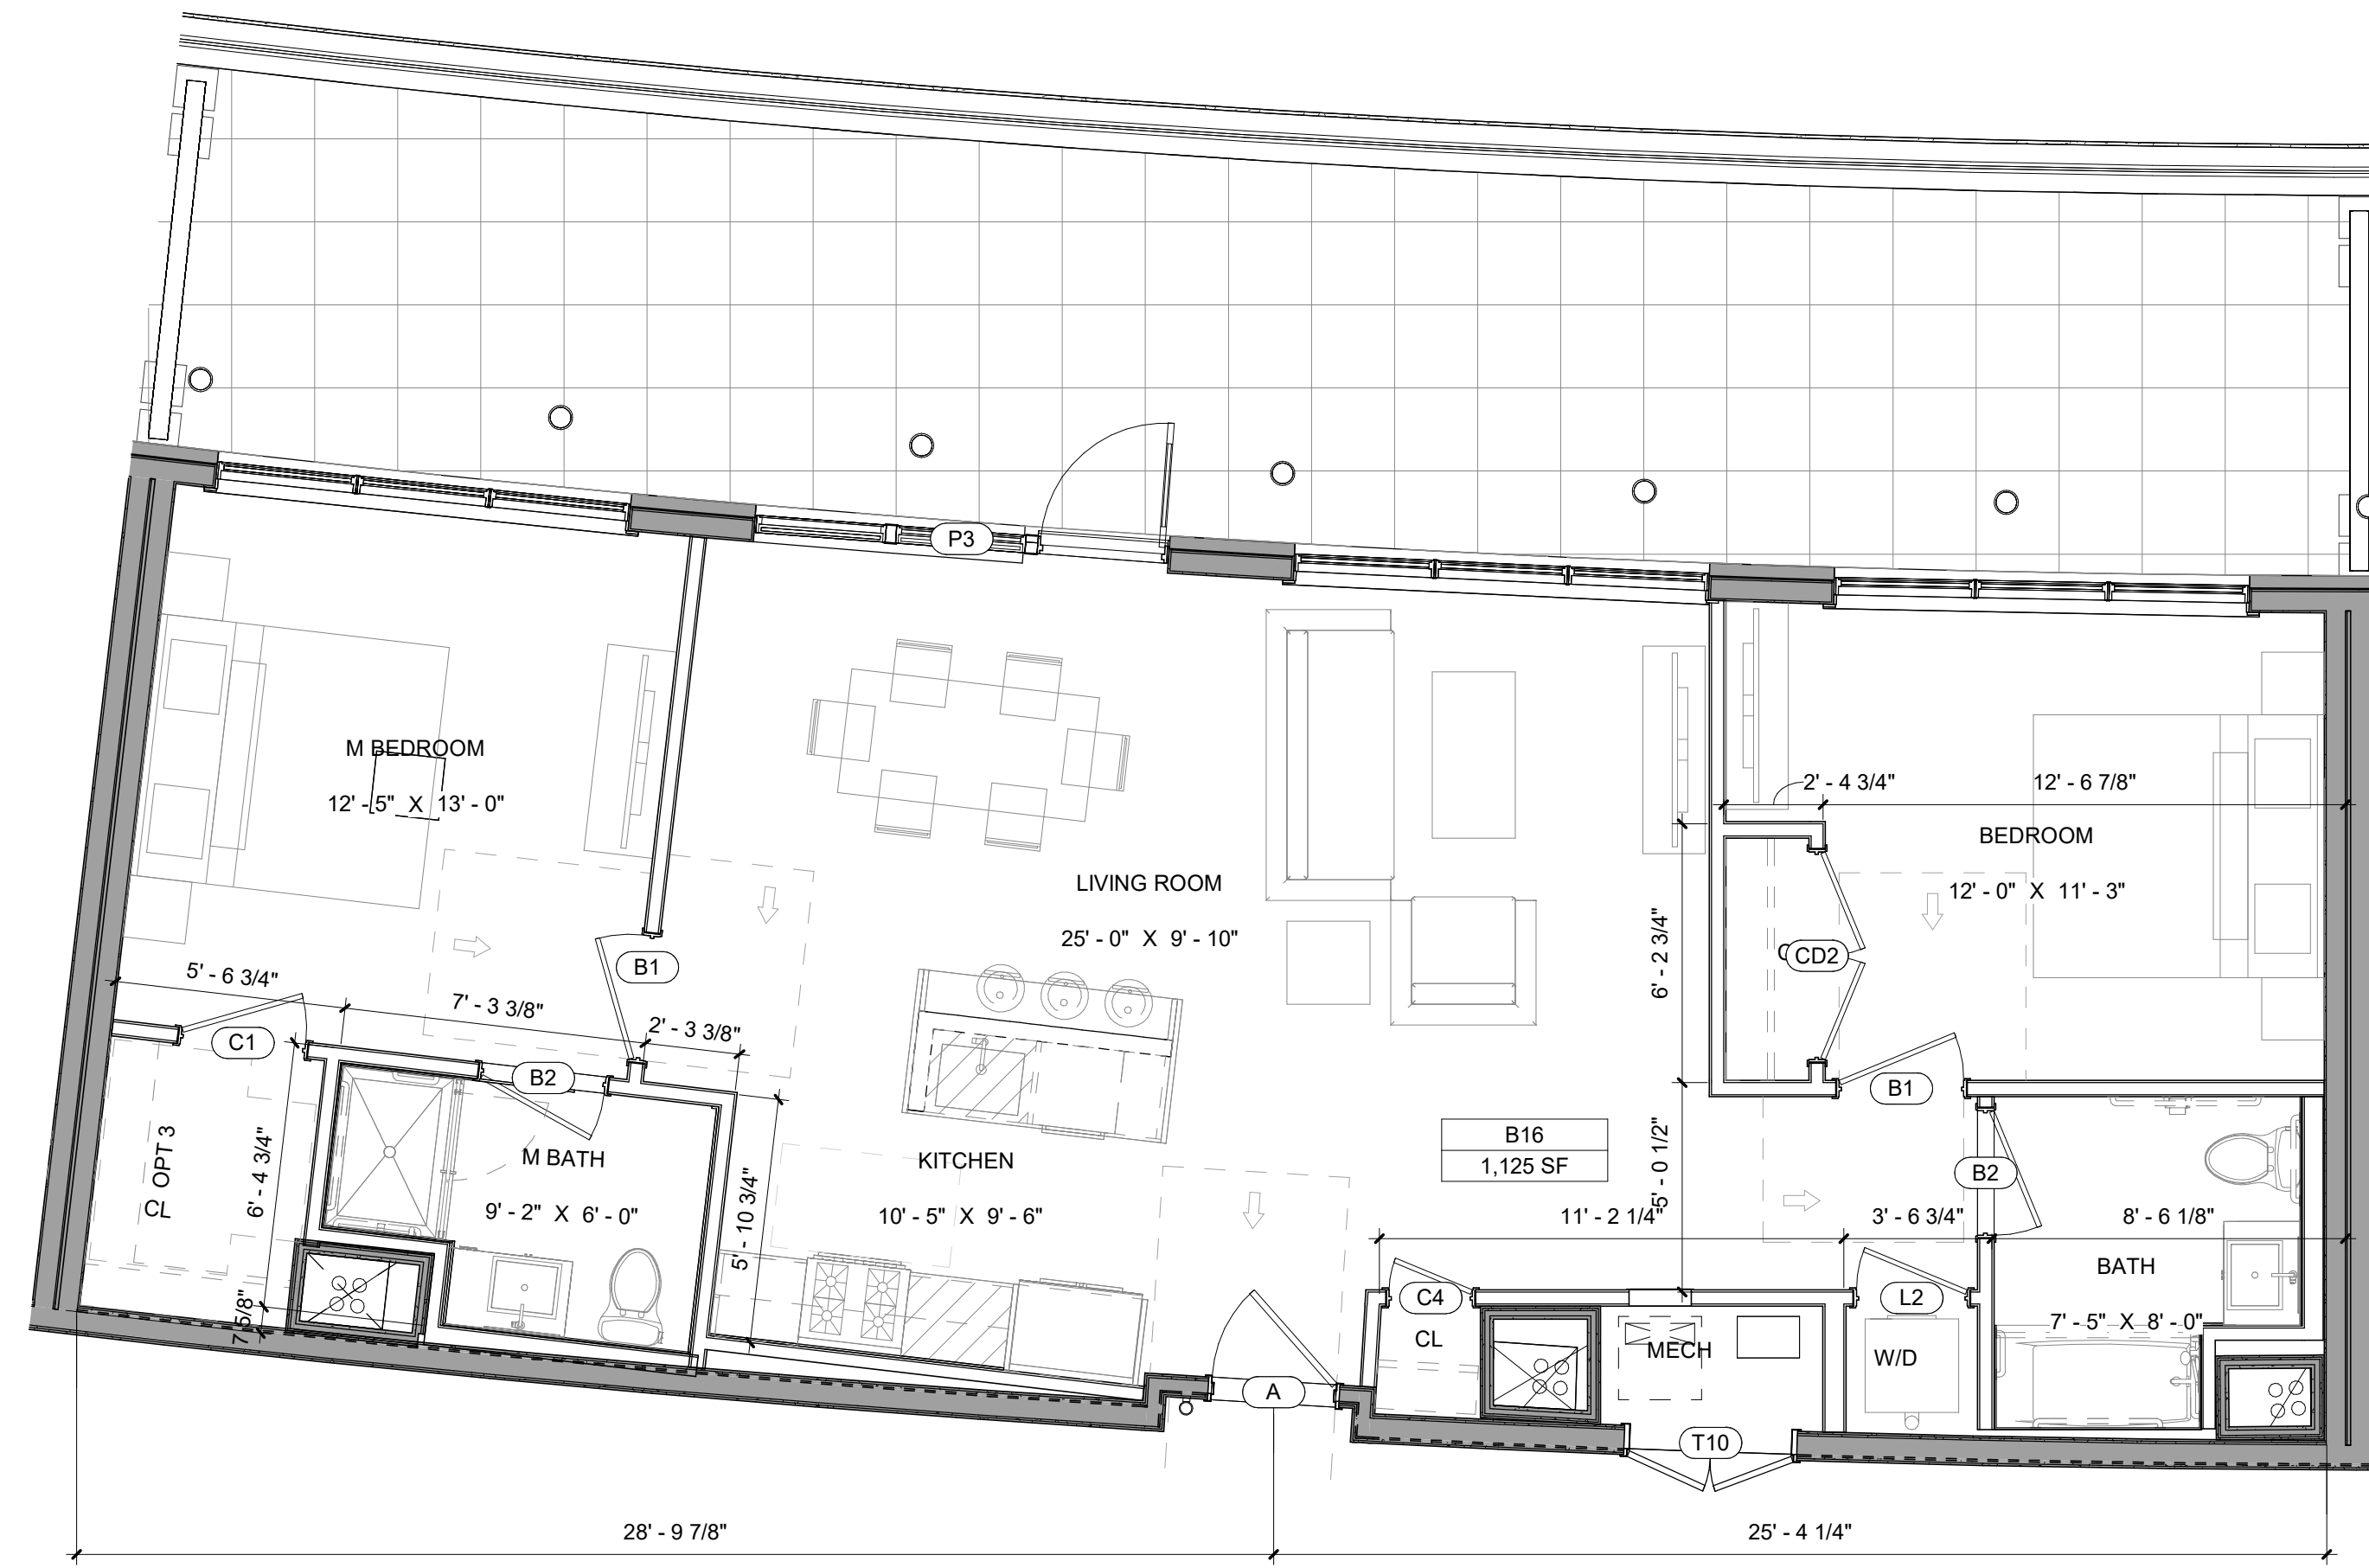


7 UNIT TYPE - B16
SCALE: 1/4" = 1'-0"

UNIT TYPE	KITCHEN TYPE	BATHROOM TYPE	M BATHROOM TYPE	COUNT	AREA
B16	K9	B10	B6	1	1,129 SF

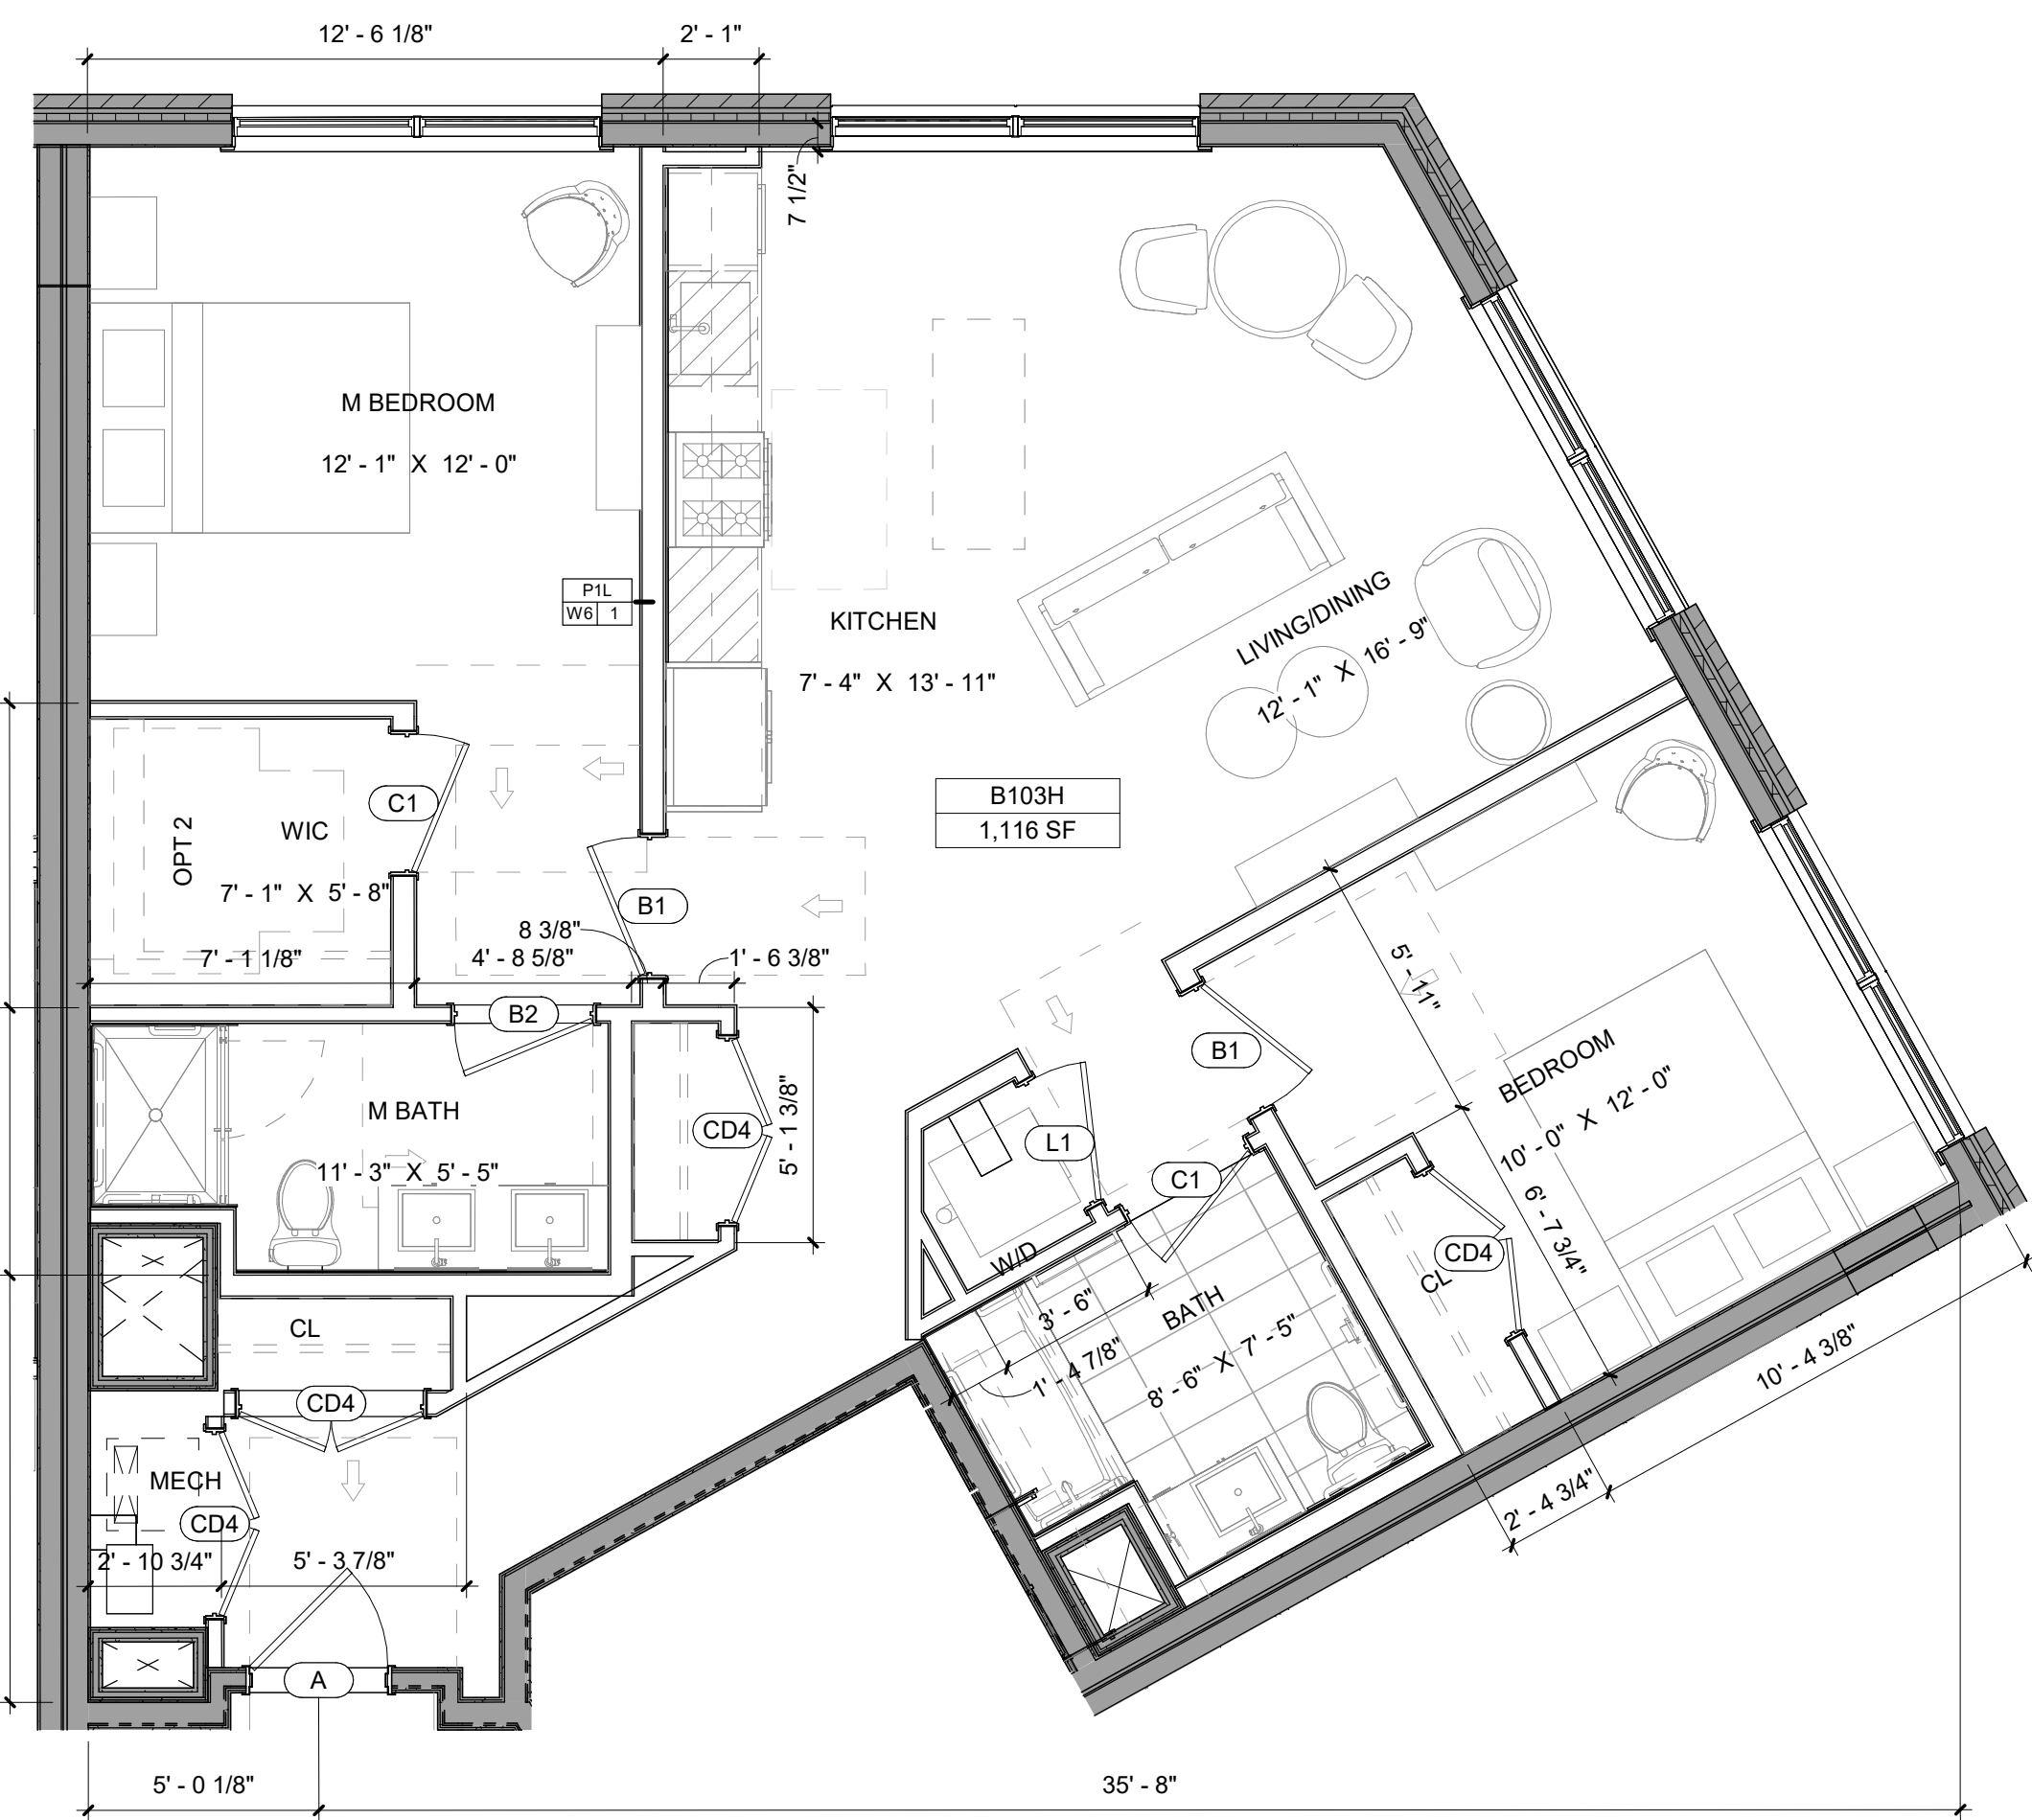


6 UNIT TYPE - B100H
SCALE: 1/4" = 1'-0"

NAME	KITCHEN TYPE	BATHROOM TYPE	M BATHROOM TYPE	COUNT	AREA
B100H	K8	B7	B6	3	1,198 SF

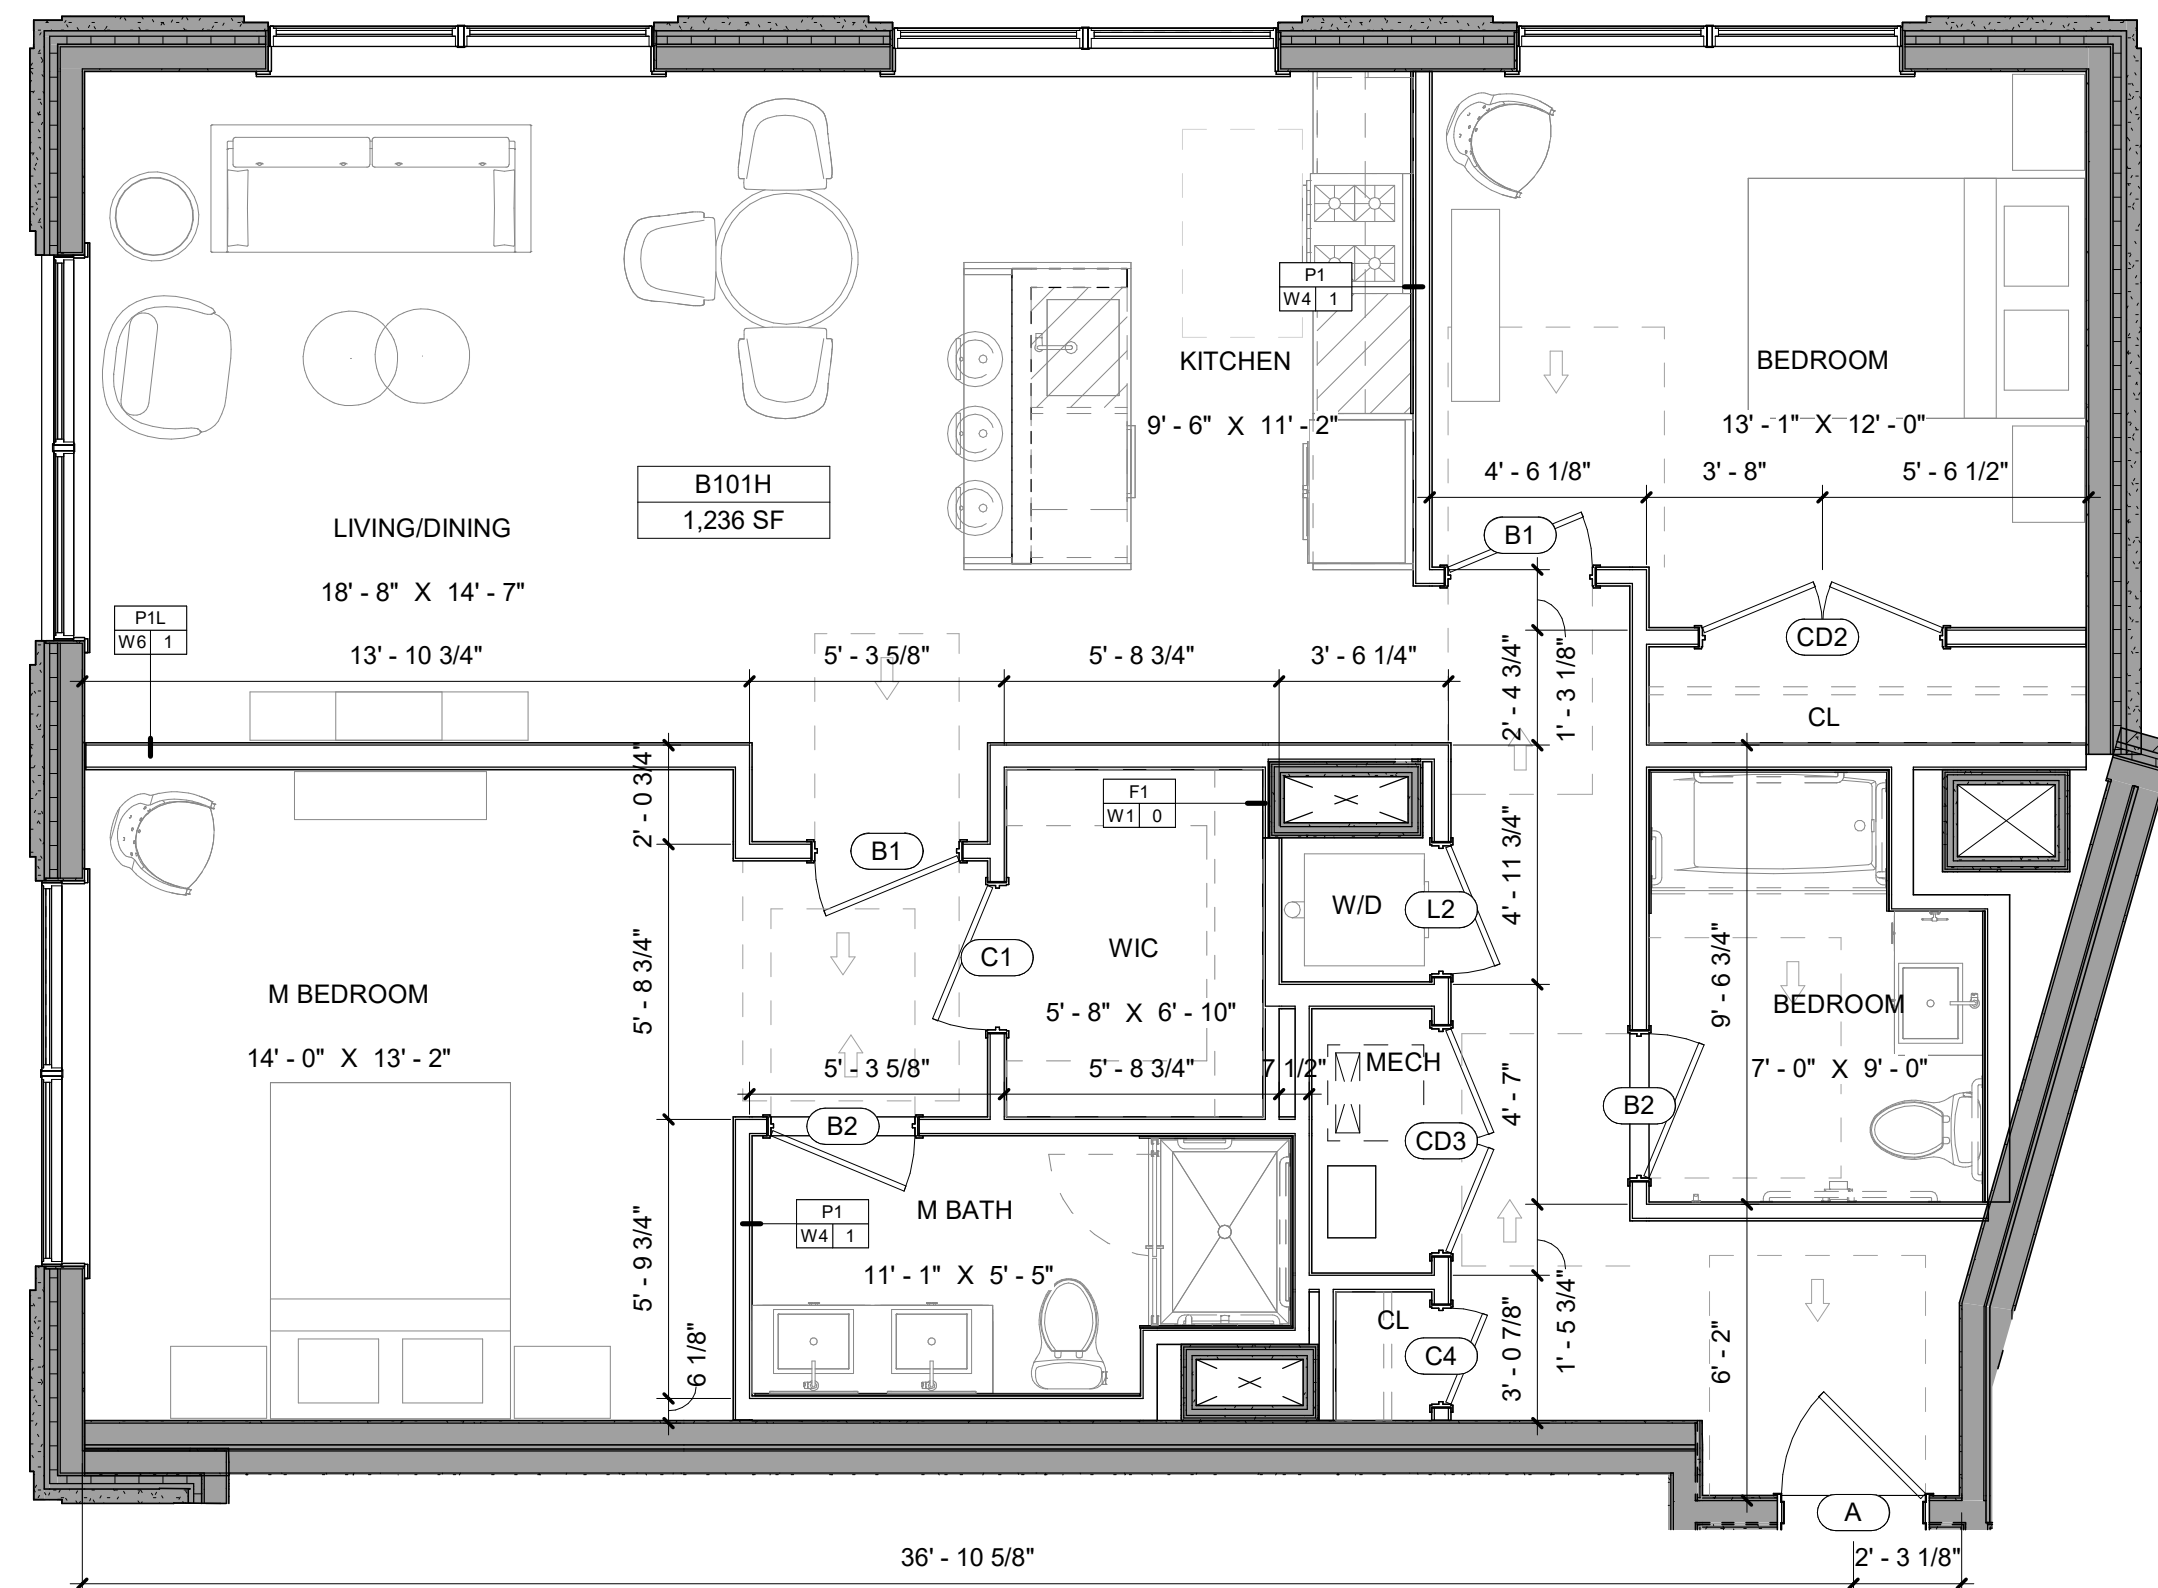


5 UNIT TYPE - B101H
SCALE: 1/4" = 1'-0"

UNIT TYPE	KITCHEN TYPE	BATHROOM TYPE	M BATHROOM TYPE	COUNT	AREA
B101H	K9	B1	B5	3	1,236 SF / 1,241 SF

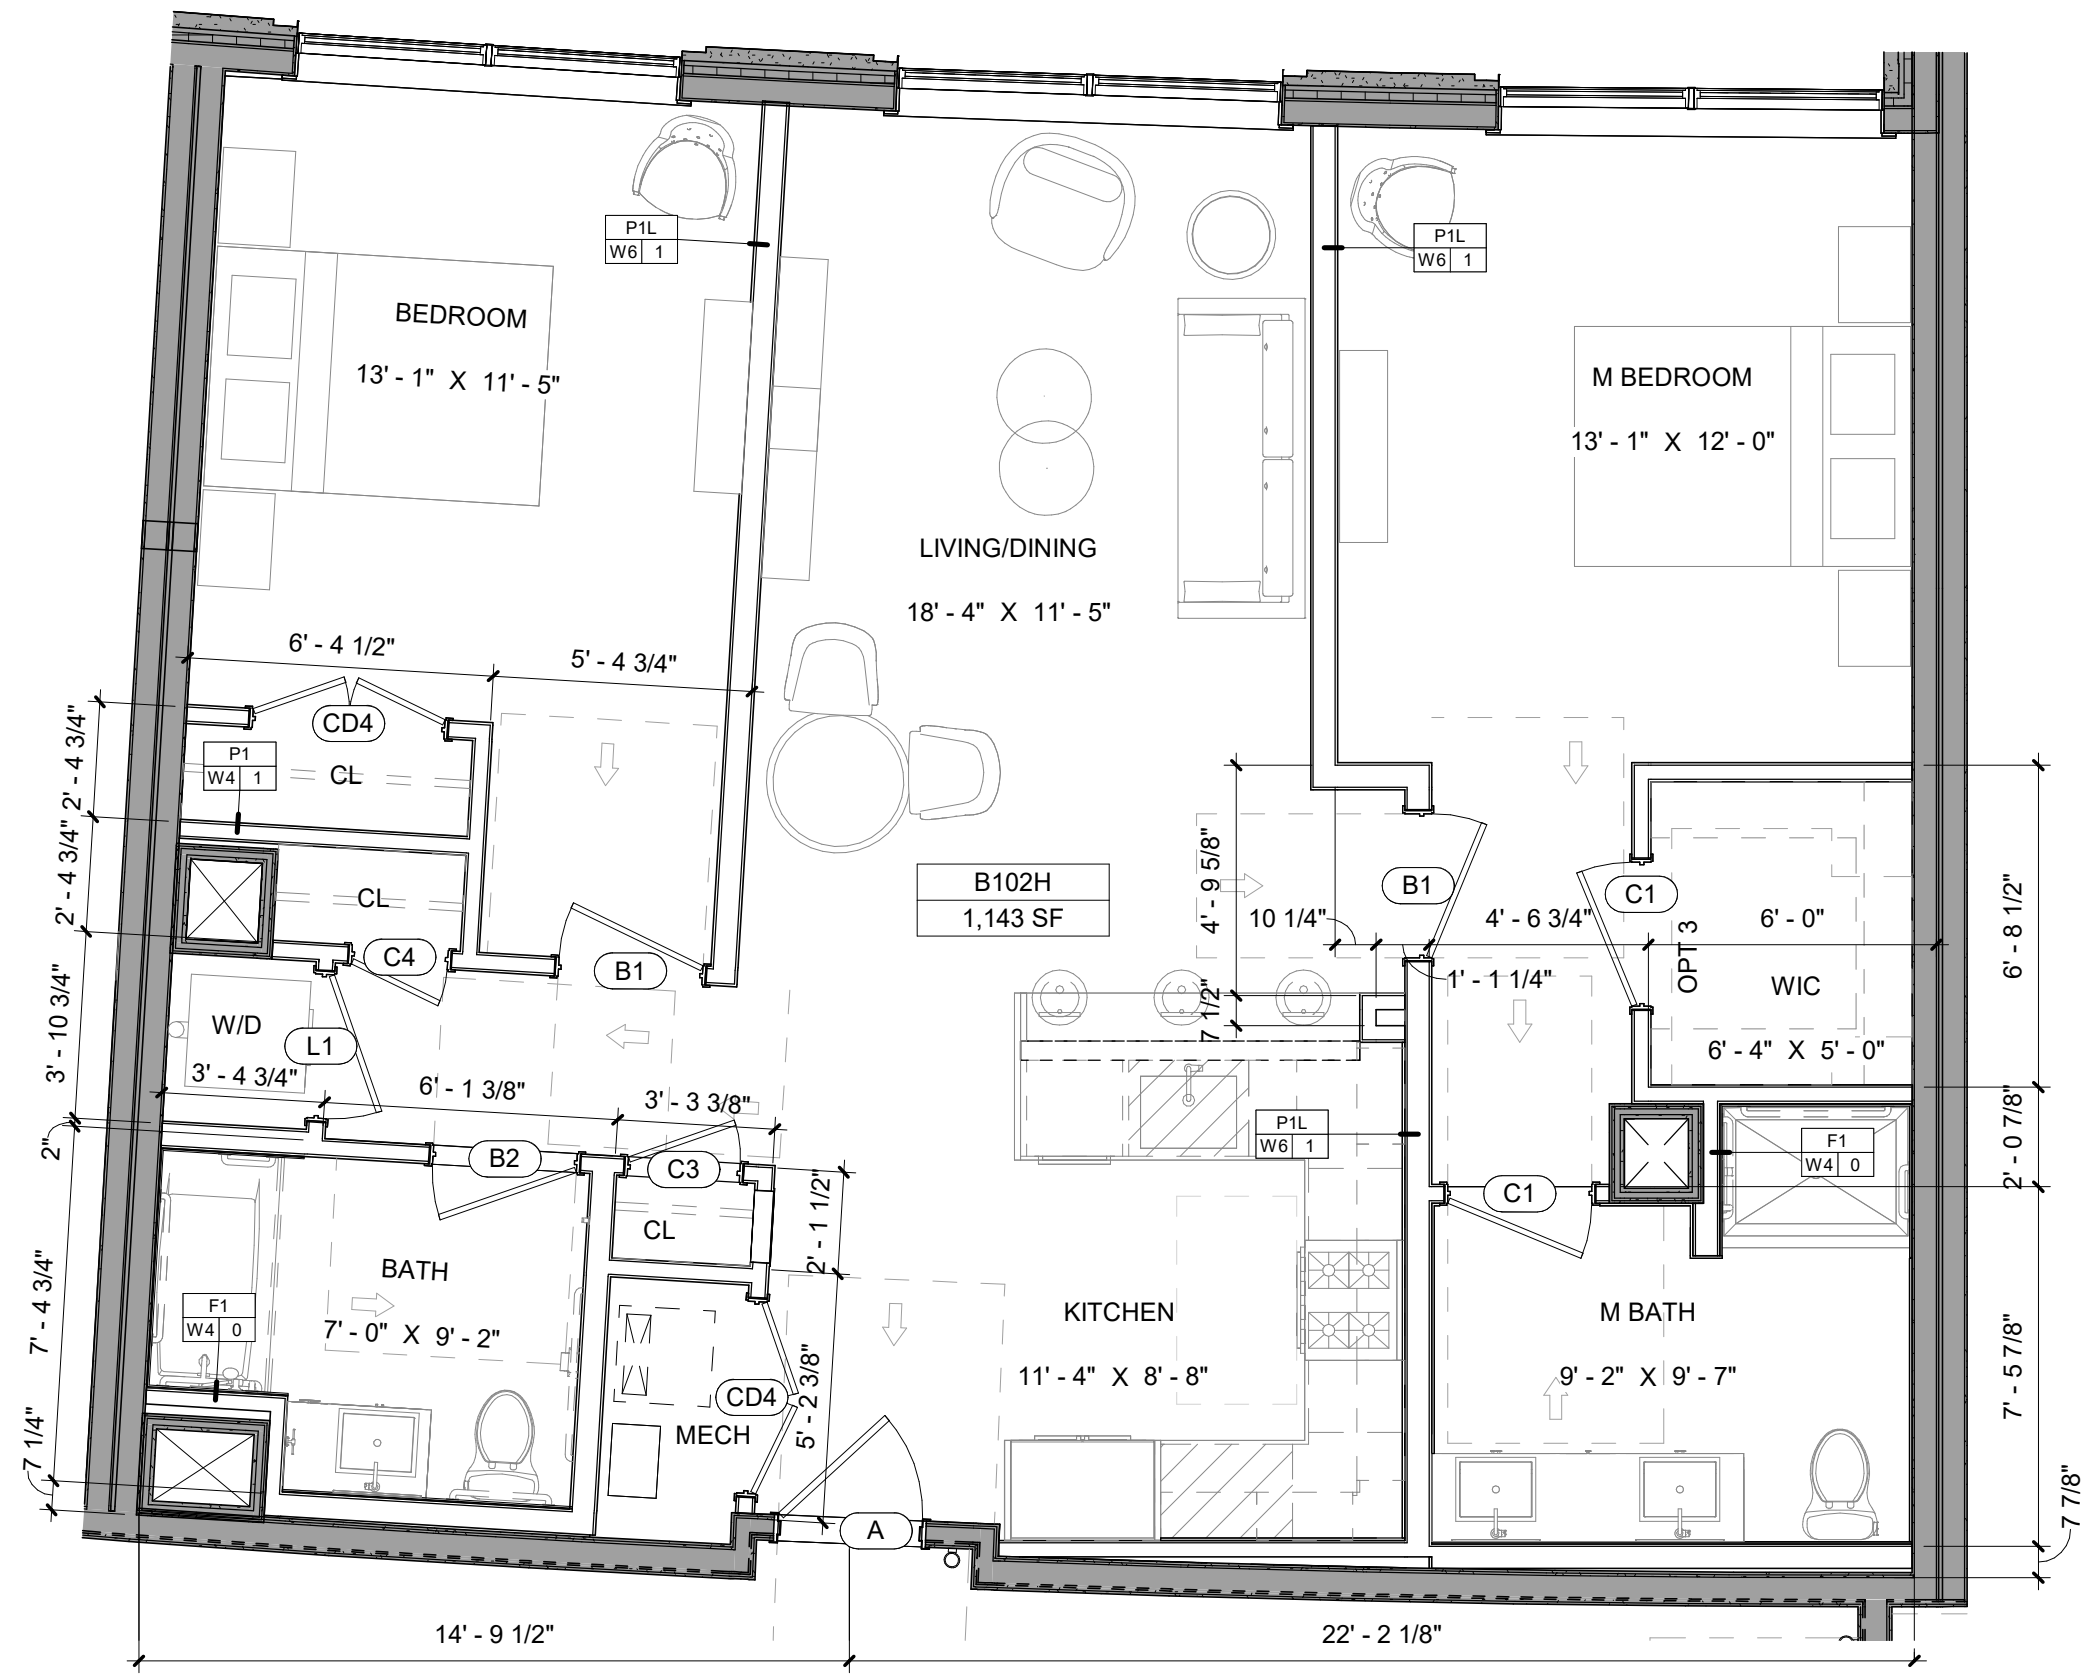

4 UNIT TYPE - B102H
SCALE: 1/4" = 1'-0"

UNIT TYPE	KITCHEN TYPE	BATHROOM TYPE	M BATHROOM TYPE	COUNT	AREA
B102H	K1	B1	B6	3	1,143 SF / 1,146 SF

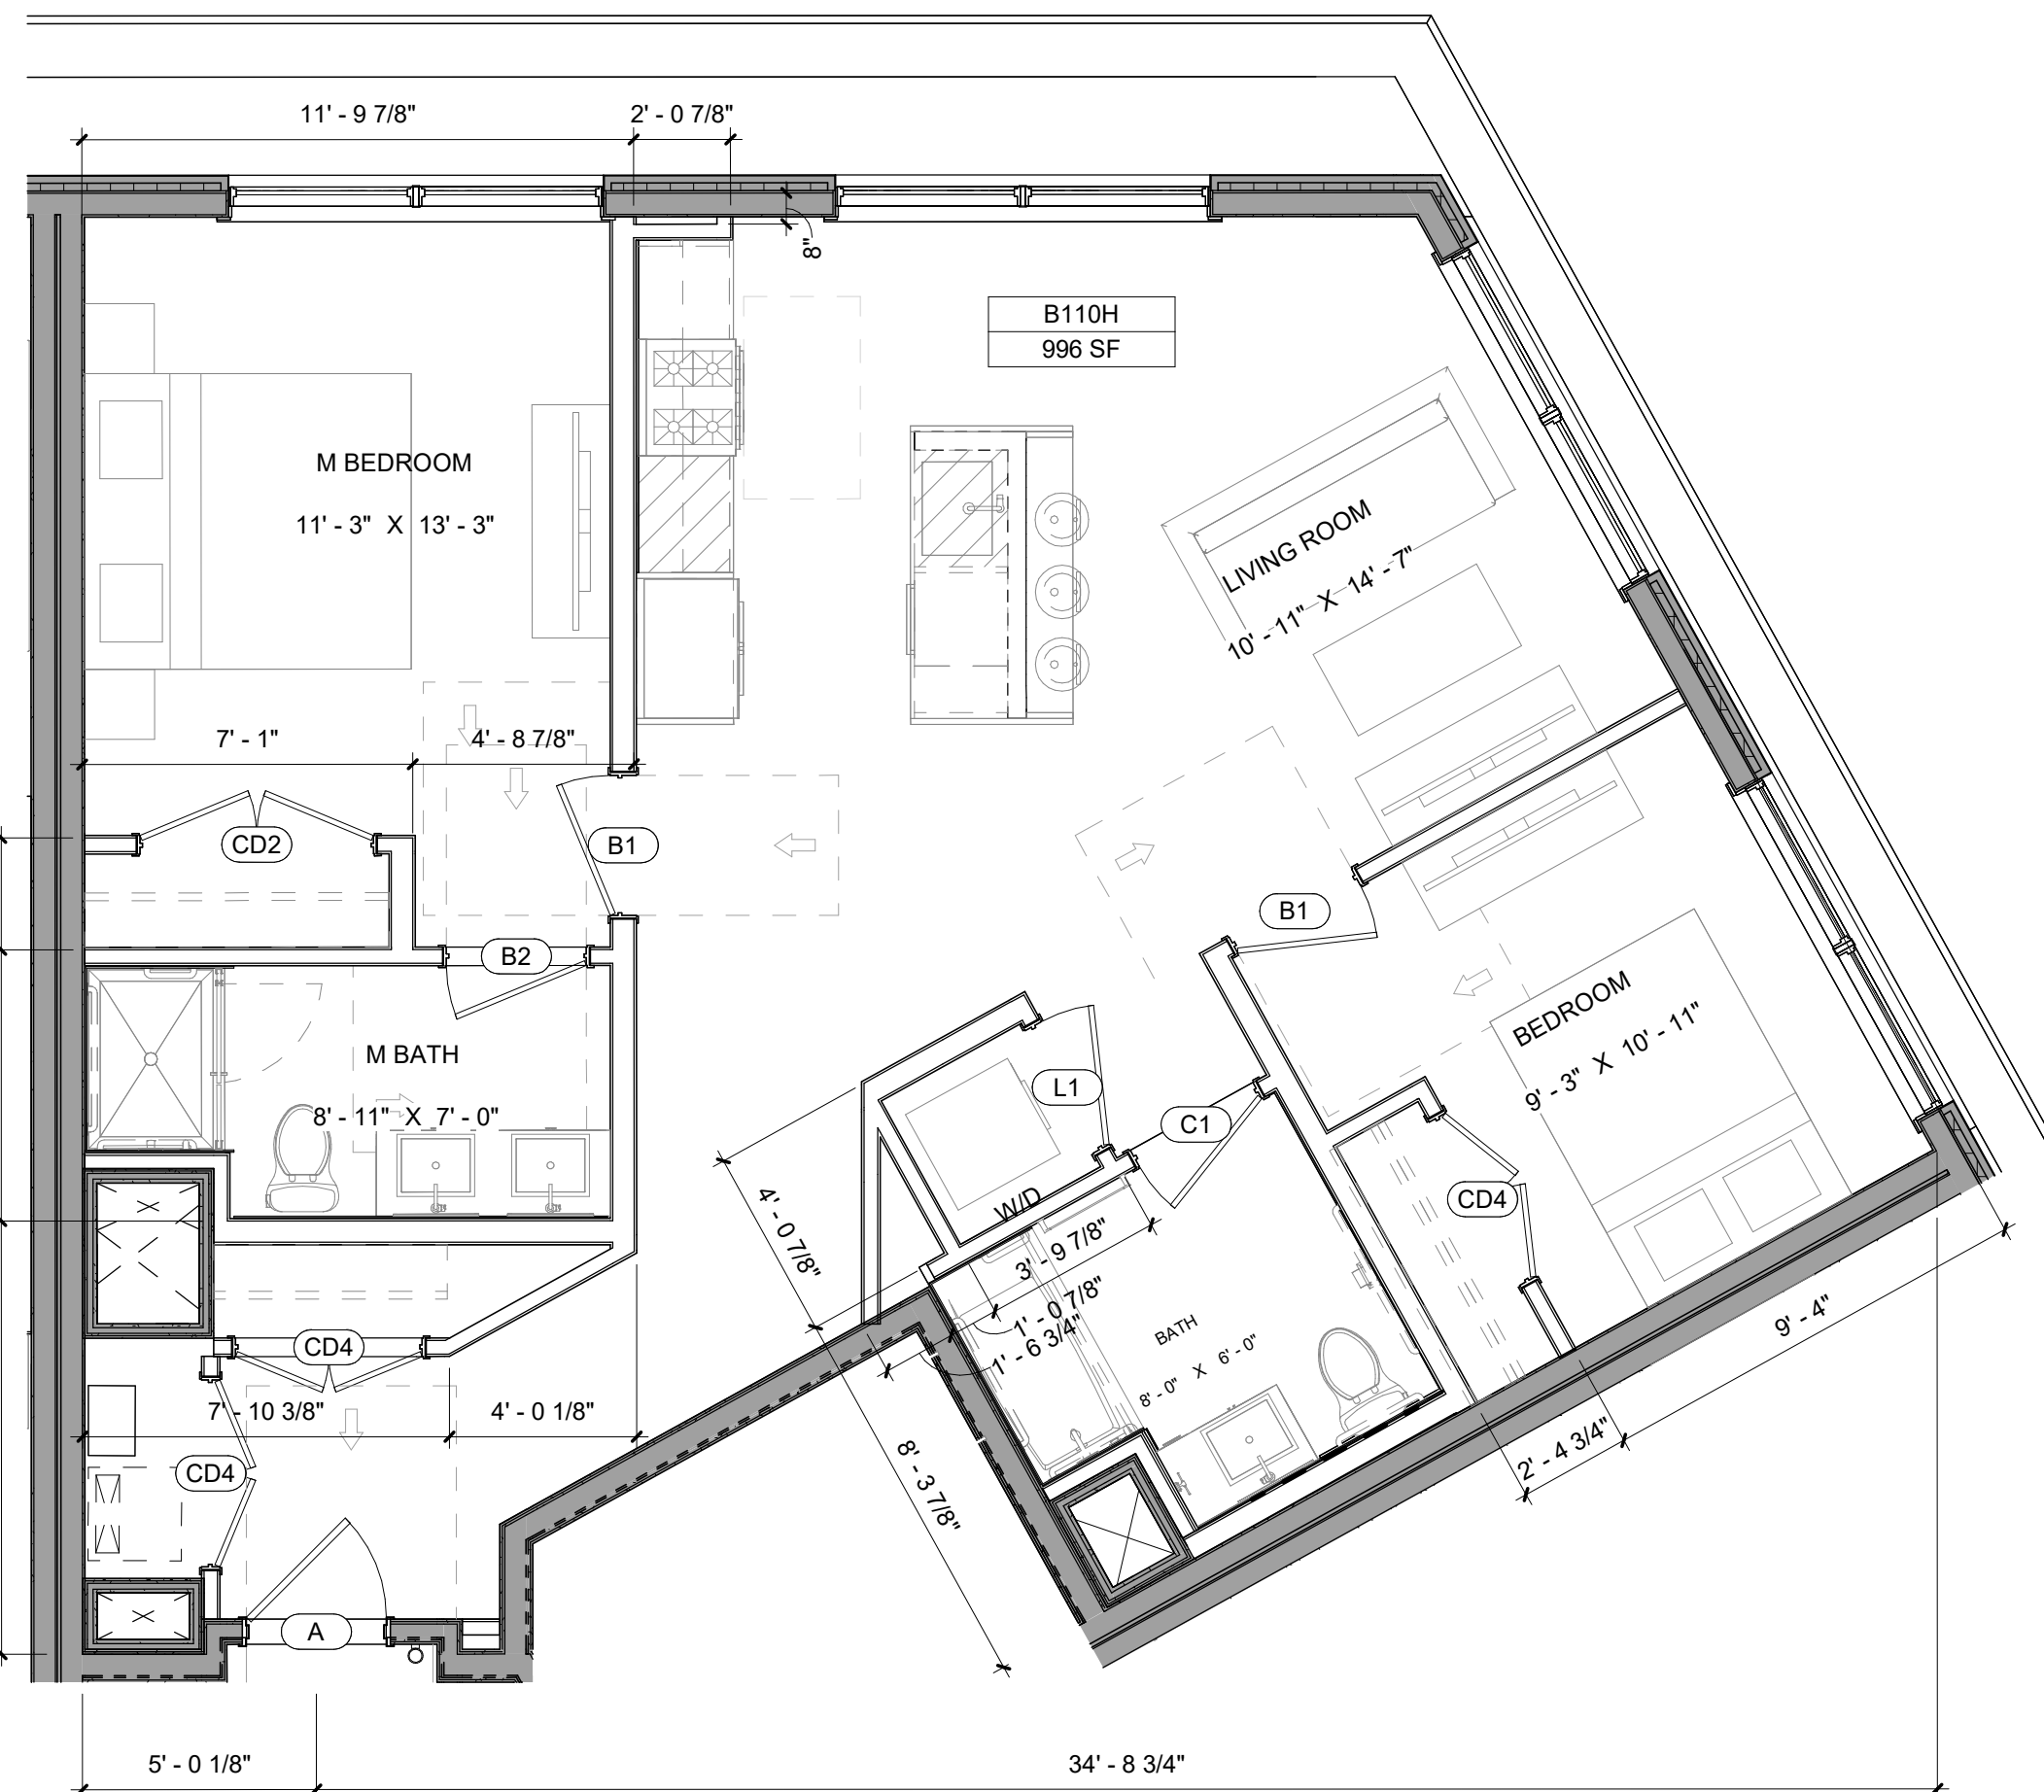


3 UNIT TYPE - B110H
SCALE: 1/4" = 1'-0"

UNIT TYPE	KITCHEN TYPE	BATHROOM TYPE	M BATHROOM TYPE	COUNT	AREA
B110H	K9	B7	B6	3	996 SF



2 UNIT TYPE - C1A - AFF
SCALE: 1/4" = 1'-0"

NAME	KITCHEN TYPE	BATHROOM TYPE	M BATHROOM TYPE	COUNT	AREA
C1A	K9	B2	B10	3	1,342 SF

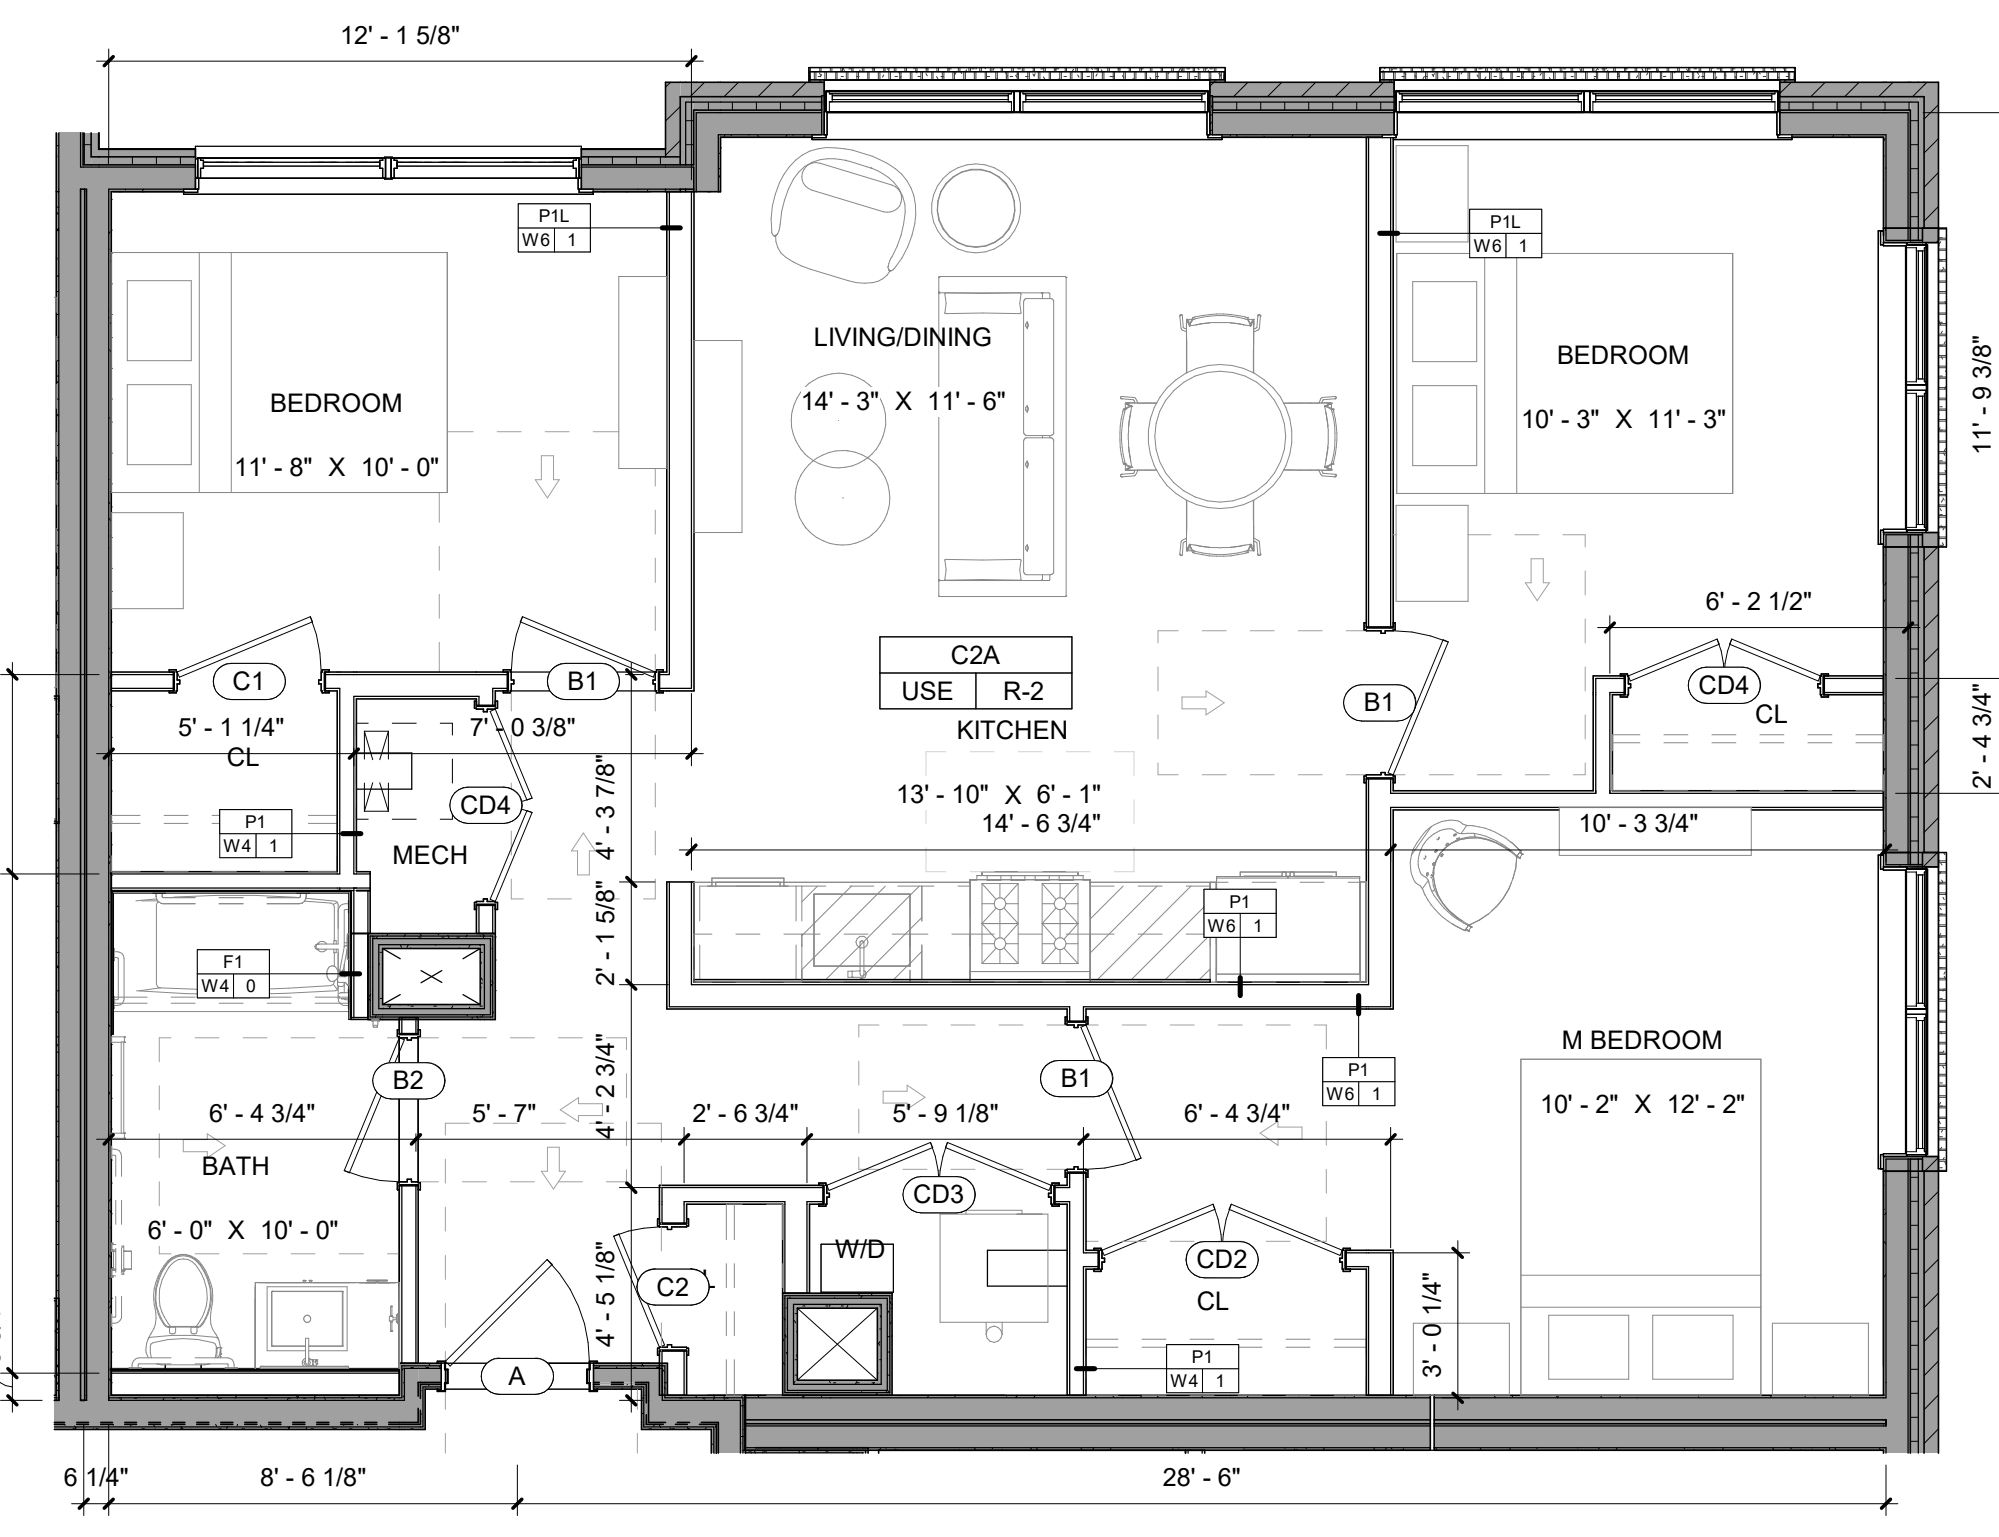

1 UNIT TYPE - C2A - AFF
SCALE: 1/4" = 1'-0"

UNIT TYPE	KITCHEN TYPE	BATHROOM TYPE	COUNT	AREA
C2A	K8	K8	1	1,918 SF

UNIT PLAN NOTES

- ALL INTERIOR DIMENSIONS TO WOOD FRAME PARTITIONS ARE TO FACE OF FRAMING. ALL INTERIOR DIMENSIONS TO METAL FRAME PARTITIONS ARE TO FACE OF FINISH AND ARE NOTED WITH ASTERISKS "X". ALL OTHER DIMENSIONS ARE AS SHOWN.
- ALL UNIT INTERIOR PARTITIONS TO BE WALL TYPE XX UNLESS OTHERWISE NOTED.
- LOCATE DOOR OPENINGS 4" FROM ADJACENT WALL UNLESS OTHERWISE NOTED.
- SEE MECHANICAL AND PLUMBING DRAWINGS FOR EQUIPMENT SPECIFICATIONS.
- SEE ELECTRICAL AND LOW VOLTAGE DRAWINGS FOR POWER AND LOW VOLTAGE PLANS.

KEYNOTES

#	DESCRIPTION
01	MECH. CHASE REF. MEP DRAWINGS
02	ELECTRICAL LOAD CENTER. REFER TO ELEC. DRAWINGS
03	IND BOX REF. TO ELEC. FOR MORE INFO
04	WALL RETURN REF. TO ELEC. DRAWINGS

MHS ARCHITECTURE

Dean Marchetto, FAIA, PP
NJ 07045
Michael Higgins, AIA, LEED
NJ21AD130830
Bruce A. Silver, AIA
NJ21AD137710
Michael Buldo, AIA
NJ21AD178800
NY 03561
Vincent Marchetto, AIA
NJ21AD151600

1422 Grand Street
Suite 5b
Hoboken, NJ 07030
T.201-795-1505
T.201-795-1505
MHSArchitecture.com

PROJECT NAME:

MORRISTOWN GREEN APARTMENTS
22 LAFAYETTE AVENUE
TOWN OF MORRISTOWN, NEW JERSEY

PREPARED FOR:

MORRISTOWN ASSOCIATES LLC
4 CUNNINGHAM DRIVE
WEST ORANGE, NJ

ISSUE

#	DATE	FOR:
1	06/03/2026	BID SET
1	07/09/26	ADDENDUM #1

ENLARGED UNIT PLANS - 2 BR EXTENDED STAY & 3 BR

PROJECT NUMBER:	2202
SCALE:	As indicated
DRAWN BY:	CM / TM / JE
CHECKED BY:	FT / MB

A09.08