


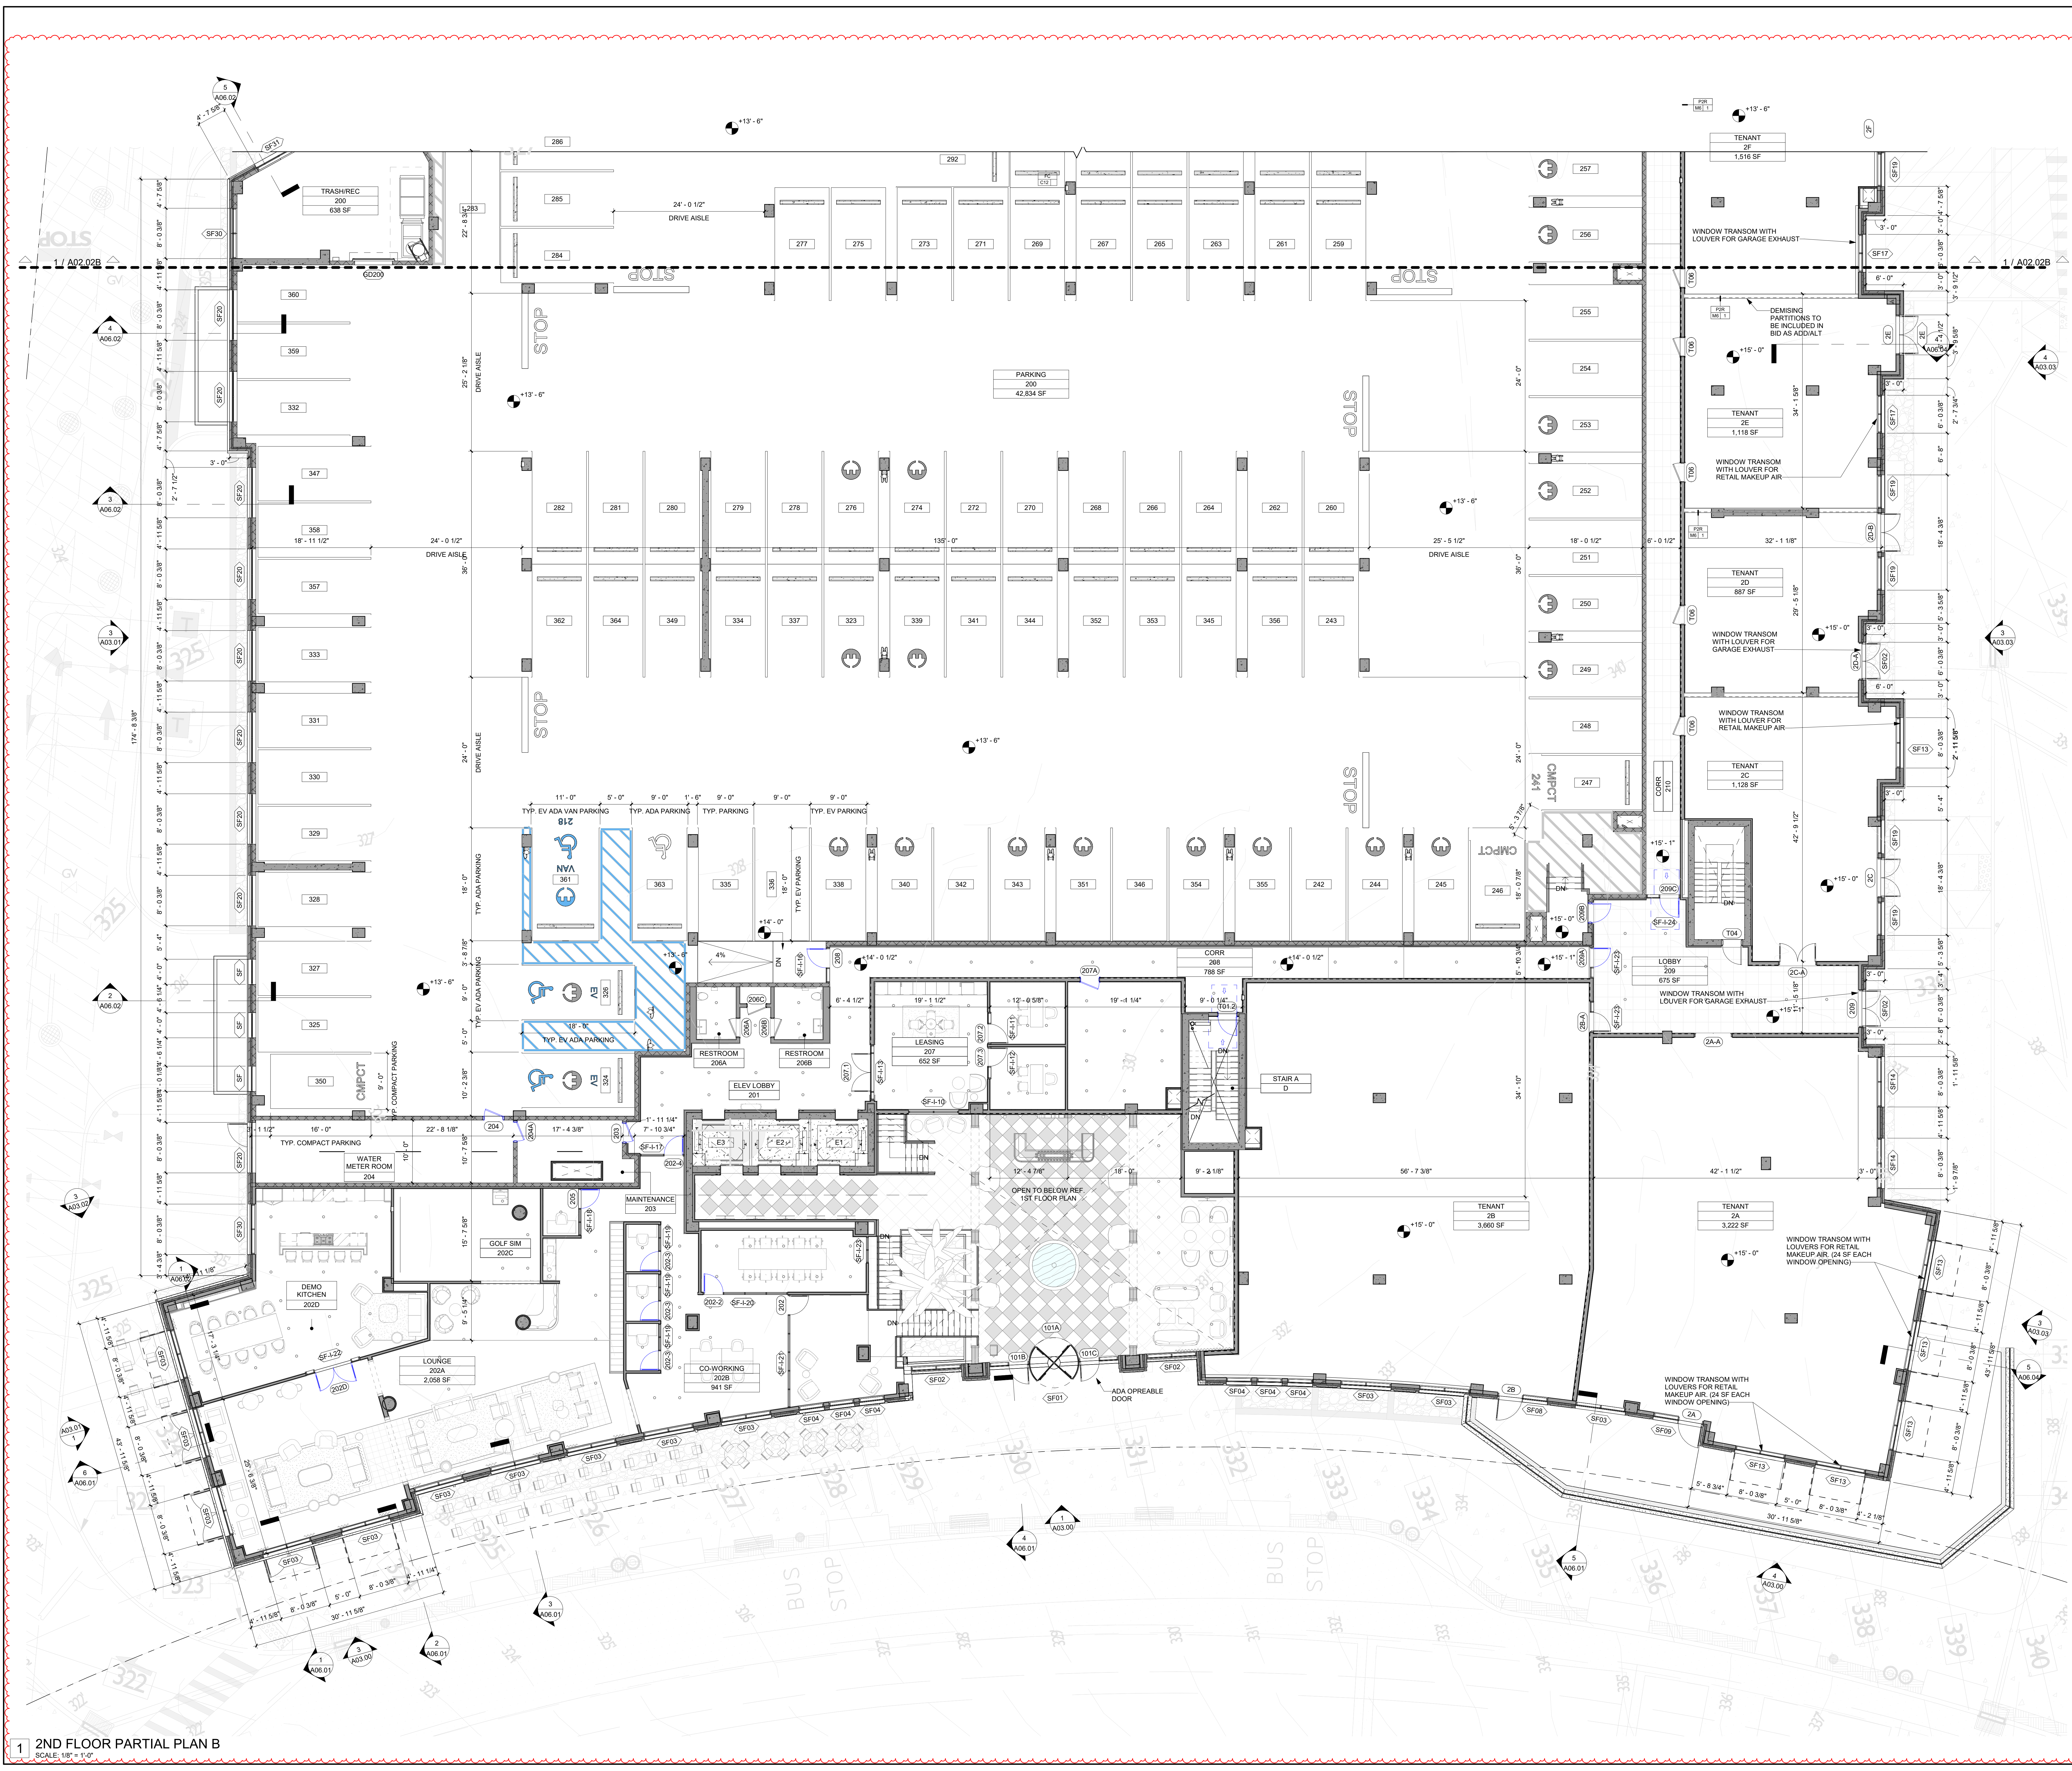

1 2ND FLOOR PARTIAL PLAN B
SCALE: 1/8" = 1'-0"

KEYNOTES	
#	DESCRIPTION

01	DESCRIPTION
----	-------------

MHS

ARCHITECTURE

1422 Grand Street
Suite 2b
Hoboken, NJ 07030
T.201-795-1505
MHSArchitecture.com

Dean Marchetto, FAIA, PP
NJ 027045
Michael Higgins, AIA, LEED
NJ21A0130830
Bruce A. Silver, AIA
NJ21A0137110
Michael Buldo, AIA
NJ21A01788000
NY 035161
Vincent Marchetto, AIA
NJ21A02151000

PROJECT NAME:
**MORRISTOWN GREEN
APARTMENTS**
22 LAFAYETTE AVENUE
TOWN OF MORRISTOWN, NEW JERSEY

PREPARED FOR:
**MORRISTOWN
ASSOCIATES LLC**
4 CUNNINGHAM DRIVE
WEST ORANGE, NJ

ISSUE	
#	DATE
1	06/03/2026
2	07/09/26
3	
4	
5	
6	
7	
8	
9	
10	

2ND FLOOR PARTIAL PLAN
A

N

PROJECT NUMBER: 2202

SCALE: 1/8" = 1'-0"

DRAWN BY: CM / TM / JE

CHECKED BY: FT / MB

A02.02A

Copyright © 2026 MHS Architecture