


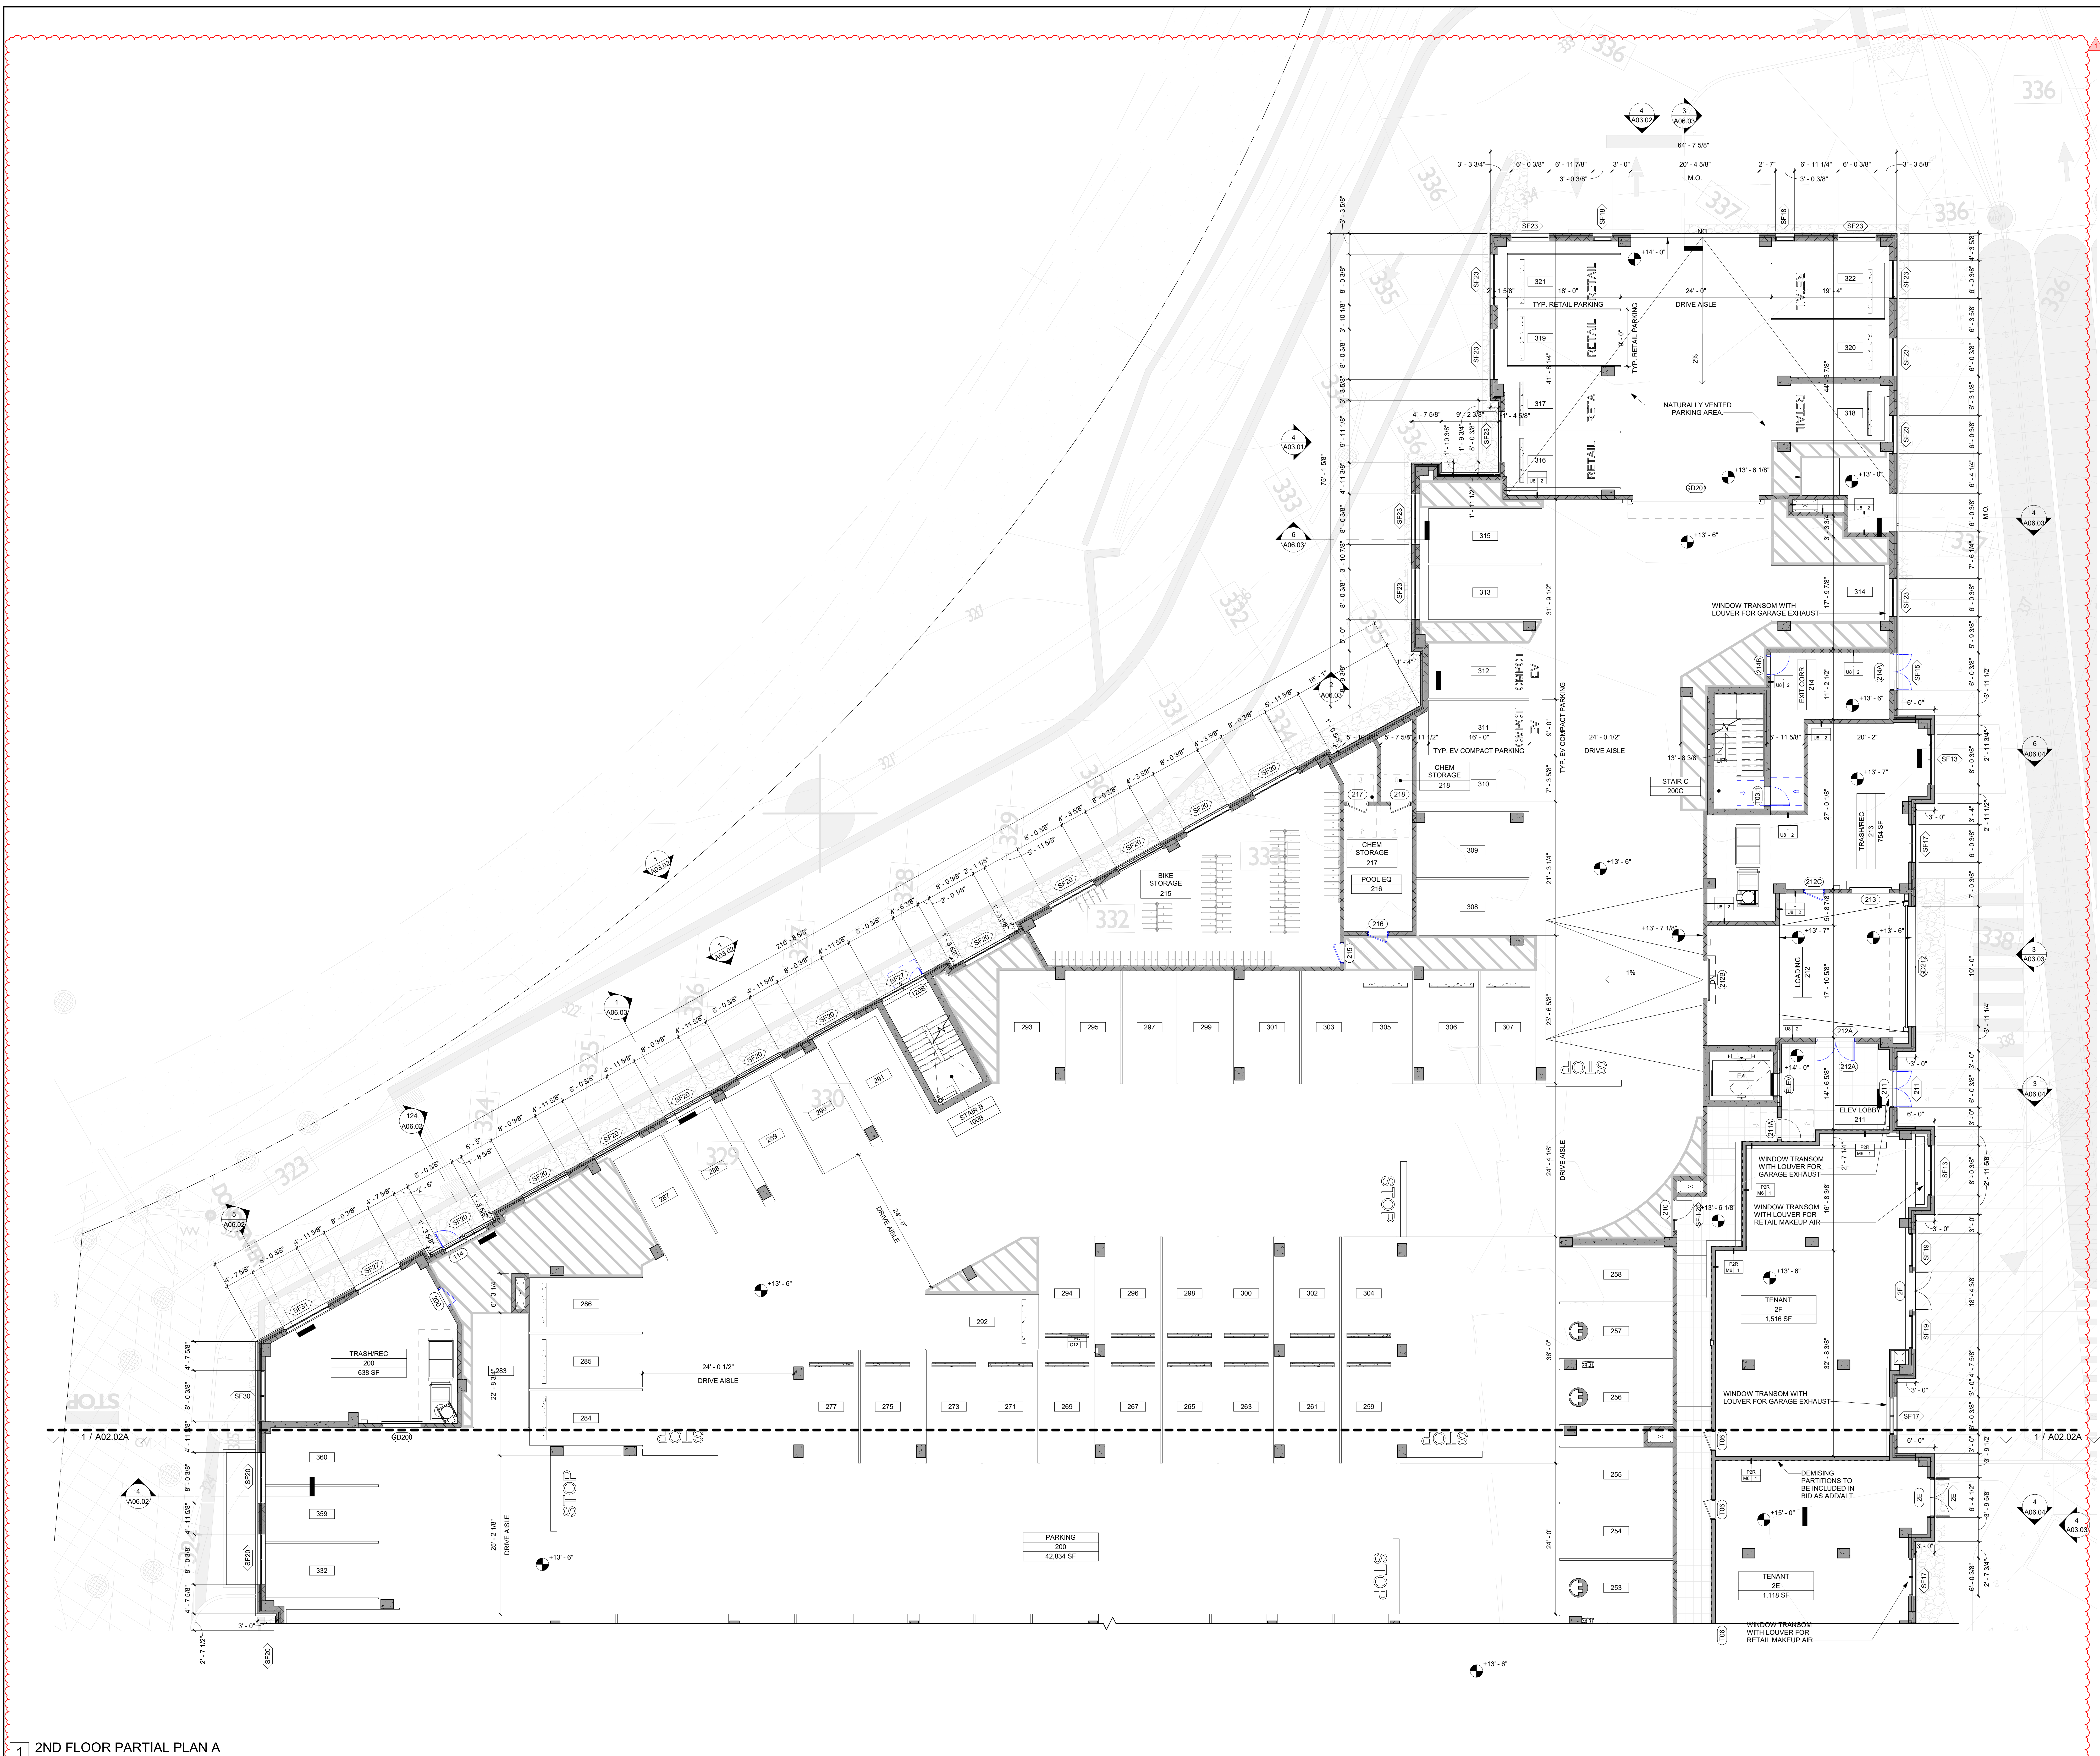

1 2ND FLOOR PARTIAL PLAN A
SCALE: 1/8" = 1'-0"

MHS
ARCHITECTURE

1422 Grand Street
Suite 2b
Hoboken, NJ 07030
T.201-795-1505
MHSarchitecture.com

Dean Marchetto, FAIA, PP
NJ 027045
Michael Higgins, AIA, LEED
NJ21A0170530
Bruce A. Sileve, AIA
NJ21A0137710
Michael Buldo, AIA
NJ21A01705300
NY 035161
Vincent Marchetto, AIA
NJ21A02151000

PROJECT NAME:
**MORRISTOWN GREEN
APARTMENTS**
22 LAFAYETTE AVENUE
TOWN OF MORRISTOWN, NEW JERSEY

PREPARED FOR:
**MORRISTOWN
ASSOCIATES LLC**
4 CUNNINGHAM DRIVE
WEST ORANGE, NJ

ISSUE	#	DATE	FOR:
	1	06/03/2026	BID SET
	1	07/09/26	ADDENDUM #1

2ND FLOOR PARTIAL PLAN
B

PROJECT NUMBER:	2202
SCALE:	1/8" = 1'-0"
DRAWN BY:	CM / TM / JE
CHECKED BY:	FT / MB

A02.02B

Copyright © 2026 MHS Architecture