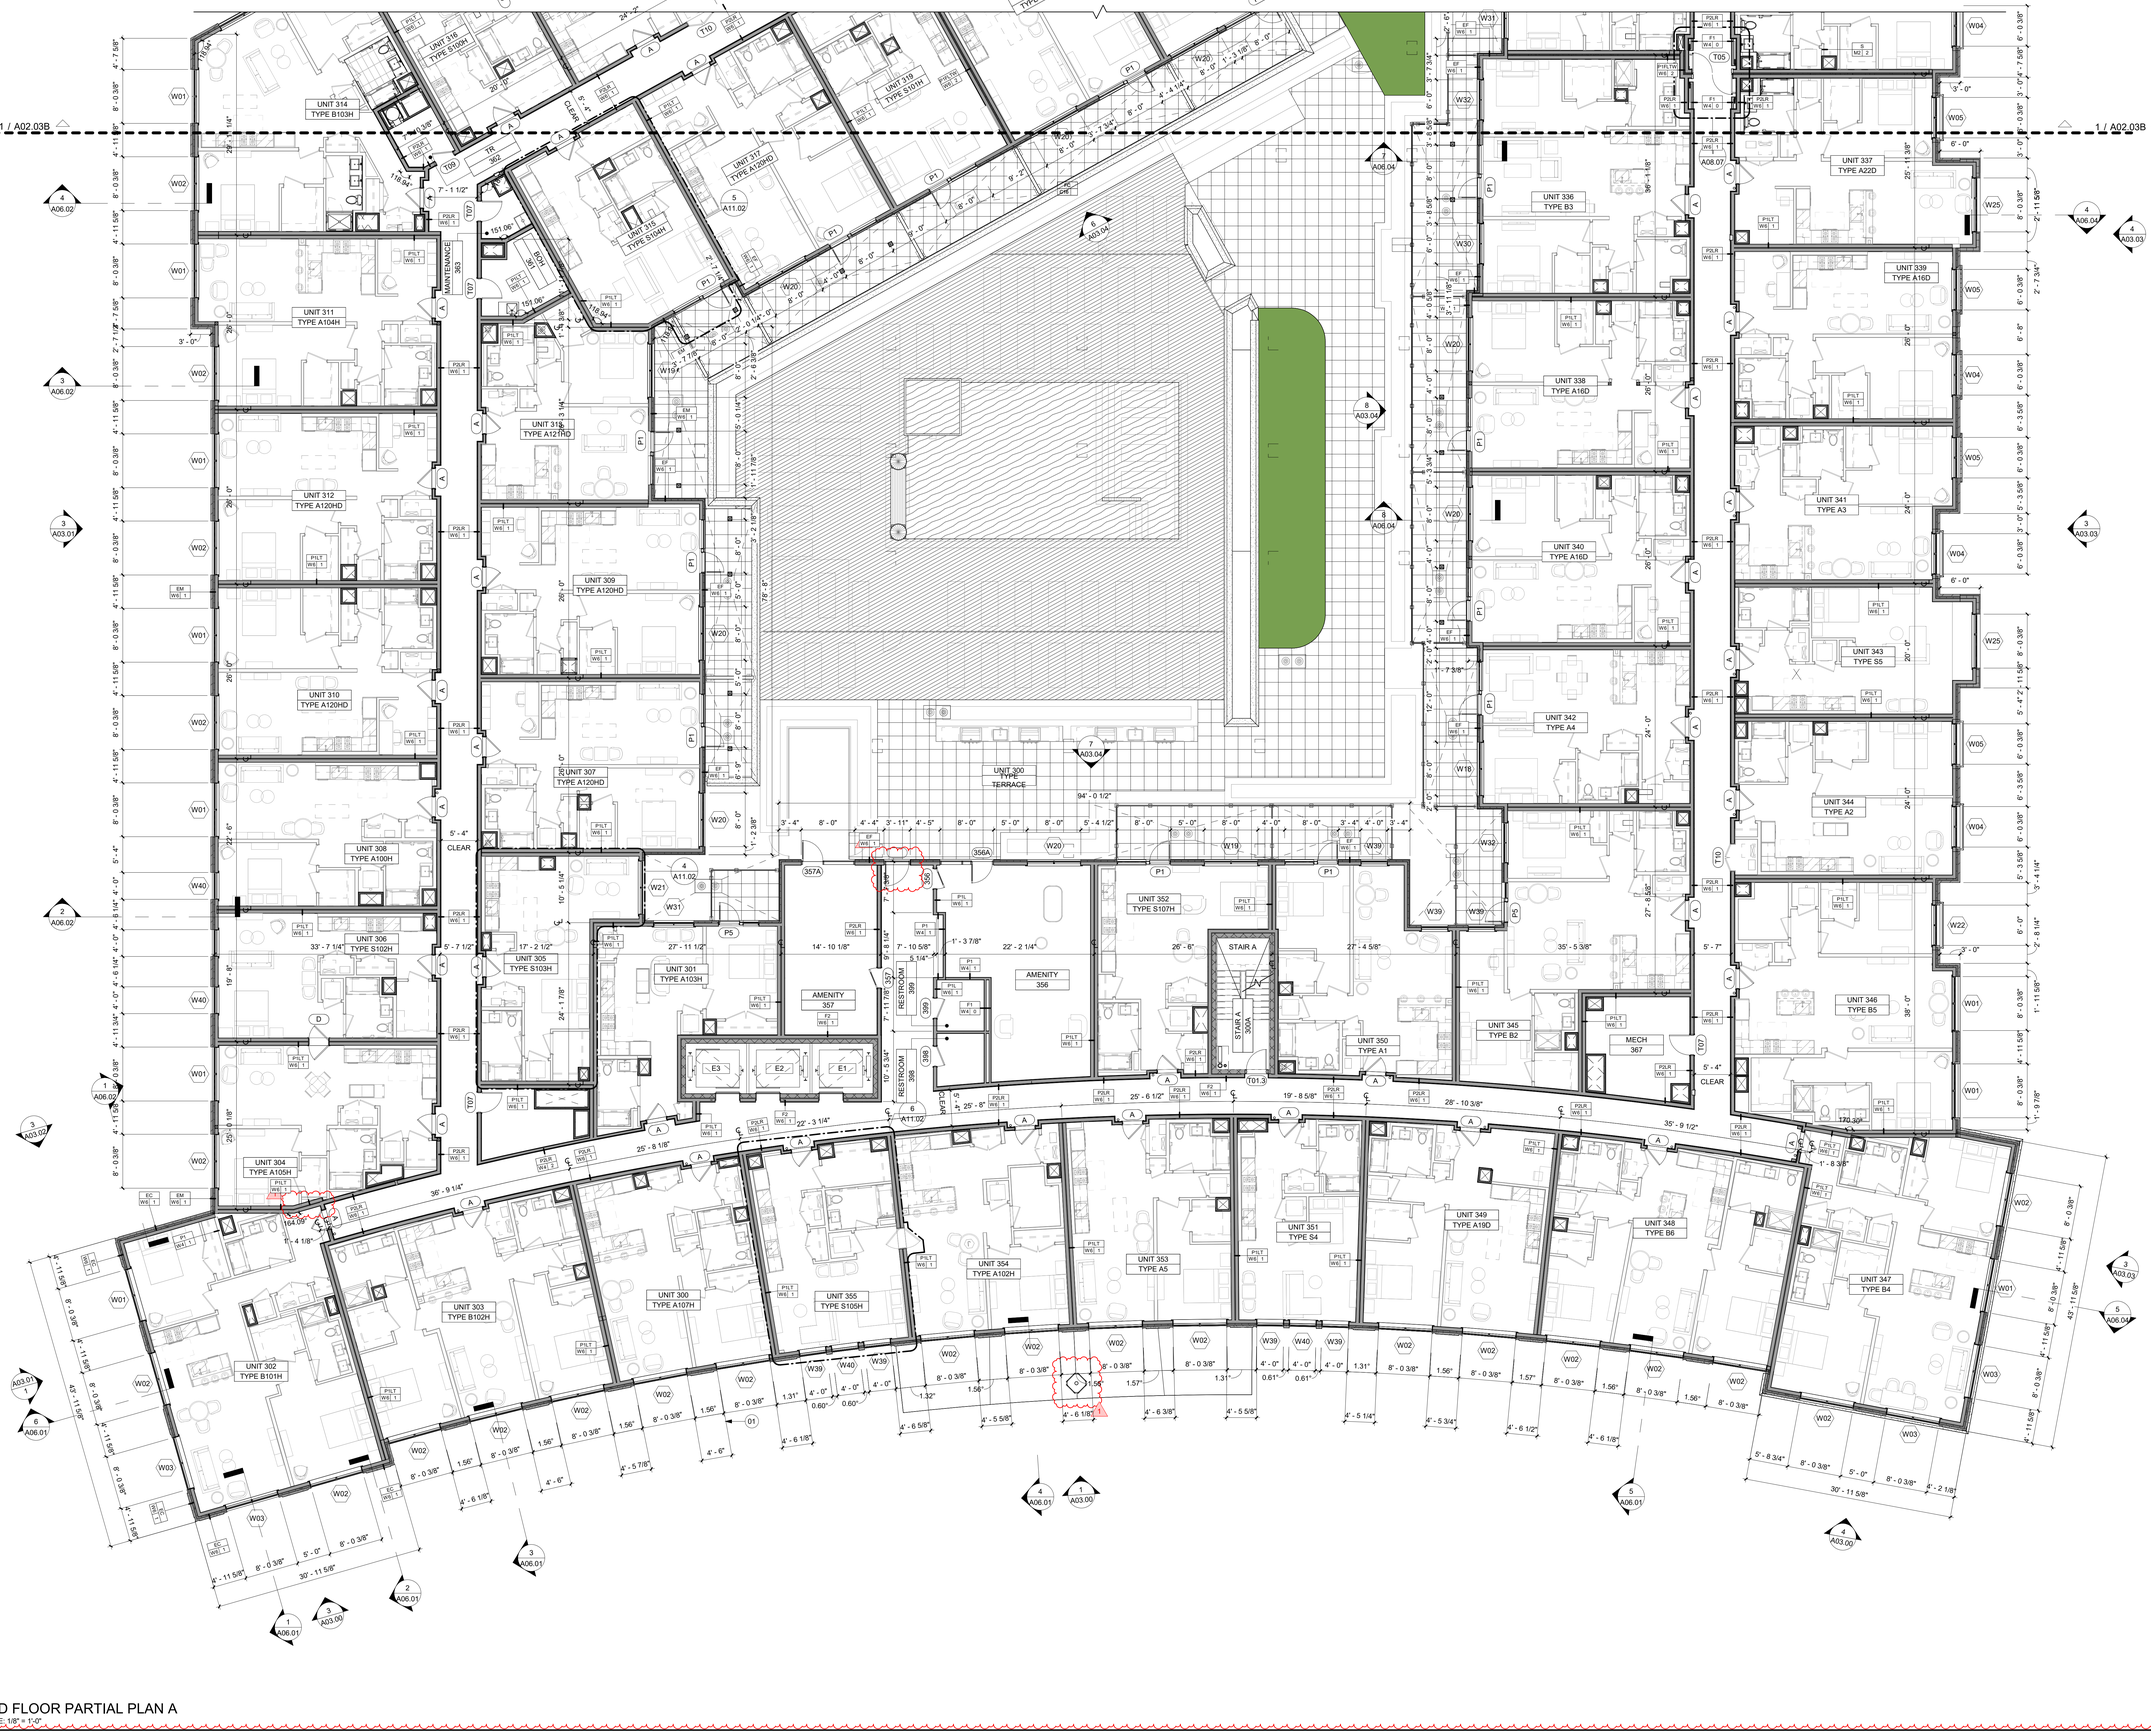


1 3RD FLOOR PARTIAL PLAN A
SCALE: 1/8" = 1'-0"

MHS ARCHITECTURE

Dean Marchetto, FAIA, PP NJ C07945
Michael Higgins, AIA, LEED NJ21A0130830
Bruce A Stieve, AIA NJ21A0137710
Michael Bubb, AIA NJ21A01786800 NY 035161
Vincent Marchetto, AIA NJ21A02161600

1422 Grand Street
Suite 5b
Hoboken, NJ 07030

T 201-795-1505
MHSarchitecture.com

PROJECT NAME:
MORRISTOWN GREEN APARTMENTS
22 LAFAYETTE AVENUE
TOWN OF MORRISTOWN, NEW JERSEY

PREPARED FOR:
MORRISTOWN ASSOCIATES LLC
4 CUNNINGHAM DRIVE
WEST ORANGE, NJ

ISSUE

#	DATE:	FOR:
	06/03/2026	BID SET
1	07/09/26	ADDENDUM #1

3RD FLOOR PARTIAL PLAN A

PROJECT NUMBER:	2202
SCALE:	1/8" = 1'-0"
DRAWN BY:	CM / TM / JE
CHECKED BY:	FT / MB

A02.03A

Copyright © 2026 MHS Architecture