


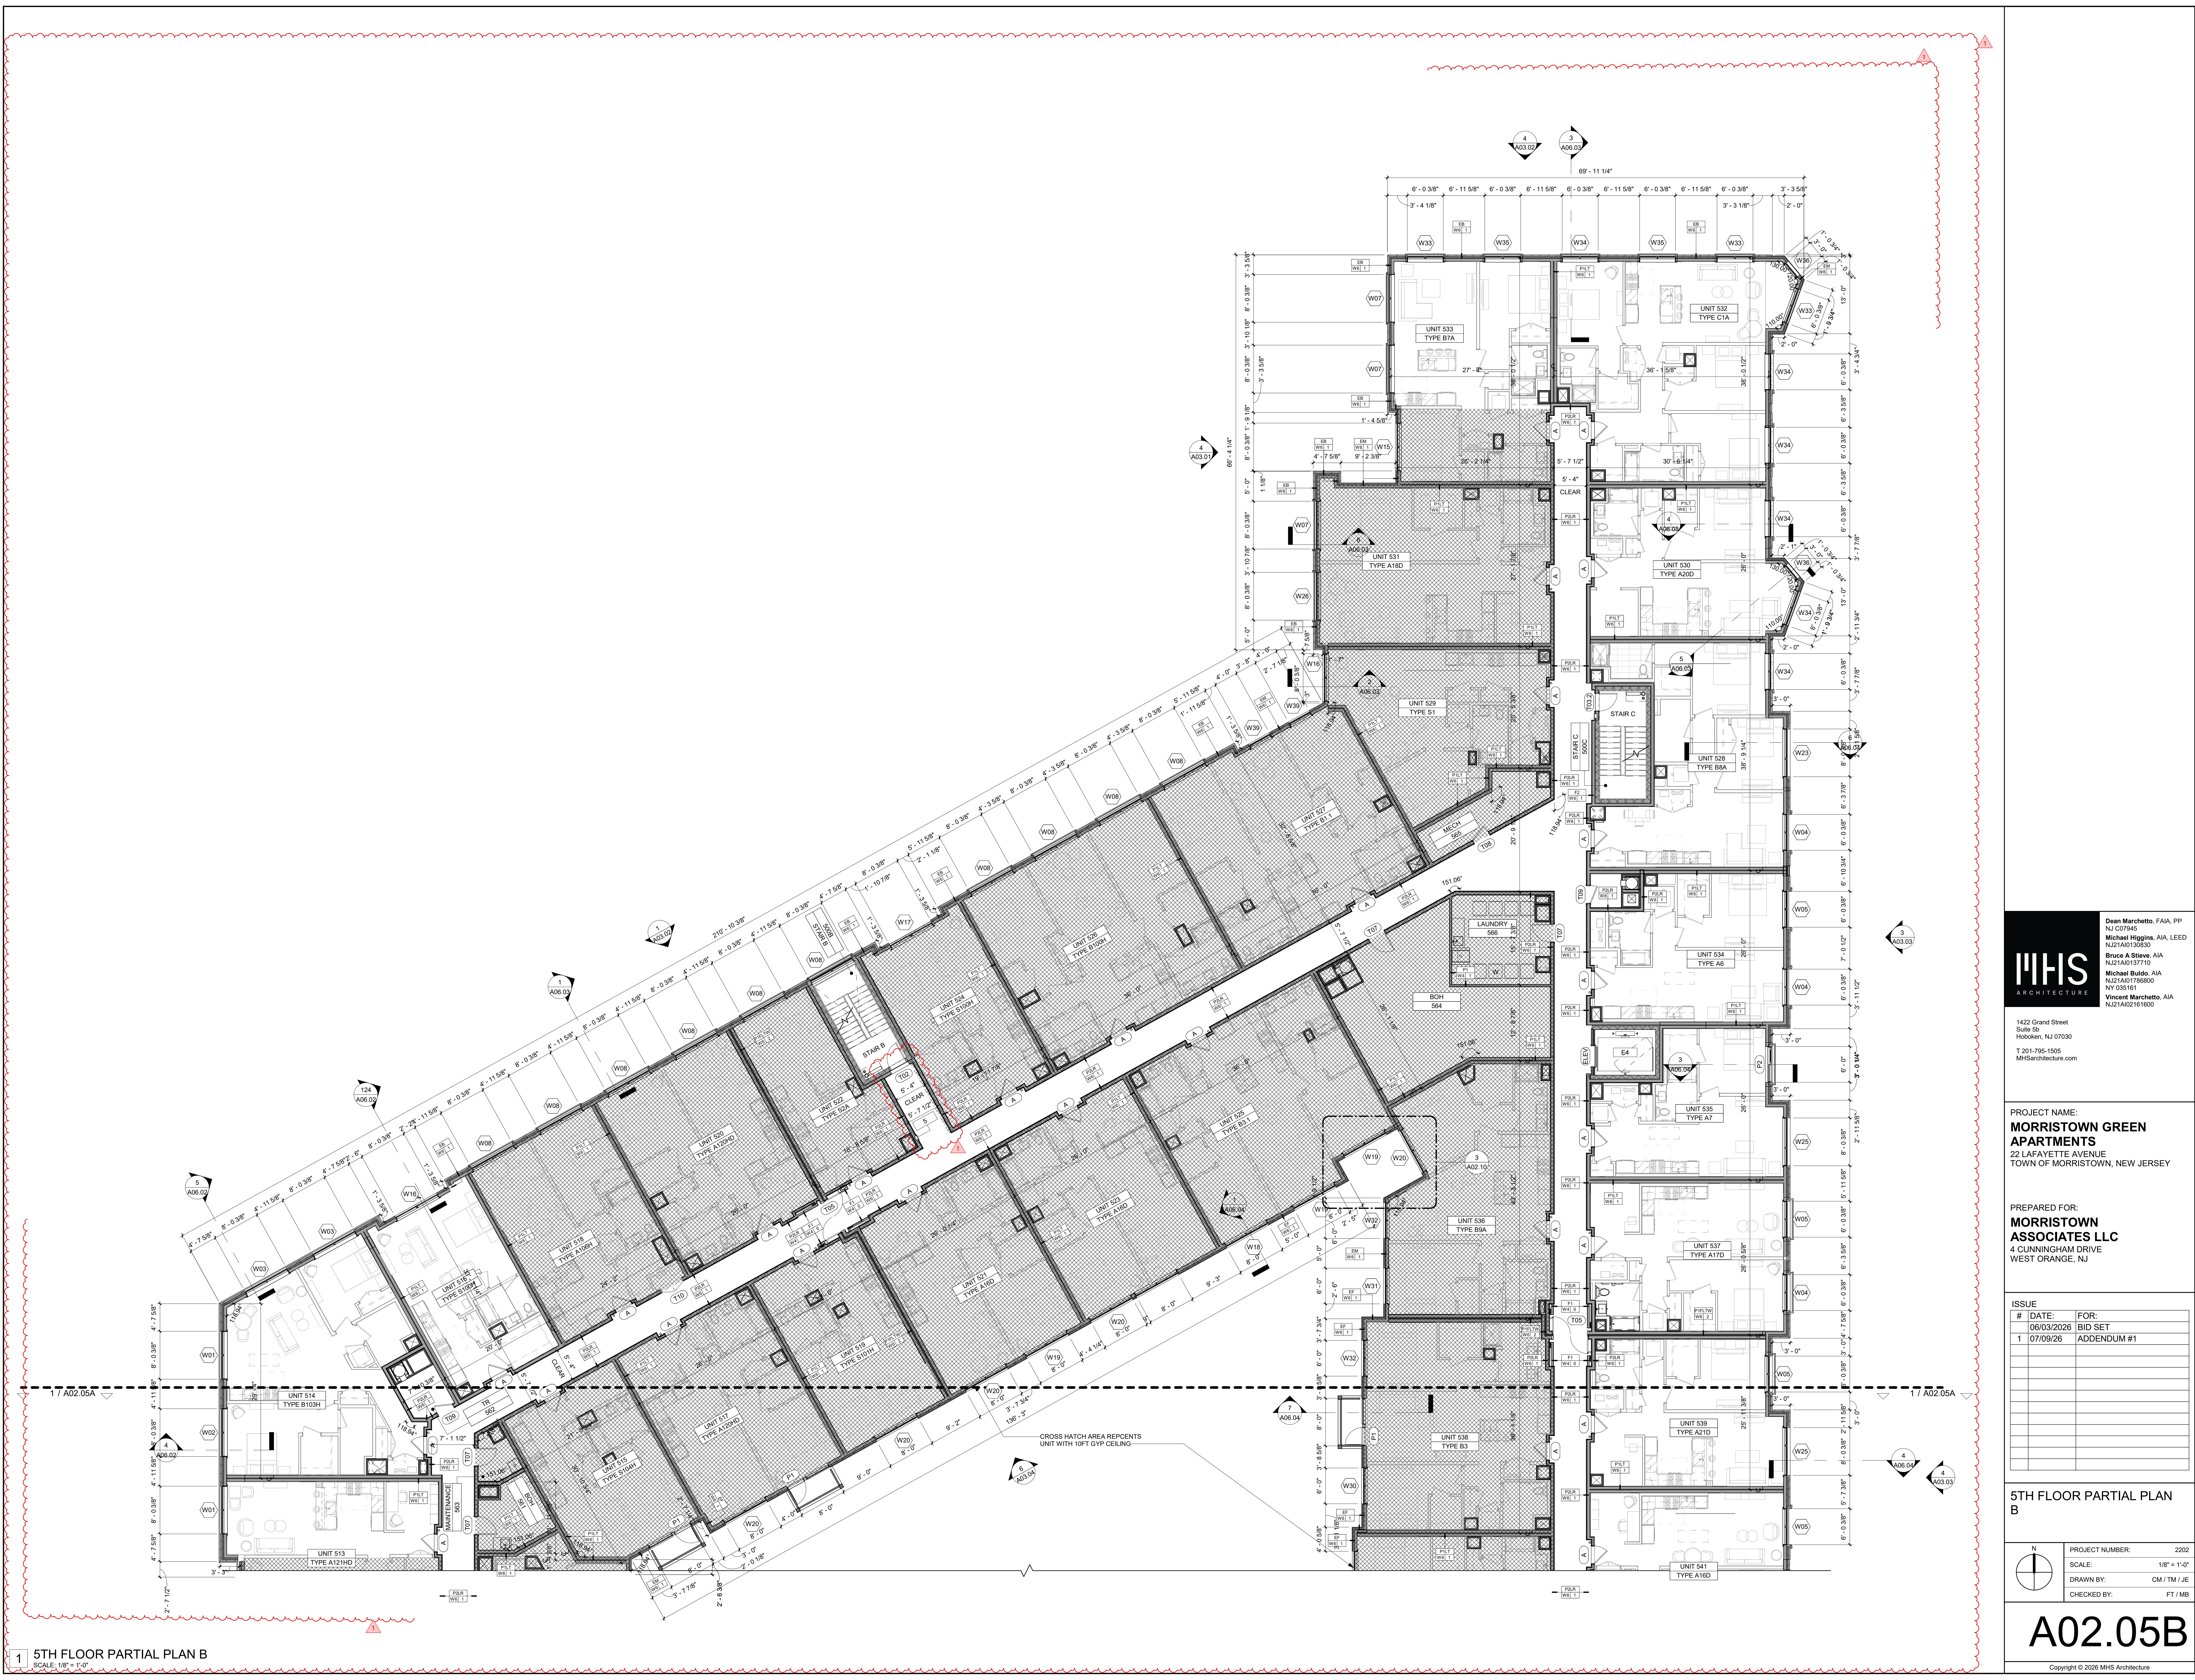

1 5TH FLOOR PARTIAL PLAN B
SCALE: 1/8" = 1'-0"

MHS
ARCHITECTURE

1422 Grand Street
Suite 25
Hoboken, NJ 07030
T.201-795-1505
MHSArchitecture.com

PROJECT NAME:
**MORRISTOWN GREEN
APARTMENTS**
22 LAFAYETTE AVENUE
TOWN OF MORRISTOWN, NEW JERSEY

PREPARED FOR:
**MORRISTOWN
ASSOCIATES LLC**
4 CUNNINGHAM DRIVE
WEST ORANGE, NJ

ISSUE	#	DATE	FOR:
	1	06/03/2026	BID SET
	1	07/09/26	ADDENDUM #1

PROJECT NUMBER:	2202
SCALE:	1/8" = 1'-0"
DRAWN BY:	CM / TM / JE
CHECKED BY:	FT / MB

A02.05B

Copyright © 2026 MHS Architecture