


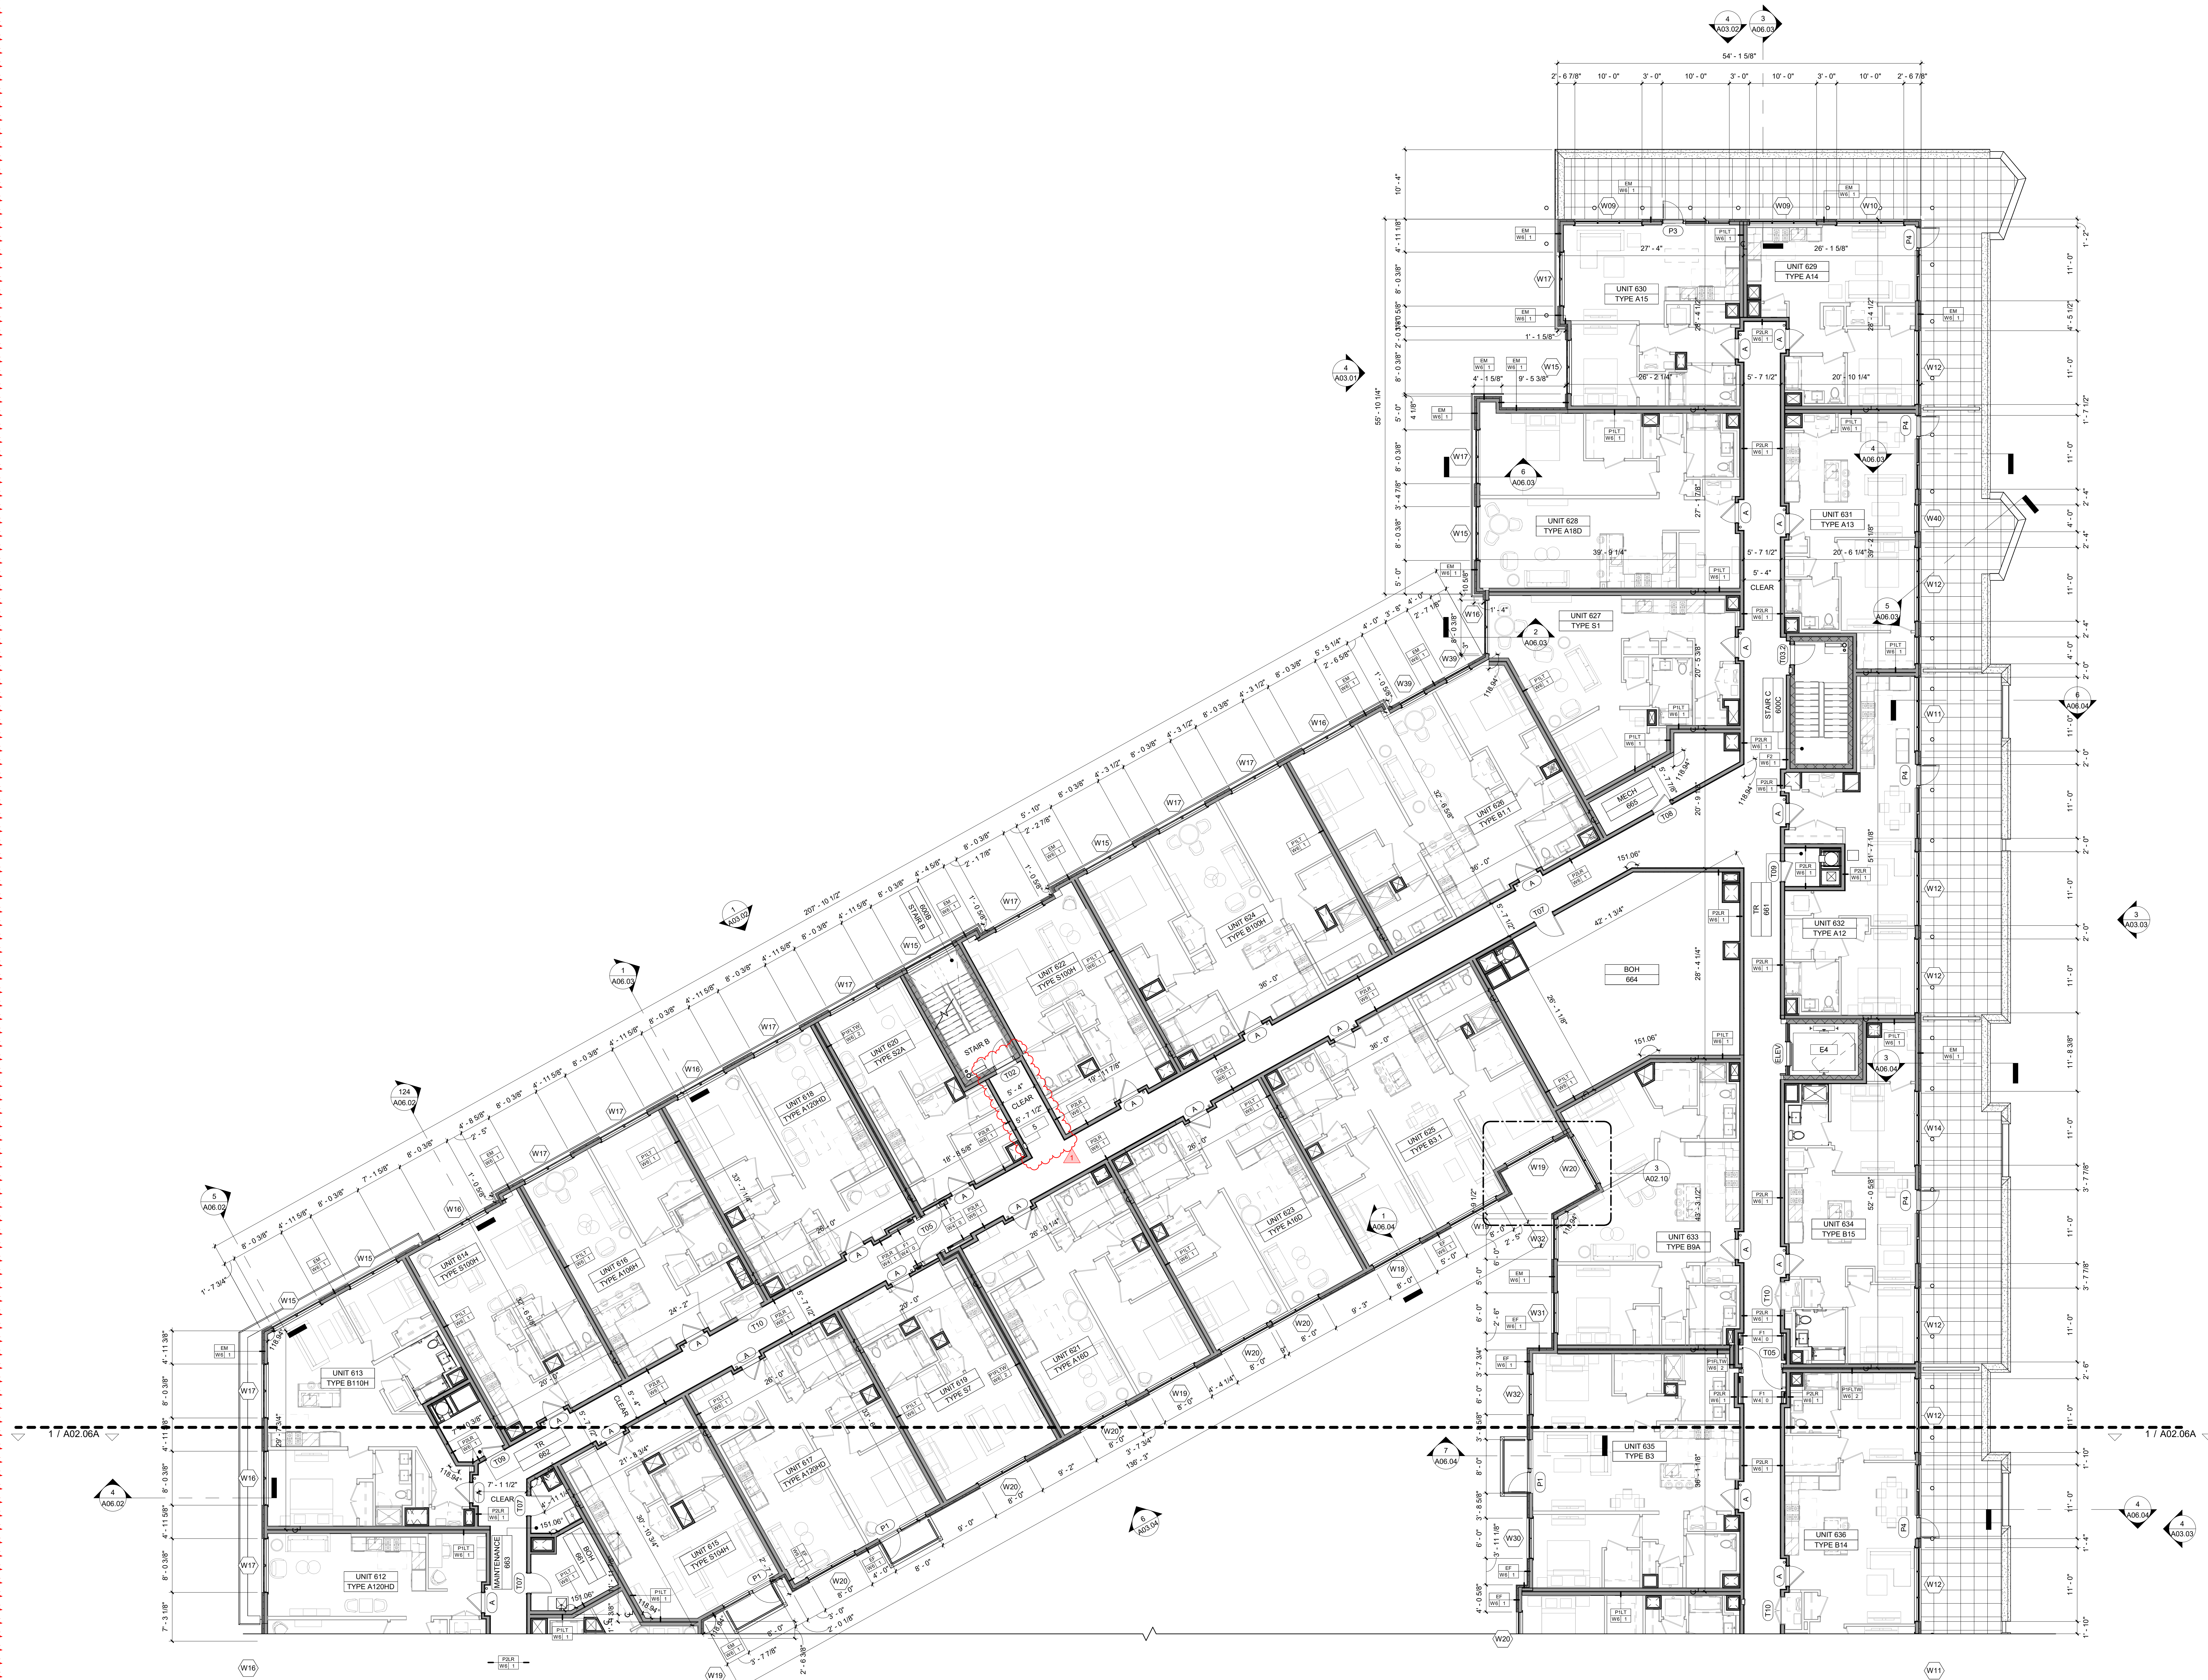

1 6TH FLOOR PARTIAL PLAN B
SCALE: 1/8" = 1'-0"

Dean Marchetto, FAIA, PP
NJ 07045
Michael Higgins, AIA, LEED
NJ21A0130830
Bruce A. Sline, AIA
NJ21A0137710
Michael Baldo, AIA
NJ21A01708800
NY 035161
Vincent Marchetto, AIA
NJ21A02151000

MHS
ARCHITECTURE

1422 Grand Street
Suite 5b
Hoboken, NJ 07030
T.201-795-1505
MHSArchitecture.com

PROJECT NAME:
**MORRISTOWN GREEN
APARTMENTS**
22 LAFAYETTE AVENUE
TOWN OF MORRISTOWN, NEW JERSEY

PREPARED FOR:
**MORRISTOWN
ASSOCIATES LLC**
4 CUNNINGHAM DRIVE
WEST ORANGE, NJ

ISSUE	
#	DATE
1	06/03/2026
2	07/09/26
FOR:	
BID SET	
ADDENDUM #1	

6TH FLOOR PARTIAL PLAN
B

	PROJECT NUMBER:	2202
	SCALE:	1/8" = 1'-0"
	DRAWN BY:	CM / TM / JE
	CHECKED BY:	FT / MB

A02.06B

Copyright © 2026 MHS Architecture