

1

2

3

4

5


A

B


C

D


E

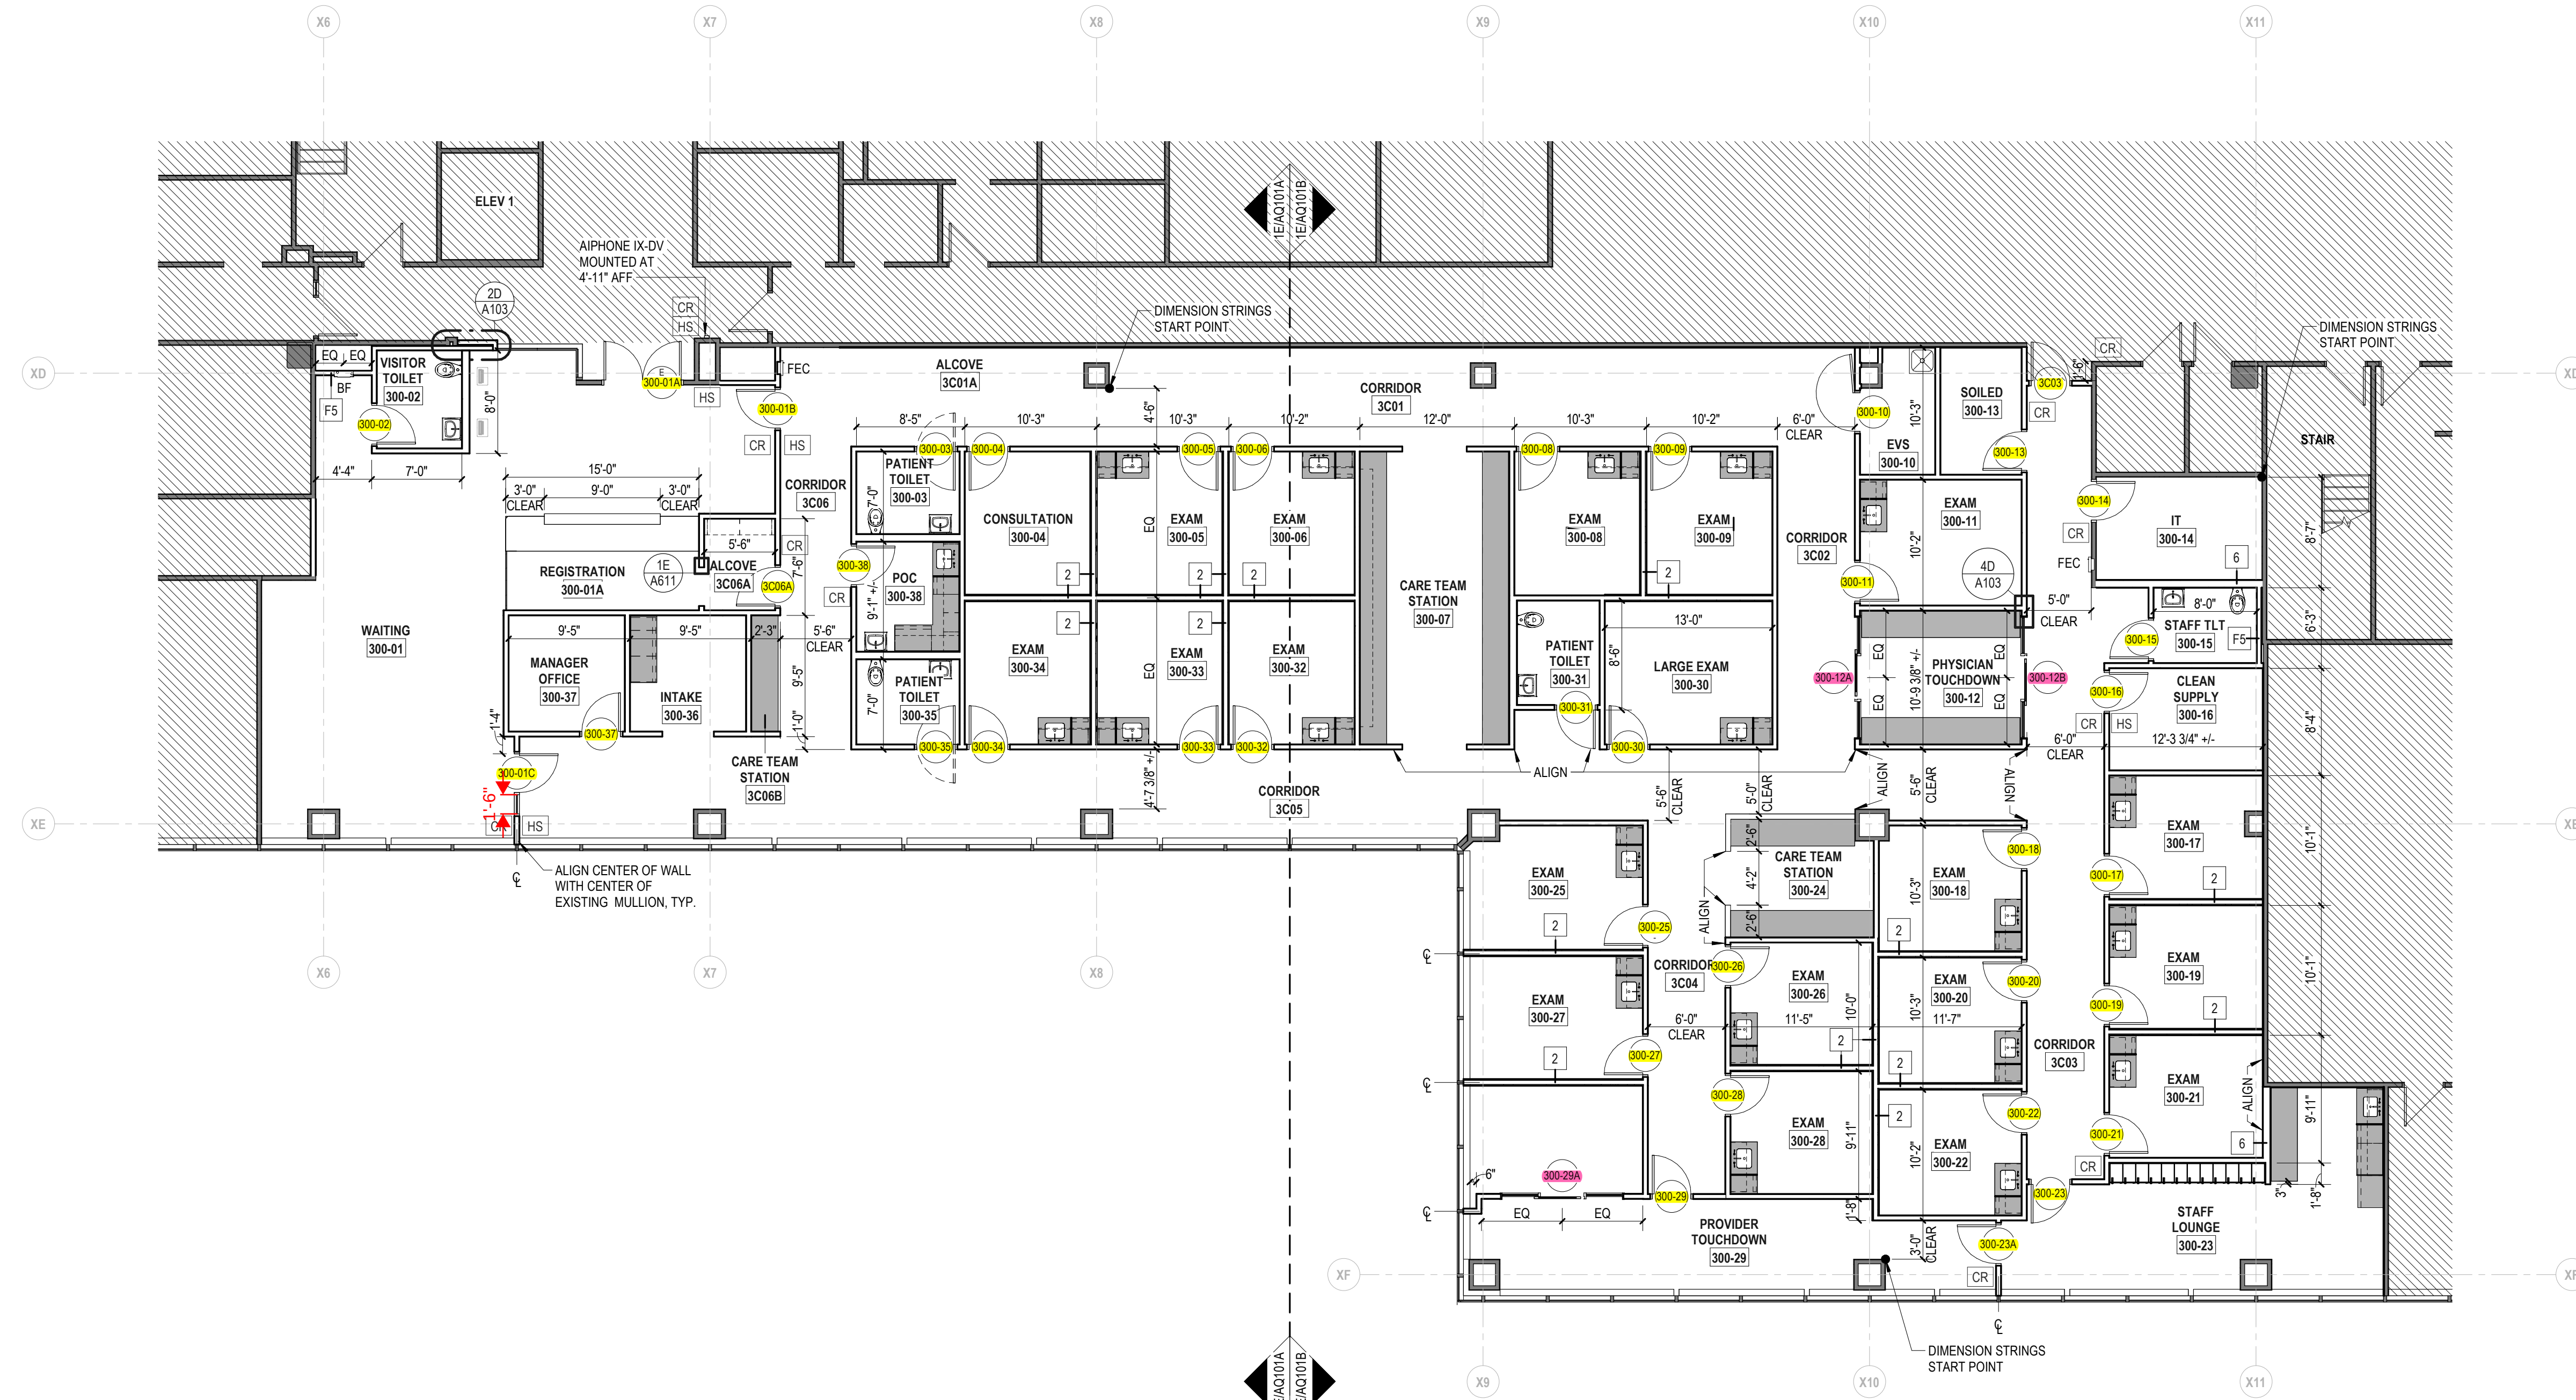

2C OVERALL THIRD FLOOR PLAN
1/8" = 1'-0"

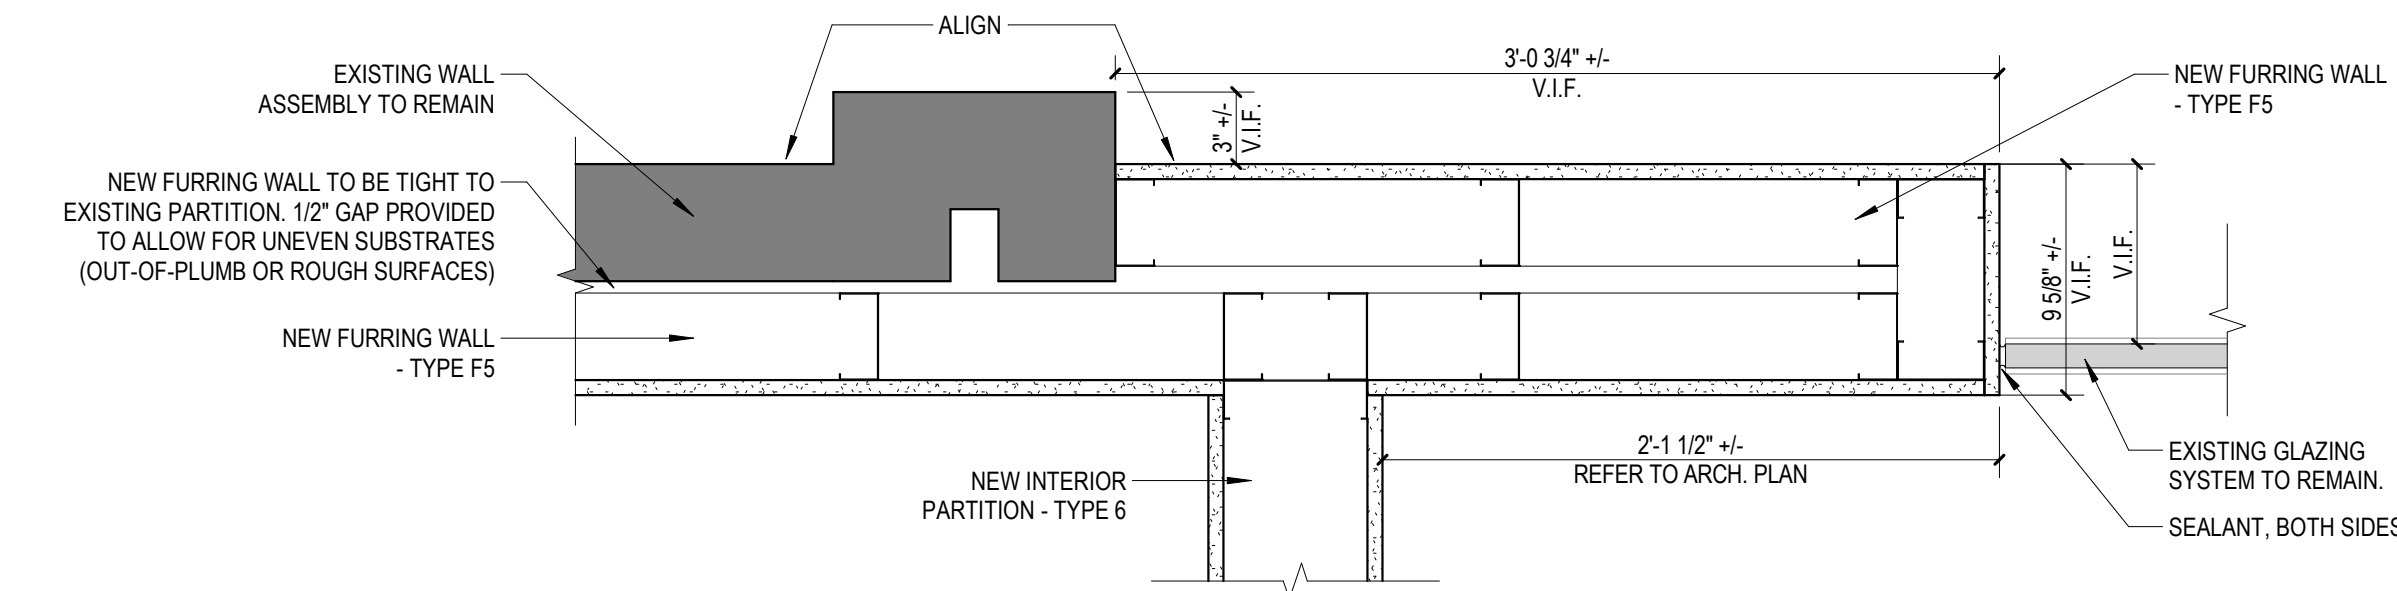

2D PLAN DETAIL - MODIFIED EXISTING GLAZING SYSTEM
1 1/2" = 1'-0"

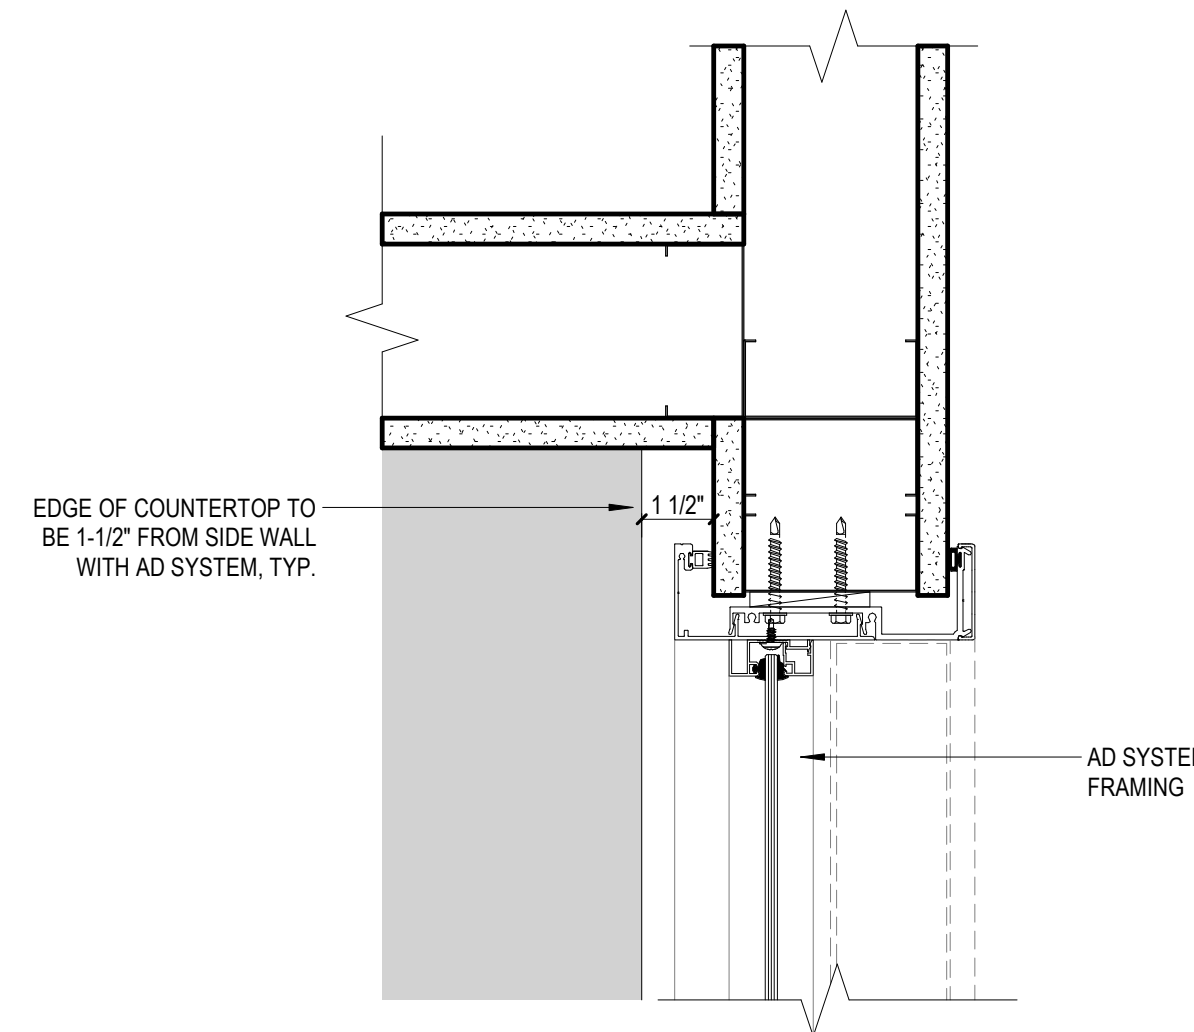

4D PLAN DETAIL - CORNER AT PHYSICIAN TOUCHDOWN, TYP.
3" = 1'-0"

FLOOR PLAN GENERAL NOTES

1. REFER TO GENERAL INFORMATION SHEET FOR LIST OF TYPICAL ABBREVIATIONS AND TYPICAL ARCHITECTURAL GRAPHIC LEGENDS AND SYMBOLS.
2. REFER TO TYPICAL PARTITION TYPES AND DETAILS. ALL PARTITIONS SHALL BE TYPE 1 UNLESS OTHERWISE NOTED.
3. REFER TO CODE INFORMATION AND FIRE SAFETY PLAN DRAWINGS FOR LOCATIONS OF FIRE-RESISTANCE RATED PARTITIONS AND NON-FIRE-RESISTANCE RATED SMOKE PARTITIONS.
4. ALIGN PARTITIONS WITH COLUMN OR MULLION CENTERLINE, UNLESS OTHERWISE NOTED.
5. DIMENSIONS ARE FROM FACE OF WALL, (I.E. FACE OF GYPSUM BOARD) OR FROM FACE OF EXISTING CONDITION OR FROM COLUMN CENTERLINE, UNLESS OTHERWISE NOTED. DIMENSIONS NOTED AS "CLEAR" SHALL BE FROM FINISH FACE TO FINISH FACE. (6. FACE OF CERAMIC TILE TO FACE OF CERAMIC TILE). VERIFY ALL EXISTING DIMENSIONS IN THE FIELD.
6. REFER TO PLAN ENLARGEMENTS FOR ADDITIONAL DIMENSIONS.
7. REFER TO DOOR AND FRAME DETAILS FOR ADDITIONAL INFORMATION. PROVIDE MINIMUM 4-INCH CLEARANCE FROM FACE OF DOOR JAMB TO FACE OF ADJACENT WALL, UNLESS OTHERWISE NOTED.
8. REFER TO TYPICAL MOUNTING LOCATIONS AND HEIGHTS FOR TOILET ACCESSORIES, EQUIPMENT, WALL SPECIALTY DESIGNATIONS, ETC.; TYPICAL TOILET ROOM ELEVATIONS AND TOILET ACCESSORY SCHEDULE.
9. PROVIDE FIRE-TREATED WOOD BLOCKING OR MINIMUM 0.0312-INCH THICK STEEL FLAT STRAP AND BACKING PLATE AT, BUT NOT LIMITED TO, THE FOLLOWING LOCATIONS: TOILET ACCESSORIES, CASEWORK, MILLWORK, DOOR WALL BUMPERS, AND ALL OTHER WALL MOUNTED EQUIPMENT OR DEVICES.
10. REFERENCING THE FIRE SAFETY PLANS, ALL EXISTING PARTITIONS INDICATED TO SERVE AS FIRE BARRIERS, FIRE PARTITIONS, SMOKE BARRIERS OR SMOKE PARTITIONS NEED TO MEET ALL REQUIREMENTS FOR STATED FIRE AND/OR SMOKE RATING.
A. CONSTRUCTION OF PARTITION MUST MATCH REQUIREMENTS FOR STATED RATING AND UL LISTING.
B. EXTENTS OF PARTITION MUST EXTEND FULL HEIGHT, SEALED TO UNDERSIDE OF DECK ABOVE PARTITION TO EXTEND FULL LENGTH WITHOUT GAPS OR INTERRUPTIONS.
C. FIRESTOPPING MUST BE PROVIDED AT ALL HOLES, PENETRATIONS AND EDGES.
12. REFER TO THE EQUIPMENT PLANS FOR RESIDENTIAL APPLIANCE, AND TOILET ACCESSORY LOCATIONS. REFER TO THE EQUIPMENT PLANS FOR EQUIPMENT LOCATIONS AND SCHEDULE.
13. REFER TO THE FINISH PLANS FOR FLOOR PATTERNS.
14. FLOOR PATCH AND FLOOR LEVELING: REPAIR EXISTING TOPPING SLAB AND CONCRETE FLOOR AT DEMOLITION OF WALLS AND AT ALL OTHER LOCATIONS AS REQUIRED. REFER TO DEMOLITION PLANS FOR ADDITIONAL INFORMATION.
15. PATCHING AND REPAIRING OF EXISTING PARTITIONS, CEILINGS, FLOORS, ETC. TO MATCH EXISTING ADJACENT CONSTRUCTION AND FINISHES, UNLESS OTHERWISE NOTED.
A. PROVIDE PATHWAYS AND OPENINGS AS REQUIRED FOR ALL INTERSECTING TRADES (EXISTING & NEW), AND THEN PATCH TO MATCH EXISTING. THIS INCLUDES AREAS OF EXISTING CONSTRUCTION ALTERED AND/OR DISTURBED BY THE DEMOLITION, INSTALLATION AND/OR RELOCATION OF ME/P/AVIT SERVICES, EQUIPMENT AND DEVICES.
B. PATCH AND REPAIR ALL AREAS ADJACENT TO, OR DISTURBED BY, NEW CONSTRUCTION AND/OR EXISTING CONSTRUCTION SCHEDULED TO BE DEMOLISHED.
C. PATCH, REPAIR AND PREP ALL EXISTING SURFACES THAT ARE TO RECEIVE NEW MATERIALS, FINISHES, ETC.

FLOOR PLAN GRAPHIC LEGEND

- NEW WALL CONSTRUCTION
- EXISTING WALL CONSTRUCTION TO REMAIN
- CASEWORK
- FEC FIRE EXTINGUISHER CABINET
- CR CARD READER
- HS AUTOMATIC - HAND SWIPE
- BF BOTTLE FILLER
- Z LOCKER
- FPD FLAT PANEL DISPLAY
- NOT IN SCOPE

Drawn
ES, JC

Checked

SRD

YaleNewHavenHealth

Northeast Medical Group Ambulatory Expansion

440 Mamaroneck Ave.
Harrison, NY

Suite 301



Number	Date	Issued For

THIRD FLOOR PLAN & PLAN DETAILS

Date
4/10/2026
Scale
As indicated
Proj. Number
25195.25

Drawing Number
A103