


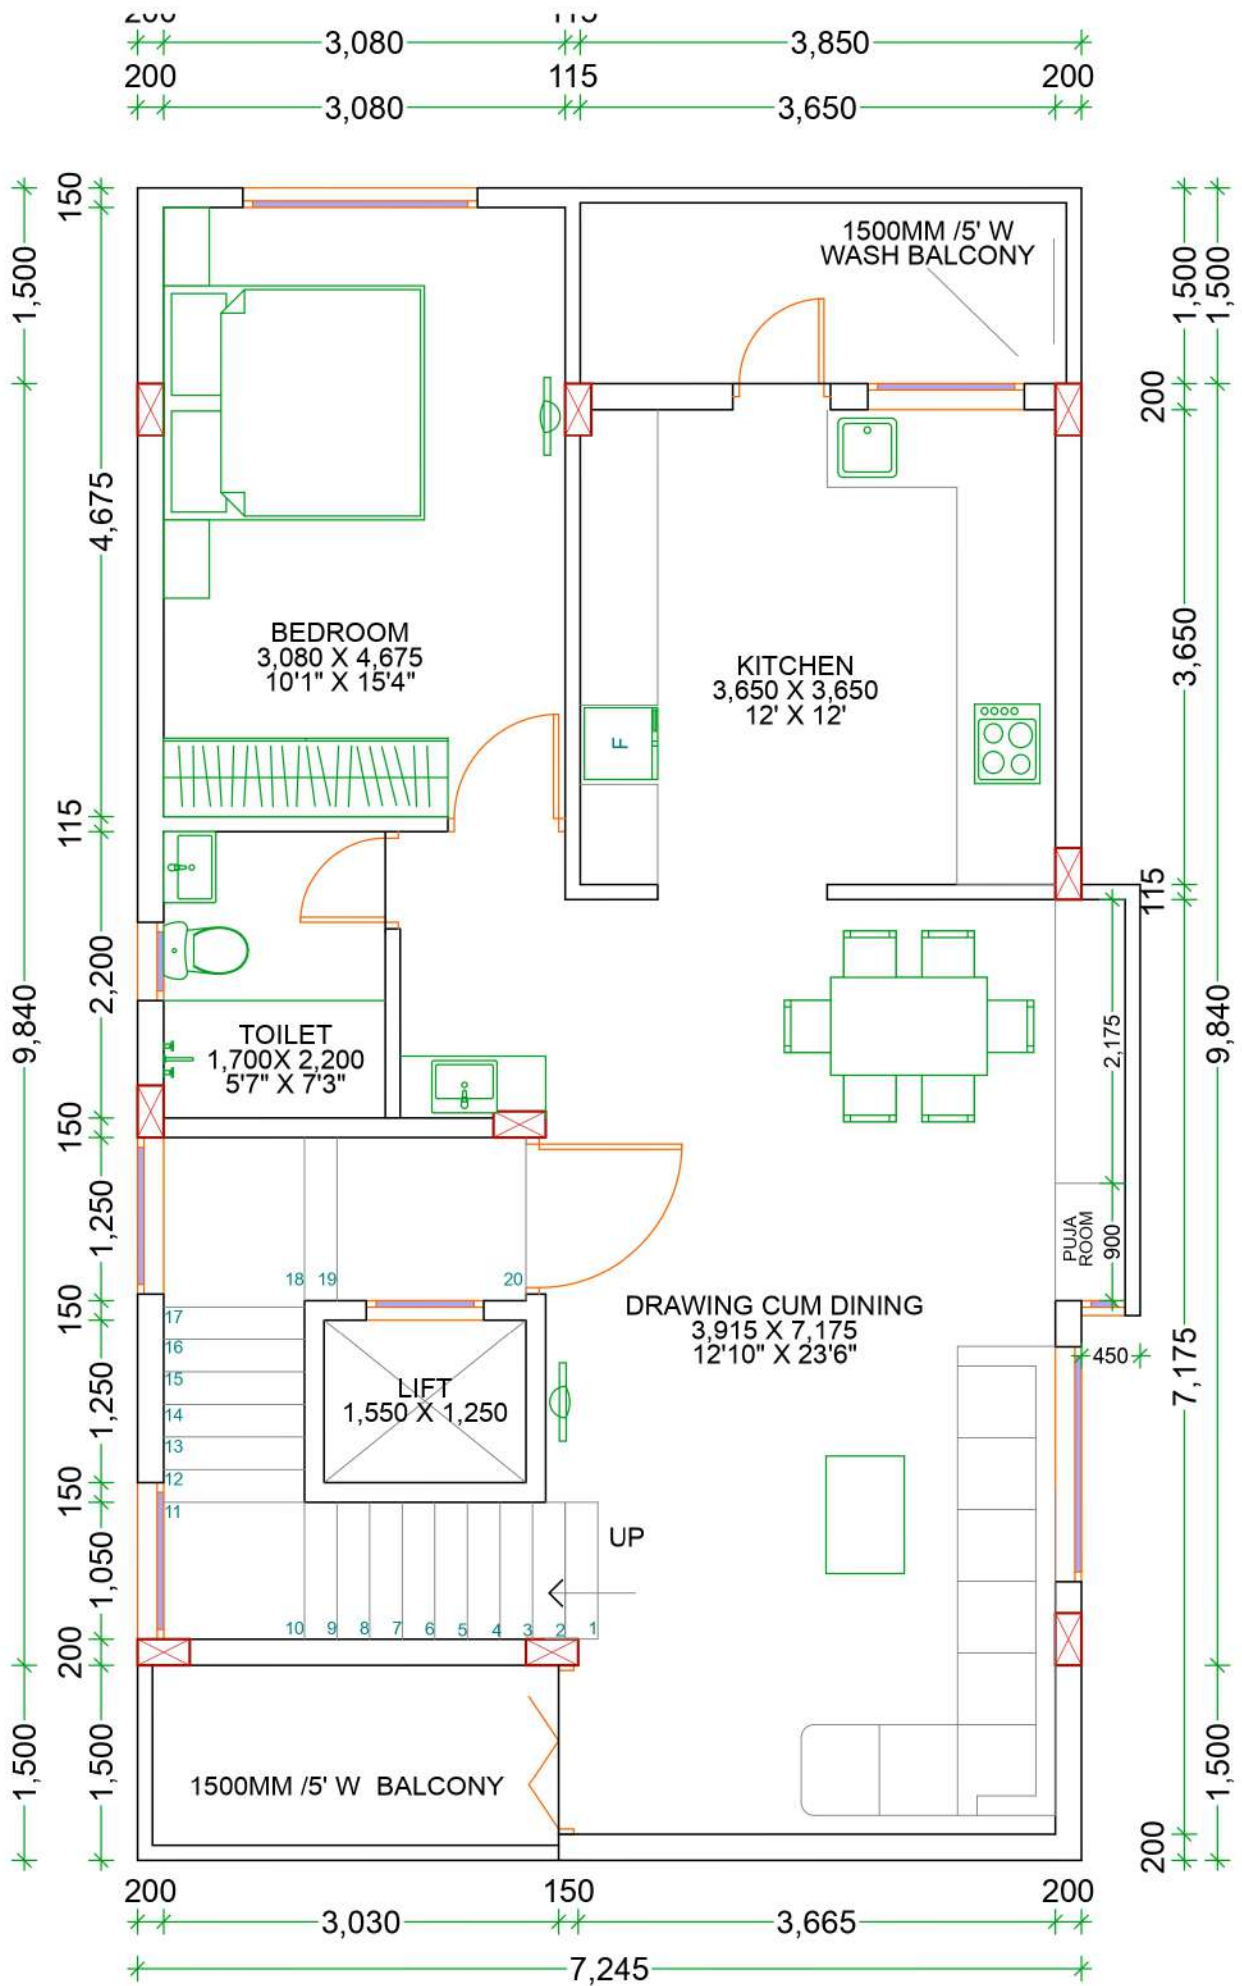

CLIENT :
SUNIL MAHANT

FIRST FLOOR

DWG NO.

1

REV NO.

10

ALL DIM. ARE IN MM

DATE :22/02/2018

SCALE :1:65

PROJECT NO.

DRAWN BY

AR.TRIPTI


CHECKED BY.

AR.RAJESH

NORTH



.RSA LAB
RAJESH SHAH ARCHITECTS
SHOP NO. 1, JAMUNNA CHS 3,
BESIDES NNS BANK, DR. AMBEDKAR
SQUARE, CENTRAL AVENUE,
NAGPUR 440008
rsalabindia@gmail.com
+91 712 27 67 318

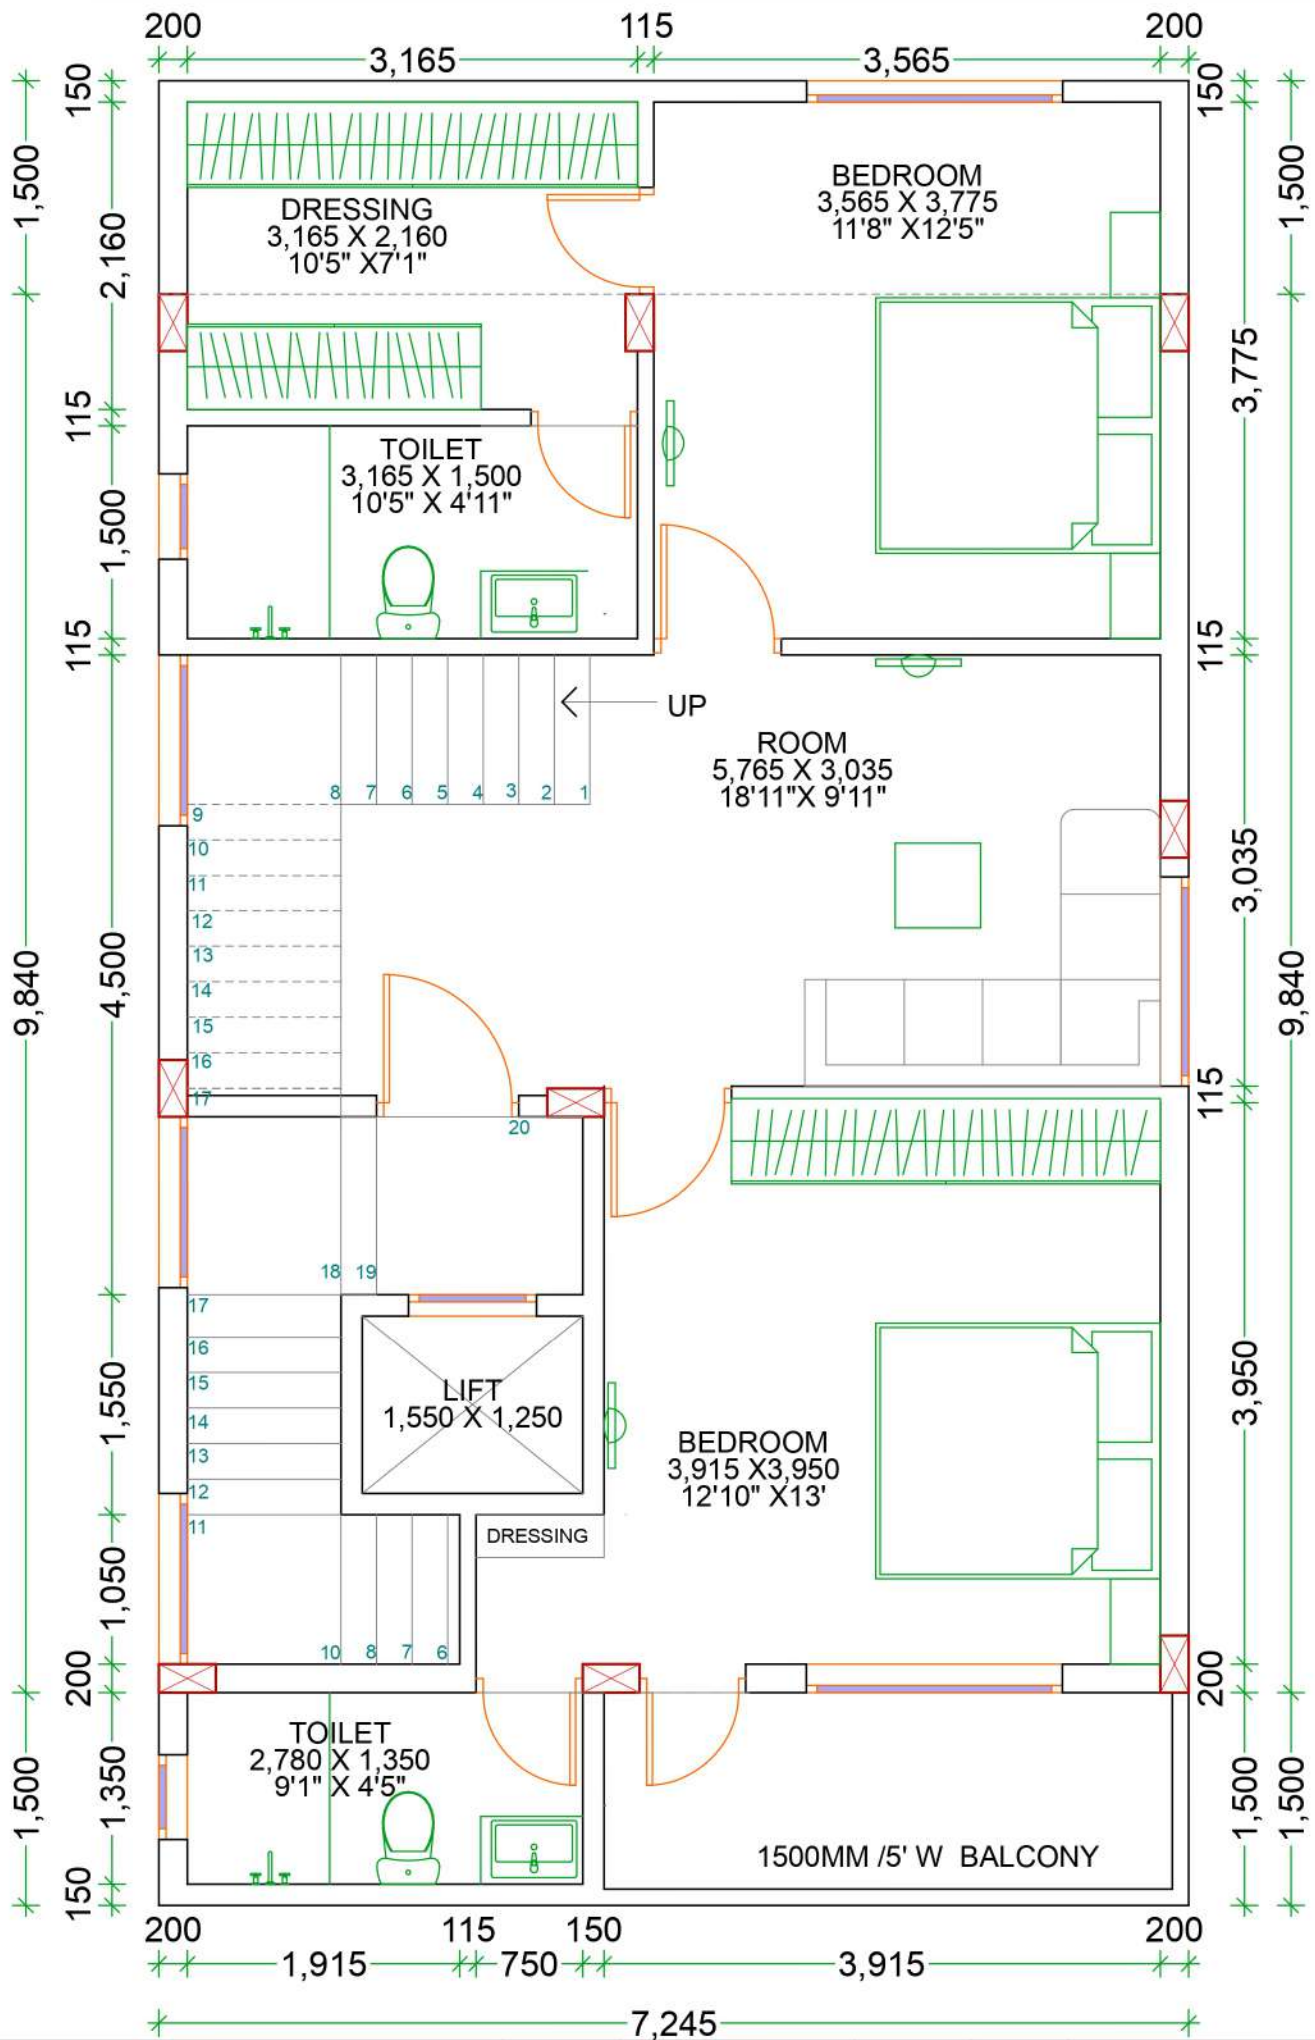

CLIENT :
SUNIL MAHANT

SECOND FLOOR

DWG NO.

1

REV NO.

12

ALL DIM. ARE IN MM

DATE :22/02/2018

SCALE :1:65

PROJECT NO.

DRAWN BY

AR.TRIPTI


CHECKED BY.

AR.RAJESH

NORTH



.RSA LAB
RAJESH SHAH ARCHITECTS
SHOP NO. 1, JAMUNNA CHS 3,
BESIDES NNS BANK, DR. AMBEDKAR
SQUARE, CENTRAL AVENUE,
NAGPUR 440008
rsalabindia@gmail.com
+91 712 27 67 318

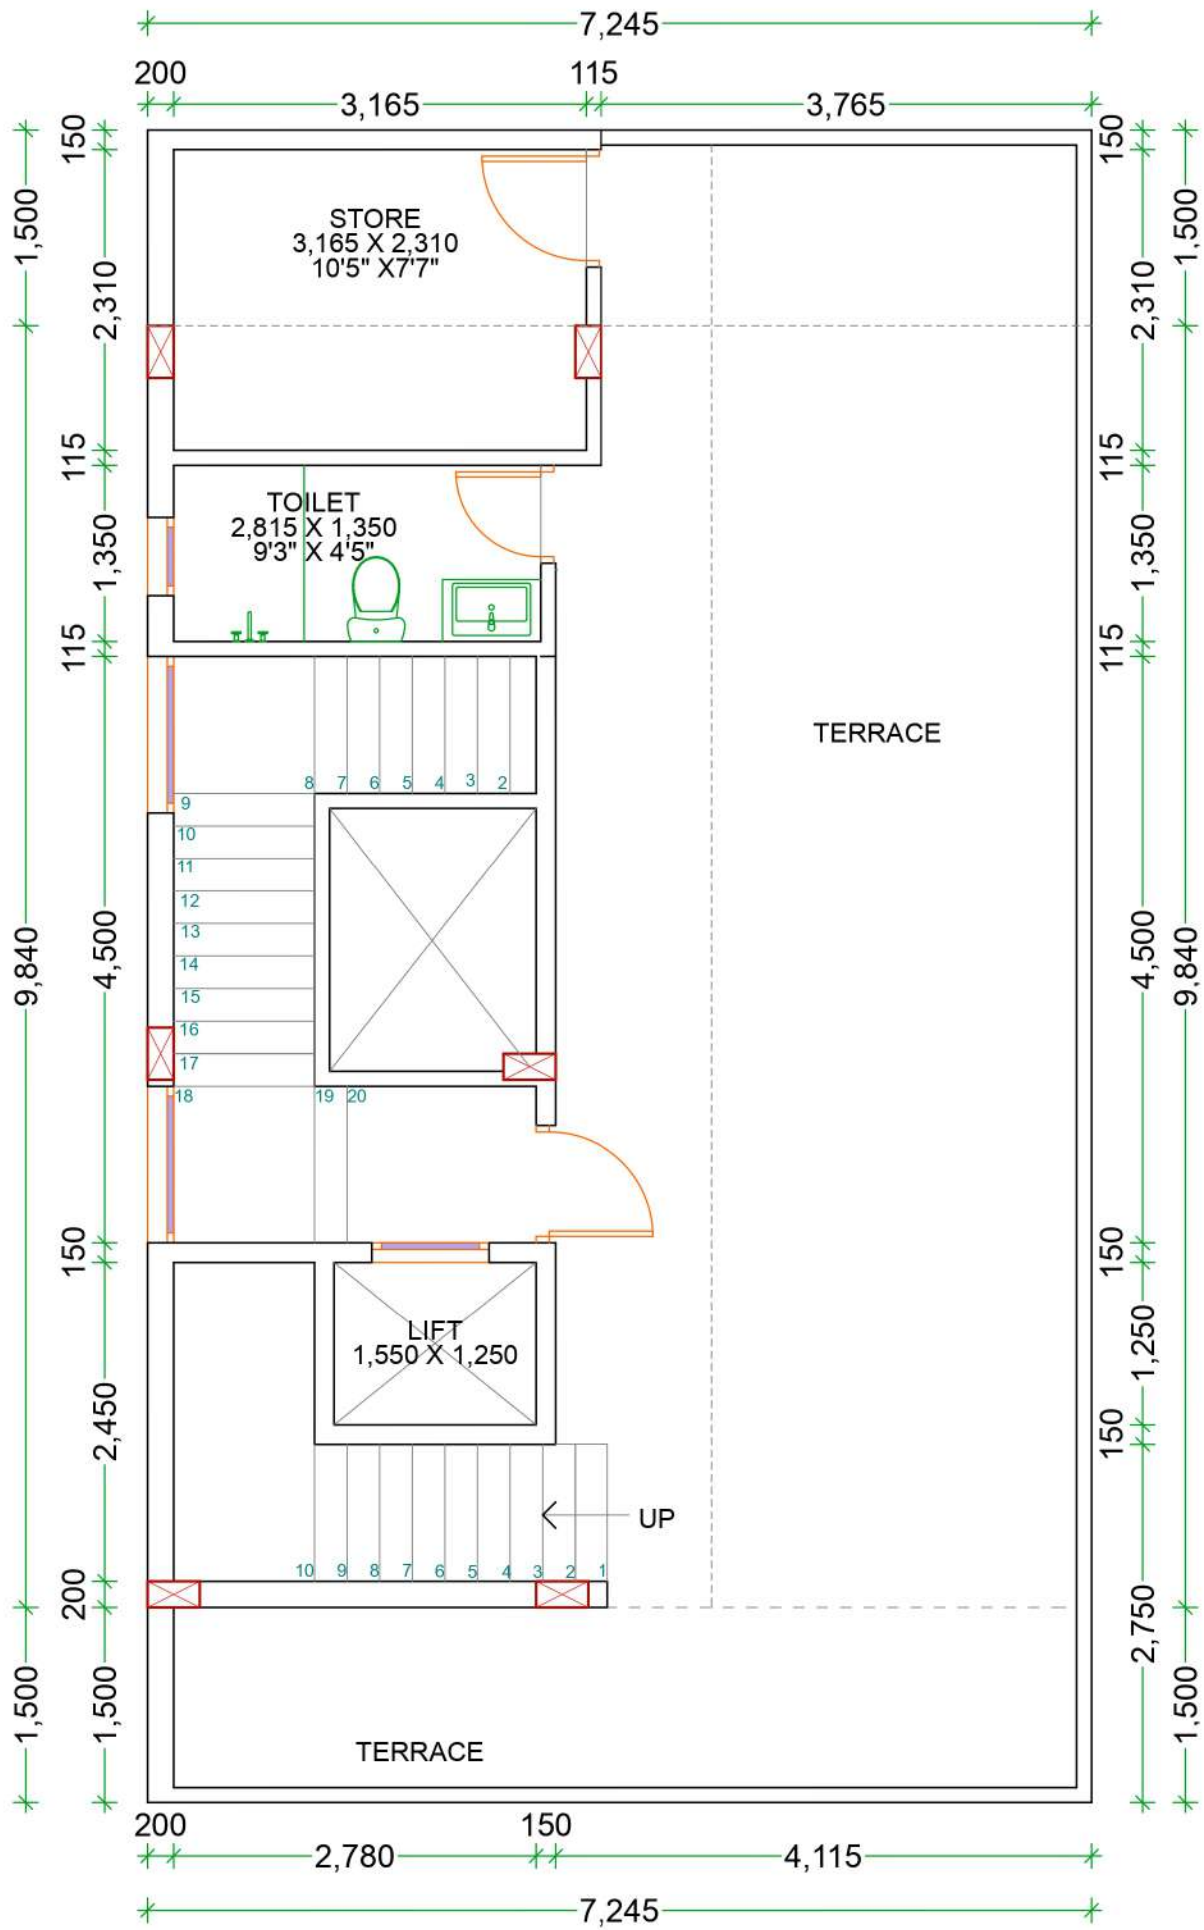

CLIENT :
SUNIL MAHANT

Terrace Floor

DWG NO.

1

REV NO.

12

ALL DIM. ARE IN MM

DATE :22/02/2018

SCALE :1:65

PROJECT NO.

DRAWN BY

AR.TRIPTI

CHECKED BY.

AR.RAJESH

NORTH



.RSA LAB
RAJESH SHAH ARCHITECTS
SHOP NO. 1, JAMUNNA CHS 3,
BESIDES NNS BANK, DR. AMBEDKAR
SQUARE, CENTRAL AVENUE,
NAGPUR 440008
rsalabindia@gmail.com
+91 712 27 67 318