


D

C

B

A

DOOR SCHEDULE							
MARK	TYPE MARK	SIZE			FIRE RATING	HARDWARE SET NO.	COMMENTS
		WIDTH	HEIGHT	THICKNESS			
FIRST LEVEL							
101A	A	3' - 0"	7' - 0"	1 3/4"		04	
101B	F	2' - 8"	6' - 8"	1 3/4"		04	
SECOND LEVEL							
201A	F	2' - 8"	6' - 8"	1 3/4"		04	
201B	F	2' - 8"	6' - 8"	1 3/4"		04	
THIRD LEVEL							
301A	F	2' - 8"	6' - 8"	1 3/4"		04	
301B	F	2' - 8"	6' - 8"	1 3/4"		04	
FOURTH LEVEL							
401A	F	2' - 8"	6' - 8"	1 3/4"		04	
401B	F	2' - 8"	6' - 8"	1 3/4"		04	
CLUBHOUSE							
C101A	C	5' - 0"	7' - 0"	1 3/4"		01	ACCESS CONTROL
C102A	H	3' - 0"	7' - 0"	1 3/4"		03	ACCESS CONTROL
C102B	H	3' - 0"	7' - 0"	1 3/4"		03	ACCESS CONTROL
C104A	A	3' - 0"	7' - 0"	1 3/8"		15	
C105A	H	3' - 0"	7' - 0"	1 3/4"		02	ACCESS CONTROL
C106A	A	3' - 0"	7' - 0"	1 3/4"		16	
C106B	E	2' - 4"	7' - 0"	1 3/8"		05	
C106C	E	2' - 4"	7' - 0"	1 3/8"		06	
C107A	H	3' - 0"	7' - 0"	1 3/8"		14	ACCESS CONTROL
C108A	A	3' - 0"	7' - 0"	1 3/8"		11	
C108B	H	3' - 0"	7' - 0"	1 3/4"		12	
C109A	A	3' - 0"	7' - 0"	1 3/8"		07	
C109B	A	3' - 0"	7' - 0"	1 3/4"		13	
C109C	U10	2' - 10"	7' - 0"	1 3/8"		08	
C110A	A	3' - 0"	7' - 0"	1 3/8"		07	
C110B	A	3' - 0"	7' - 0"	1 3/4"		13	
C110C	U10	2' - 10"	7' - 0"	1 3/8"		08	
C111A	A	3' - 0"	7' - 0"	1 3/8"		09	
C111B	L	2' - 7 1/2"	6' - 6 3/4"	1"		10	POCKET DOOR
C112A	U10	2' - 10"	7' - 0"	1 3/8"		17	
C113B	A	3' - 0"	7' - 0"	1 3/4"		04	FIRE RISER
G.01	J	4' - 0"	6' - 0"			G1	
G.02	J	4' - 0"	6' - 0"			G1	
MAINTENANCE SHED							
M101A	G	12' - 0"	8' - 0"	1 1/2"		R1	ELECTRIC OVERHEAD DOOR
M102A	A	3' - 0"	7' - 0"	1 3/4"		04	
M103A	A	3' - 0"	7' - 0"	1 3/8"		06	

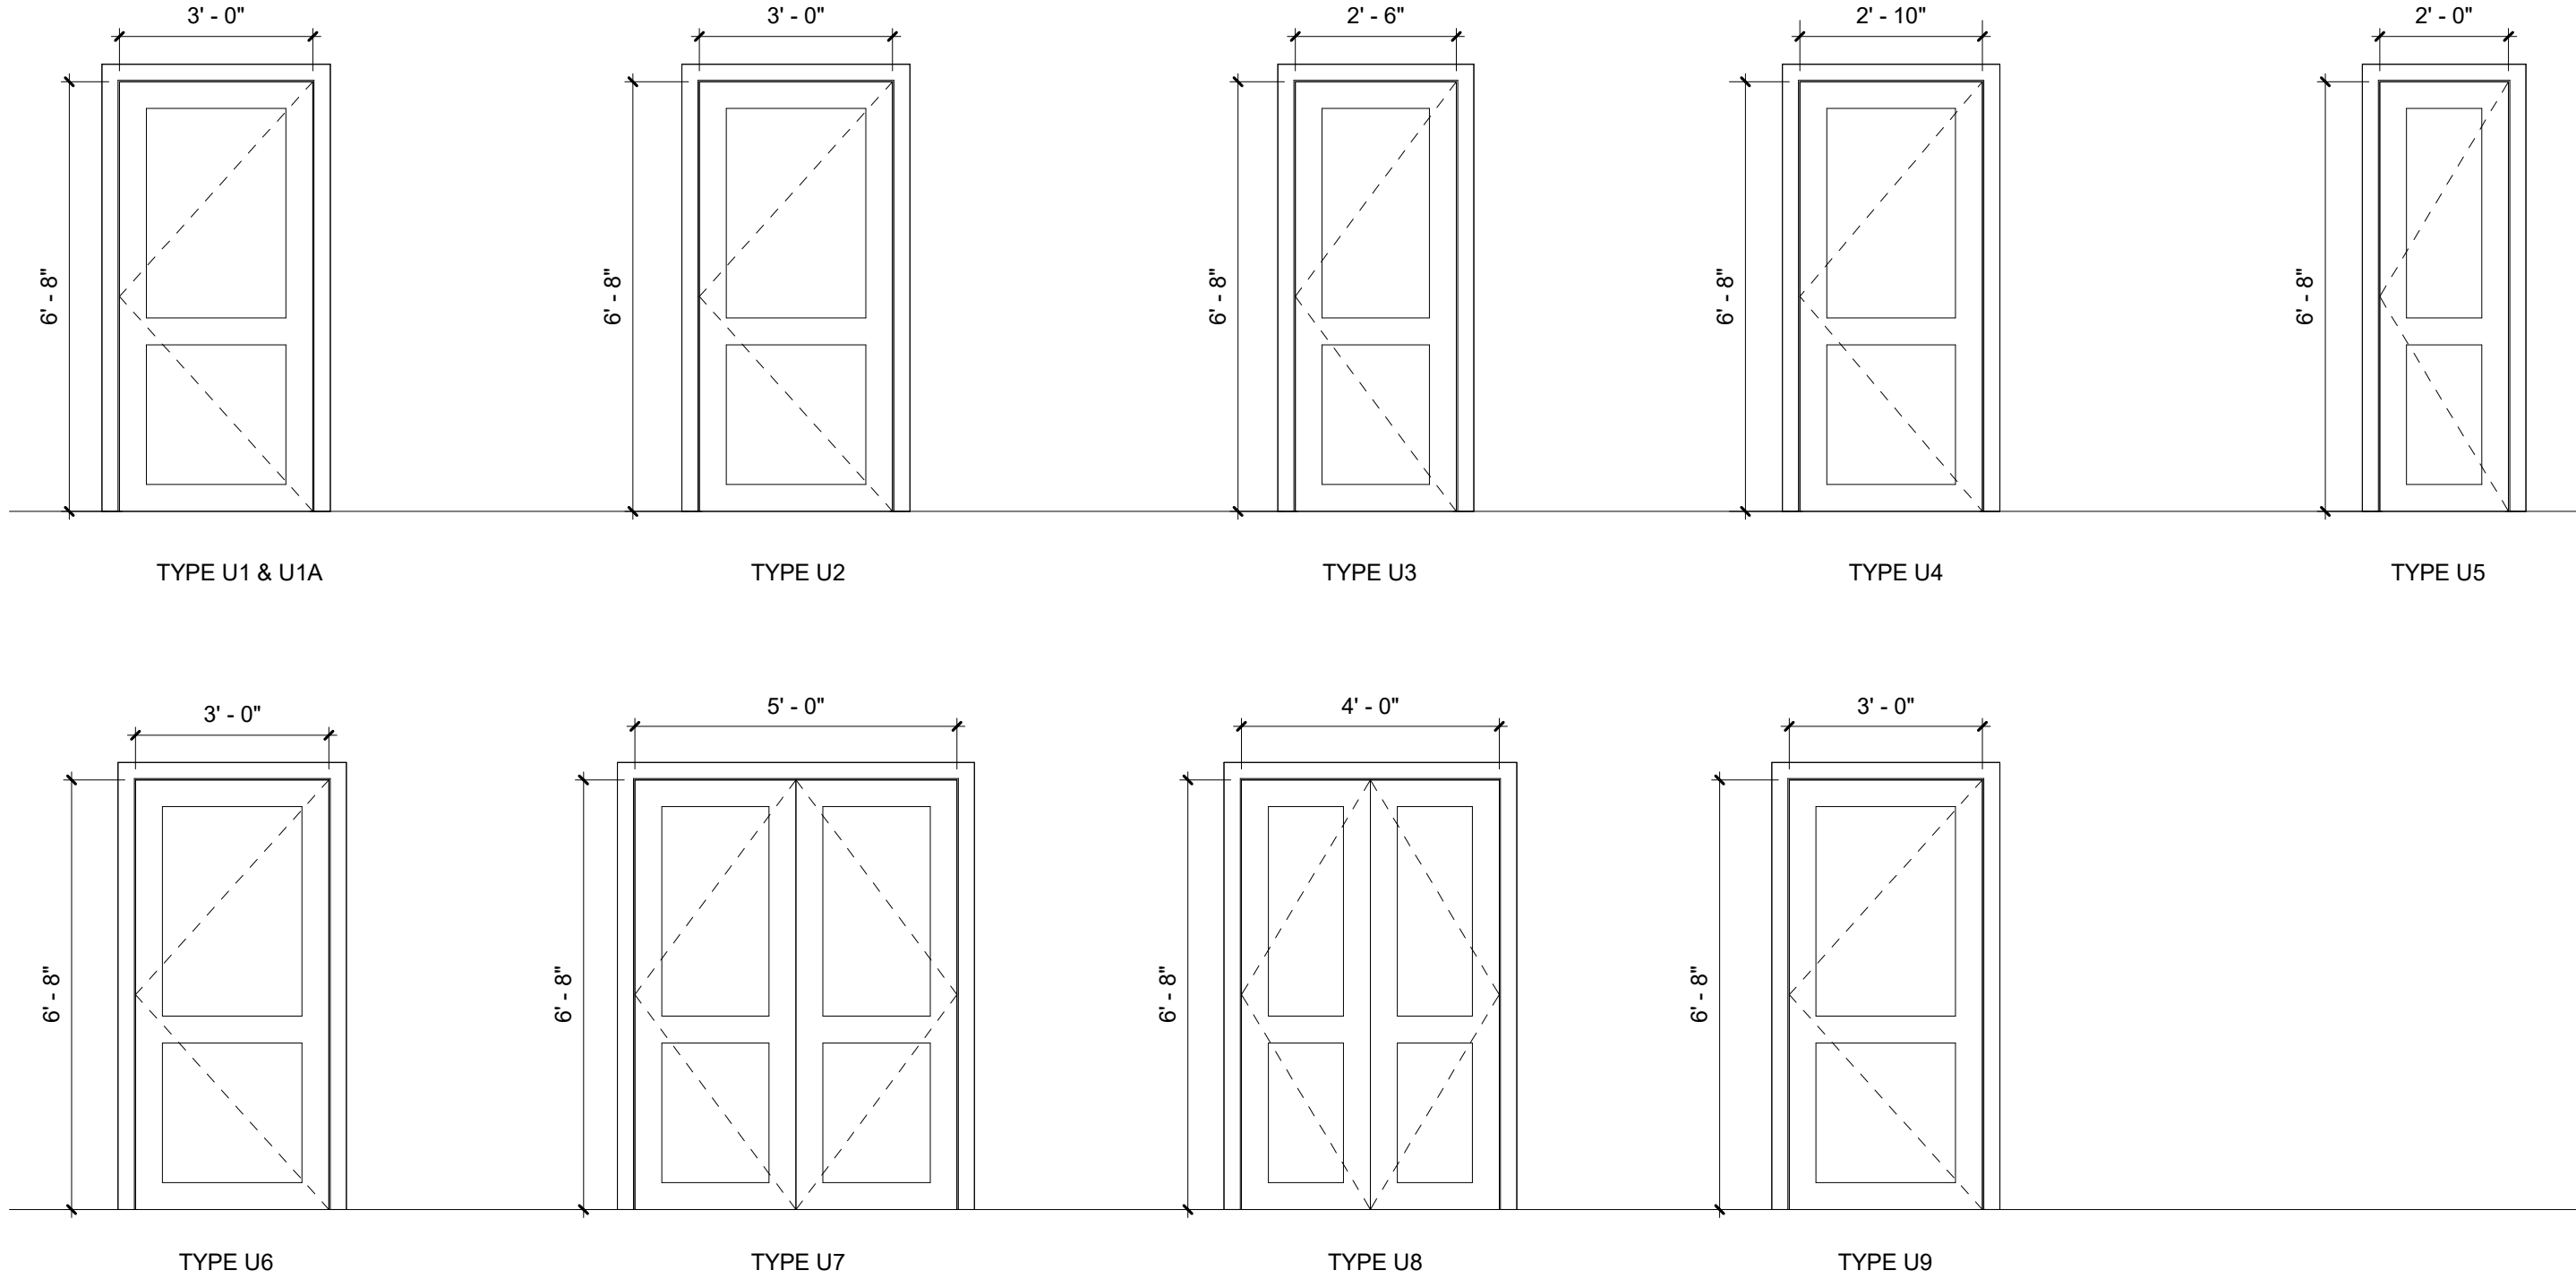


UNIT DOOR TYPES

3/8" = 1'-0"

UNIT DOOR SCHEDULE								
TYPE MARK	SIZE			PANEL TYPE	FRAME TYPE	FIRE RATING	HARDWARE SET NO.	COMMENTS
	WIDTH	HEIGHT	THICKNESS					
U1	3' - 0"	6' - 8"	1 3/4"	FIBERGLASS	WOOD	90 MIN.	U-01	DOORS HAVE A CLEAR WIDTH OF 2' - 9 3/4"
U1A	3' - 0"	6' - 8"	1 3/4"	FIBERGLASS	WOOD	90 MIN.	U-01	DOORS HAVE A CLEAR WIDTH OF 2' - 9 3/4"
U2	3' - 0"	6' - 8"	1 3/8"	HOLLOW CORE WOOD	WOOD		U-02	DOORS HAVE A CLEAR WIDTH OF 2' - 9 3/4"
U2A	3' - 0"	6' - 8"	1 3/8"	HOLLOW CORE WOOD	WOOD		U-03	DOORS HAVE A CLEAR WIDTH OF 2' - 9 3/4"
U3	2' - 6"	6' - 8"	1 3/4"	HOLLOW CORE WOOD	WOOD			
U4	2' - 10"	6' - 8"	1 3/8"	HOLLOW CORE WOOD	WOOD		U-03	
U5	2' - 0"	6' - 8"	1 3/8"	HOLLOW CORE WOOD	WOOD		U-03	
U6	3' - 0"	6' - 8"	1 3/8"	HOLLOW CORE WOOD	WOOD		U-02	DOORS HAVE A CLEAR WIDTH OF 2' - 9 3/4"
U7	5' - 0"	6' - 8"	1 3/8"	HOLLOW CORE WOOD	WOOD		U-04	
U8	4' - 0"	6' - 8"	1 3/8"	HOLLOW CORE WOOD	WOOD		U-04	
U9	3' - 0"	6' - 8"	1 3/8"	HOLLOW CORE WOOD	WOOD		U-03	DOORS HAVE A CLEAR WIDTH OF 2' - 9 3/4"

DOORS IN FIRE RATED CORRIDORS (DOOR TYPES U1 AND U3) SHALL COMPLY WITH IBC 716.2.2.1

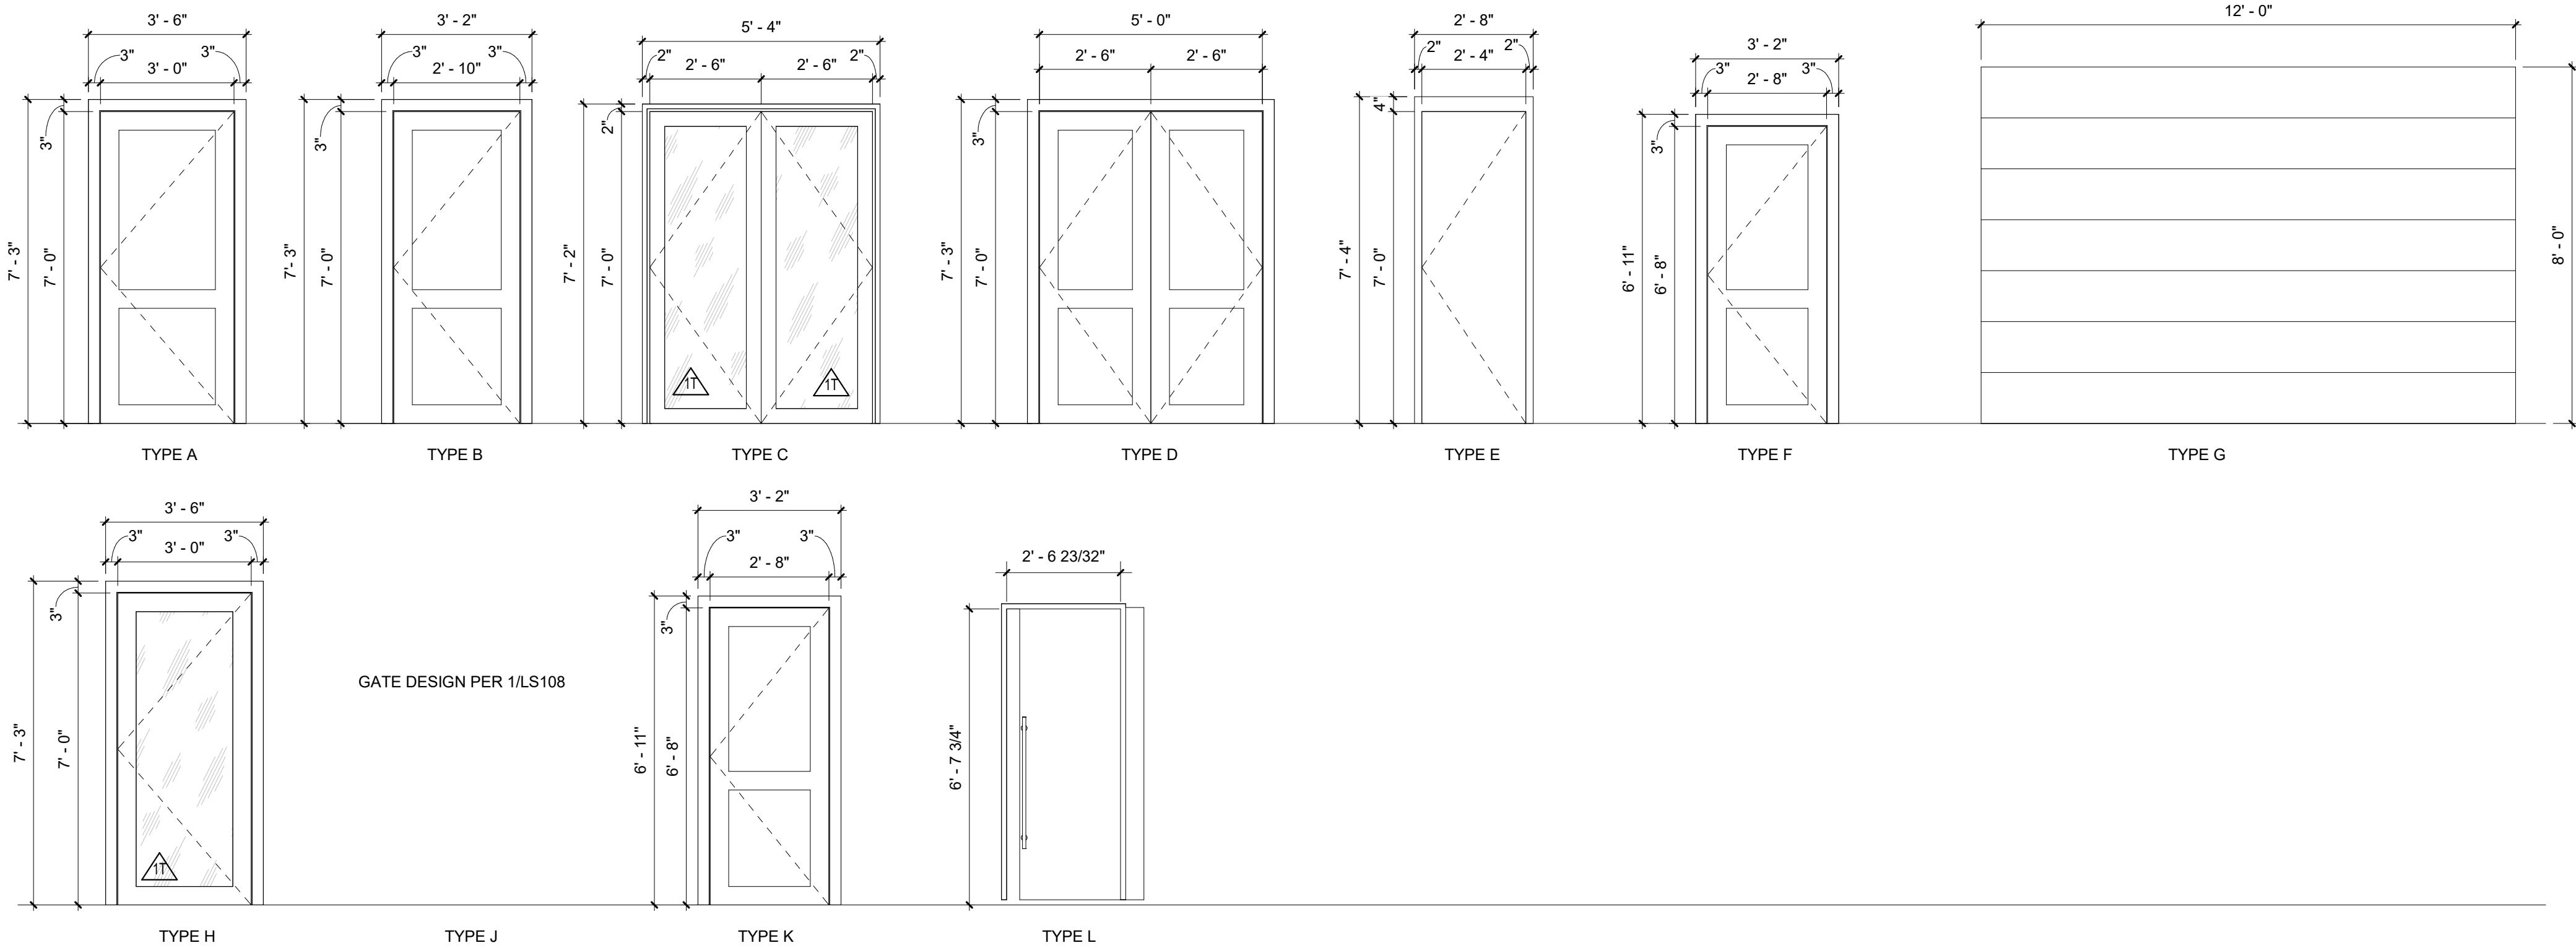

DOOR TYPES

3/8" = 1'-0"

GLASS TYPES

3/4" (3/16" - 3/8" - 3/16") INSULATED, CLEAR LOW-E GLAZING SYSTEM, U-VALUE = 0.35 OR BETTER, SOLAR HEAT GAIN COEFFICIENT = 0.40 OR BETTER

3/4" (3/16" - 3/8" - 3/16") INSULATED TEMPERED, CLEAR LOW-E GLAZING SYSTEM, U-VALUE = 0.35 OR BETTER, SOLAR HEAT GAIN COEFFICIENT = 0.40 OR BETTER

CRSA

ARCHITECTURE • PLANNING • INTERIORS

175 S MAIN STREET, STE 300 • SLC, UTAH 84111
801-355-5915 www.crsa-us.com

ENSGN
THE STANDARD IN ENGINEERING

Ensign Engineering and Land Survey
45 West 10000 South, Ste. 500
Sandys, Utah 84070
Phone: 801.255.0529
www.ensignutah.com

BHB STRUCTURAL

2744 S. Main Street
Salt Lake City, Utah 84115
801.355.5656
bhb@bhbengineers.com

VAN BOERUM & FRANK ASSOCIATES, INC.
CONSULTING ENGINEERS
WWW.VBFA.COM

VBFA
40 W. 1250 N. STE. 1B
LOGAN, UT 84341

393 East Riverside Drive
Suite 202
St. George, Utah 84770
P: 435.628.3670
F: 435.628.3680
www.bnaconsulting.com
© 2011 BNA CONSULTING

BNA CONSULTING
SALT LAKE ST. GEORGE

393 East Riverside Drive
Suite 202
St. George, Utah 84770
P: 435.628.3670
F: 435.628.3680
www.bnaconsulting.com
© 2011 BNA CONSULTING

DESERT EDGE architecture

720 S. RIVER RD, SUITE D2100B
ST. GEORGE, UTAH 84790
P: 435.673.7362

Water Design Inc.
Water Design, Inc.

6740 S 1300 E, Suite 110
Salt Lake City, Utah 84121
P: 801.261.4009

NORTHERN FLATS APARTMENTS

CORNER OF KNUDSEN BLVD
AND HAWTHORNE RD
CHUBBUCK, IDAHO 83202

STAMP



ISSUE TYPE:	DATE:
PERMIT SET	2022-4-30
1 ASI #01	2022-03-25
2 ASI #02	2022-3-29
PROJECT NUMBER:	21-065
DRAWN BY:	TRM
CHECKED BY:	SG

DOOR TYPES AND SCHEDULE

AE601