

D

C

OPTION B



1. REFER TO SPECIFICATIONS FOR ADDITIONAL INFORMATION
2. INSTALL WINDOW FLASHING IN ORDER SHOWN
3. ADD CONTINUOUS AIR SEAL AROUND PERIMETER USING BACKER ROD AND SEALANT, OR LOW PRESSURE MINIMAL EXPANDING FOAM
4. SEALANT SHALL BE COMPATIBLE WITH MEMBRANE PRODUCT
5. UNDERLAYMENTS SHOULD BE INSTALLED TO FORM WATER-SHEDDING LAPS



B

$$\frac{3}{4}'' = 1'-0''$$

A



3/8" = 1'-0"

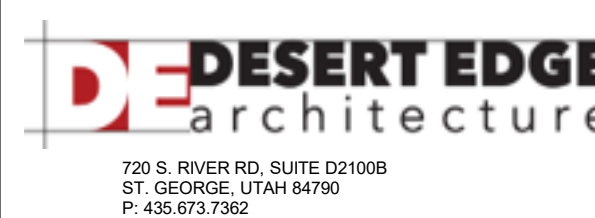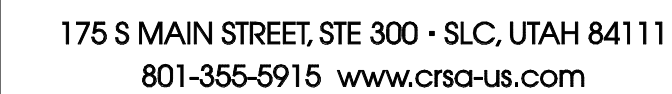

CORNER OF KNUDSEN BLVD
AND HAWTHORNE RD
CHUBBUCK, IDAHO 83202

LICENSE
ARCHITECT
AR-98718

SCOTT D. GILBERT
STATE OF IDAHO

ISSUE TYPE:	DATE:
PERMIT SET	2022-4-30
	
2 ASI #02	2022-3-29
PROJECT NUMBER:	21-065
DRAWN BY:	TRM
CHECKED BY:	SG

WINDOW TYPES

AE602