

DOOR AND OPENING LEGEND

AS PER CODE TAGGED AT EACH DOOR LOCATION ON CONSTRUCTION PLANS


OPENING CODE	GENERAL DESCRIPTION	RATING	PANEL TYPE	MAT'L	FINISH	DOOR				FRAME			SECTIONS		COMMENTS
						No. OF LEAVES	WIDTH	HEIGHT	THCKNS	TYPE	MAT'L	FINISH	JAMB	HEAD	
A	SINGLE FLUSH SWING	-	F	SC	PT	1	3'-0"	8'-0"	1-3/4"	01	HM	PT	2/A621	1/A621	-
A.1	SINGLE FLUSH SWING	-	F	MILLWORK	WDV-1	1	3'-0"	8'-0"	1-3/4"	01	WD	WDV-1	10/A621	9/A621	MILLWORK FRAME AND DOOR
A.2	SINGLE FLUSH SWING	90	EX	EX	PT	1	EX	EX	EX	01	HM	PT	EX	EX	NOTE 3
A.3	SINGLE FLUSH SWING	-	F	SC	PT	1	MATCH EXISTING	MATCH EXISTING	MATCH EXISTING	01	HM	PT	2/A621	1/A621	NOTE 2
B	PAIR FLUSH SWING	-	F	MILLWORK	PT	2	3'-0 7/8"-0"	8'-11.5"	1-3/4"	01	WD	PT	8/A621	6/A621 SIM	-
B.1	PAIR FLUSH SWING	-	FP	SC	PT	2	3'-0 7/8"-0"	8'-0"	1-3/4"	01	HM	PT	2/A621	1/A621	-
B.2	PAIR FLUSH SWING	-	FV	SC	PT	2	EX	EX	EX	01	HM	PT	2/A621	1/A621	-
C	CASED OPENING	-	-	-	-	-	3'-0"	8'-0"	-	02	HM	PT	4/A621	3/A621	-
D	DEMOUNTABLE OFFICE FRONT - SINGLE	-	D	AL/GL	FF	1	3'-0"	8'-10"	1-3/4"	-	AL	FF	A613	A613	-
D.1	DEMOUNTABLE OFFICE FRONT - SINGLE	-	D1	AL/GL	FF	1	3'-3"	8'-11.5"	1-3/4"	-	AL	FF	A613	A613	-
D.2	DEMOUNTABLE OFFICE FRONT - DOUBLE	-	D2	AL/GL	FF	2	3'-3 7/8"-3'	8'-10"	1-3/4"	-	AL	FF	A613	A613	-
D3	DOUBLE SWING - FULL GLASS	-	FG	GL	FF	2	3'-3 7/8"-3'	9'-0"	5/8"	-	-	-	-	7/A621	FRAMELESS GLASS DOOR BY OFFICE FRONT MANUFACTURER
D4	SINGLE ENTRY SWING - FULL LITE	-	DE	AL/GL	FF	1	3'-0"	9'-0"	1-3/4"	-	-	-	-	-	FULL-LIGHT ALUM./GLASS DOOR BY DEMOUNTABLE DOOR MANUF.
F	SINGLE FLUSH	45	F	SC	PT	2	3'-0"	8'-0"	1-3/4"	01	HM	PT	2/A621	1/A621	-
G	SINGLE FLUSH SWING	-	F	MILLWORK	PT	1	3'-0"	8'-10"	1-3/4"	01	WD	PT	6 / A621	5 / A621	CONCEALED WOOD FRAME
H	SINGLE FLUSH	-	F	SC	PT	1	VIF	VIF	1-3/4"	EX	EX	PT	EX	EX	NOTE 1
H1	SINGLE FLUSH	-	F	SC	PT	1	VIF	VIF	1-3/4"	EX	EX	PT	EX	EX	NOTE 1
H2	SINGLE FLUSH	-	EX	EX	PT	1	VIF	VIF	1-3/4"	EX	EX	PT	EX	EX	NOTE 4
J	SINGLE FLUSH SWING	-	F	WOOD	STAIN	1	3'-0"	9'-0"	1-3/4"	01	HM	PT	2/A621	1/A621	TO MATCH EXISTING BUILDING STANDARD CORRIDOR DOORS AND FRAMES

ABBREVIATIONS

AL ALUMINUM
EX EXISTING
GL GLASS
HM HOLLOW METAL
MLWK MILLWORK
MTL METAL
PT PAINT
SC SOLID CORE DOOR
STC SOUND TRANSMISSION CLASS
STL STEEL
WD WOOD


OPENING NOTES

- EXISTING CORE TOILET ROOM STALL DOORS ON FLOOR 20 TO BE REPLACED WITH FLUSH, PAINT GRADE WOOD DOOR, SAME OVERALL SIZE AND THICKNESS. VERIFY EXISTING CONDITIONS IN FIELD. PROVIDE NEW HARDWARE TO MATCH EXISTING IN NEW PROJECT FINISH.
- EXISTING CORE DOOR AND FRAME TO BE REPLACED WITH HM FRAME AND PAINT GRADE FLUSH WOOD DOOR OF SAME OVERALL SIZE. VERIFY EXISTING CONDITIONS IN FIELD.
- EXISTING DOOR RATINGS COULD NOT BE CONFIRMED AT TIME OF ARCHITECTURAL SURVEY. CONFIRM DOOR ASSEMBLY HAS A 90 MINUTE RATING. IF EXISTING DOOR HAS A 90 MINUTE RATING, THEN EXISTING EGRESS STAIR DOOR, FRAME, AND HARDWARE TO REMAIN. PAINT EXISTING DOOR AND FRAME TO MATCH ADJACENT WALL SURFACE. IF DOOR ASSEMBLY CAN NOT BE VERIFIED, THEN REPLACE DOOR AND FRAME WITH NEW 90 MINUTE ASSEMBLY TO MATCH EXISTING OPENING WITH PAINT GRADE DOOR AND FRAME.
- EXISTING TOILET ROOM DOOR TO REMAIN. REMOVE EXISTING HARDWARE AND REPLACE WITH NEW LIKE-FUNCTIONING HARDWARE IN NEW PROJECT FINISH. PREPARE DOOR AND FRAME TO RECEIVE NEW PAINT FINISH.

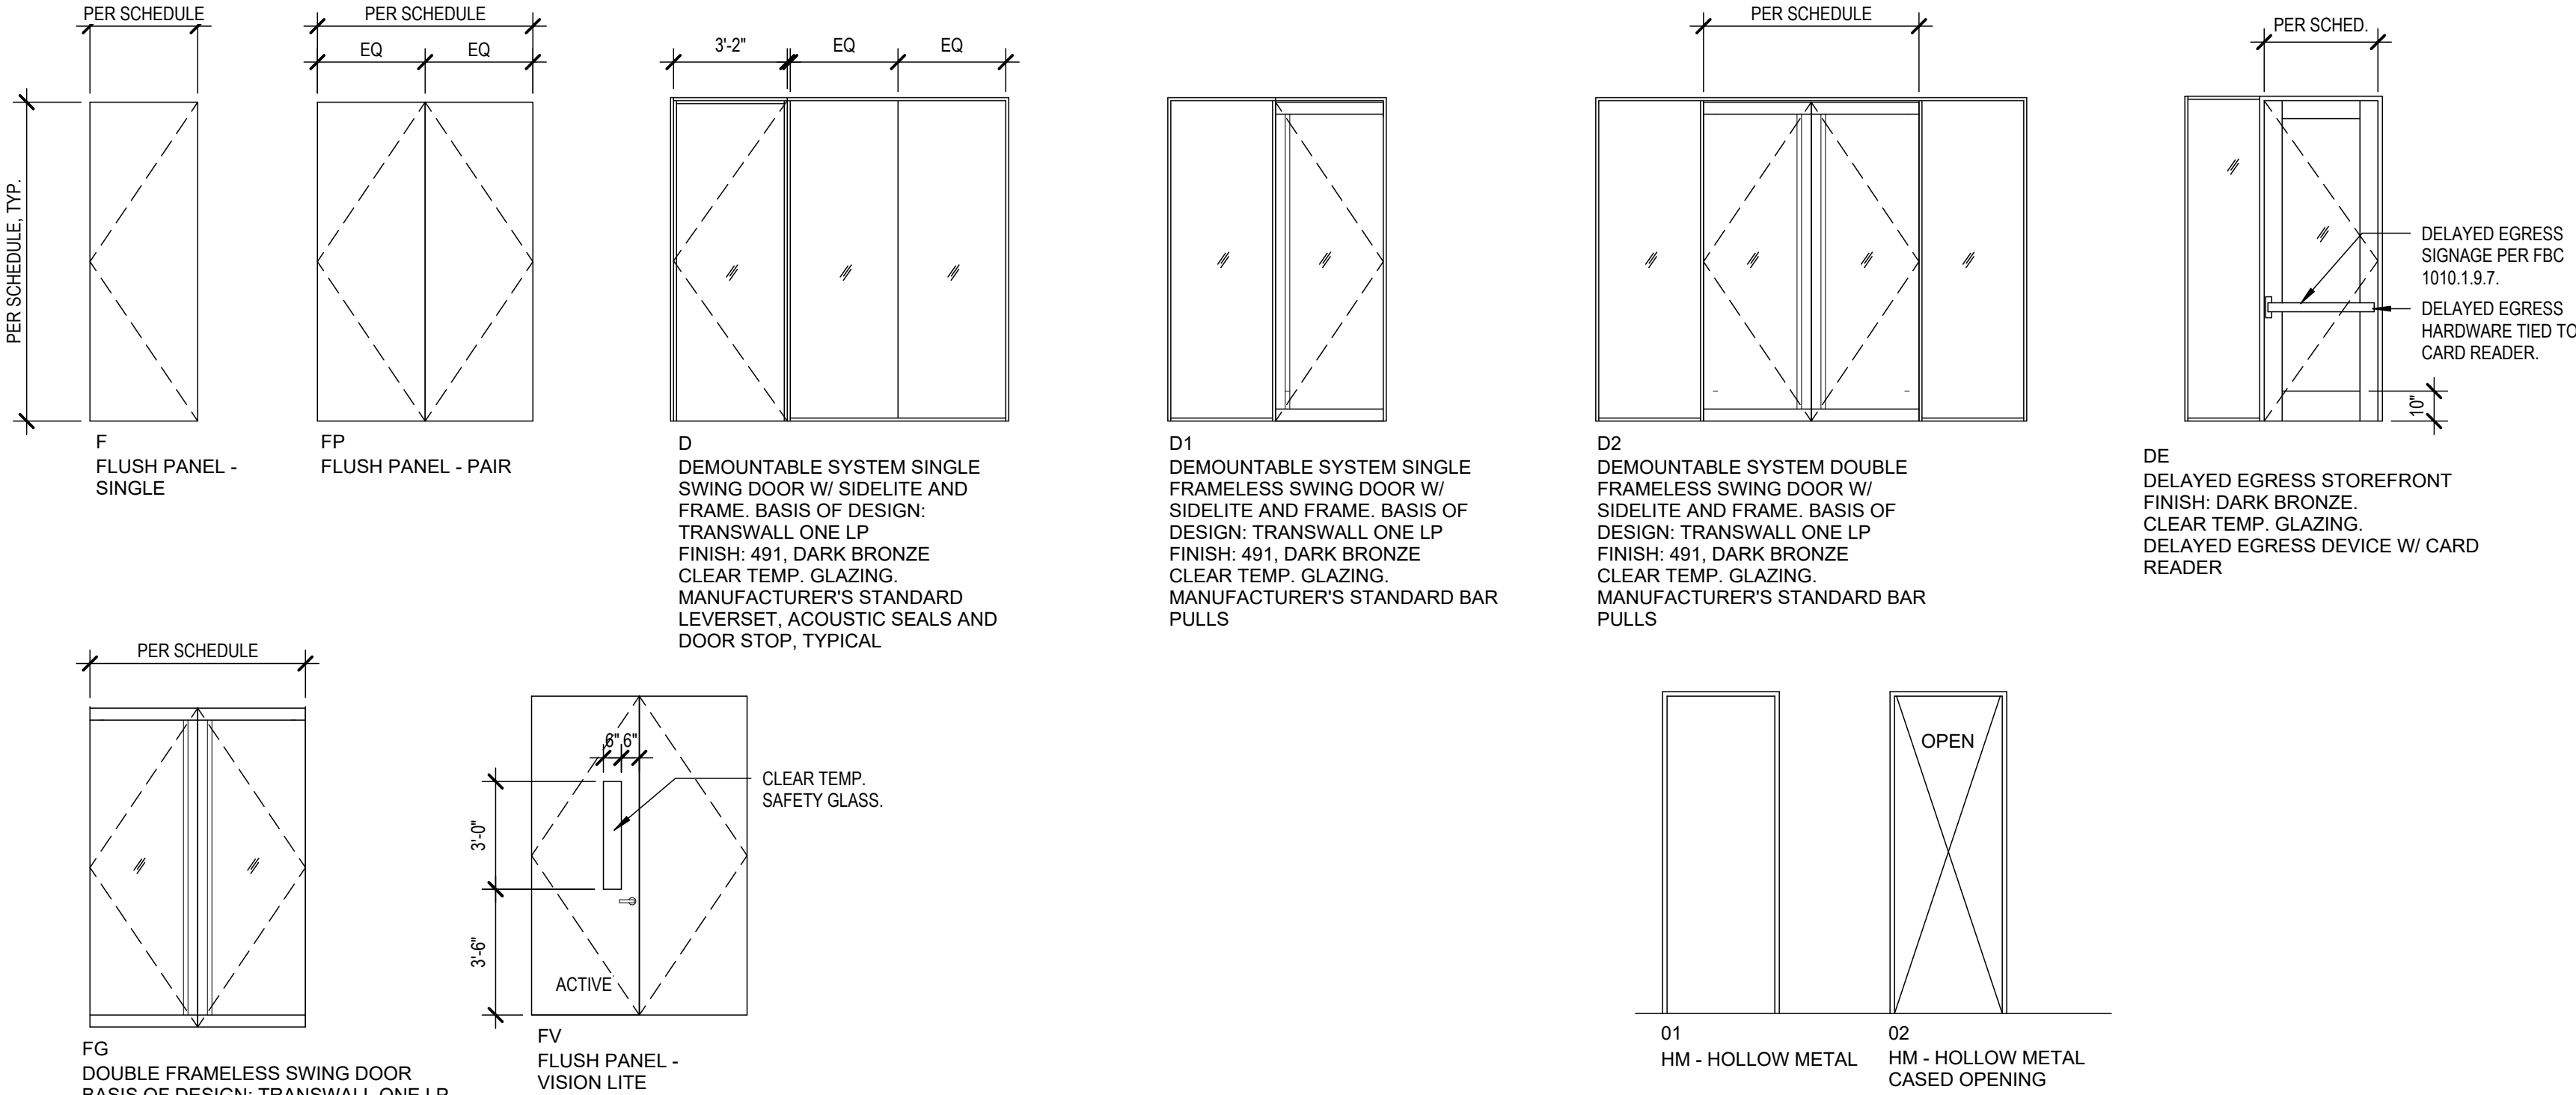

3 DOOR AND FRAME TYPES

1/4" = 1'-0"

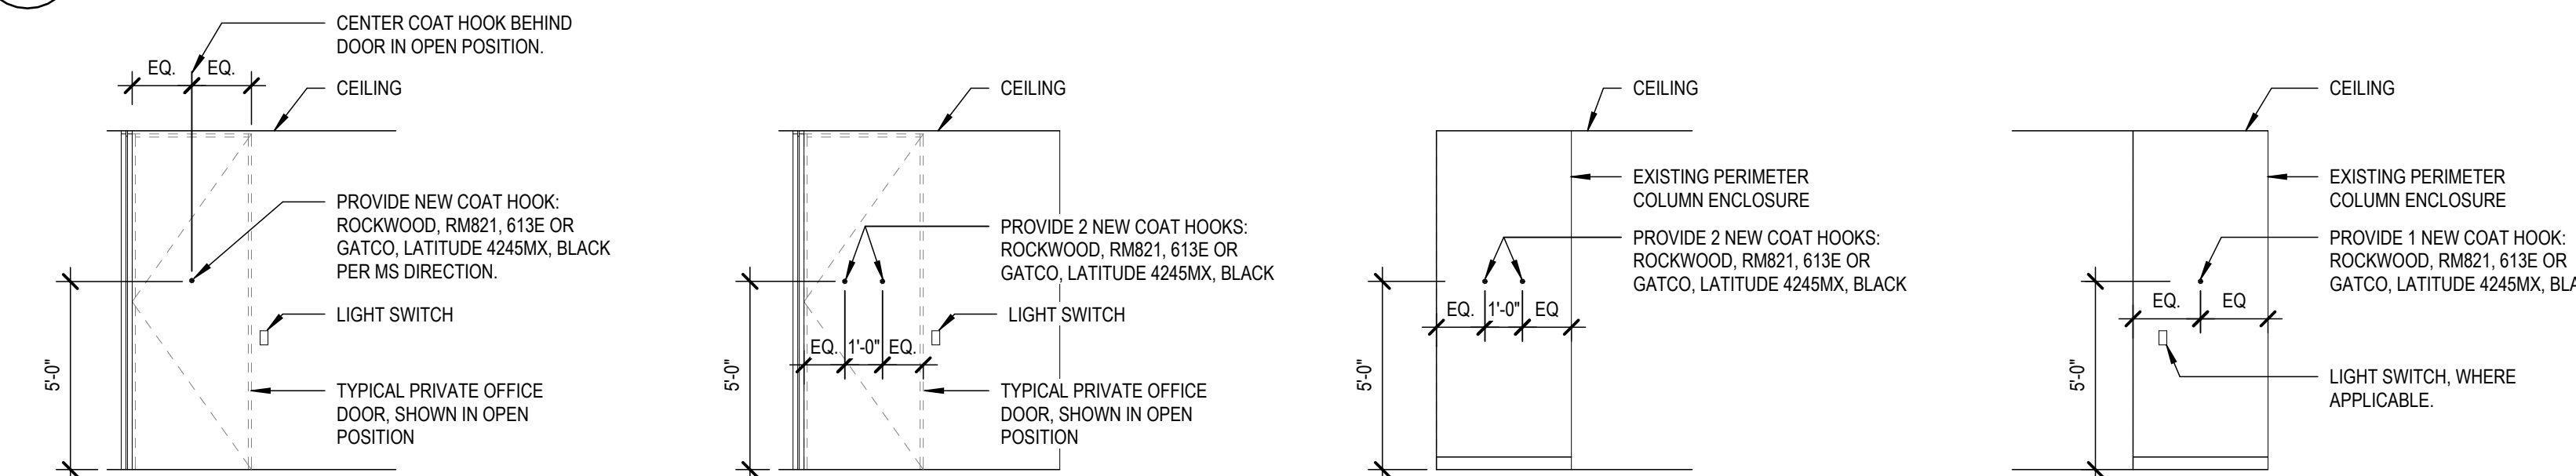

1-PERSON PRIVATE OFFICE (TYP. THROUGHOUT, see plans)

SHARED PRIVATE OFFICE (see plans)

SHARED PRIVATE OFFICE (SIDE OF COLUMN, see plans)

SHARED PRIVATE OFFICE (SIDE OF COLUMN, see plans)

- PROVIDE AND INSTALL COAT HOOKS AS NOTED ON ELEVATIONS ABOVE.
- INSTALL PER MOUNTING LOCATIONS SHOWN ABOVE. IF LOCATION NOTED ABOVE CONFLICTS WITH EXISTING WALL MOUNTED DEVICES, BRING IT TO THE ATTENTION OF THE ARCHITECT FOR RESOLUTION PRIOR TO INSTALLING.
- PRICING FOR BOTH COAT HOOKS SPECIFIED, MORGAN STANLEY TO MAKE FINAL SELECTION PRIOR TO WORK BEING EXECUTED.

2 COAT HOOK LOCATION ELEVATIONS

1/4" = 1'-0"

HARDWARE TYPE EX

EXISTING DOOR AND FRAME TO REMAIN

INDICATES EXISTING HARDWARE SET. IF HARDWARE FINISHES MATCH PROJECT STANDARD, 613E. THEN REPLACE ANY NON-FUNCTIONING OR BROKEN DEVICES AT THIS LOCATION WITH NEW TO MATCH EXISTING. IF EXISTING HARDWARE DOES NOT MATCH PROJECT STANDARD, PROVIDE NEW HARDWARE WITH FUNCTIONS TO MATCH EXISTING HARDWARE FUNCTION AND KEYING AT SAME DOOR (i.e. AN EXISTING LOCKING DOOR IS TO RECEIVE A NEW SIMILARLY LOCKING HARDWARE SET), IN PROJECT STANDARD FINISH, 613E.

HARDWARE TYPE 1 - SINGLE FLUSH DOOR-PASSAGE

HINGES: (4) by Stanley FB1191 613E
OFFICE PASSAGE SET: (1) by SCHLAGE L9010-LATITUDE-B 613E
CONCEALED O.H. CLOSER: (1) by LCN 3133 613E
FLOOR STOP: (1) by ROCKWOOD #446 613E
SILENCERS: (3) by ROCKWOOD #608/609 GREY

HARDWARE TYPE 1D - SINGLE DEMOUNTABLE SWING DOOR-PASSAGE

HINGES: (1) PAIR TRANSWALL ONE LP MANUF. STD 491, DK BRONZE
OFFICE PASSAGE SET: (1) by SCHLAGE 9010 446 613E
FLOOR STOP: (1) by ROCKWOOD #446 613E
COAT HOOKS: AT OFFICES ONLY, PER DETAIL 2 ON THIS SHEET US108E

HARDWARE TYPE 2 - SINGLE FLUSH DOOR-LOCKING

HINGES: (4) by Stanley FB1191 613E
CLASSROOM LOCK SET: (1) by SCHLAGE L9070-LATITUDE-B 613E
O.H. CONCEALED STOP: (1) by RIXSON 1-336 series 613E
SILENCERS: (2) by ROCKWOOD #608/609 GREY

HARDWARE TYPE 2D-CR - SINGLE DEMOUNTABLE SWING DOOR-w/ CARD READER

RAIL FITTINGS: (1) pair by DORMAKABA 4" TOP RAIL 613E
(1) pair OFFSET PIVOTS MANUF. STD 491, DK BRONZE
HINGES: (1) by SCHLAGE 4" TAPERED BOTTOM RAIL 613E
TOP ELECTROMAGNETIC LOCK: (1) by RIXSON M450P-ATS 613E
US108E LOCK: PROVIDE CUSTOM 613E FINISHED ALUMINUM COVER TO CONCEAL
MANUF. STD 491, DK BRONZE
PULL SET: (1) pair by ROCKWOOD RM3311-88 US108E
CLOSER: (1) by DORMA TS93 695
FLOOR STOP: (1) by ROCKWOOD #446 US108E
CARD READER: (1) by SECURITY VENDOR SEE ADDITIONAL NOTES BELOW

NOTE: BALANCE OF ELECTRONIC HARDWARE (INCLUDING CARD READER, MONITORING SWITCH, REQUEST TO EXIT BUTTON, MOTION SENSOR, ETC.) TO BE SPECIFIED BY SECURITY VENDOR. CONTRACTOR SHALL PROVIDE FULLY FUNCTIONING ASSEMBLY AT PROJECT COMPLETION.

HARDWARE TYPE 2D - SINGLE DEMOUNTABLE DOOR-LOCKING (OFFICE)

HINGES: (1) PAIR TRANSWALL ONE LP MANUF. STD 491, DK BRONZE
OFFICE LOCKSET: (1) by SCHLAGE 9000 series 446 613E
FLOOR STOP: (1) by ROCKWOOD #446 US108E

HARDWARE TYPE 3 - SINGLE DOOR - COATS

HINGES: (4) by Stanley FB1191 613E
DUMMY TRIM: (1) by SCHLAGE L0170-LATITUDE-B 613E
O.H. CONCEALED STOP: (1) by RIXSON 1-336 series 613E
ROLLER CATCH: (1) by VES RHL30 613E
SILENCERS: (4) by ROCKWOOD #608/609 GREY

HARDWARE TYPE 3A - DOOR PAIR - CLOSETS & COATS

OFFSET PIVOTS: (2) by RIXSON XXX 626
INTERMEDIATE HINGE: (1) by RIXSON XXX 626
DUMMY TRIM: (2) by SCHLAGE L0170-LATITUDE-B 608
O.H. CONCEALED STOP: (2) by RIXSON 1-330 series 626
ROLLER CATCH: (2) by VES RHL30 626
SILENCERS: (2) by ROCKWOOD #608/609 GREY

HARDWARE TYPE 4 - NOT USED

HARDWARE TYPE 4 - SINGLE FLUSH LOCKING w/ CARD READER (FAIL SECURE) COMM. ROOM, OPS, SECONDARY ENTRY

HINGES: (3) by Stanley FB1191 613E
ELECTRIFIED HINGE: (1) by Stanley 613E
ELECTRIC LOCK SET: (1) by SCHLAGE L9009EL-LATITUDE-B 613E
OVERHEAD CLOSER: (1) by LCN #4010 series, parallel arm 613E
CARD READER SYSTEM: (1) by SECURITY VENDOR
SILENCERS: (4) by ROCKWOOD #608/609 GREY

NOTE: NO EXPOSED FASTENERS AT EITHER FACE OF DOOR WILL BE ACCEPTED.

NOTE: BALANCE OF ELECTRONIC HARDWARE (INCLUDING CARD READER, MONITORING SWITCH, REQUEST TO EXIT BUTTON, MOTION SENSOR, ETC.) TO BE PROVIDED AND INSTALLED BY SECURITY VENDOR. CONTRACTOR IS RESPONSIBLE TO COORDINATE WITH SECURITY VENDOR AND SHALL PROVIDE A FULLY FUNCTIONING ASSEMBLY AT PROJECT COMPLETION. REFER TO ENGINEERING DRAWINGS FOR ADDITIONAL INFORMATION.

HARDWARE TYPE 5A - PAIR, FLUSH LOCKING w/ CARD READER (FAIL SAFE) FREIGHT ELEVATOR LOBBY

HINGES: (7) by Stanley FB1191 613E
ELECTRIFIED HINGE: (1) by Stanley 613E
ELECTRIC LOCK SET: (1) by SCHLAGE L9009EL-LATITUDE-B 613E
FLUSH BOLTS: (1) PAIR by ROCKWOOD #4010 series, parallel arm US108E
SURFACE CLOSER: (2) by LCN #4010 series, parallel arm 613E
CARD READER SYSTEM: (1) by SECURITY VENDOR
SILENCERS: (6) by ROCKWOOD #608/609 GREY

NOTE: NO EXPOSED FASTENERS AT EITHER FACE OF DOOR WILL BE ACCEPTED.

NOTE: BALANCE OF ELECTRONIC HARDWARE (INCLUDING CARD READER, MONITORING SWITCH, REQUEST TO EXIT BUTTON, MOTION SENSOR, ETC.) TO BE SPECIFIED BY SECURITY VENDOR. CONTRACTOR IS RESPONSIBLE TO COORDINATE WITH SECURITY VENDOR AND SHALL PROVIDE A FULLY FUNCTIONING ASSEMBLY AT PROJECT COMPLETION. REFER TO ENGINEERING DRAWINGS FOR ADDITIONAL INFORMATION.

HARDWARE TYPE 6 - SINGLE FLUSH DOOR-PRIVACY LOCKING

MOTHERS ROOM

HINGES: (4) by Stanley FB1191 613E
PRIVACY LOCK SET: (1) by SCHLAGE L9496-LATITUDE-B 613E
WITH "OCCUPIED" INDICATOR: (1) by Stanley 613E
FLOOR STOP: (1) by ROCKWOOD #446 613E
SILENCERS: (3) by ROCKWOOD #608/609 GREY
COAT HOOK: (2) (PROJECT STD. SEE DETAIL 1 THIS SHEET) CENTER ON BACK OF DOOR, ONE AT 48", ONE AT 60". 613E
SURFACE CLOSER: (1) by LCN (on private side of door) #4010 series, parallel arm 613E

HARDWARE TYPE 6A - SINGLE FLUSH DOOR-PRIVACY LOCKING

MOTHERS ROOM, UNISEX TOILET ROOMS (CLIENT FACING)

HINGES: (4) by Stanley FB1191 613E
PRIVACY LOCK SET: (1) by SCHLAGE L9496-LATITUDE-B 613E
WITH "OCCUPIED" INDICATOR: (1) by Stanley 613E
FLOOR STOP: (1) by ROCKWOOD #446 613E
DOOR BOTTOM: (1) MORTISED AUT DROP BOTTOM LEGACY TYPE 7463
NEOPRENE SEALS: HEAD AND JAMBS, LEGACY TYPE 5077 (DB, DARK BRONZE AT WOOD
VENEER DOORS & FRAMES (CLIENT HUBS) GREY
COAT HOOK: (3) by ROCKWOOD #608/609
SURFACE CLOSER: (2) (PROJECT STD. SEE DETAIL 1 THIS SHEET) 613E
(1) by LCN (on private side of door) #4010 series, parallel arm 613E

HARDWARE TYPE 7D-CR - DOUBLE DEMOUNTABLE SWING DOORS-w/ CARD READER

RAIL FITTINGS: (2) pair by DORMAKABA 4" TOP RAIL 613E
CONCEALED CLOSERS: (2) by DORMA RT586 TOP ARM, AND 491, DK BRZ
FLOOR PIVOT, WHITE COVER PLATE M452P-ATS **MATCH
TOP ELECTROMAGNETIC LOCK: (2) by SCHLAGE PROVIDE CUSTOM 613E FINISHED ALUMINUM COVER TO CONCEAL
US108E MAGLOCK: MAGLOCK
PULL SET: (2) pair by ROCKWOOD RM3311-88 US108E
FLOOR STOP: (2) by ROCKWOOD #446 613E
CARD READER: (1) by SECURITY VENDOR SEE ADDITIONAL NOTES BELOW

NOTE: BALANCE OF ELECTRONIC HARDWARE (INCLUDING CARD READER, MONITORING SWITCH, REQUEST TO EXIT BUTTON, MOTION SENSOR, ETC.) TO BE SPECIFIED AND INSTALLED BY SECURITY VENDOR. CONTRACTOR IS RESPONSIBLE TO COORDINATE WITH SECURITY VENDOR AND PROVIDE A FULLY FUNCTIONING ASSEMBLY AT PROJECT COMPLETION. REFER TO ENGINEERING DRAWINGS FOR ADDITIONAL INFORMATION.

NOTE: PROVIDE REMOTE DOOR RELEASE BUTTON AT RECEPTION DESK.

DOOR OPERATION:
a. DOOR PAIR SHALL BE NORMALLY CLOSED AND LOCKED.
b. VALID KEY OR CREDENTIAL SHALL BE REQUIRED TO ENTER.
c. UPON PRESENTATION OF VALID KEY OR CREDENTIAL TO CARD READER, LOCK SHALL ELECTRONICALLY UNLOCK AND PERMIT MANUAL ENTRY.

d. HARDWARE INSTALLER SHALL COORDINATE WITH ELECTRICAL AND SECURITY SYSTEMS IN ORDER TO PROVIDE A FULLY FUNCTIONING ASSEMBLY AT PROJECT COMPLETION.

HARDWARE TYPE 8 - SINGLE FLUSH DOOR-PUSH/PULL

HINGES: (3) by Stanley FB1191 613E
PUSH PLATE/ PULL SET: (1) by ROCKWOOD XXX 613E
KICK PLATE: (1) by ROCKWOOD XXX 613E
CONCEALED O.H. CLOSER: (1) by LCN 3133 613E
FLOOR STOP: (1) by ROCKWOOD #446 613E
SILENCERS: (3) by ROCKWOOD #608/609 GREY

HARDWARE TYPE 8 - SINGLE FLUSH DOOR-PUSH/PULL FRAMELESS (MFR)

TOP/BOTTOM PIVOTS: (4) by RIXSON XXX 626
INTERMEDIATE PIVOT: (1) by RIXSON XXX 626
BAR PULL SET: (1) by ROCKWOOD RM3311-88 626
CONCEALED O.H. CLOSER: (1) by RIXSON 3133 613E
FLOOR STOP: (1) by ROCKWOOD #446 613E

HARDWARE TYPE 10D-CR - SINGLE LOCKING CONTROLLED ACCESS - DELAYED EGRESS w/ CARD READER

HINGES: (4) by Stanley FB1191 613E
EXIT DEVICE: (1) by VonDuprin, CHEXIT CX38 643E
DELAYED EGRESS: (1) by VonDuprin PS902 (GC TO VERIFY) -
POWER SUPPLY: (1) by VonDuprin (GC TO CONFIRM WIRE SIZE WITH SECURITY VENDOR)
ELEC. POWER TRANSFER: (1) by VonDuprin (GC TO CONFIRM WIRE SIZE WITH SECURITY VENDOR)
SURFACE CLOSER: (1) by LCN 4040XP 685 DK BRZ
FLOOR STOP: (1) by ROCKWOOD #446 613E
CARD READER: (1) by SECURITY VENDOR SEE ADDITIONAL NOTES BELOW

NOTE: BALANCE OF ELECTRONIC HARDWARE (INCLUDING CARD READER, MONITORING SWITCH, ETC.) TO BE PROVIDED AND INSTALLED BY SECURITY VENDOR. CONTRACTOR IS RESPONSIBLE TO COORDINATE WITH SECURITY VENDOR AND SHALL PROVIDE A FULLY FUNCTIONING ASSEMBLY AT PROJECT COMPLETION. REFER TO ENGINEERING DRAWINGS FOR ADDITIONAL INFORMATION.

NOTE: DELAYED EGRESS HARDWARE (AND SIGN) SHALL BE INSTALLED IN ACCORDANCE WITH NFPA LIFE SAFETY CODE SECTION 7.2.1.6.1.

Morgan Stanley

5 CONCOURSE PARKWAY
ATLANTA, GA 30328
CIIPS: 2025-00254

Project
Interior Office Renovation
5 Concourse Parkway
Atlanta, GA 30328

Prepared For
Morgan Stanley
5 Concourse Parkway - Atlanta, GA



Hellmuth, Obata & Kassabaum, Inc.

All reproduction & intellectual property rights reserved © 2026

In Association with

One Penn Plaza
250 W 54th Street, 4th Floor
New York, NY 10119

52 Temple Place
Boston, MA 02111

1001 Avenue of the Americas, 4th Floor
New York, NY 10018

122 South Broad Street, Suite 2320
Philadelphia, PA 19109

Key Plan

NOTE: FULL PROJECT SCOPE IS SHOWN AT PLANS, ELEVATIONS AND DETAILS. WORK IS TO BE COMPLETED IN MULTIPLE PHASES. SEE SCHEMATIC PHASING DIAGRAM AT SHEET G601. COORDINATE FINAL DEMARCATION BETWEEN PHASES WITH TENANT REPRESENTATIVE AND ON-SITE CONDITIONS.

Professional Seals

No.	Description	Date
1	75% CD REVIEW	2026-06-23
2	PERMIT SET / ISSUE FOR BID	2026-07-07

Project No: 26.75003.00
Sheet Title

DOOR, FRAME AND HARDWARE LEGENDS

Original is 42 x 36. Do not scale contents of this drawing.
Sheet Number

A620

1 KEYING SCHEDULE

1/4" = 1'-0"

