




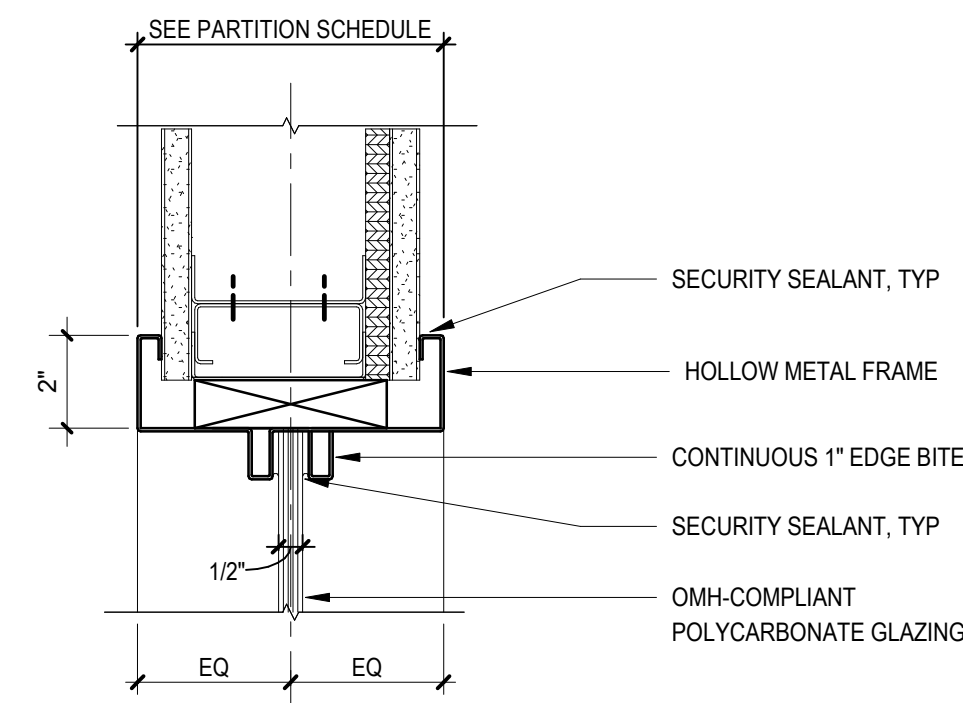


D1 HM WINDOW HEAD - BH
3" = 1'-0"

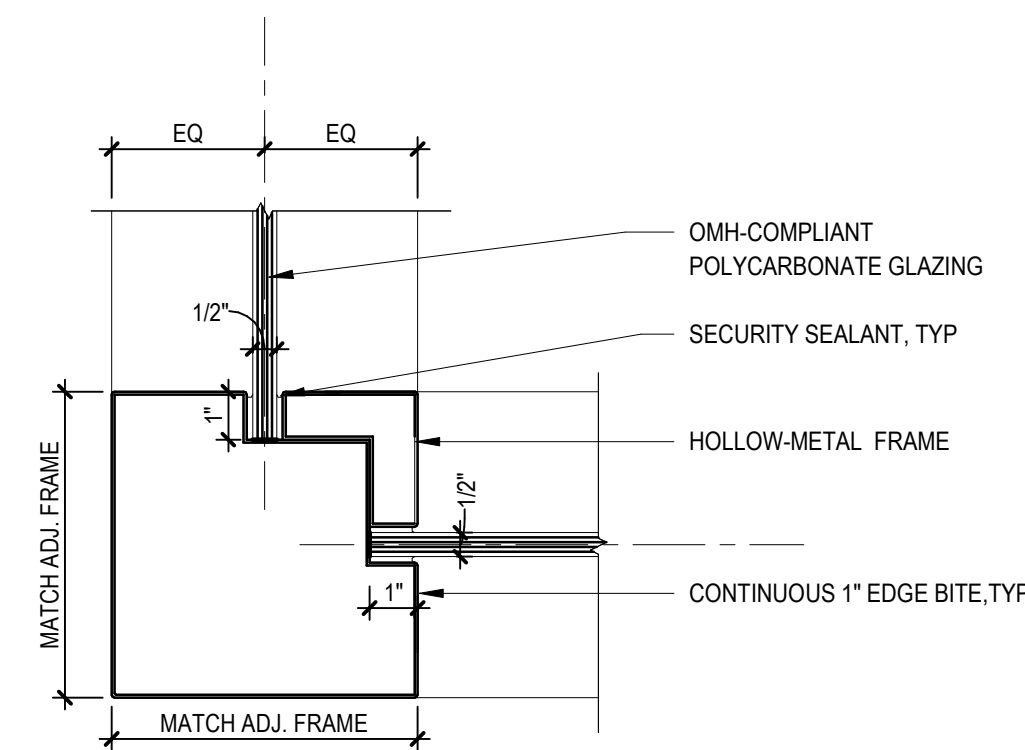


D2 HM WINDOW CORNER - BH
3" = 1'-0"

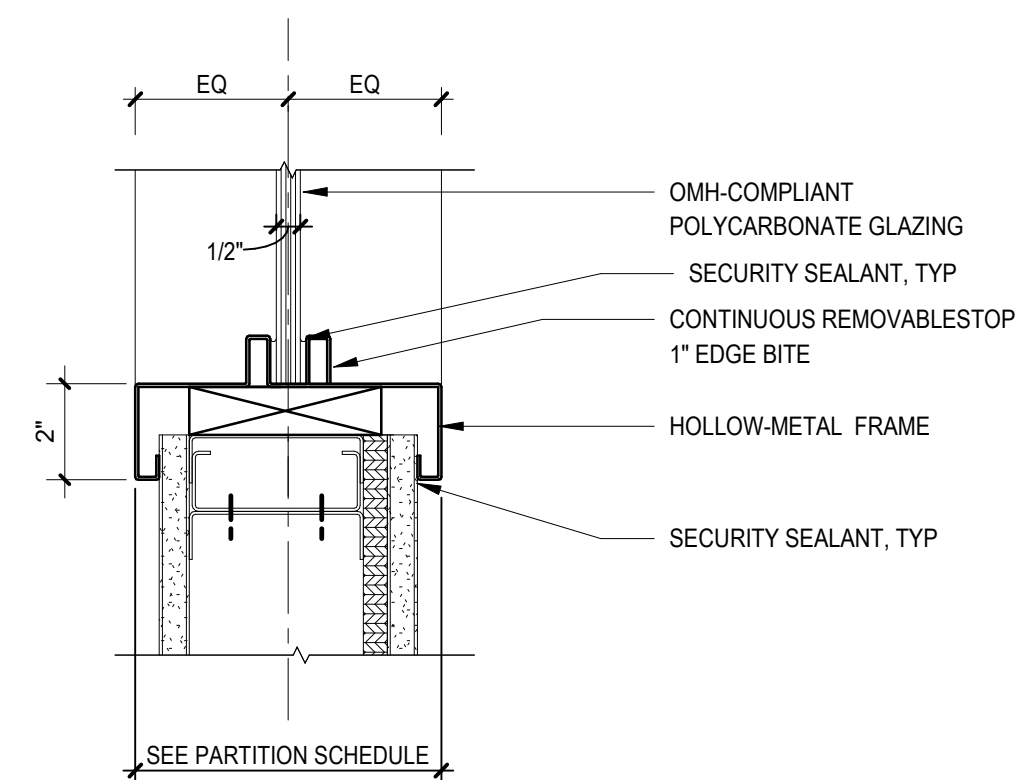


C1 HM WINDOW SILL- BH
3" = 1'-0"

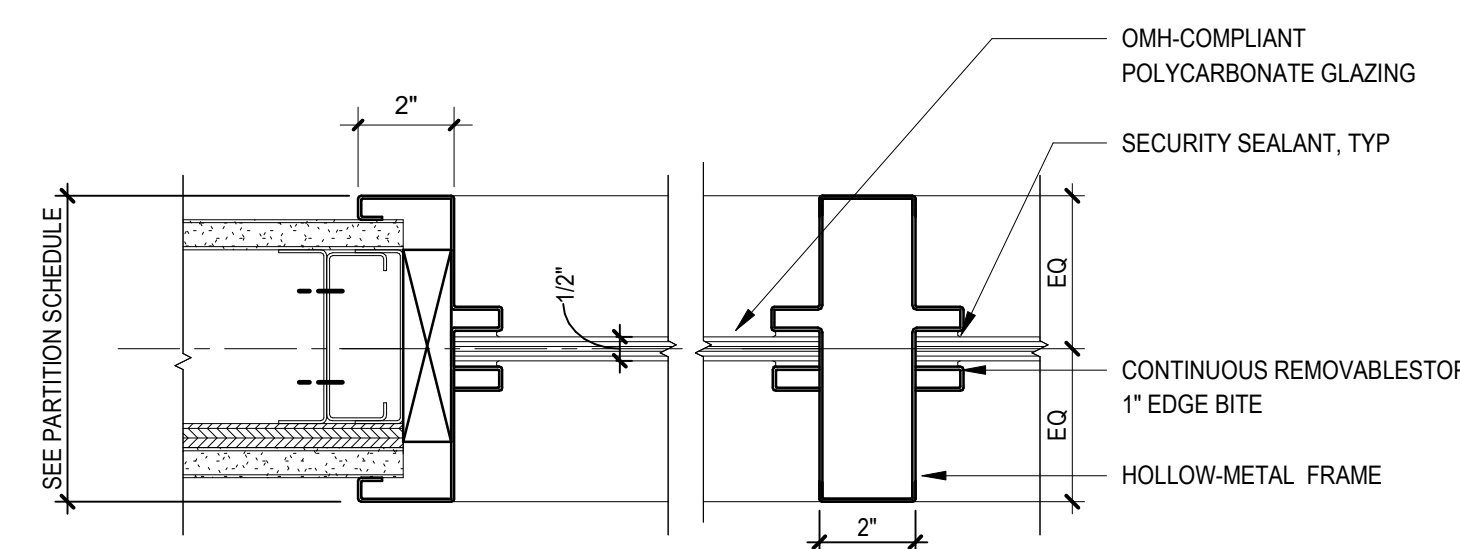


C2 HM WINDOW JAMB- BH

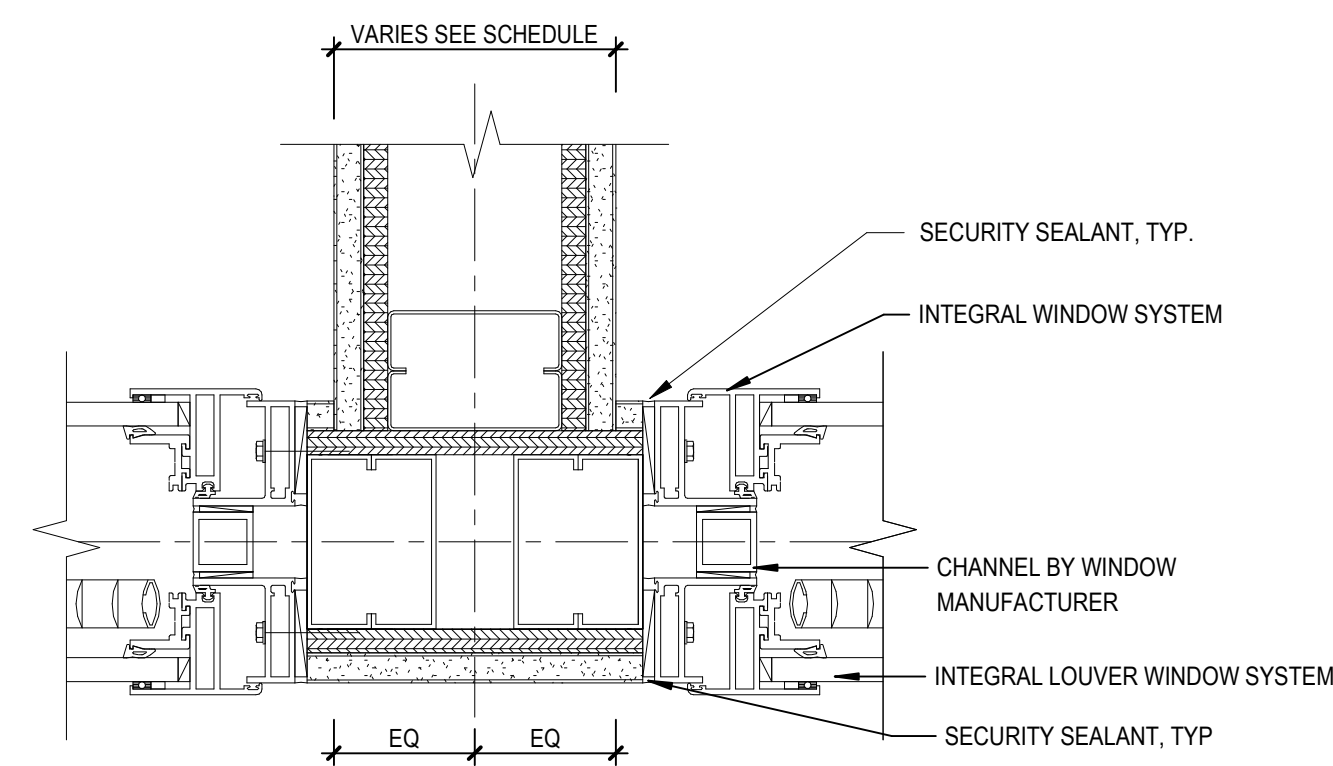


B1 WINDOW W/ INTEGRAL LOUVER @CORNER
3" = 1'-0"

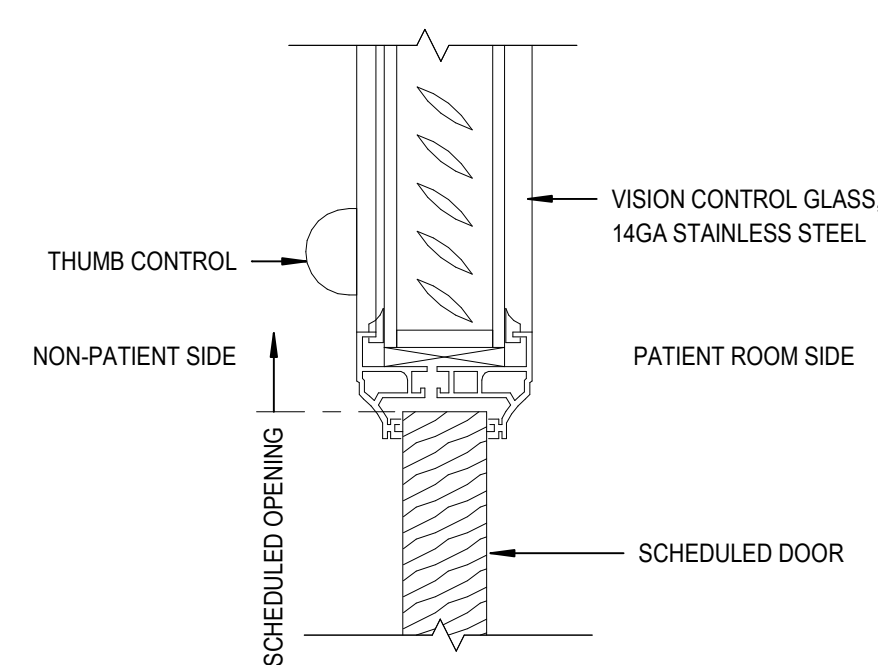

B2 INTEGRAL LOUVER @DOOR
3" = 1'-0"

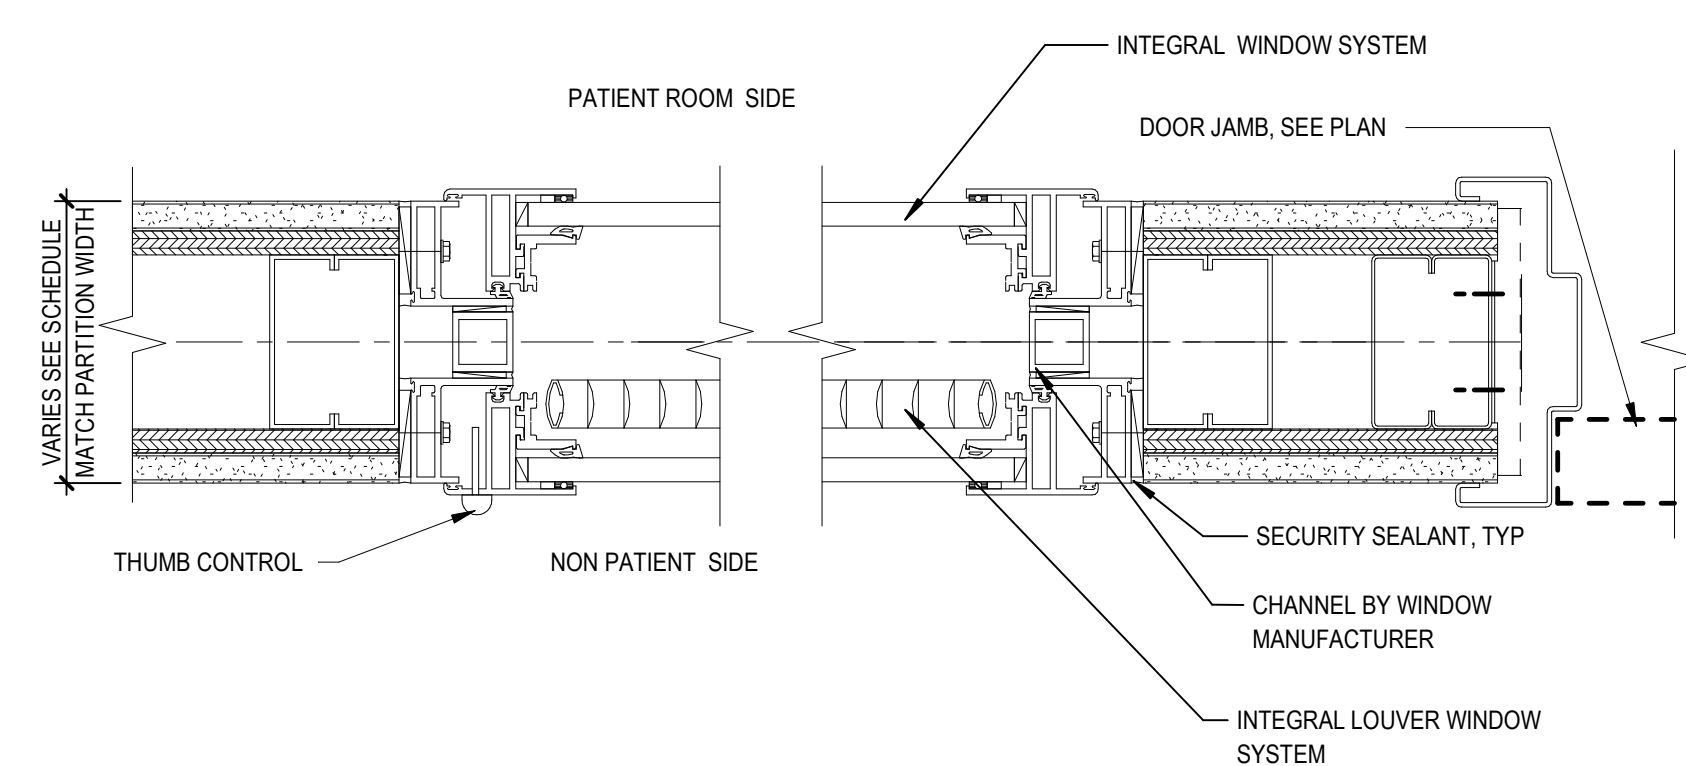

(A1) WINDOW W/ INTEGRAL LOUVER JAMB
3" = 1'-0"

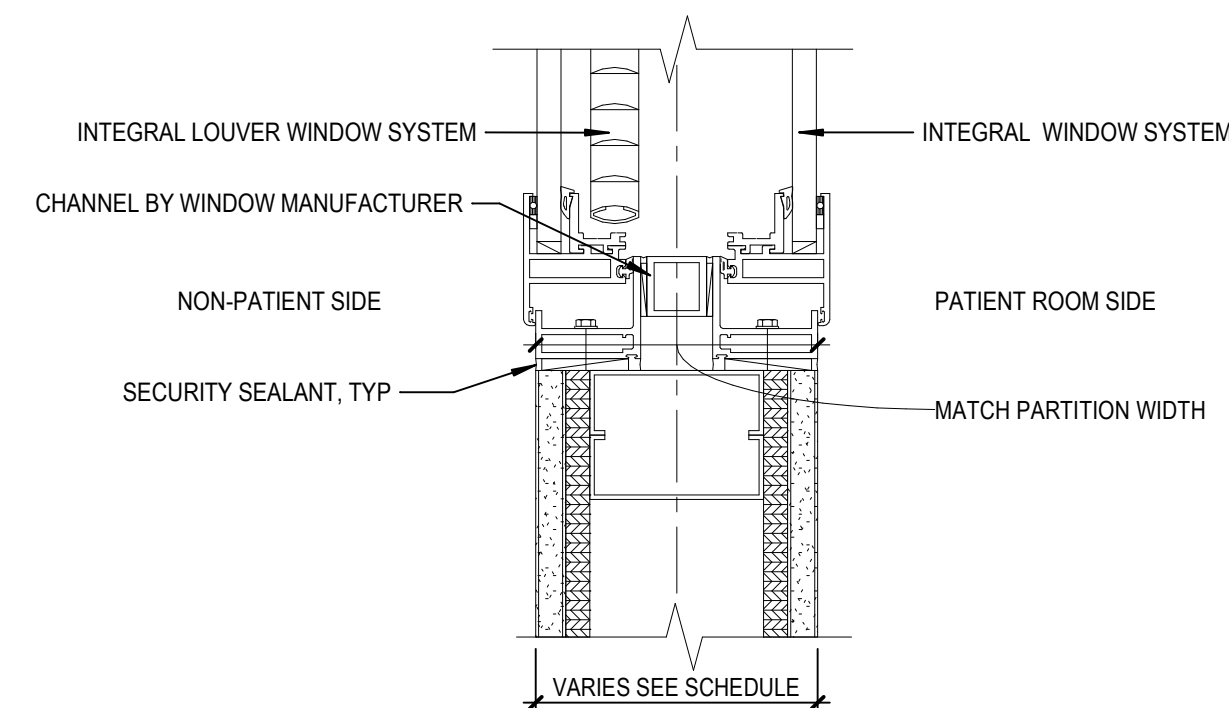

A2 WINDOW W/ INTEGRAL LOUVER HEAD-SILL SIM
3" = 1'-0"

WINDOW AND FRAME SCHEDULE							
MARK	WINDOW				COMMENTS	Manufacturer	
	ROUGH OPENING SIZE		MATERIAL TYPE	FINISH			GLAZING
	W	H					
W1	4'-0"	4'-0"	AL		1/2" POLYCARBONATE INTERIOR & IGU EXTERIOR	EXTERIOR BEHAVIORAL HEALTH WITH INTEGRAL BLINDS AND PRIVACY FILM ON EXTERIOR SIDE, VIF EXISTING OPENING SIZE	WAUSAU
W2	1'-6"	3'-10"	AL		1/2" POLYCARBONATE & 1/2" POLYCARBONATE	BACK-TO-BACK BEHAVIORAL HEALTH INTERIOR ACCESSORY WINDOWS WITH INTEGRAL BLINDS. COLOR MATCHED	WAUSAU
W4	3'-10"	4'-2"	AL		IGU	SINGLE HUNG, VIF EXISTING OPENING SIZE	KAWNEER
W4.A	3'-10"	4'-2"	HM		IGU	FIXED WITH LOUVER, VIF EXISTING OPENING SIZE	KAWNEER