




WINDOW SCHEDULE						
WINDOW No.	QTY.	MANUF.	WIDTH	HEIGHT	SILL HT.	COMMENTS
W1	3	ARMORTEK	<varies>	<varies>	<varies>	BULLET RESISTANT ALUMINUM TRANSACTION WINDOW FRAMES W/ SPEAK THRU
W2	2		5'-0"	4'-0"	3'-0"	

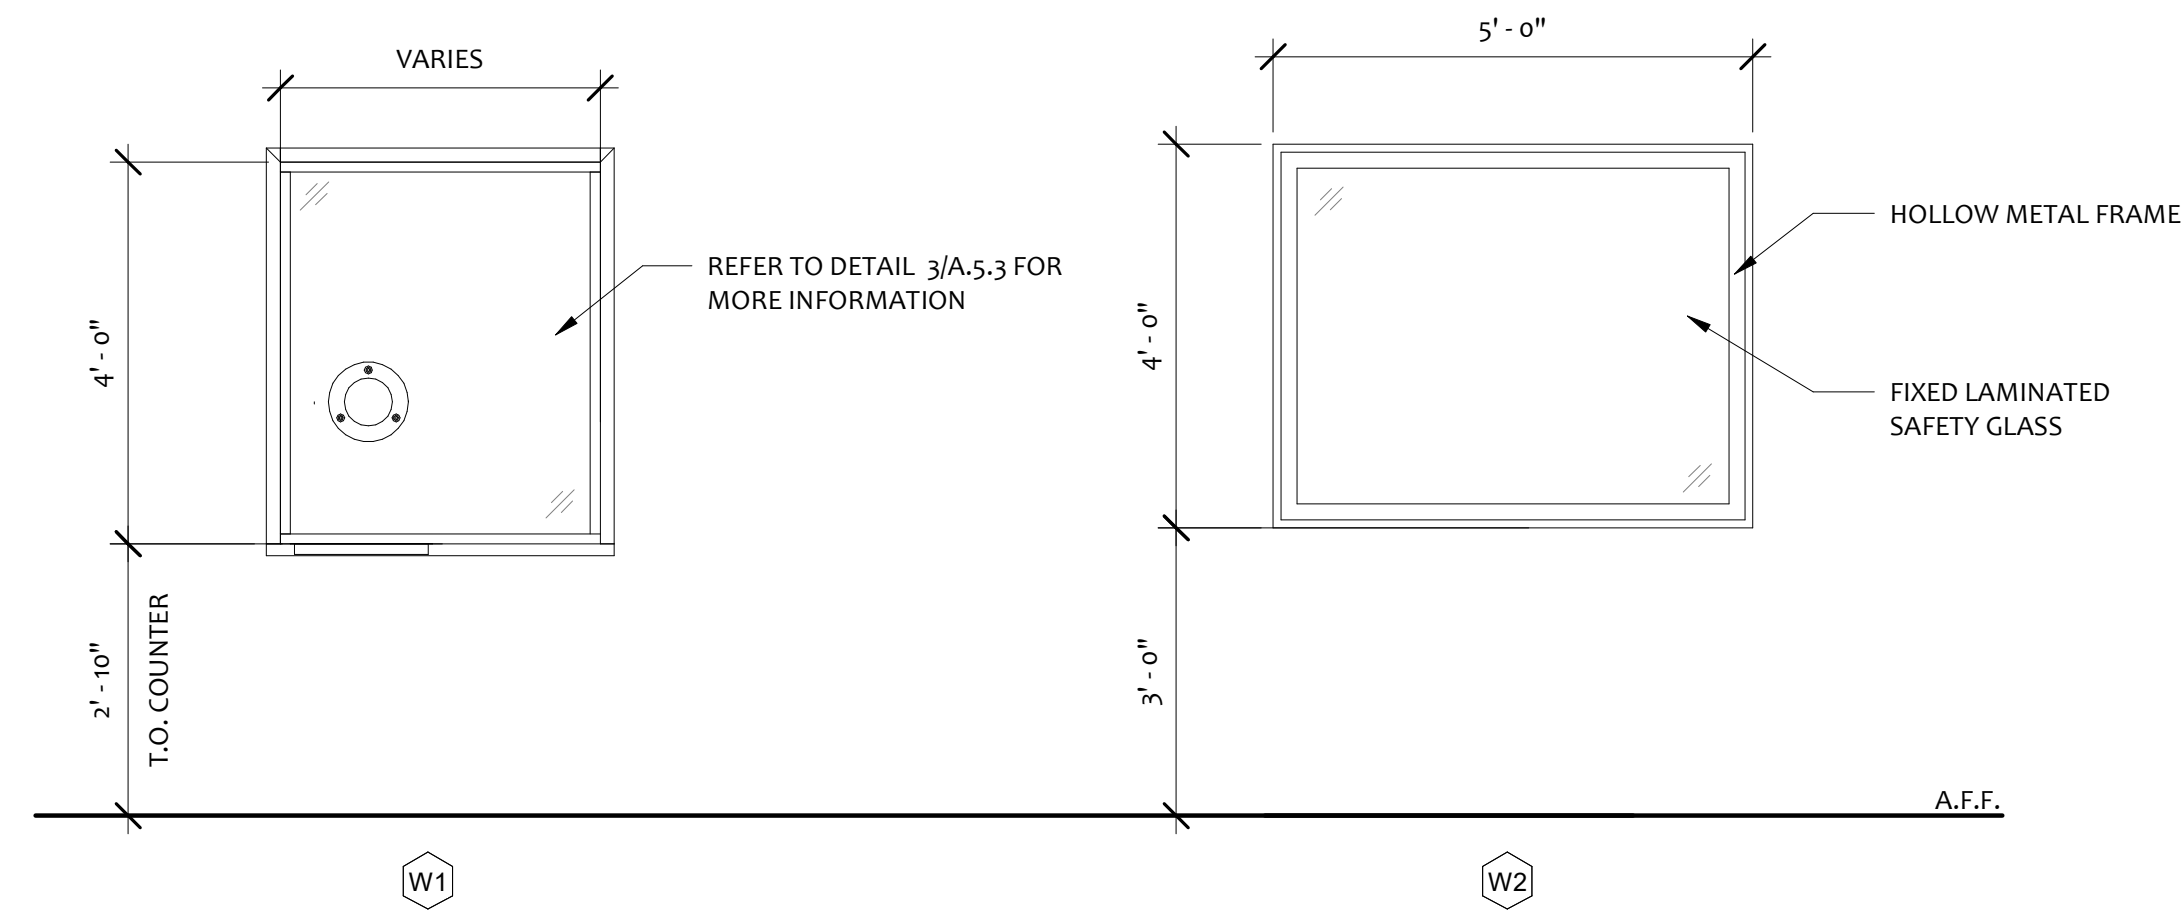


1 WINDOW ELEVATIONS
1/2" = 1'-0"

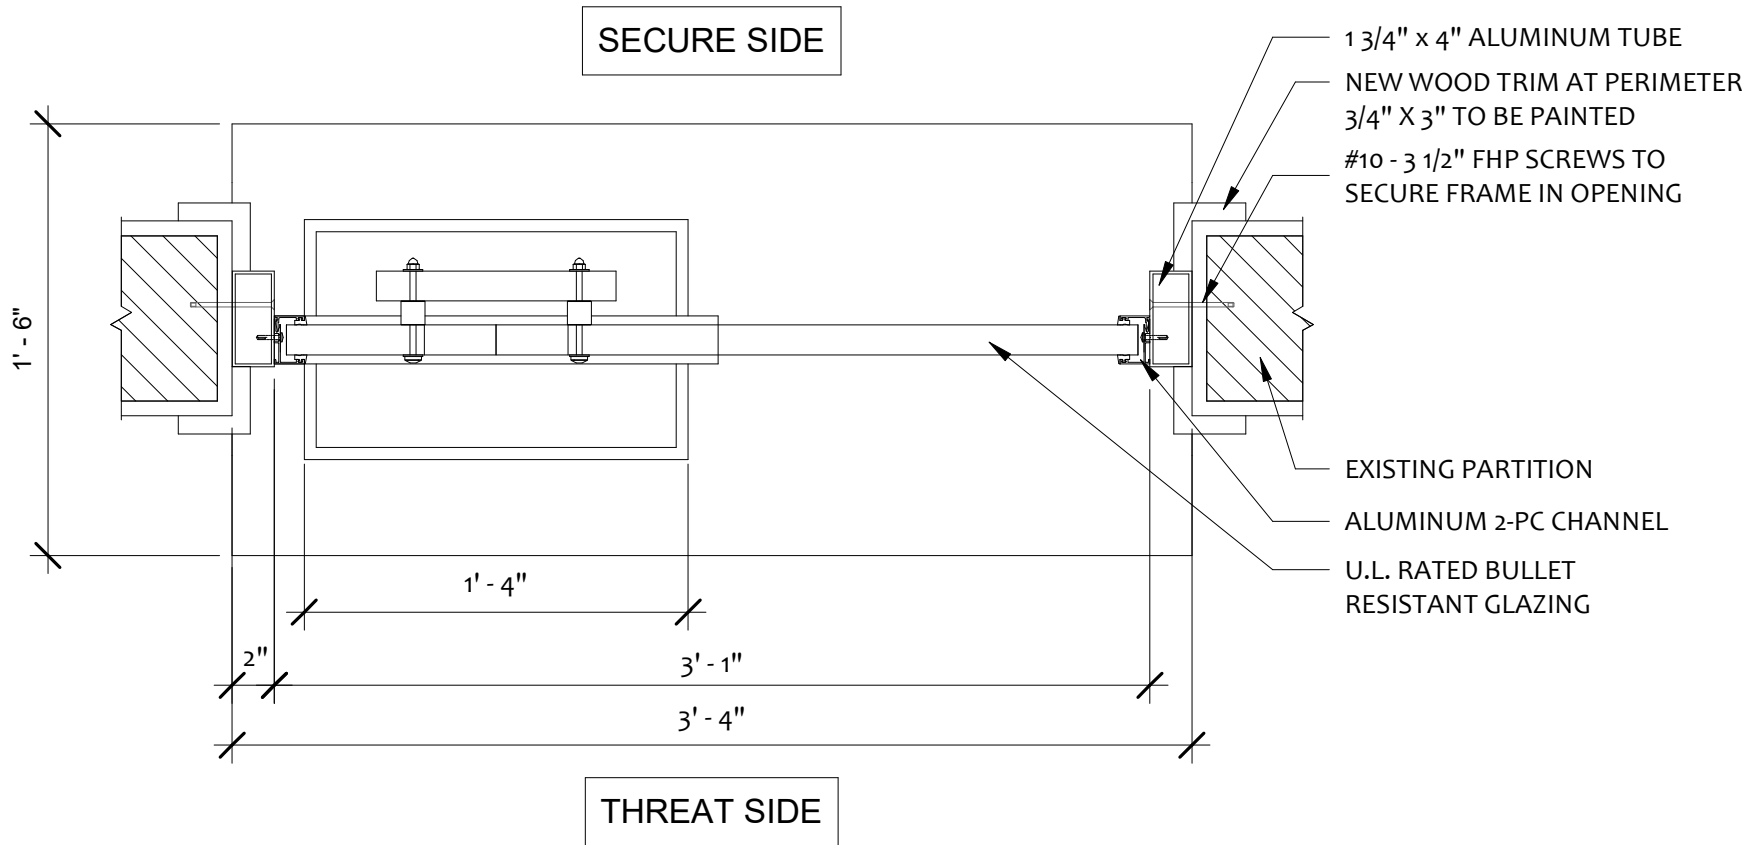

2 SECURE TRANSACTION WINDOW PLAN DETAIL
1 1/2" = 1'-0"

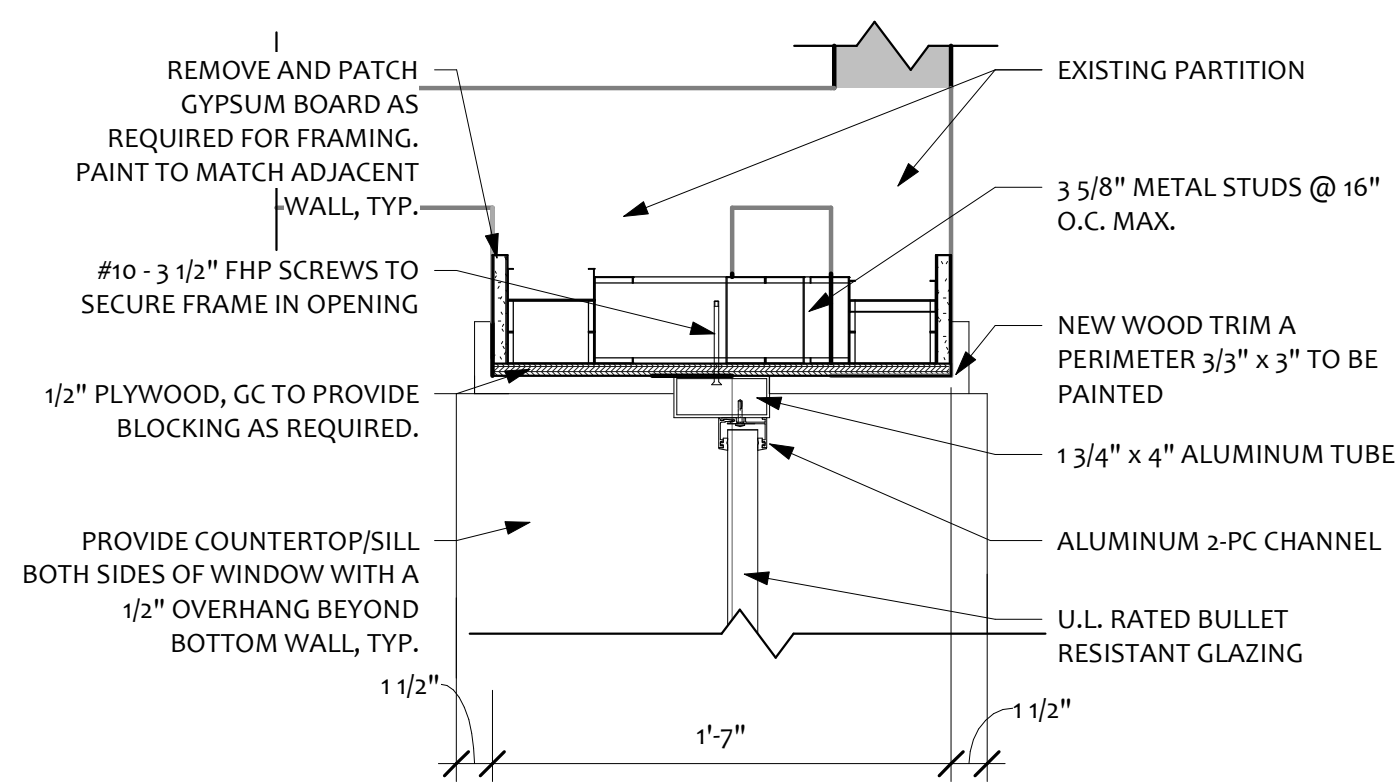


3 CONSTRUCTION PLAN - THIRD FLOOR - Callout 2
1 1/2" = 1'-0"


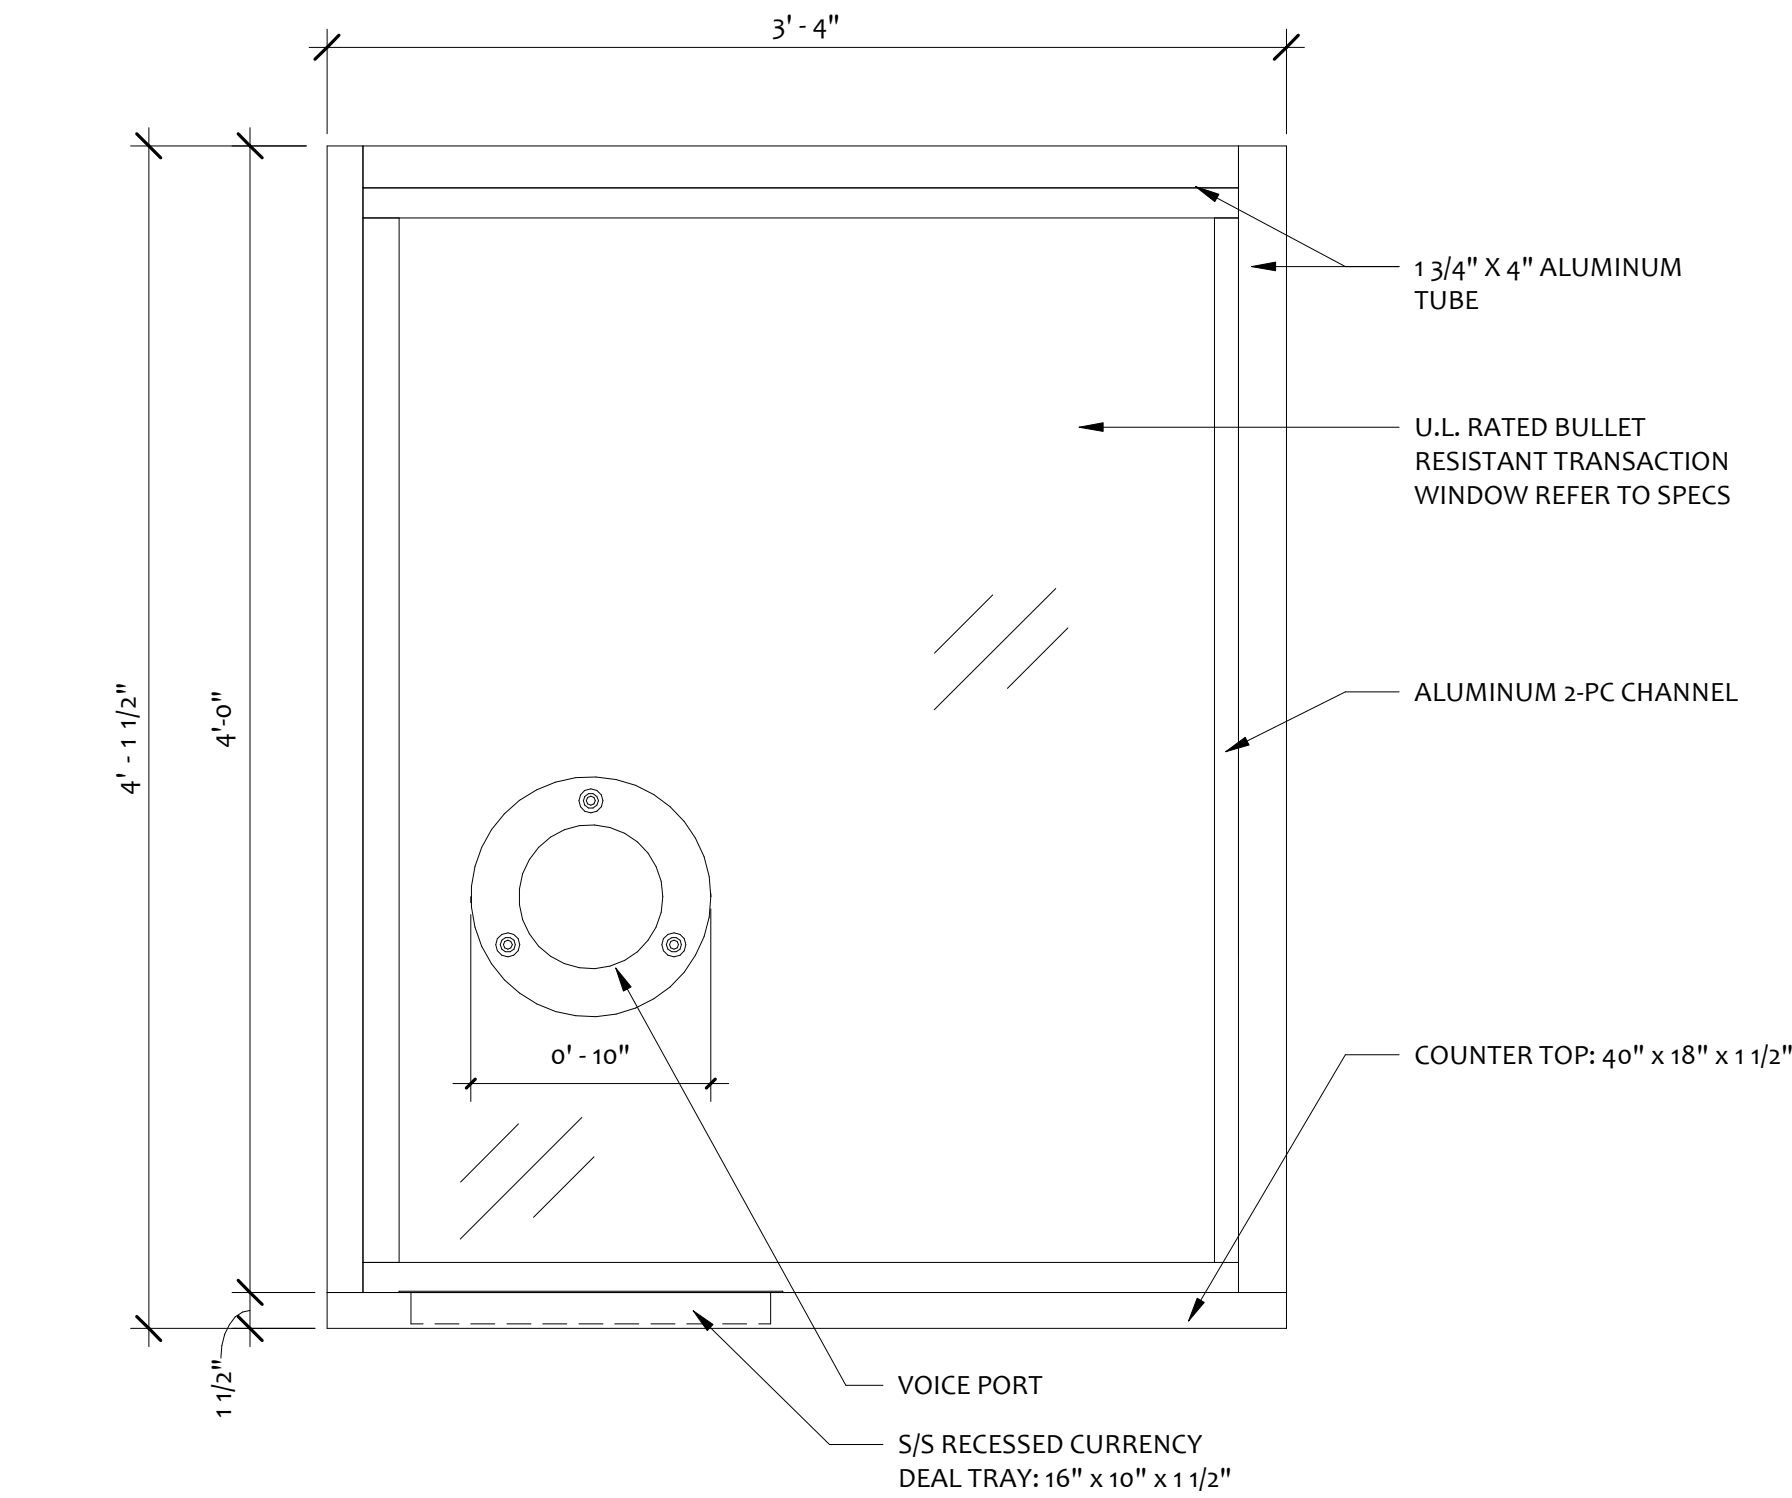


4 SECURE TRANSACTION WINDOW ELEVATION
1 1/2" = 1'-0"

THREAT SIDE

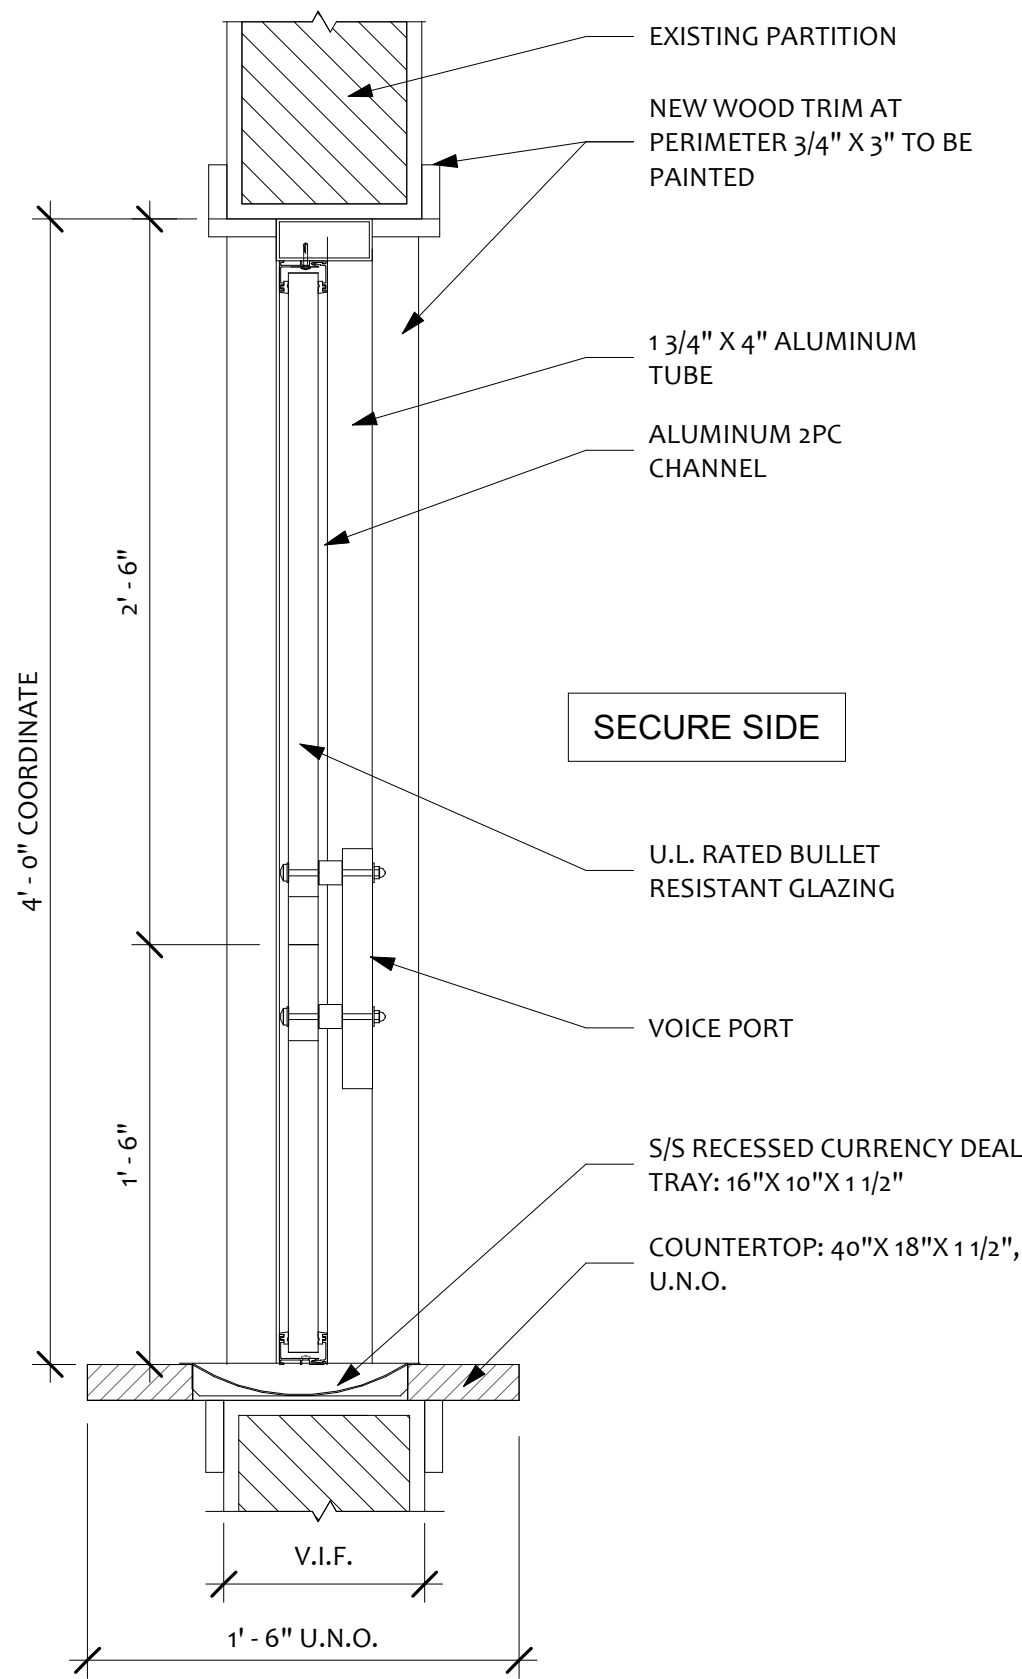

5 SECURE TRANSACTION WINDOW SECTION
1 1/2" = 1'-0"

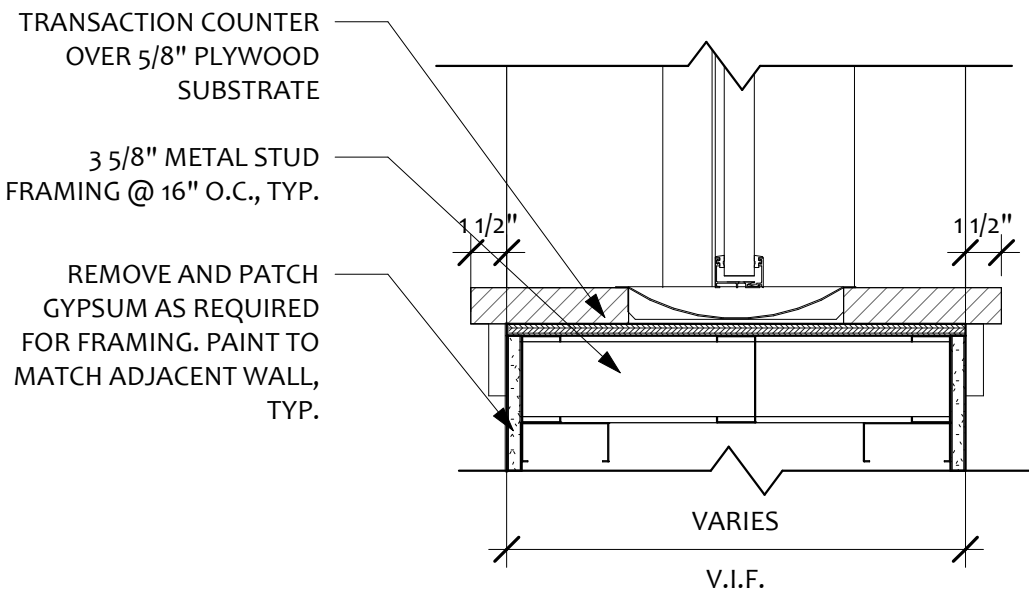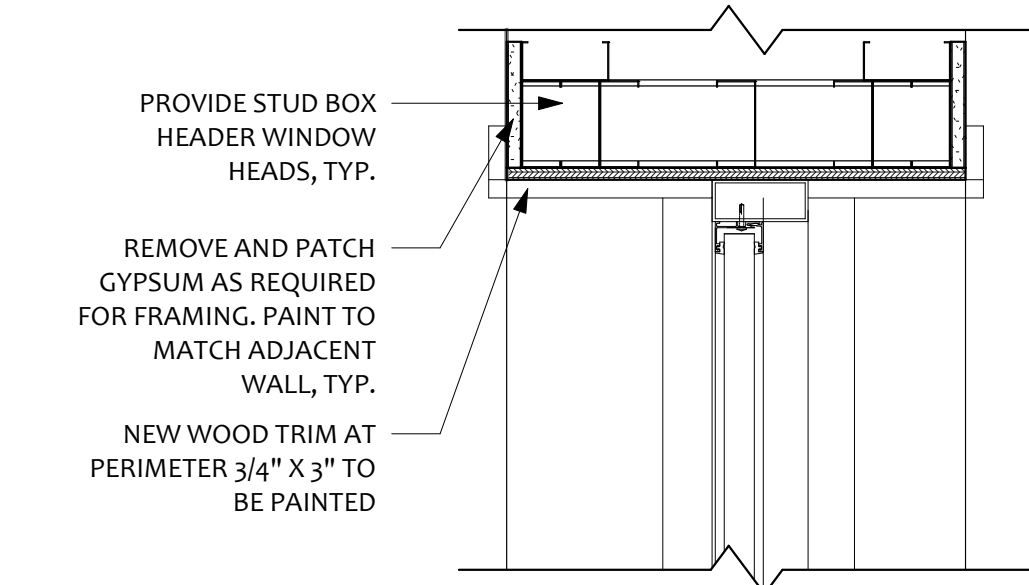

6 SECURE TRANSACTION WINDOW SECTION IN EXISTING WALL
1 1/2" = 1'-0"

INTERIOR ALTERATIONS
FOR
UNION COUNTY EDUCATIONAL SERVICES
COMMISSION
AT
WESTLAKE / UCESC BOE
53 CARDINAL DR., WESTFIELD, NEW JERSEY 07090

Consulting Engineer's Seal:

WINDOW SCHEDULE & DETAILS

No.	DATE:	COMMENTS:
	3/10/2026	ISSUE FOR BID
DATE:	3/10/2026	SOLUTION No.
SCALE:	As indicated	25.138B
DRAWN BY:	SW	DRAWING No.
CHECKED BY:	YO	A.5.5