


www.slamcoll.com

1. REFER TO GENERAL INFORMATION SHEET FOR LIST OF TYPICAL ABBREVIATIONS AND TYPICAL ARCHITECTURAL GRAPHIC LEGENDS AND SYMBOLS.
2. REFER TO TYPICAL PARTITION TYPES AND DETAILS. ALL PARTITIONS SHALL BE TYPE 1 UNLESS OTHERWISE NOTED.
3. REFER TO CODE INFORMATION AND FIRE SAFETY PLAN DRAWINGS FOR LOCATIONS OF FIRE-RESISTANCE RATED PARTITIONS AND NON-FIRE-RESISTANCE RATED SMOKE PARTITIONS.
4. ALIGN PARTITIONS WITH COLUMN OR MULLION CENTERLINE, UNLESS OTHERWISE NOTED.
5. DIMENSIONS ARE FROM FACE OF WALL TO FACE WALL, I.E. FACE OF OUTSIDE BOARDER OR FROM FACE OF EXISTING CONCRETE OR FORM CONSTRUCTION, UNLESS OTHERWISE NOTED. DIMENSIONS NOTED AS "CLEAR" SHALL BE FROM FINISH FACE TO FINISH FACE. (a) FACE OF CERAMIC TILE TO FACE OF CERAMIC TILE. VERIFY ALL EXISTING DIMENSIONS IN THE FIELD.
6. REFER TO PLAN ENLARGEMENTS FOR ADDITIONAL DIMENSIONS.
7. REFER TO DOOR AND FRAME DETAILS FOR ADDITIONAL INFORMATION. PROVIDE MINIMUM 1" CLEARANCE FROM FACE OF DOOR LAMB TO FACE OF ADJACENT WALL, UNLESS OTHERWISE NOTED.
8. REFER TO TYPICAL MOUNTING LOCATIONS AND HEIGHTS FOR TOILET ACCESSORIES, EQUIPMENT, WALL SPECIALTY DESIGNATIONS, ETC. (TYPICAL TOILET ROOM ELEVATIONS AND TOILET ACCESSORY SCHEDULE.)
9. PROVIDE FIRE TREATED WOOD BLOCKING OR MINIMUM 0.0132" THICK STEEL PLATE STRIP AND BACKING PLATE AT, BUT NOT LIMITED TO, THE FOLLOWING LOCATIONS: TOILET ACCESSORIES, CASEWORK, MILLWORK, DOOR WALL BUMPERS, AND ALL OTHER WALL MOUNTED EQUIPMENT OR DEVICES.
10. REFERENCE THE FIRE SAFETY PLANS, ALL EXISTING PARTITIONS INDICATED TO SERVE AS FIRE BARRIERS. FIRE PARTITIONS, SMOKE BARRIERS OR SMOKE PARTITIONS REQUIRED TO MEET ALL REQUIREMENTS FOR STATED FIRE AND SMOKE RATING.
 - A. CONSTRUCTION OF PARTITION MUST MATCH REQUIREMENTS FOR STATED FIRE AND SMOKE RATING.
 - B. EXTENTS OF PARTITION MUST EXTEND FULL HEIGHT, SEALED TO UNDERSIDE OF DECK ABOVE. PARTITION TO EXTEND LaterALLY FULL LENGTH WITHOUT INTERRUPTIONS.
 - C. FIRSTFLOOR PARTS MUST BE PROVIDED AT ALL DOORS, PENETRATIONS AND EGRESS.
12. REFER TO THE EQUIPMENT PLANS FOR RESIDENTIAL APPLIANCE, AND TOILET ACCESSORY LOCATIONS. REFER TO THE EQUIPMENT PLANS FOR EQUIPMENT LOCATIONS AND SCHEDULE.
13. REFER TO THE FINISH PLANS FOR PART PATTERNS.
14. FLOOR PLATCH AND FLOOR LEVELING: REPAIR EXISTING TYPING SLAB AND CONCRETE FLOOR AT DEMOLITION OF WALLS AND AT ALL OTHER LOCATIONS REQUIRED. REFER TO DEMOLITION PLANS FOR ADDITIONAL INFORMATION.
15. PATCHING AND REPAIRING OF EXISTING PARTITIONS, CEILINGS, FLOORS, ETC. TO MATCH ADJACENT CONSTRUCTION AND FINISHES, UNLESS OTHERWISE NOTED.
 - A. PROVIDE PATHWAYS AND OPENINGS AS REQUIRED FOR ALL INTERSECTING CONSTRUCTION AND FINISHES AND THEN PATCH TO MATCH EXISTING. THIS INCLUDES AREAS OF EXISTING CONSTRUCTION ALTERED AND/OR DISTURBED BY THE DEMOLITION, INSTALLATION AND/OR RELOCATION OF MEP/AVT PATHWAYS, EQUIPMENT AND DEVICES.
 - B. PATCH REPAIR ALL AREAS ADJACENT TO, OR DISTURBED BY, NEW CONSTRUCTION TO MATCH EXISTING CONSTRUCTION SCHEDULED TO BE DEMOLISHED.
 - C. PATCH REPAIR AND FINISH ALL EXISTING SURFACES THAT ARE TO RECEIVE NEW MATERIALS, FINISHES, ETC.

	NEW WALL CONSTRUCTION
	EXISTING WALL CONSTRUCTION TO REMAIN
	CASEWORK
	FIRE EXTINGUISHER CABINET
	CARD READER
	AUTOMATIC - HAND SWIPE
	BOTTLE FILLER
	Z LOCKER
	FLAT PANEL DISPLAY
	NOT IN SCOPE

**440 Mamaroneck Ave.
Harrison, NY
Suite 301**

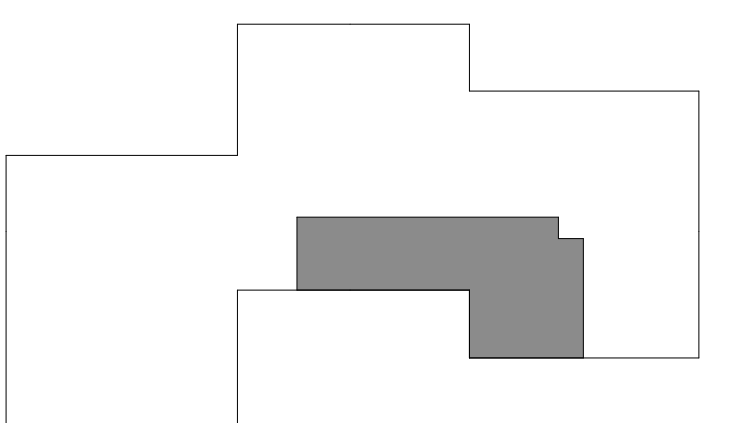

Number	Date	Issued For

Date 4/10/2026	Drawing Number
Scale As indicated	A103
Proj. Number 25195.25	

